


LE 180 - LA MULATIERE

BANDEAU TYPE 5

NIVEAU 0

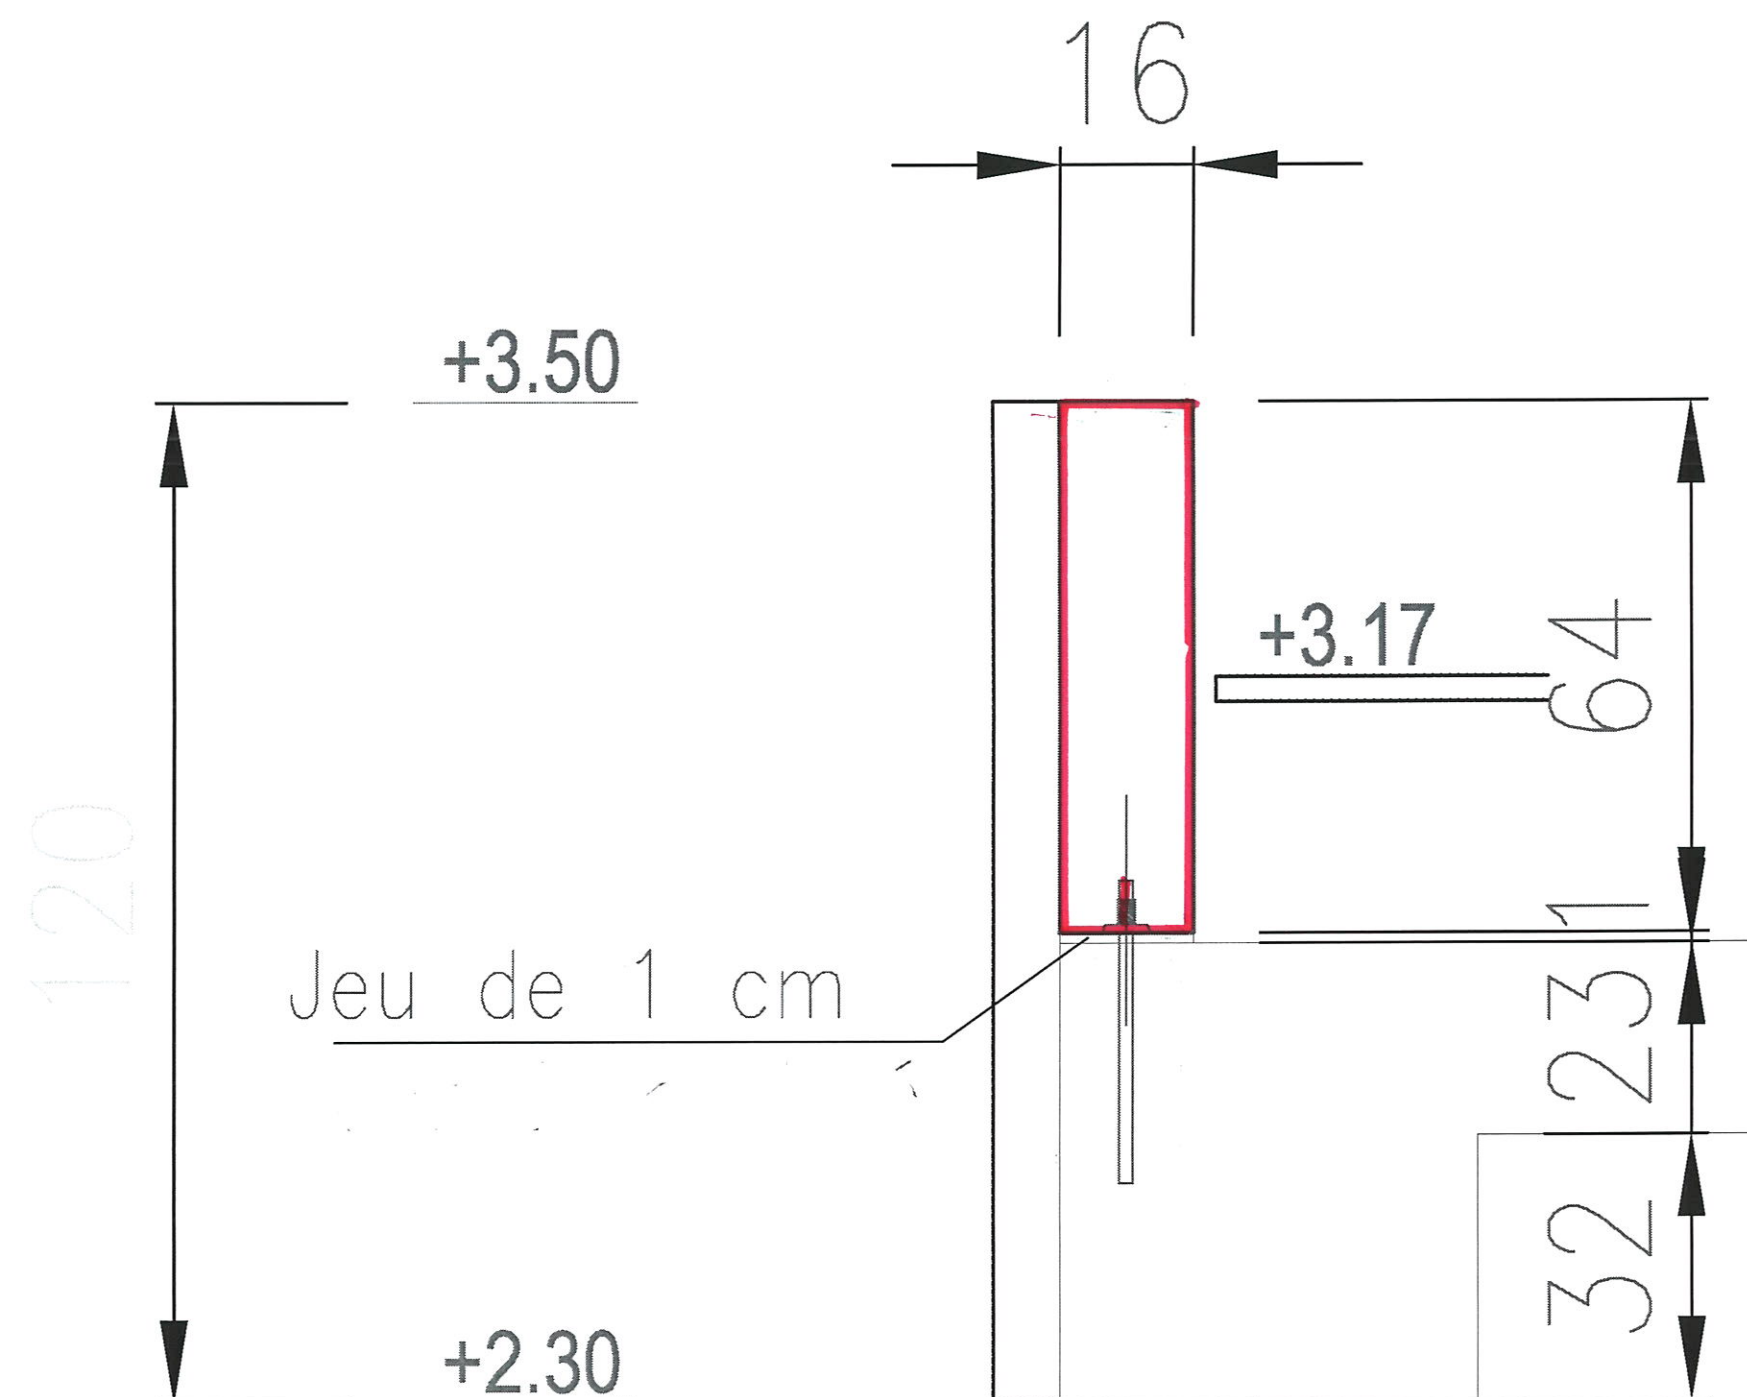


le 12 février - Yves.

LE 180 - LA MULATIERE


BANDEAU TYPE 5

NIVEAU 0

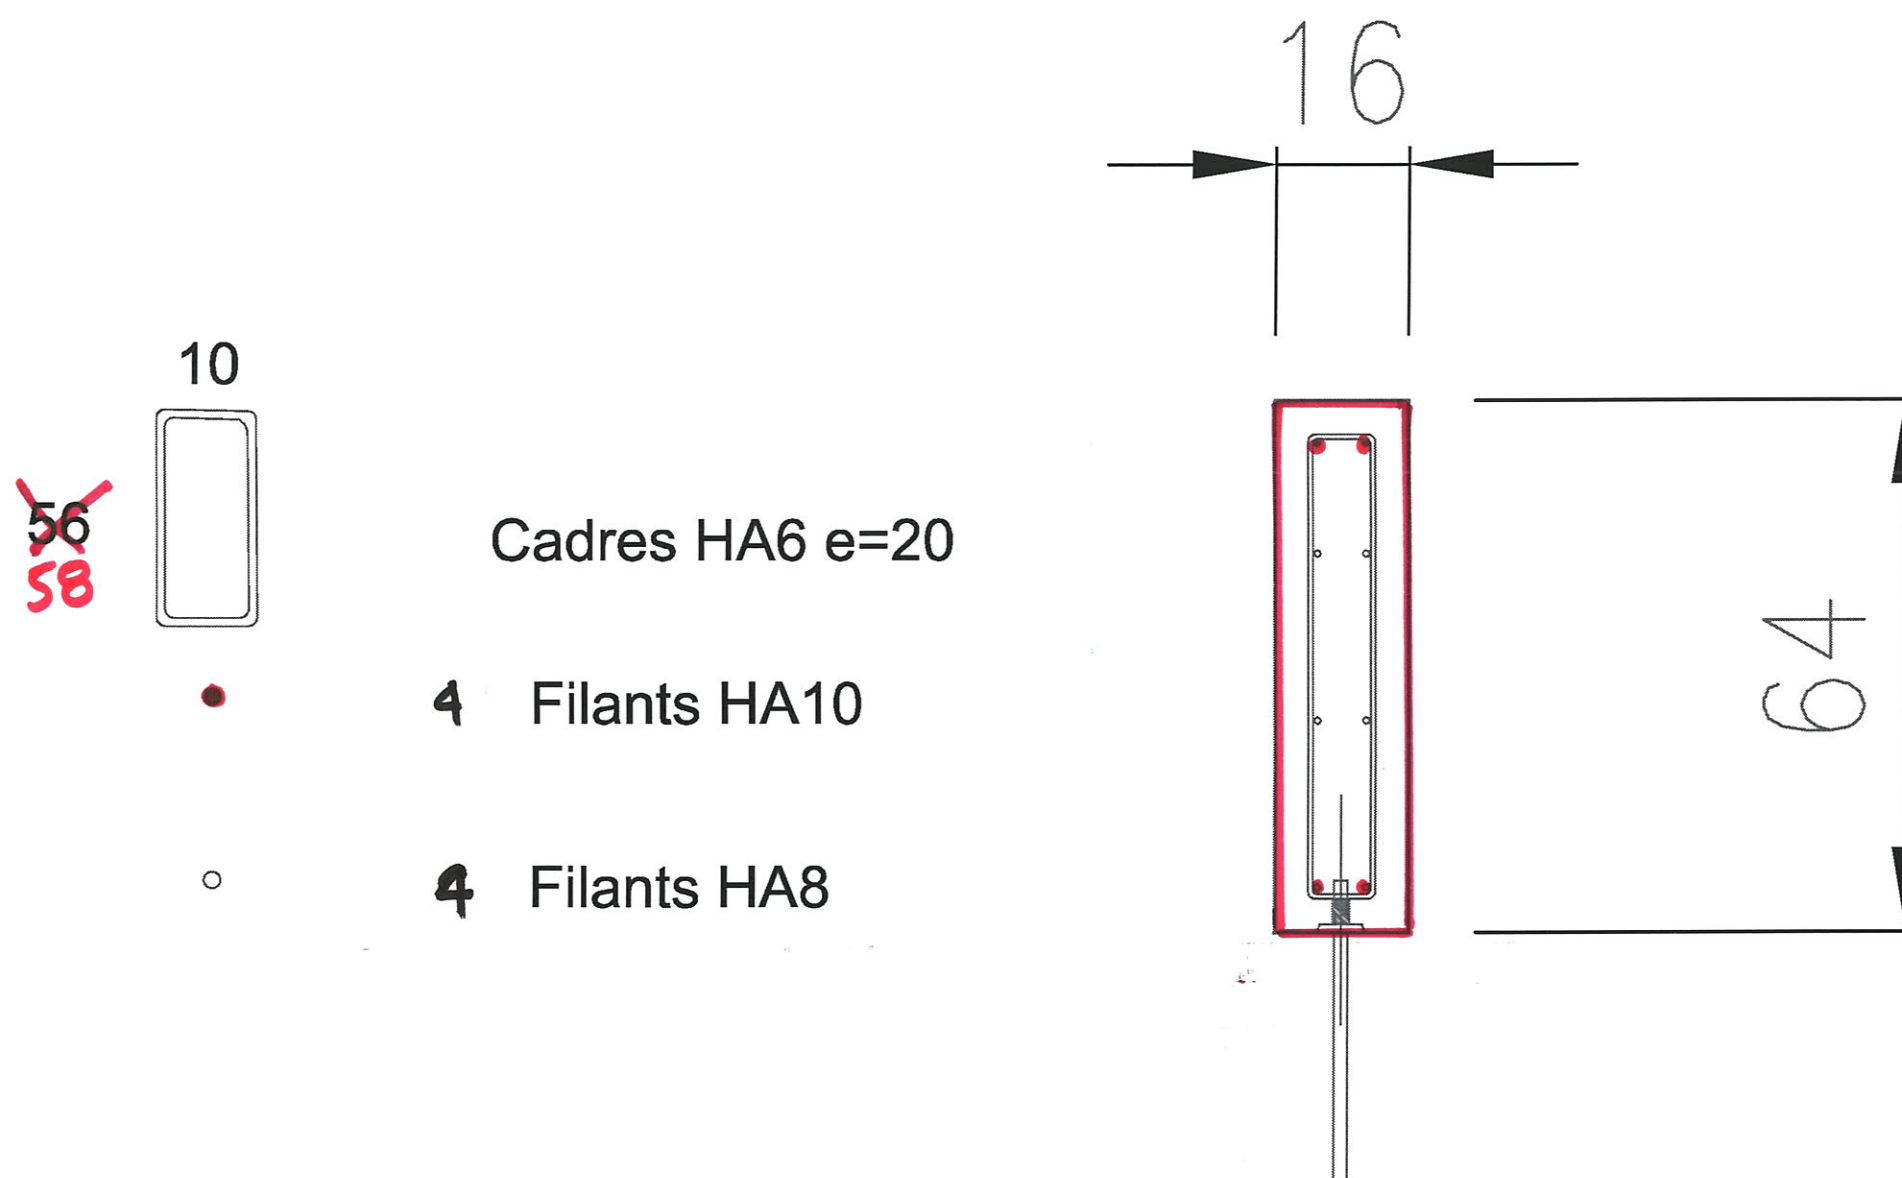


Plancher Niveau R0 BAT. A

PAUCO
solution ①

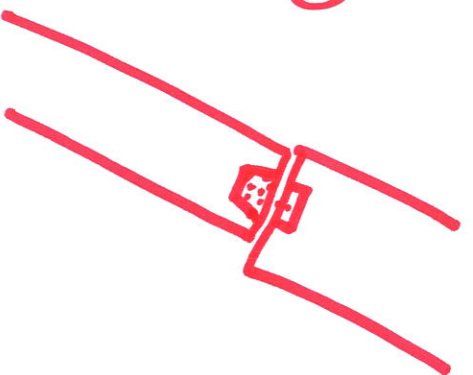


Ponce dans la banche

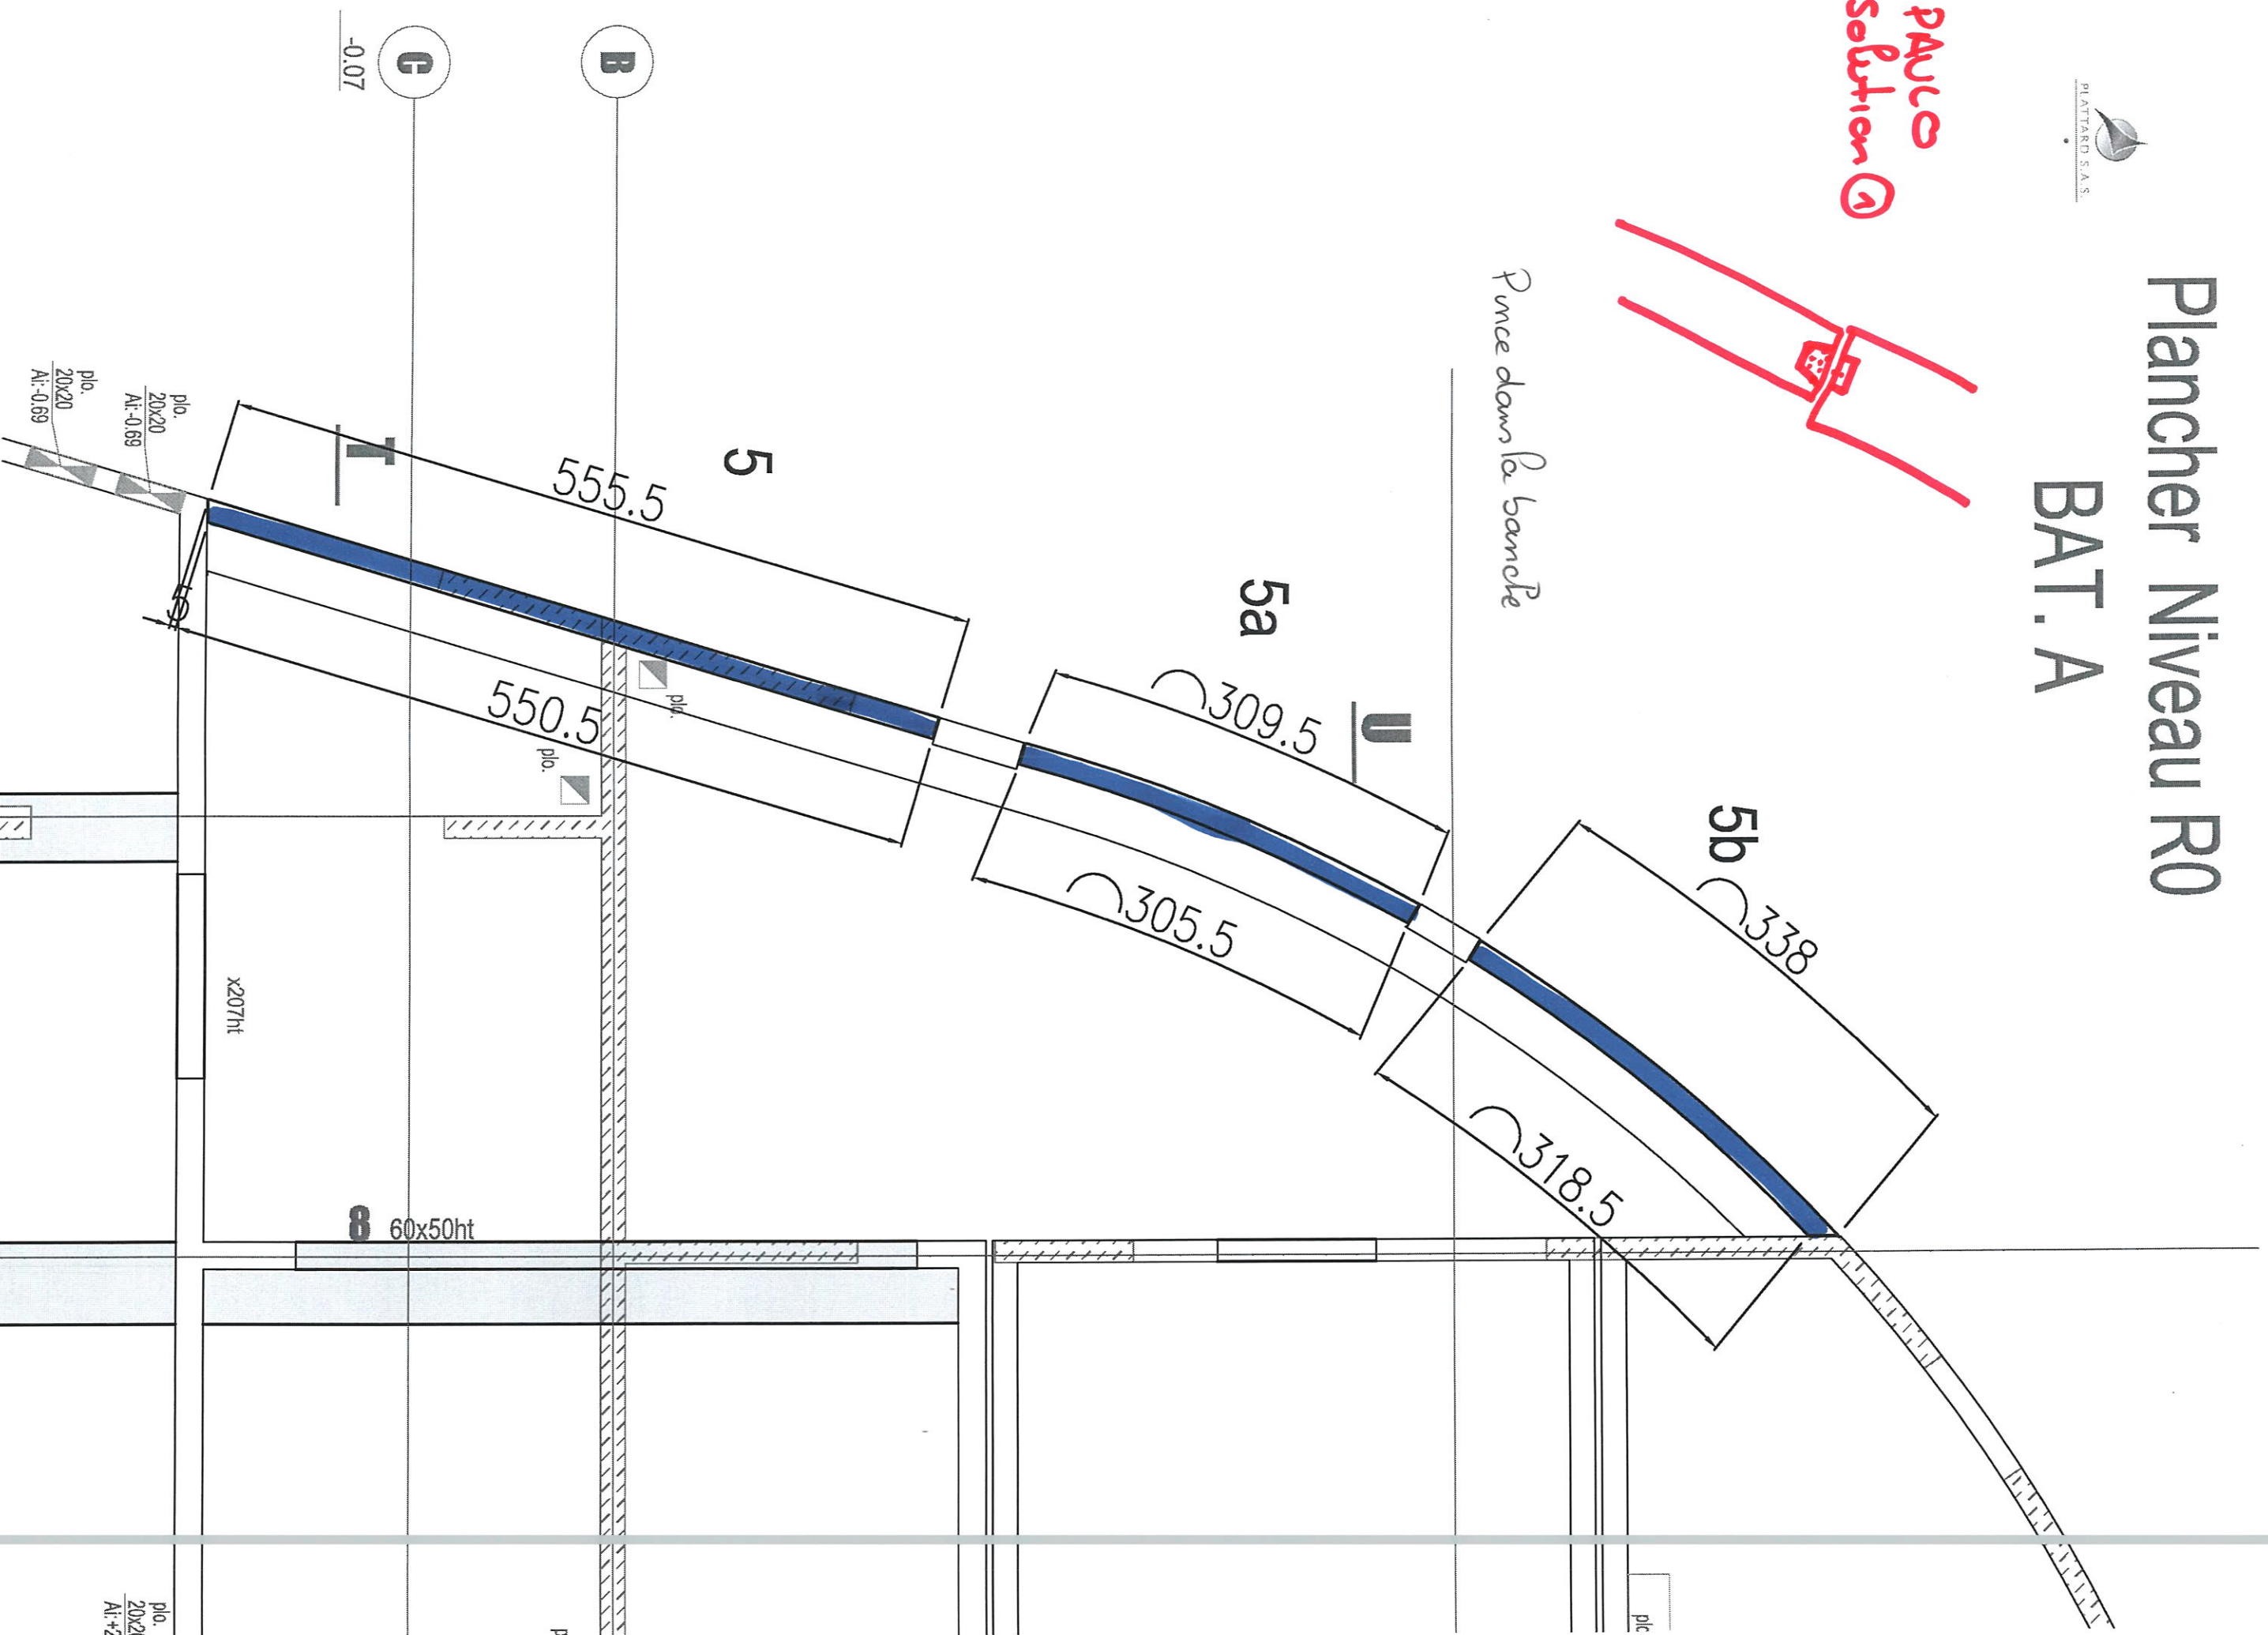


MOULE	N	NC	observations	CONTROLE	N	NC	observations	BETON	N	NC	observations	FICHE AUTO-CONTROLE	
Conformité moule				Dimensions				Conformité béton				Opérateur :	
Etat du moule				Armature				Mise en place				Responsable prod :	
Propreté et huilage				Inserts				Aspect de surface				Date :	

Ent. FONTANEL	Elément: BANDEAUX		FICHE DE FABRICATION	Surface: m²	POIDS	REPERE	Nbr
LE 180 - LA MULATIERE					1.24 T	5	1
				coffrage			

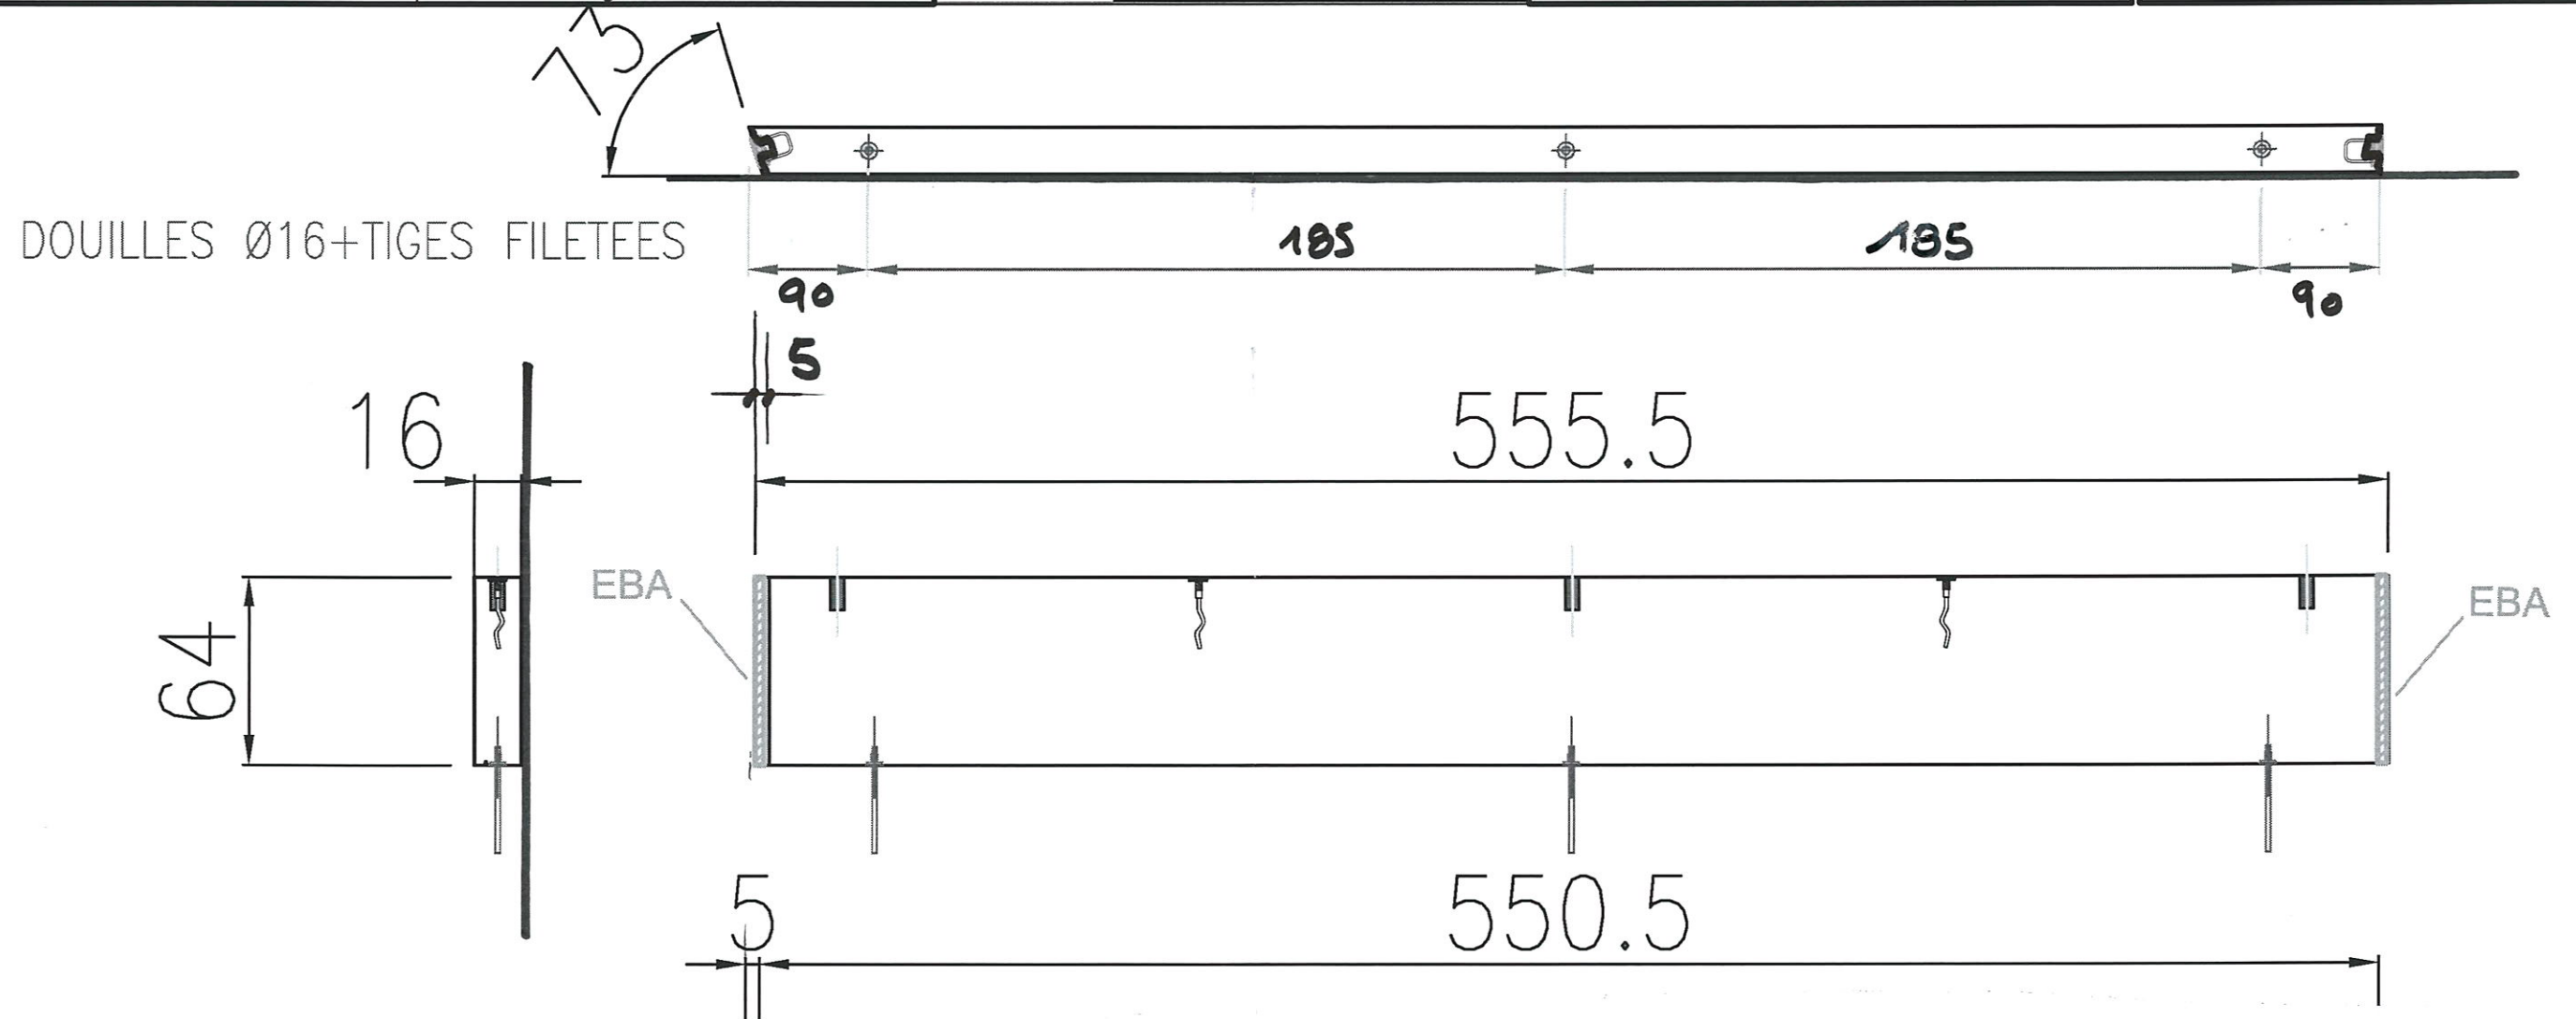

LEVAGE		Douille Ø	INSERTS		Ancre Frimeda T	INSERTS		EBA	INSERTS		TP - JV	DATE: 16/11/2015	
		Douille Ø			Renfort Ø			Douille étalement			PVC Ø80	Plan N°	Page N°
		Renfort Ø dx			Trifer			Ankrobox Ø50			Tube garde-corps	Indice	

MOULE	N	NC	observations	CONTROLE	N	NC	observations	BETON	N	NC	observations	FICHE AUTO-CONTROLE	
Conformité moule				Dimensions				Conformité béton				Opérateur :	
Etat du moule				Armature				Mise en place				Responsable prod :	
Propreté et huilage				Inserts				Aspect de surface				Date :	
Ent. FONTANEL								Surface: m ²	POIDS			REPERE	Nbr
LE 180 - LA MULATIERE		Elément: BANDEAUX		coffrage		FICHE DE FABRICATION		Volume: 0.32 m ³	0.76 T			5a	1

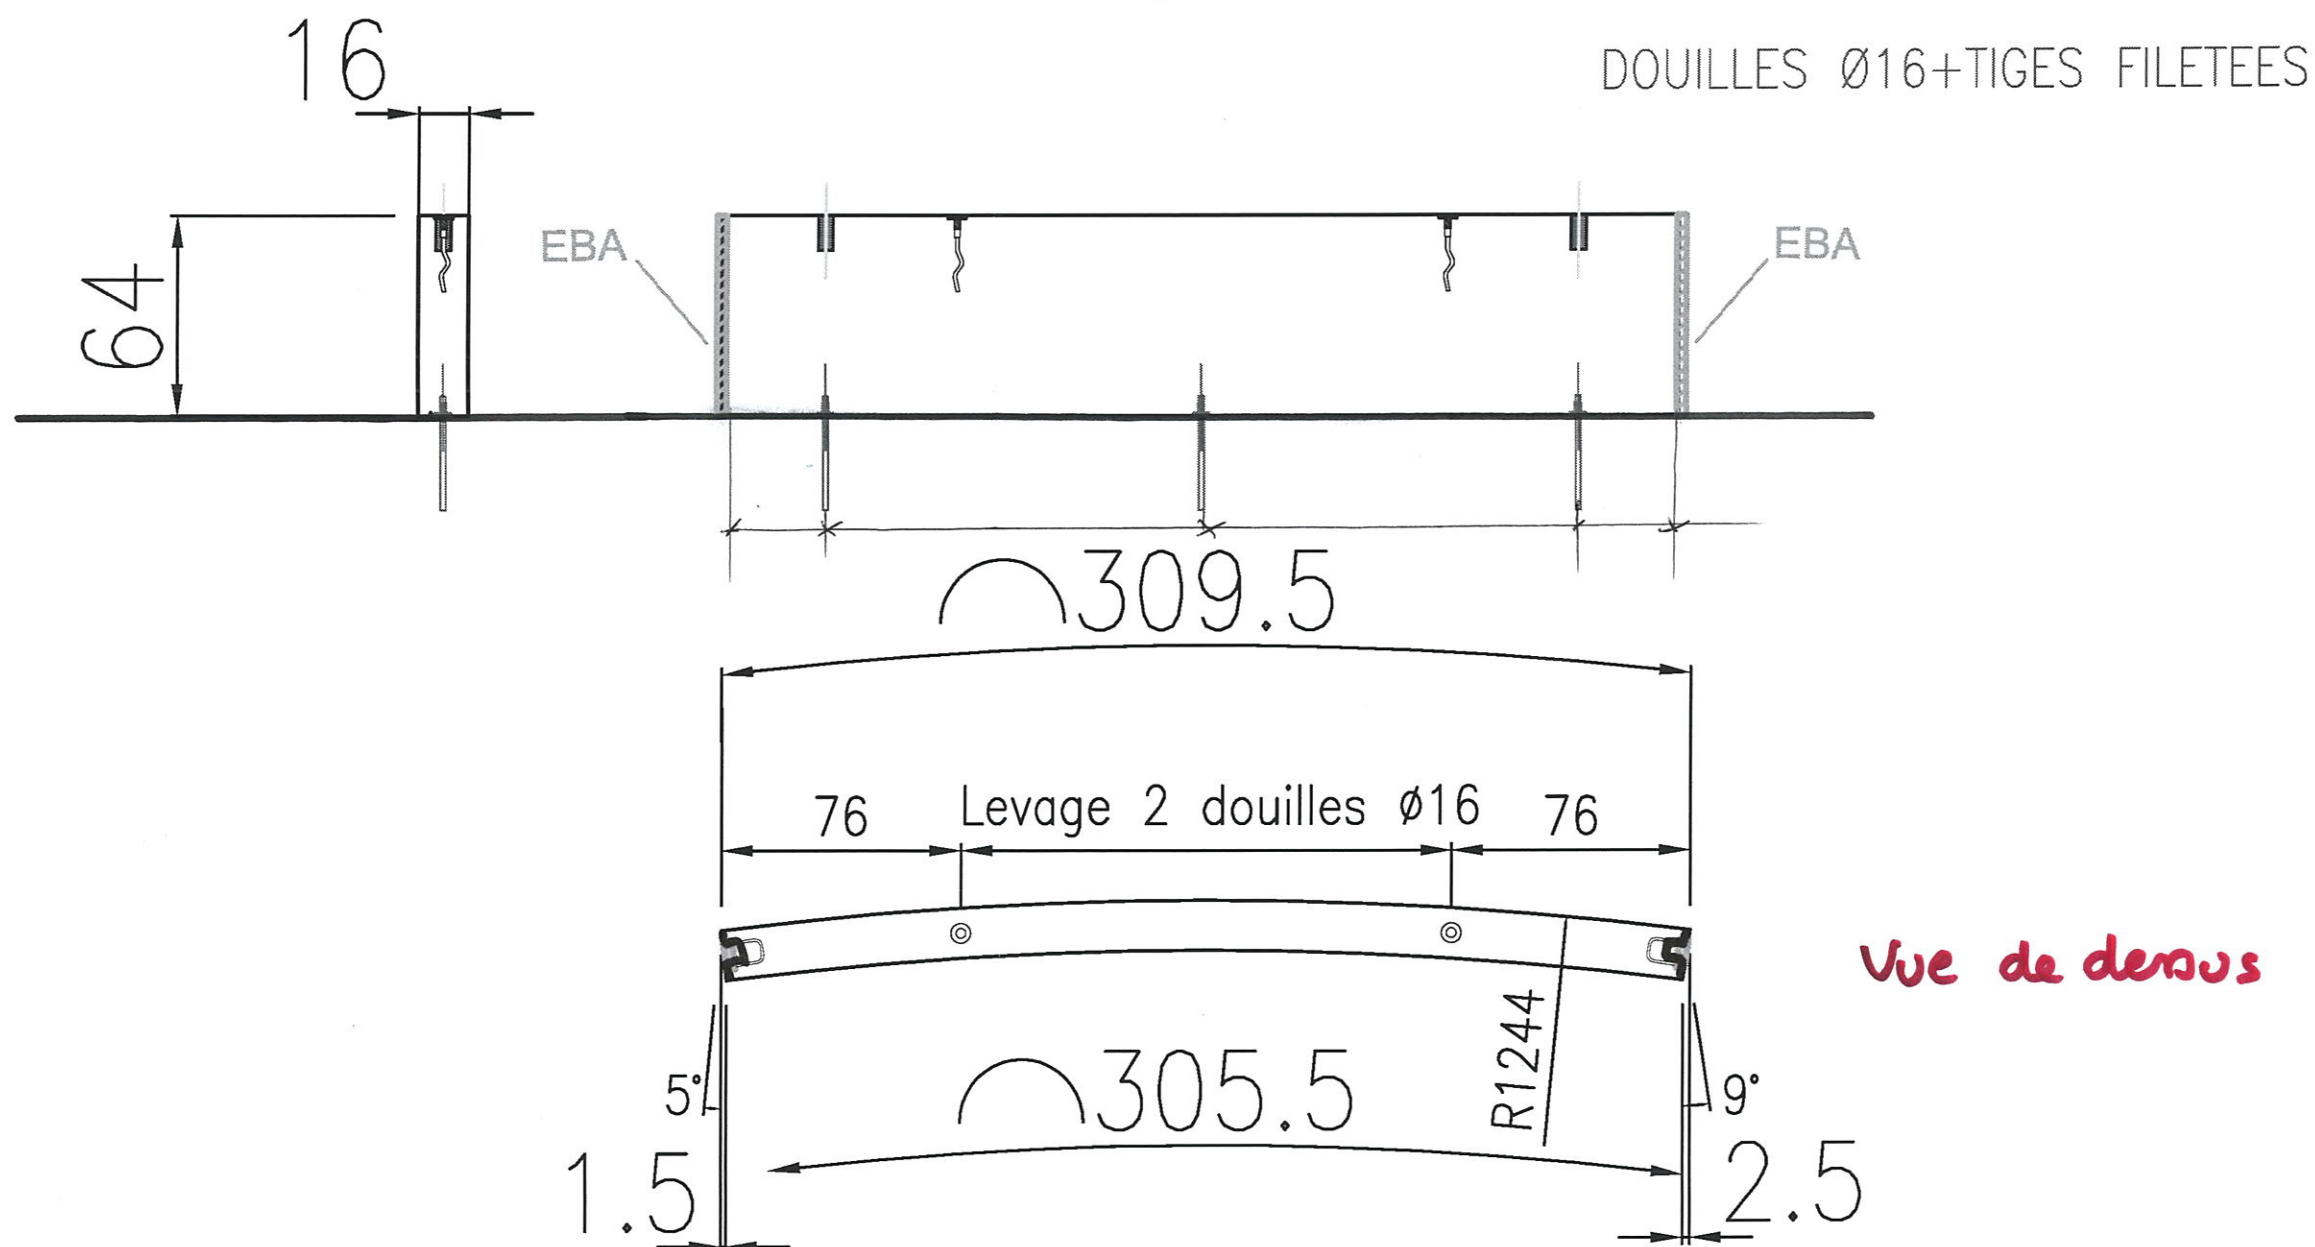


LEVAGE		Douille Ø	INSERTS		Ancre Frimeda T	INSERTS		EBA	INSERTS		TP - JV	DATE: 16/11/2015	
		Douille Ø			Renfort Ø			Douille étalement			PVC Ø80	Plan N°	Page N°
		Renfort Ø dx			Trifer			Ankrobox Ø50			Tube garde-corps	Indice	

MOULE	N	NC	observations	CONTROLE	N	NC	observations	BETON	N	NC	observations	FICHE AUTO-CONTROLE	
Conformité moule				Dimensions				Conformité béton				Opérateur :	
Etat du moule				Armature				Mise en place				Responsable prod :	
Propreté et huilage				Inserts				Aspect de surface				Date :	

Ent. FONTANEL			FICHE DE FABRICATION	Surface: m²		POIDS	REPERE	Nbr	
LE 180 - LA MULATIERE							0.83 T	5b	1
				Volume: 0.34 m3					


Elément: BANDEAUX	
coffrage	

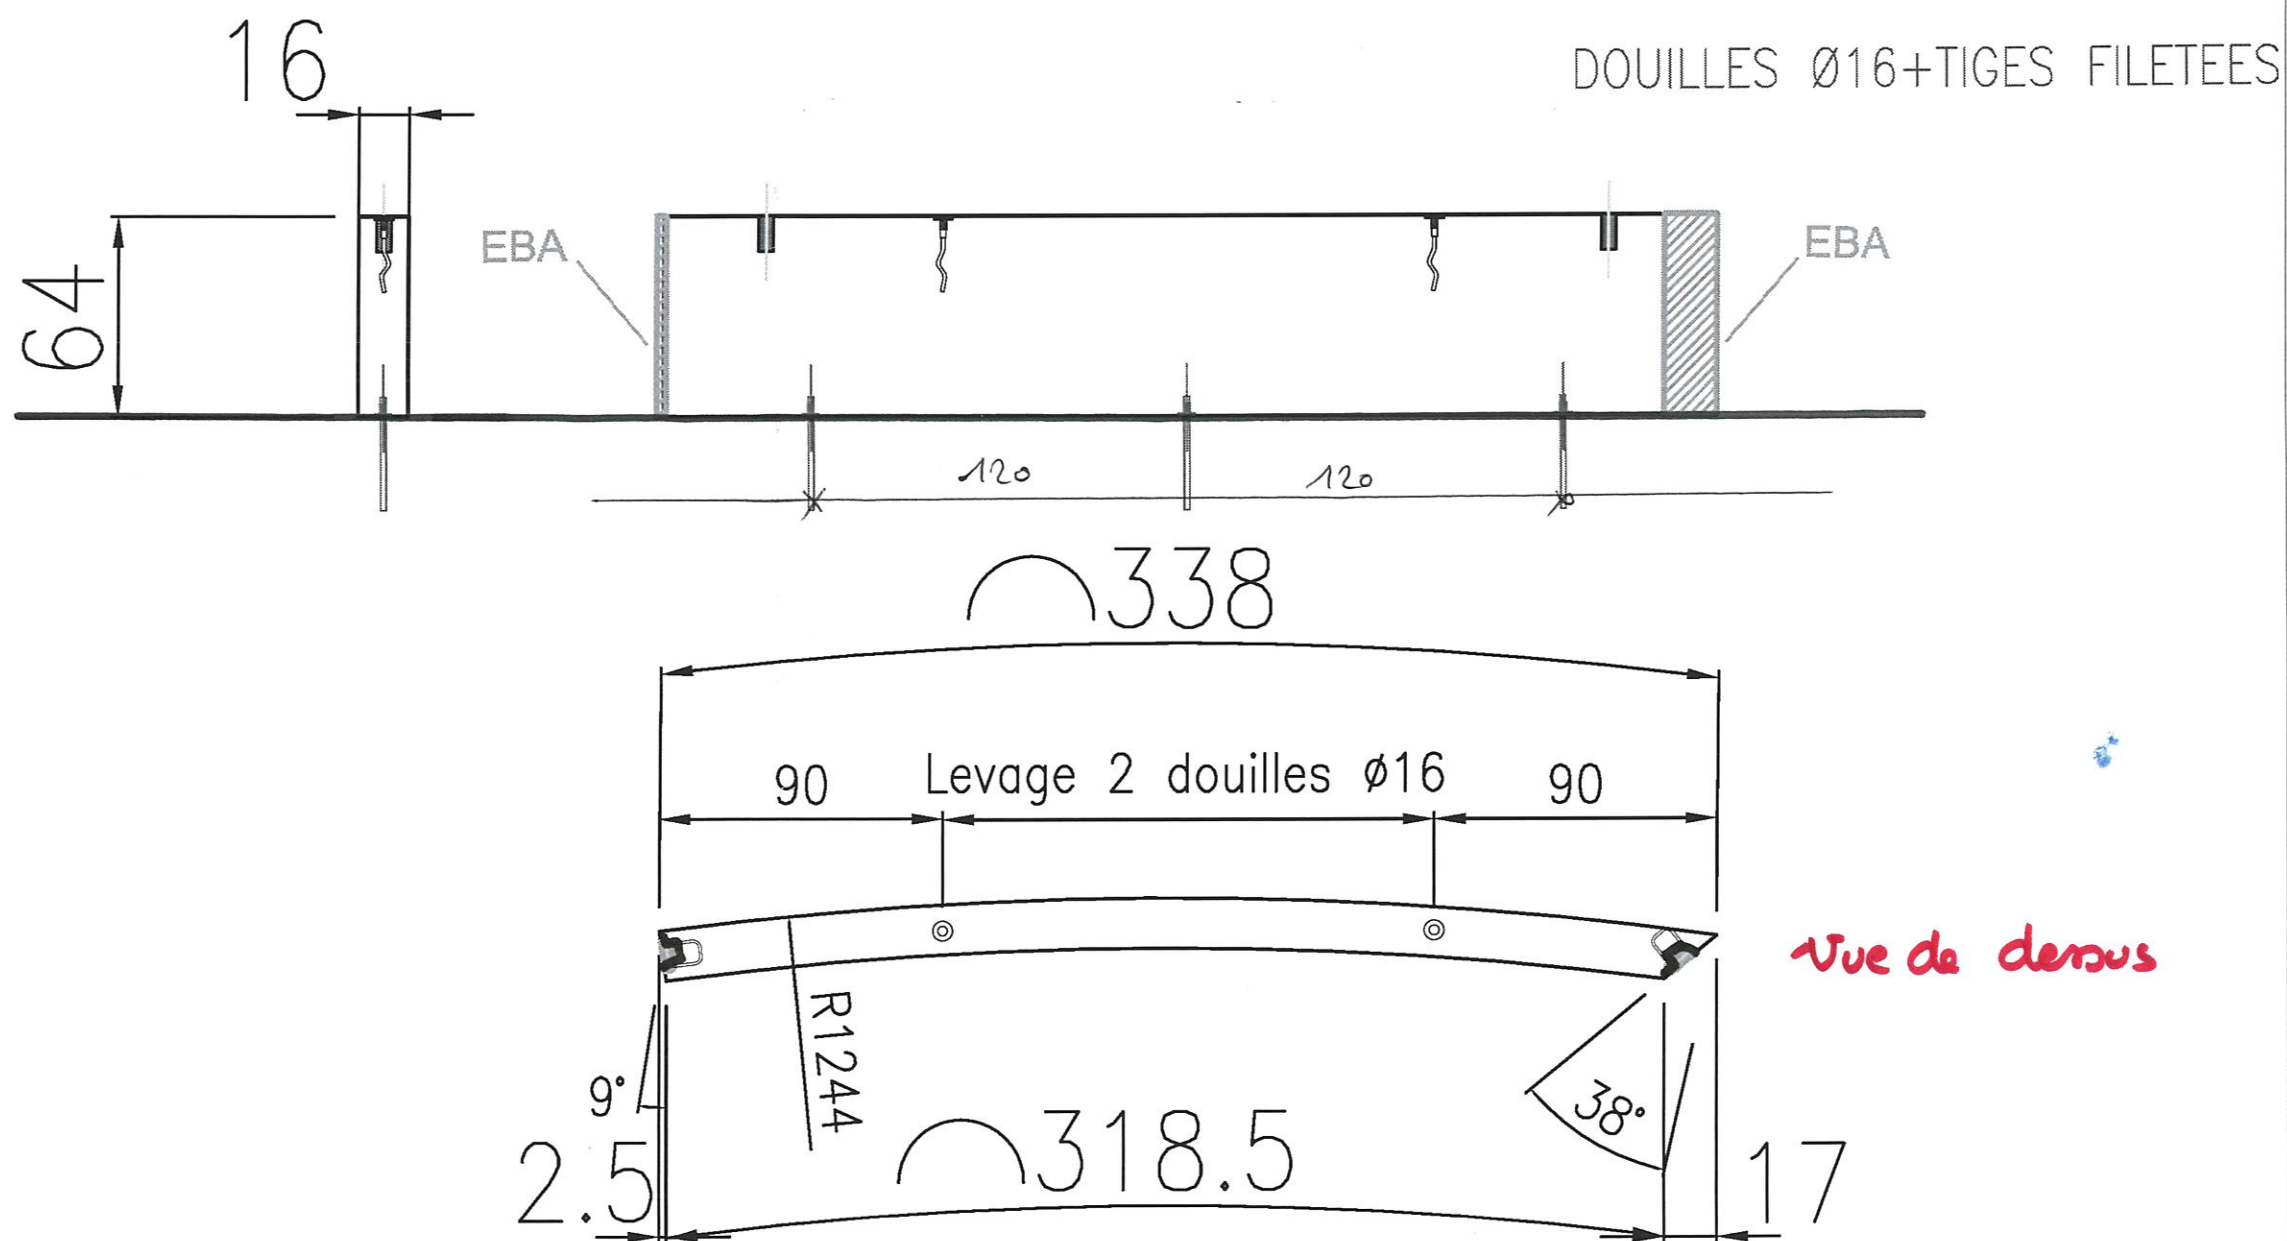

LEVAGE		Douille Ø	INSERTS		Ancre Frimeda T	INSERTS		EBA	INSERTS		TP - JV	DATE: 16/11/2015	
		Douille Ø			Renfort Ø			Douille étaie			PVC Ø80	Plan N°	Page N°
		Renfort Ø dx			Trifer			Ankrbox Ø50			Tube garde-corps	Indice	

MOULE	N	NC	observations	CONTROLE	N	NC	observations	BETON	N	NC	observations	FICHE AUTO-CONTROLE	
Conformité moule				Dimensions				Conformité béton				Opérateur :	
Etat du moule				Armature				Mise en place				Responsable prod :	
Propreté et huilage				Inserts				Aspect de surface				Date :	

Ent. FONTANEL	Elément: BANDEAUX	 FICHE DE FABRICATION	Surface: m²	POIDS	REPERE	Nbr
			Volume: 0.348 m³	0,87 T		

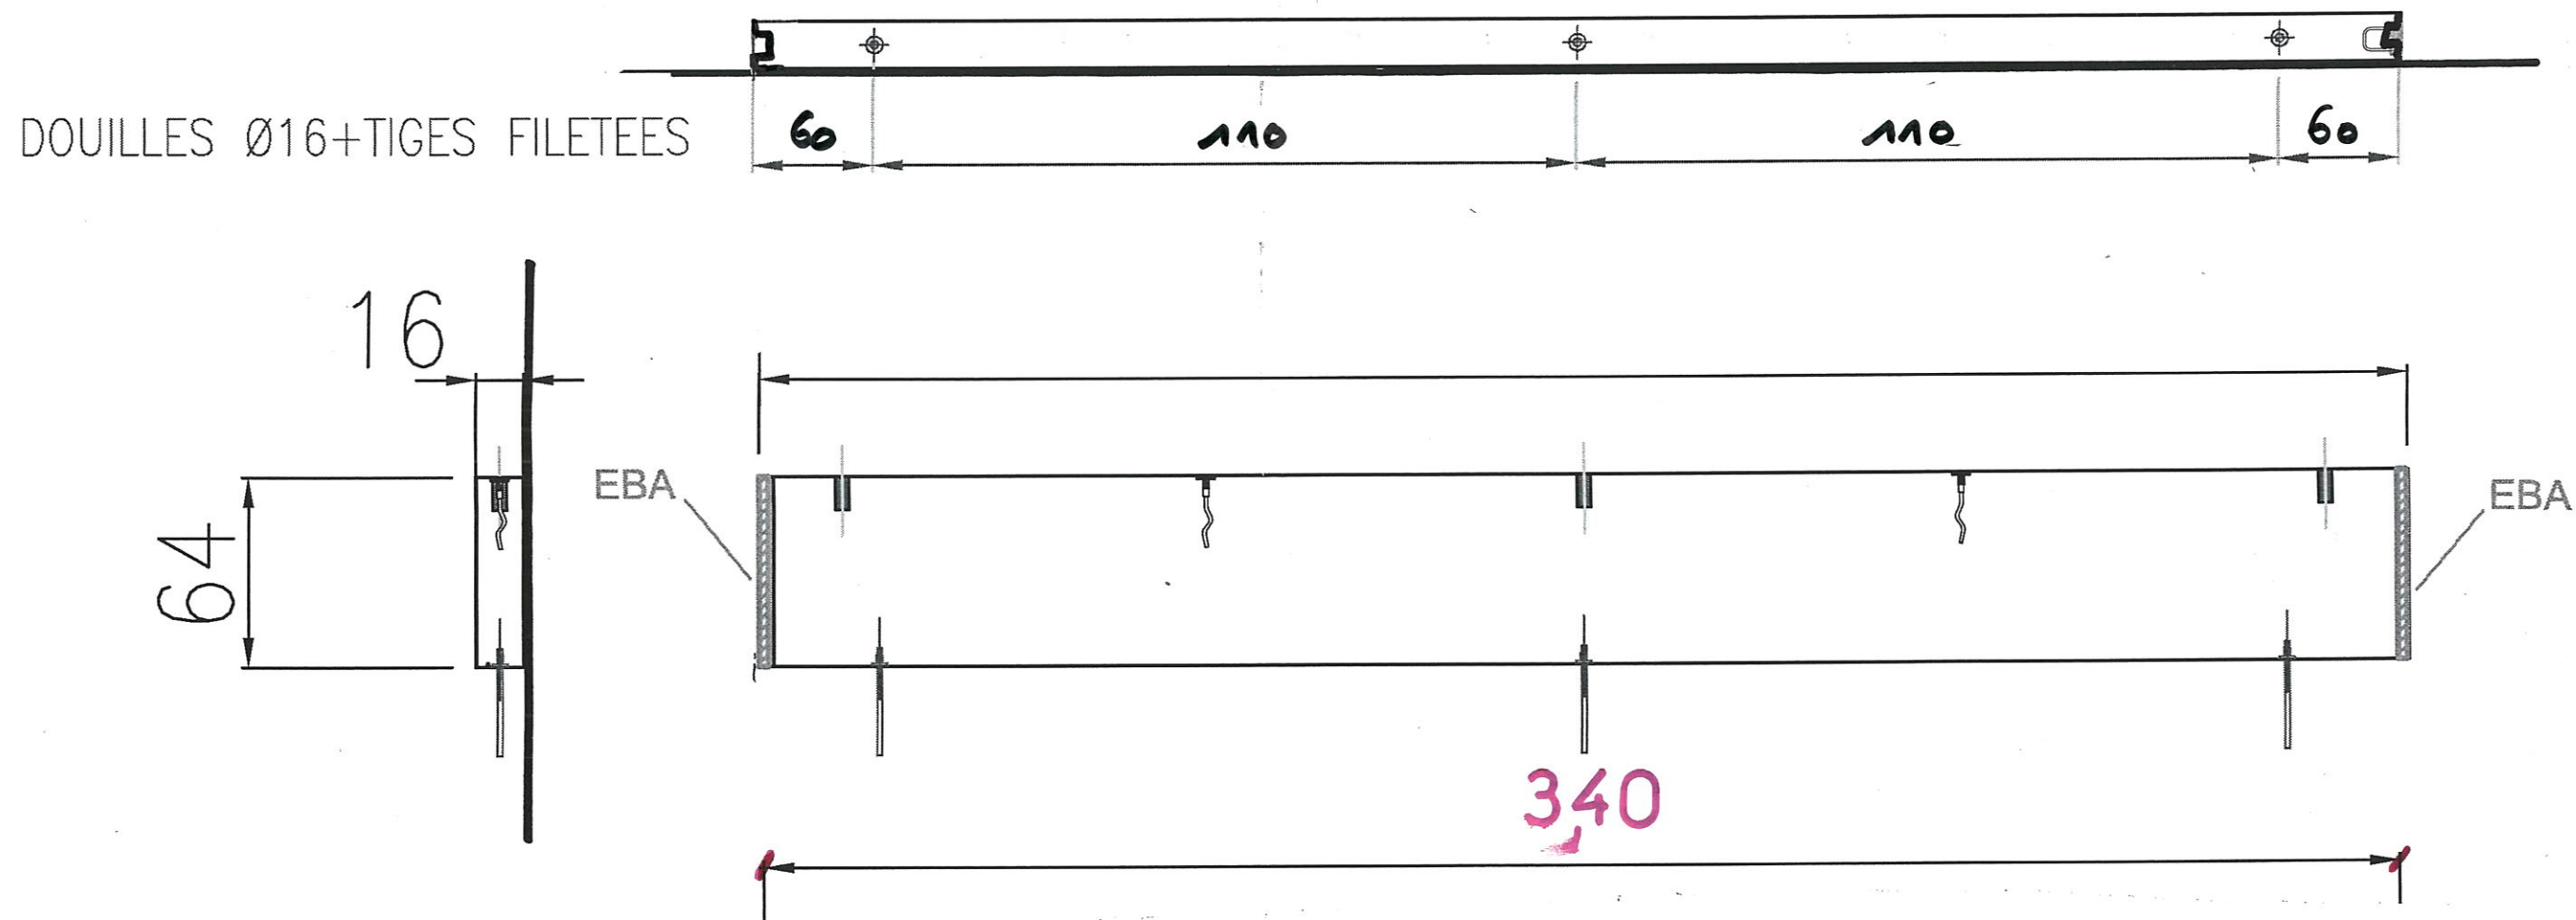

LEVAGE		Douille Ø	INSERTS		Ancre Frimeda T	INSERTS		EBA	INSERTS		TP - JV	DATE: 16/11/2015			
		Douille Ø			Renfort Ø			Douille étaiement			PVC Ø30	Plan N°		Page N°	
		Renfort Ø dx			Trifer			Ankrobox Ø50			Tube garde-corps	Indice			

+0.07

16

18

-0.07

23

7

-0.07

-0.27

20

18

±0.00

+0.07

LARMIE

R

+3.47

COUPE Q

Ech: 1/25

16

5

62

+2.85

23

+2.97

12

+2.85

23

32

+2.30

Ø35

8

16

+3.50

COUPE P

Ech: 1/25

+3.17

64

33


65


+2.85

32

+2.30


32

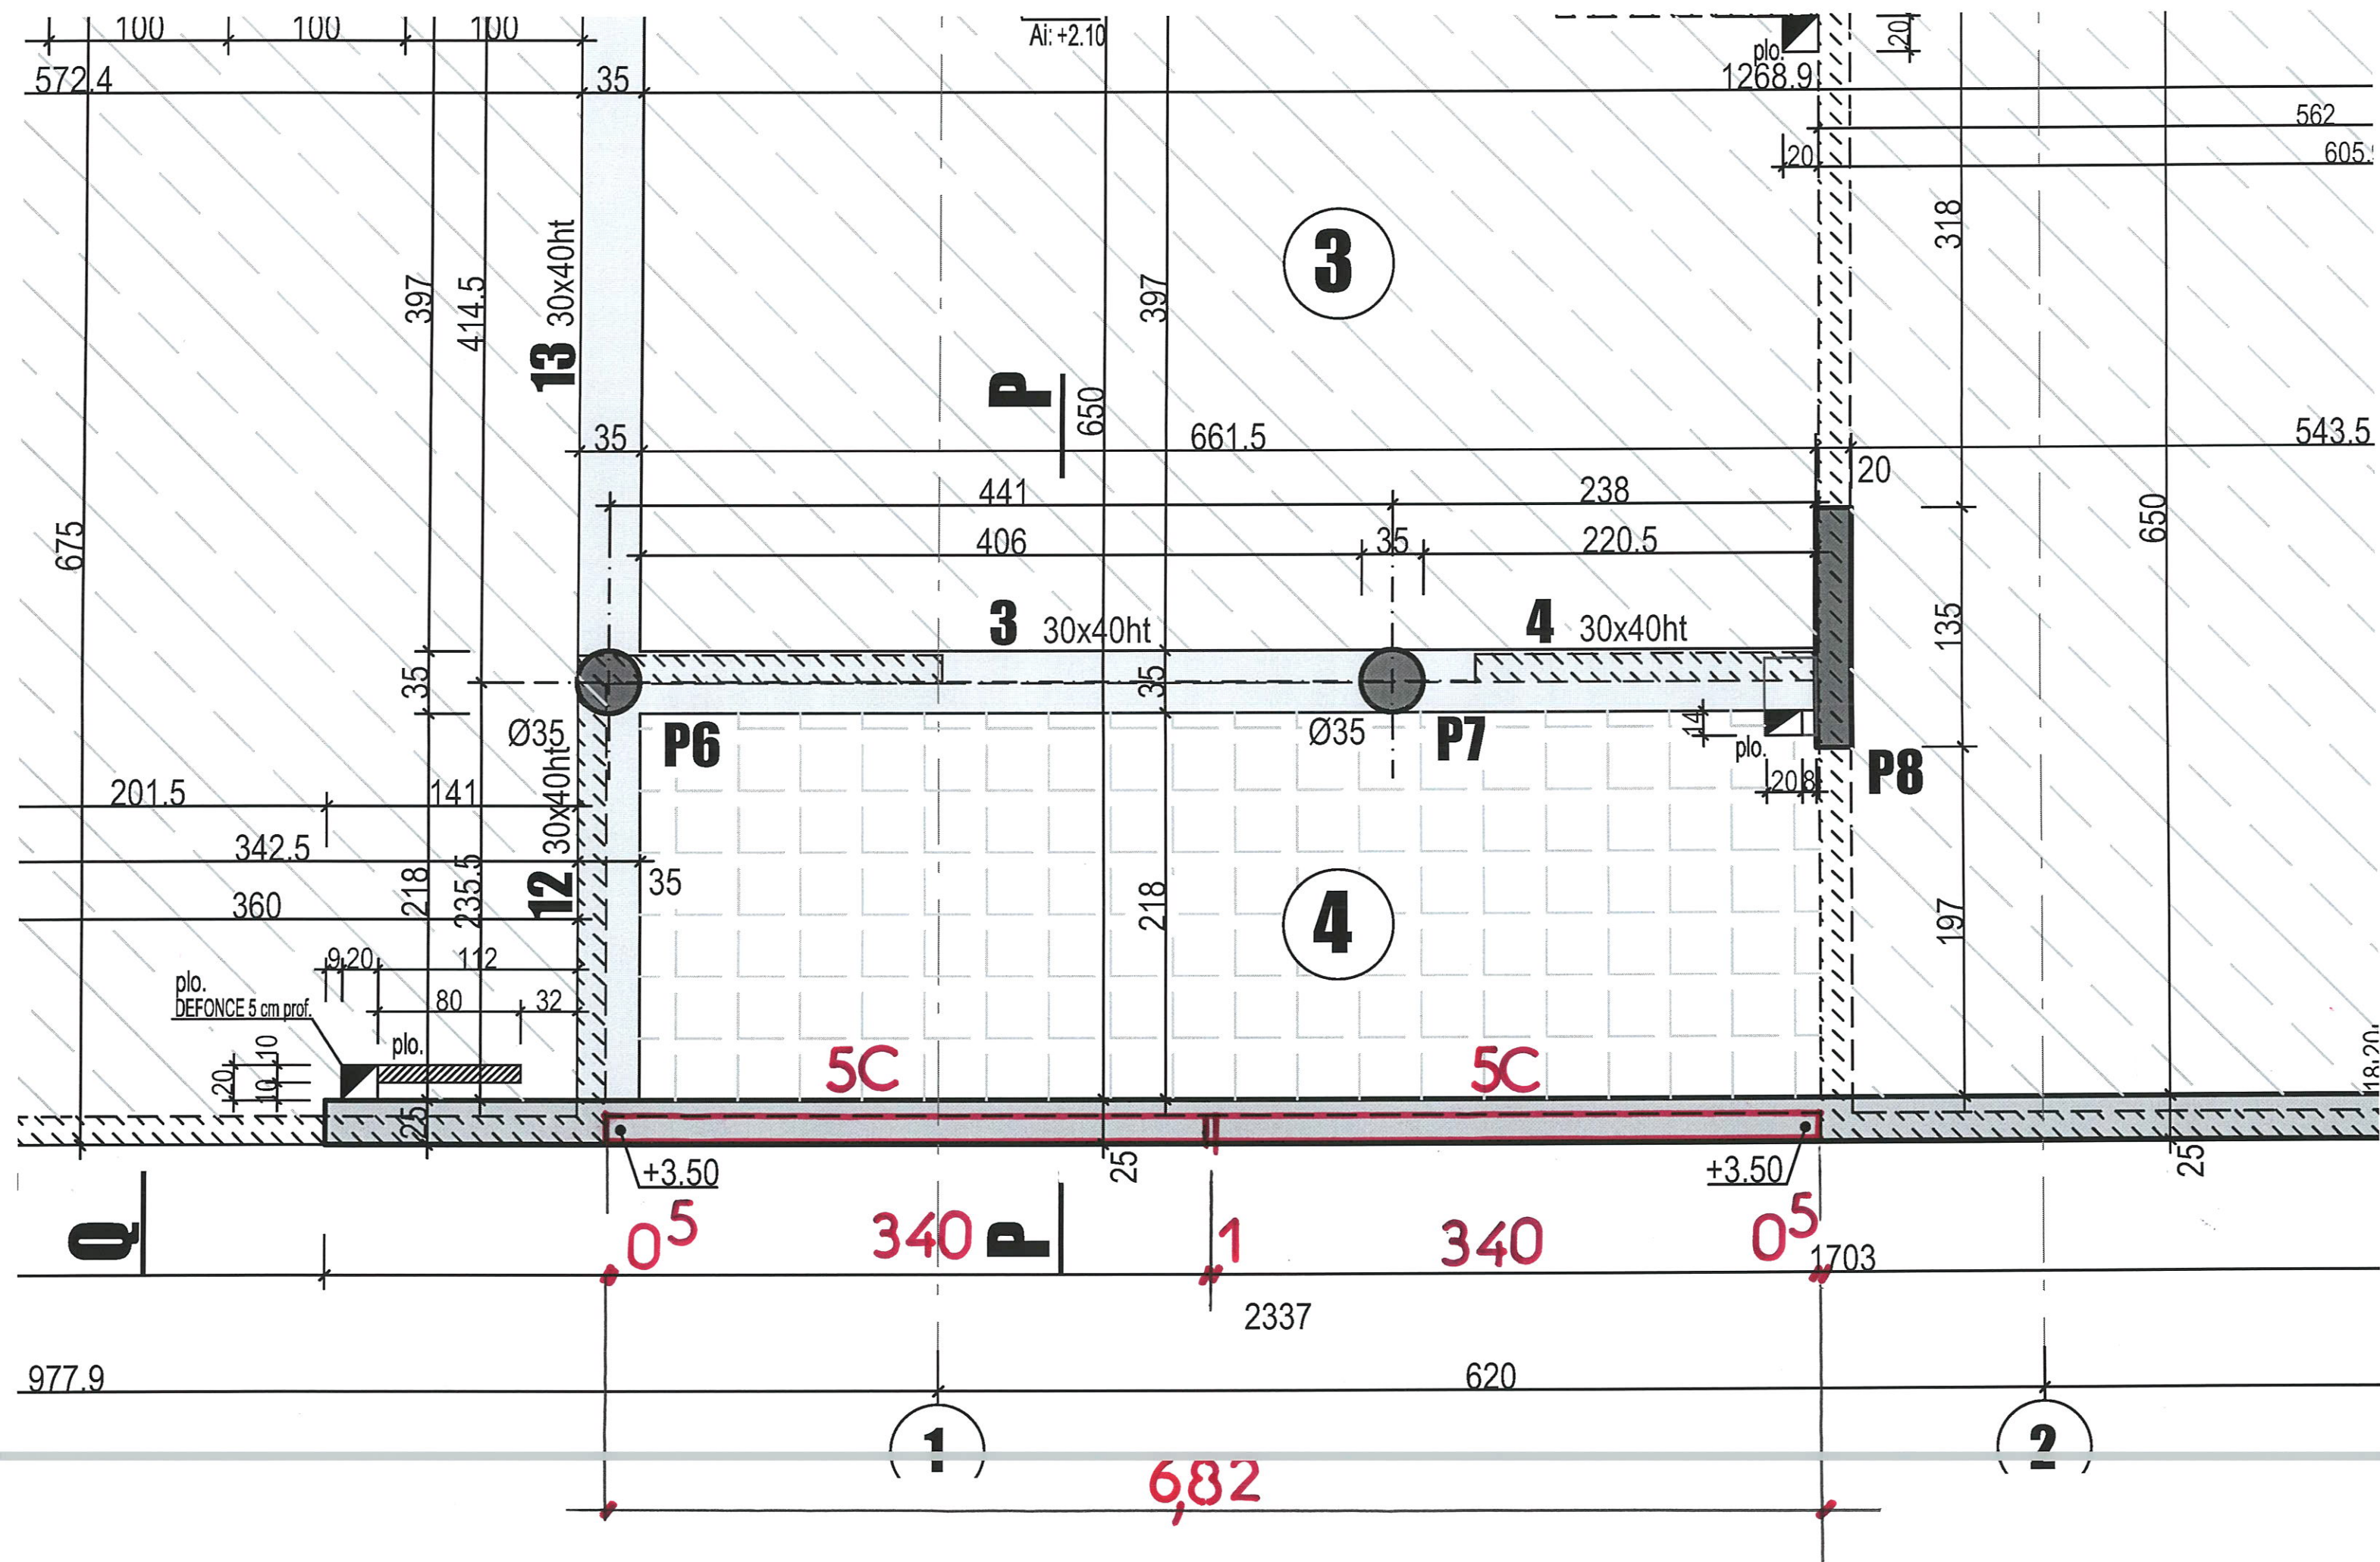

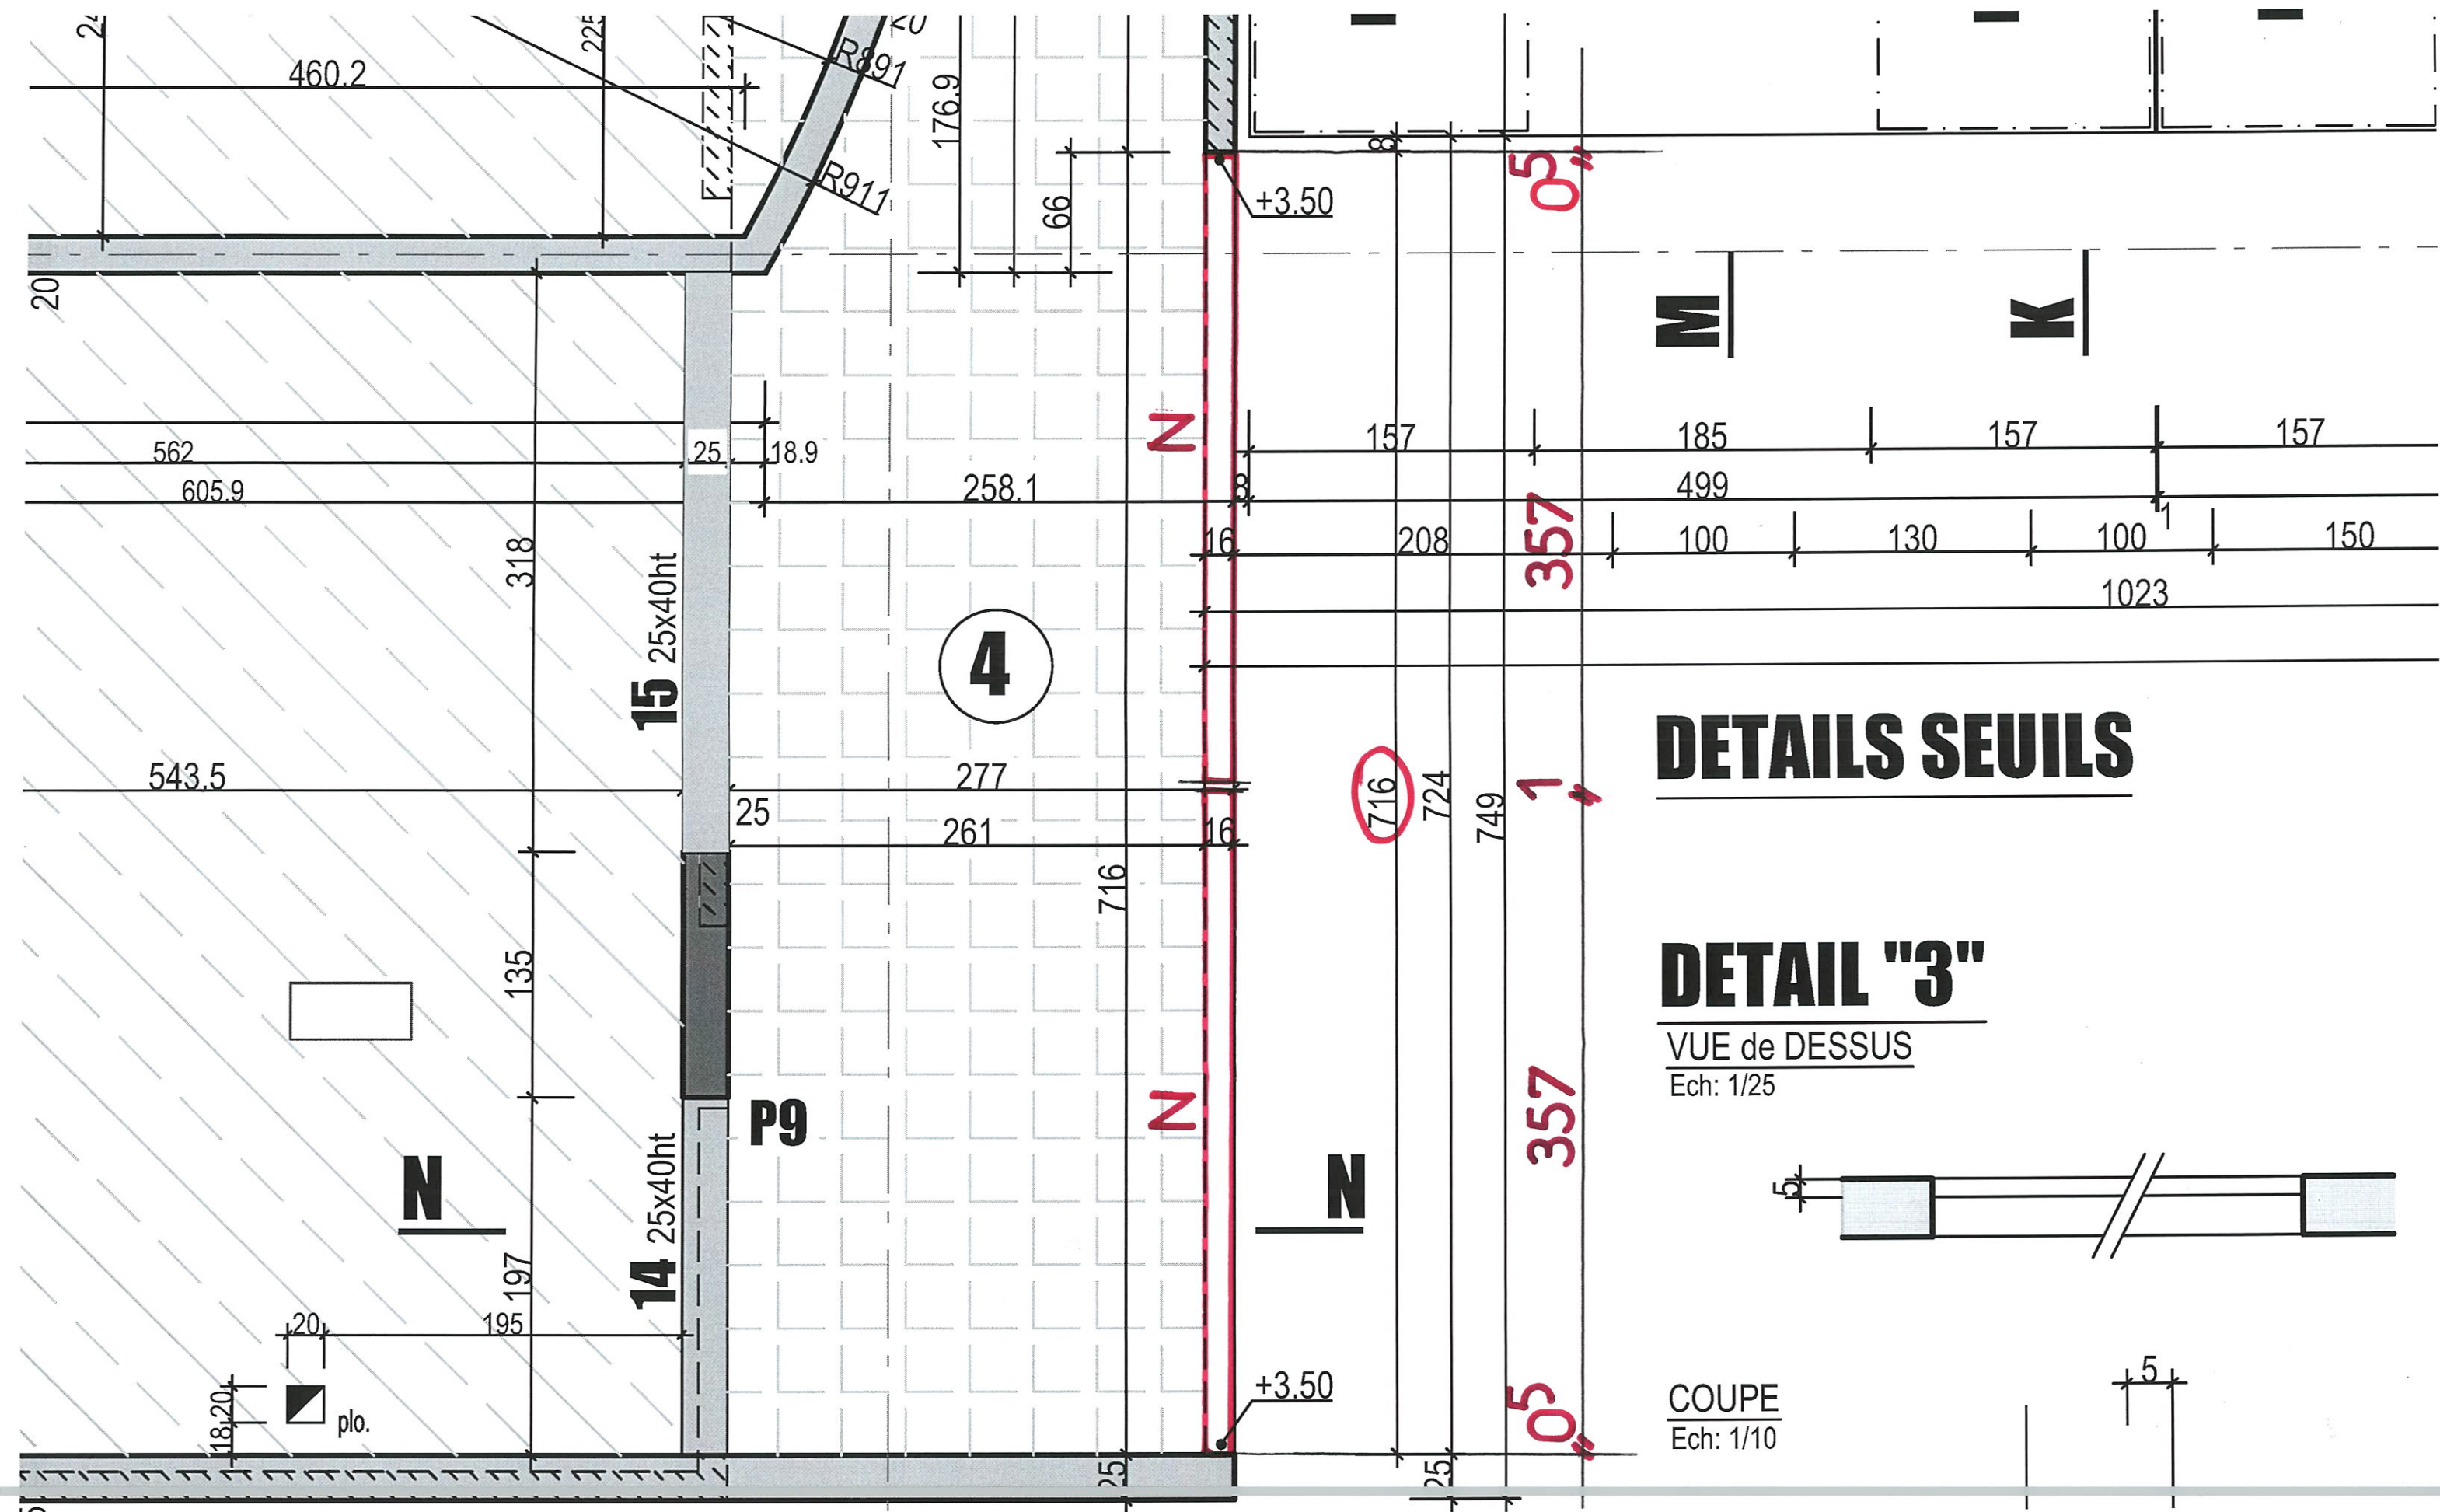


COUPE N

Ech: 1/25

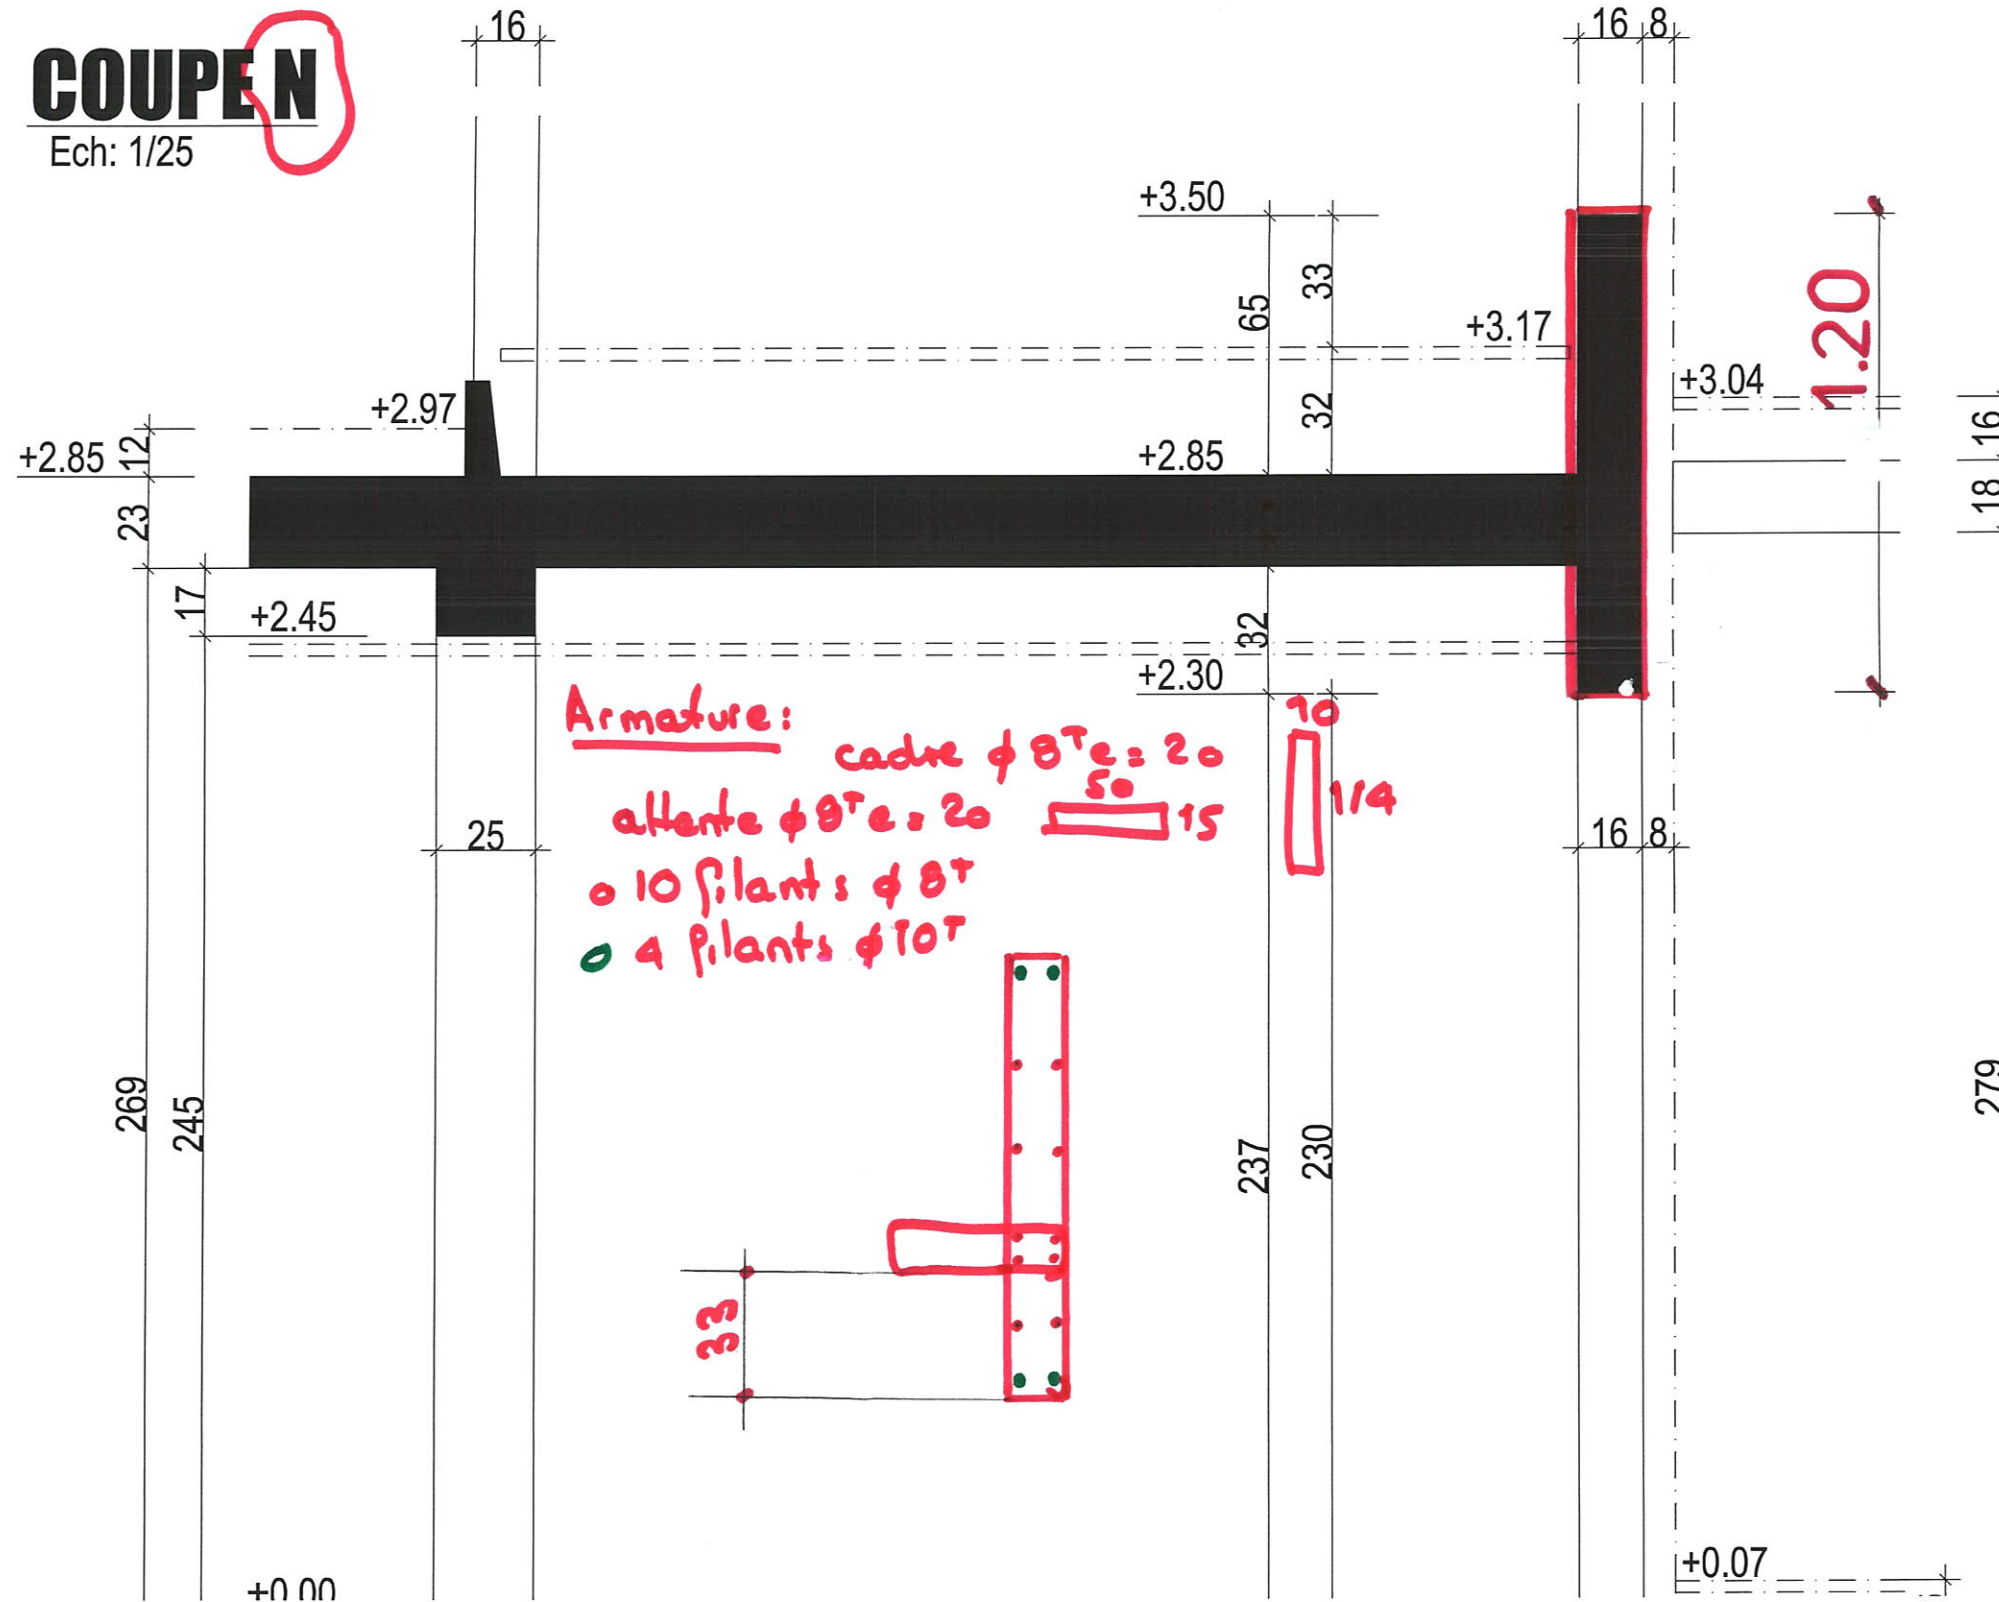


COUPE M


Ech: 1/25

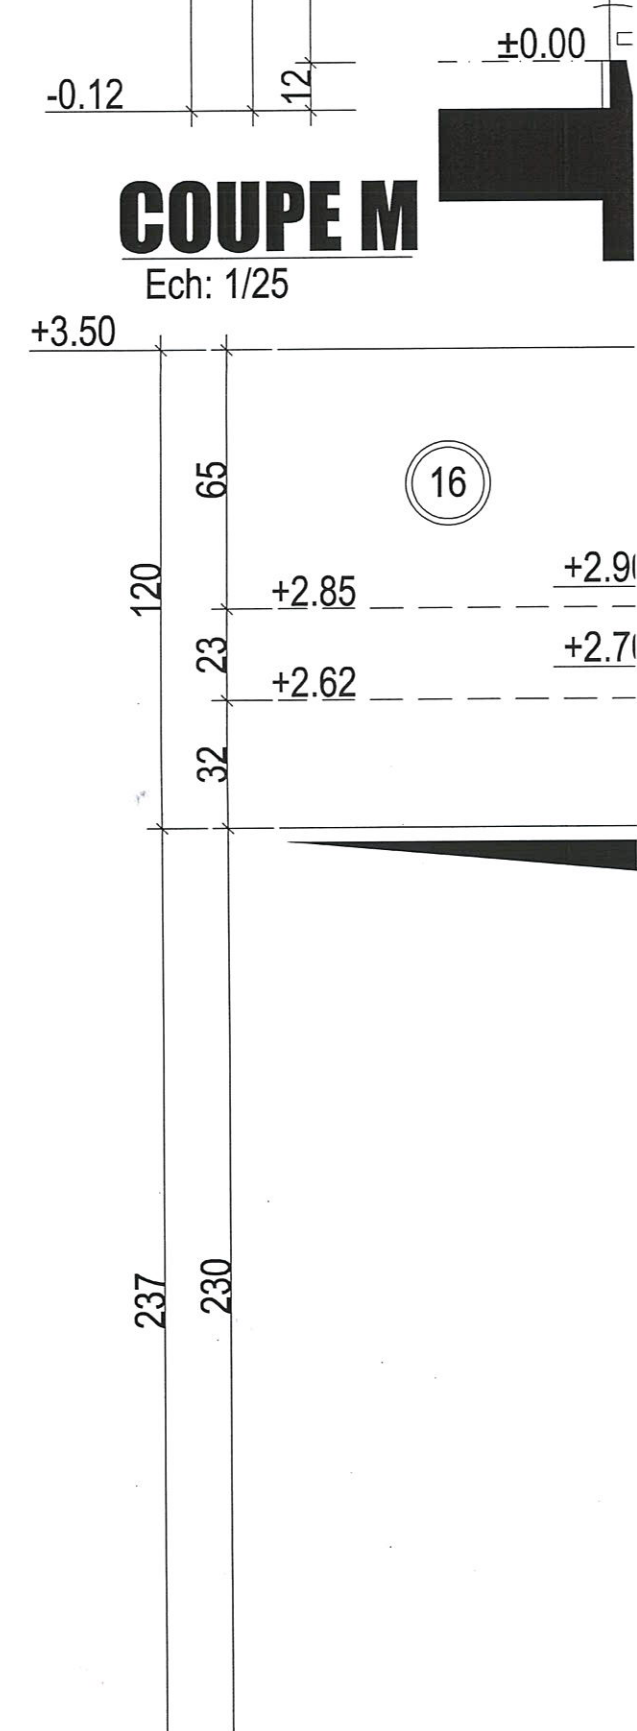


PLATTARD S.A.S.

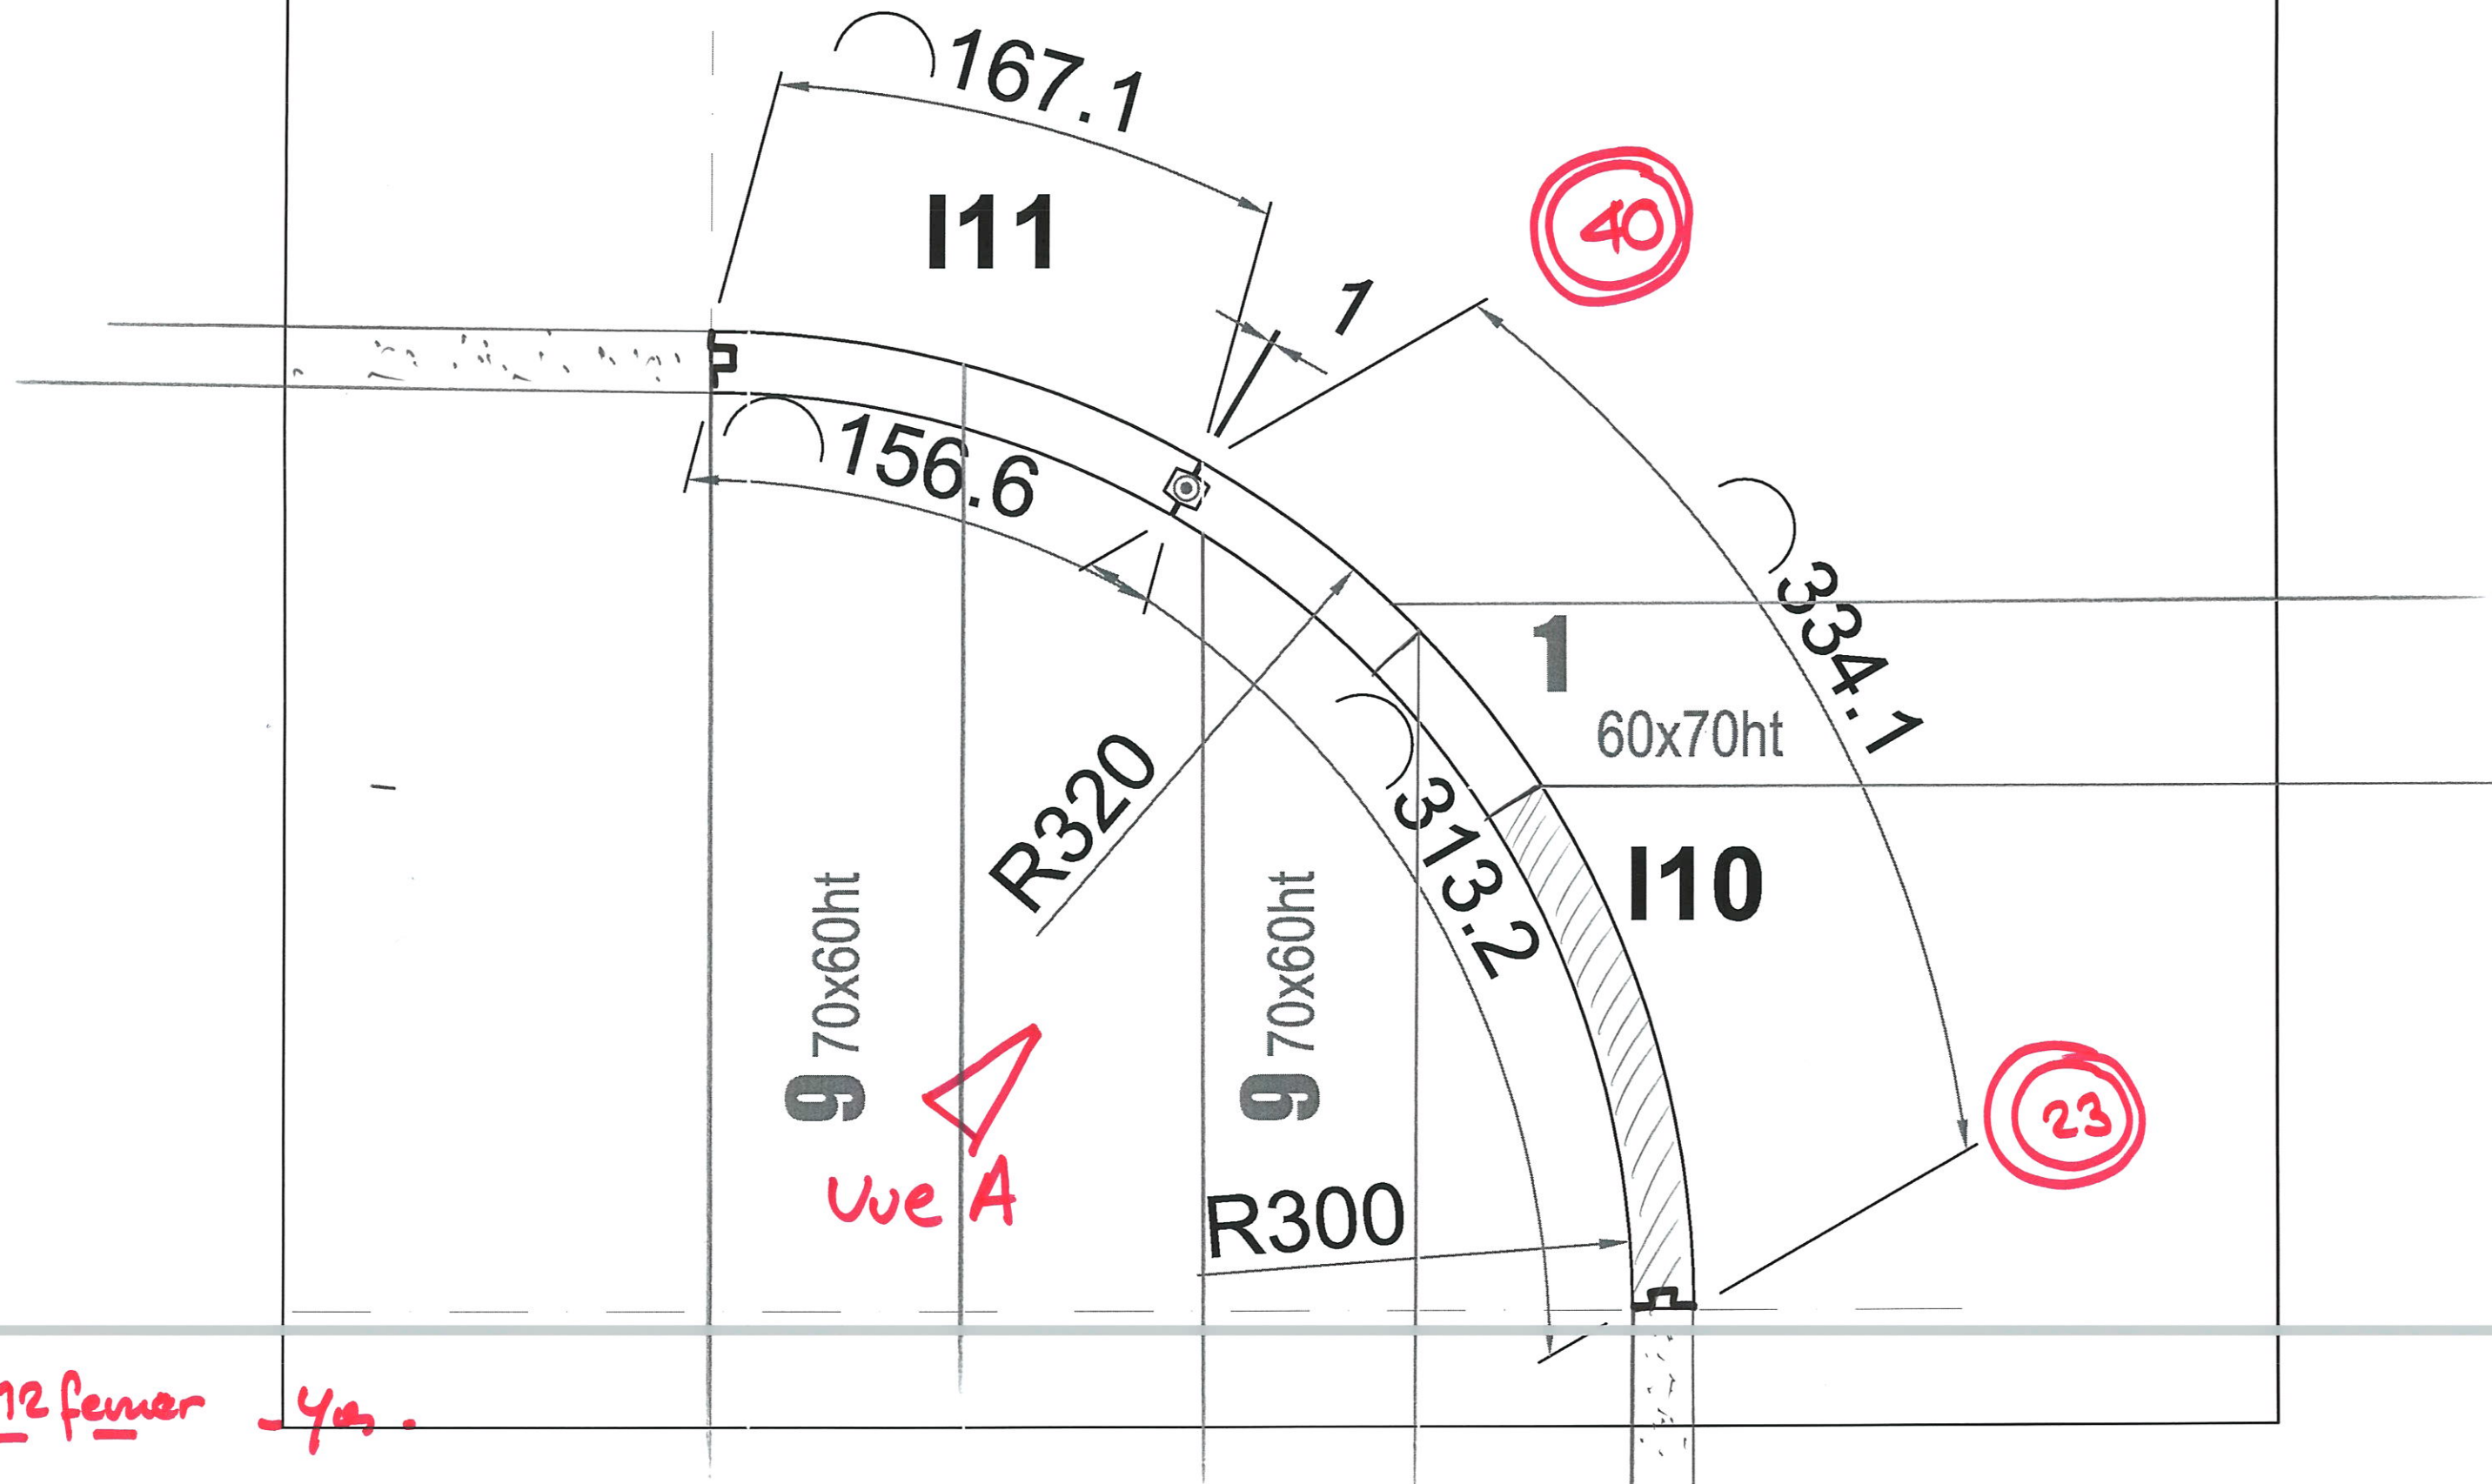

12 febru - Yes.


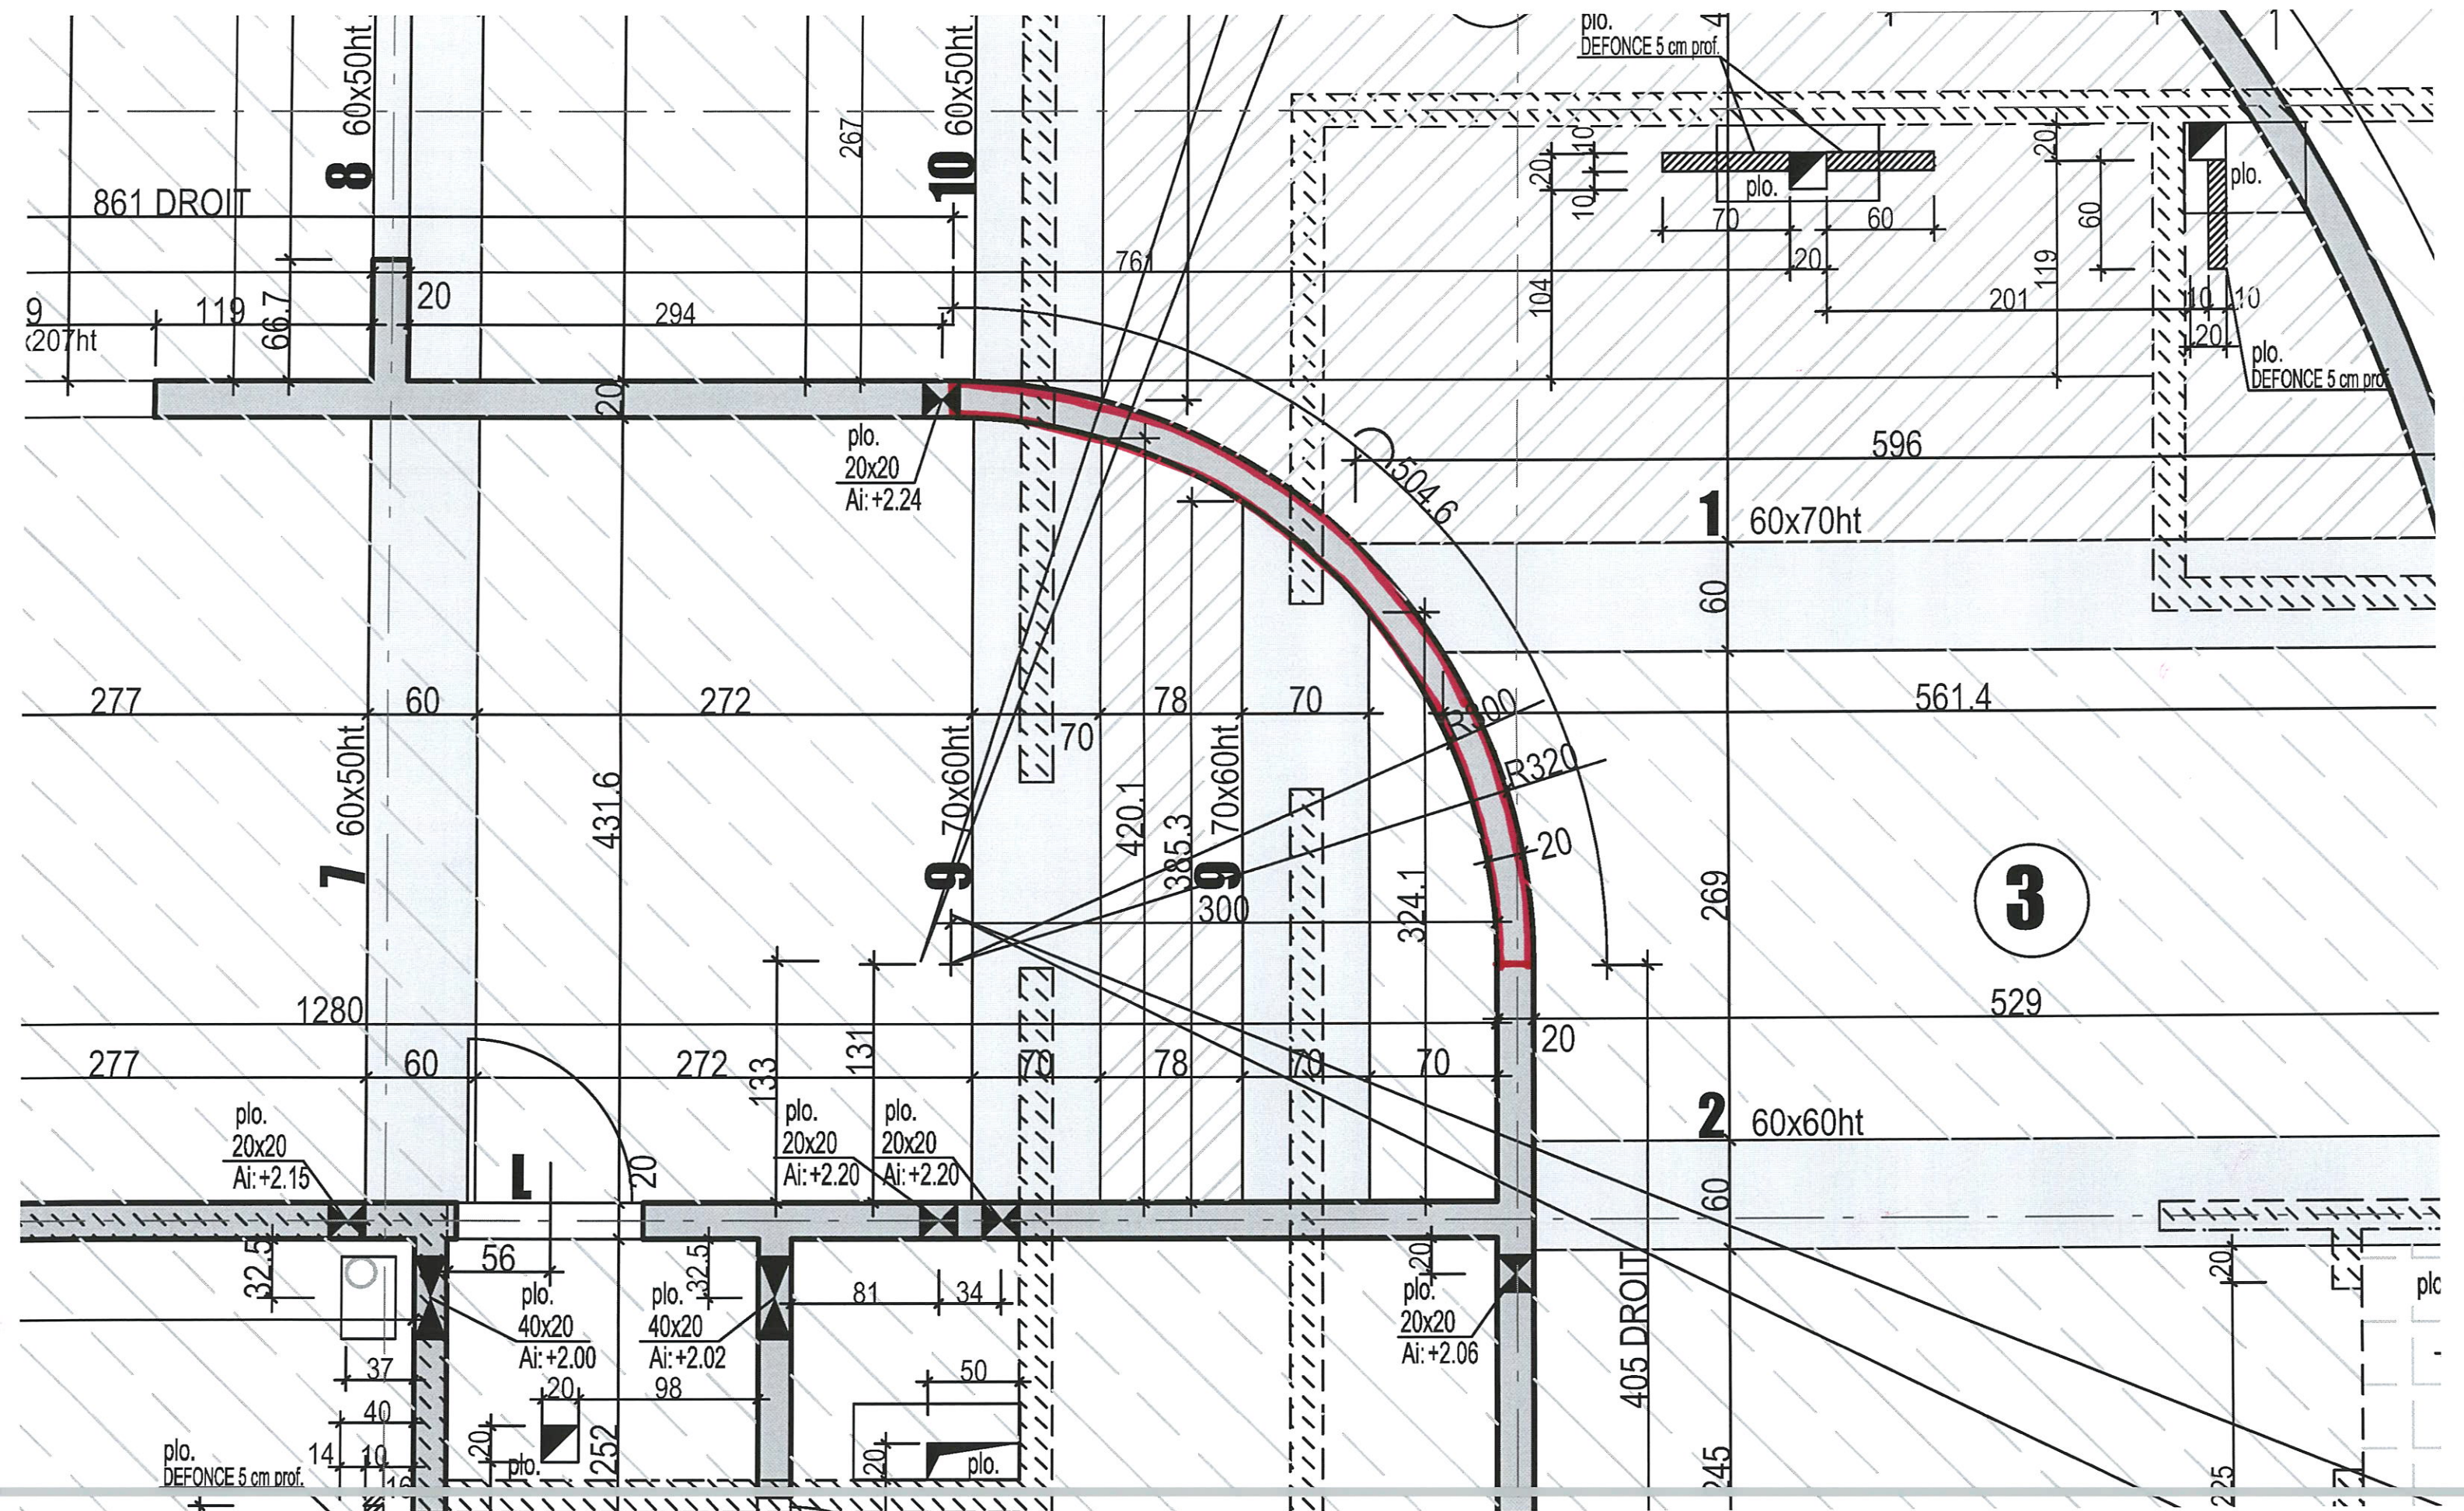



LE 180° - LA MULATIERE

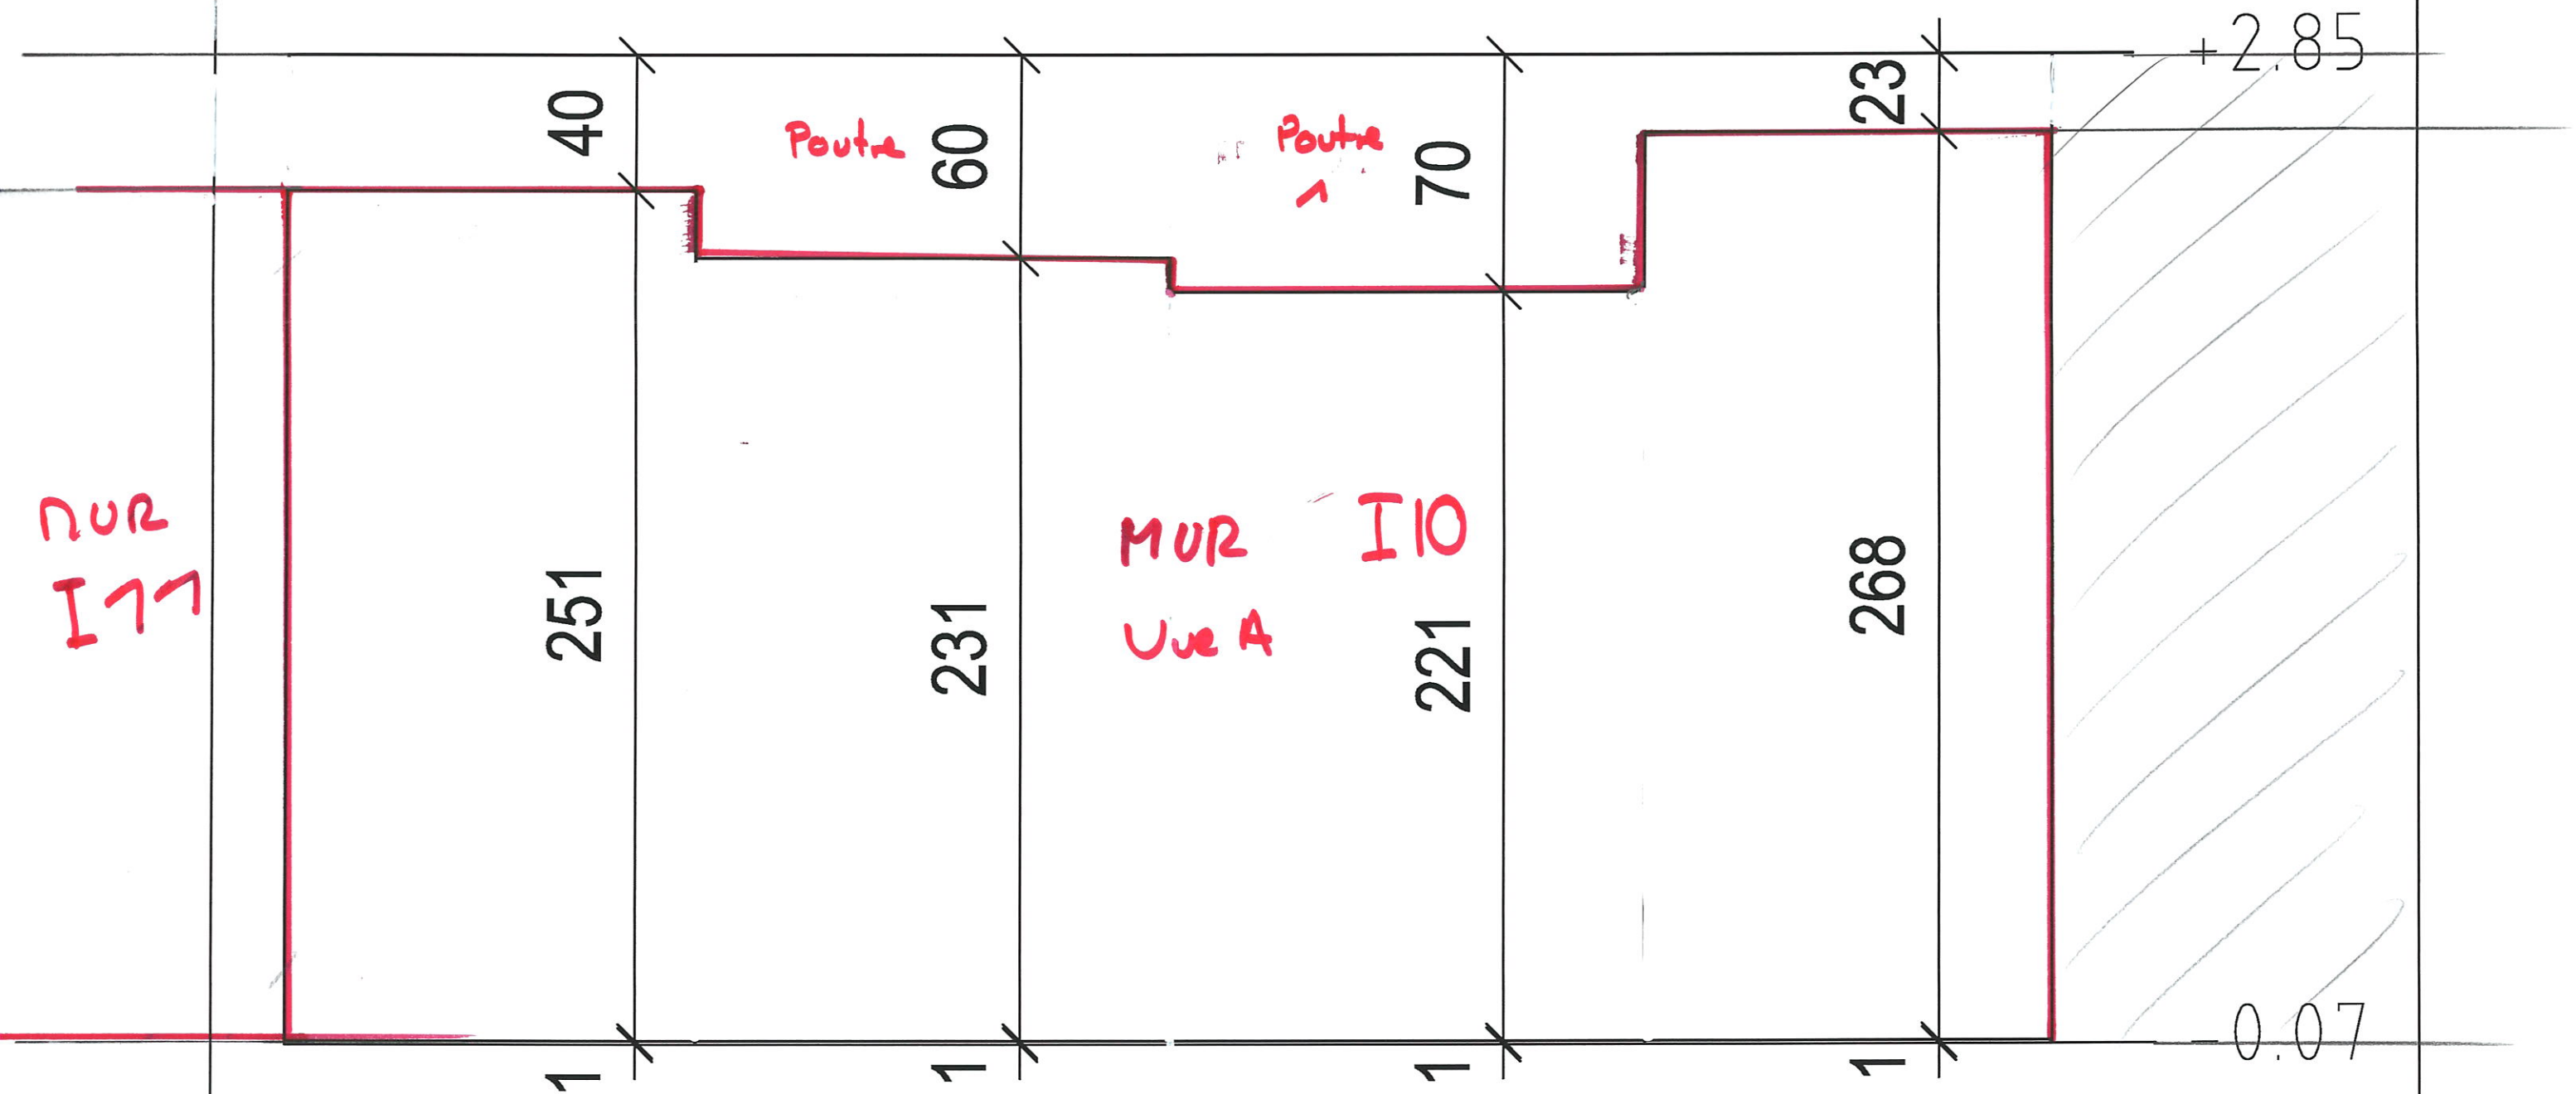

MOULE	N	NC	observations	CONTROLE	N	NC	observations	BETON	N	NC	observations	FICHE AUTO-CONTROLE	
Conformité moule				Dimensions				Conformité béton				Opérateur :	
Etat du moule				Armature				Mise en place				Responsable prod :	
Propreté et huilage				Inserts				Aspect de surface				Date :	


Ent. FONTANEL		Elément: PANNEAUX			FICHE DE FABRICATION	Surface: m²		POIDS		REPERE		Nbr	
180°- LA MULATIERE		ARRONDIS						1.92 T		111		1	
		coffrage				Volume: 0.80 m3							

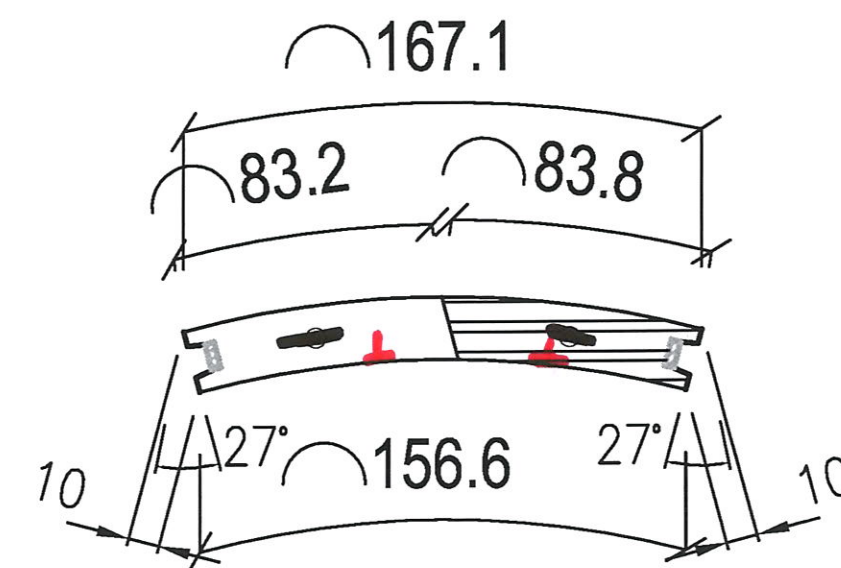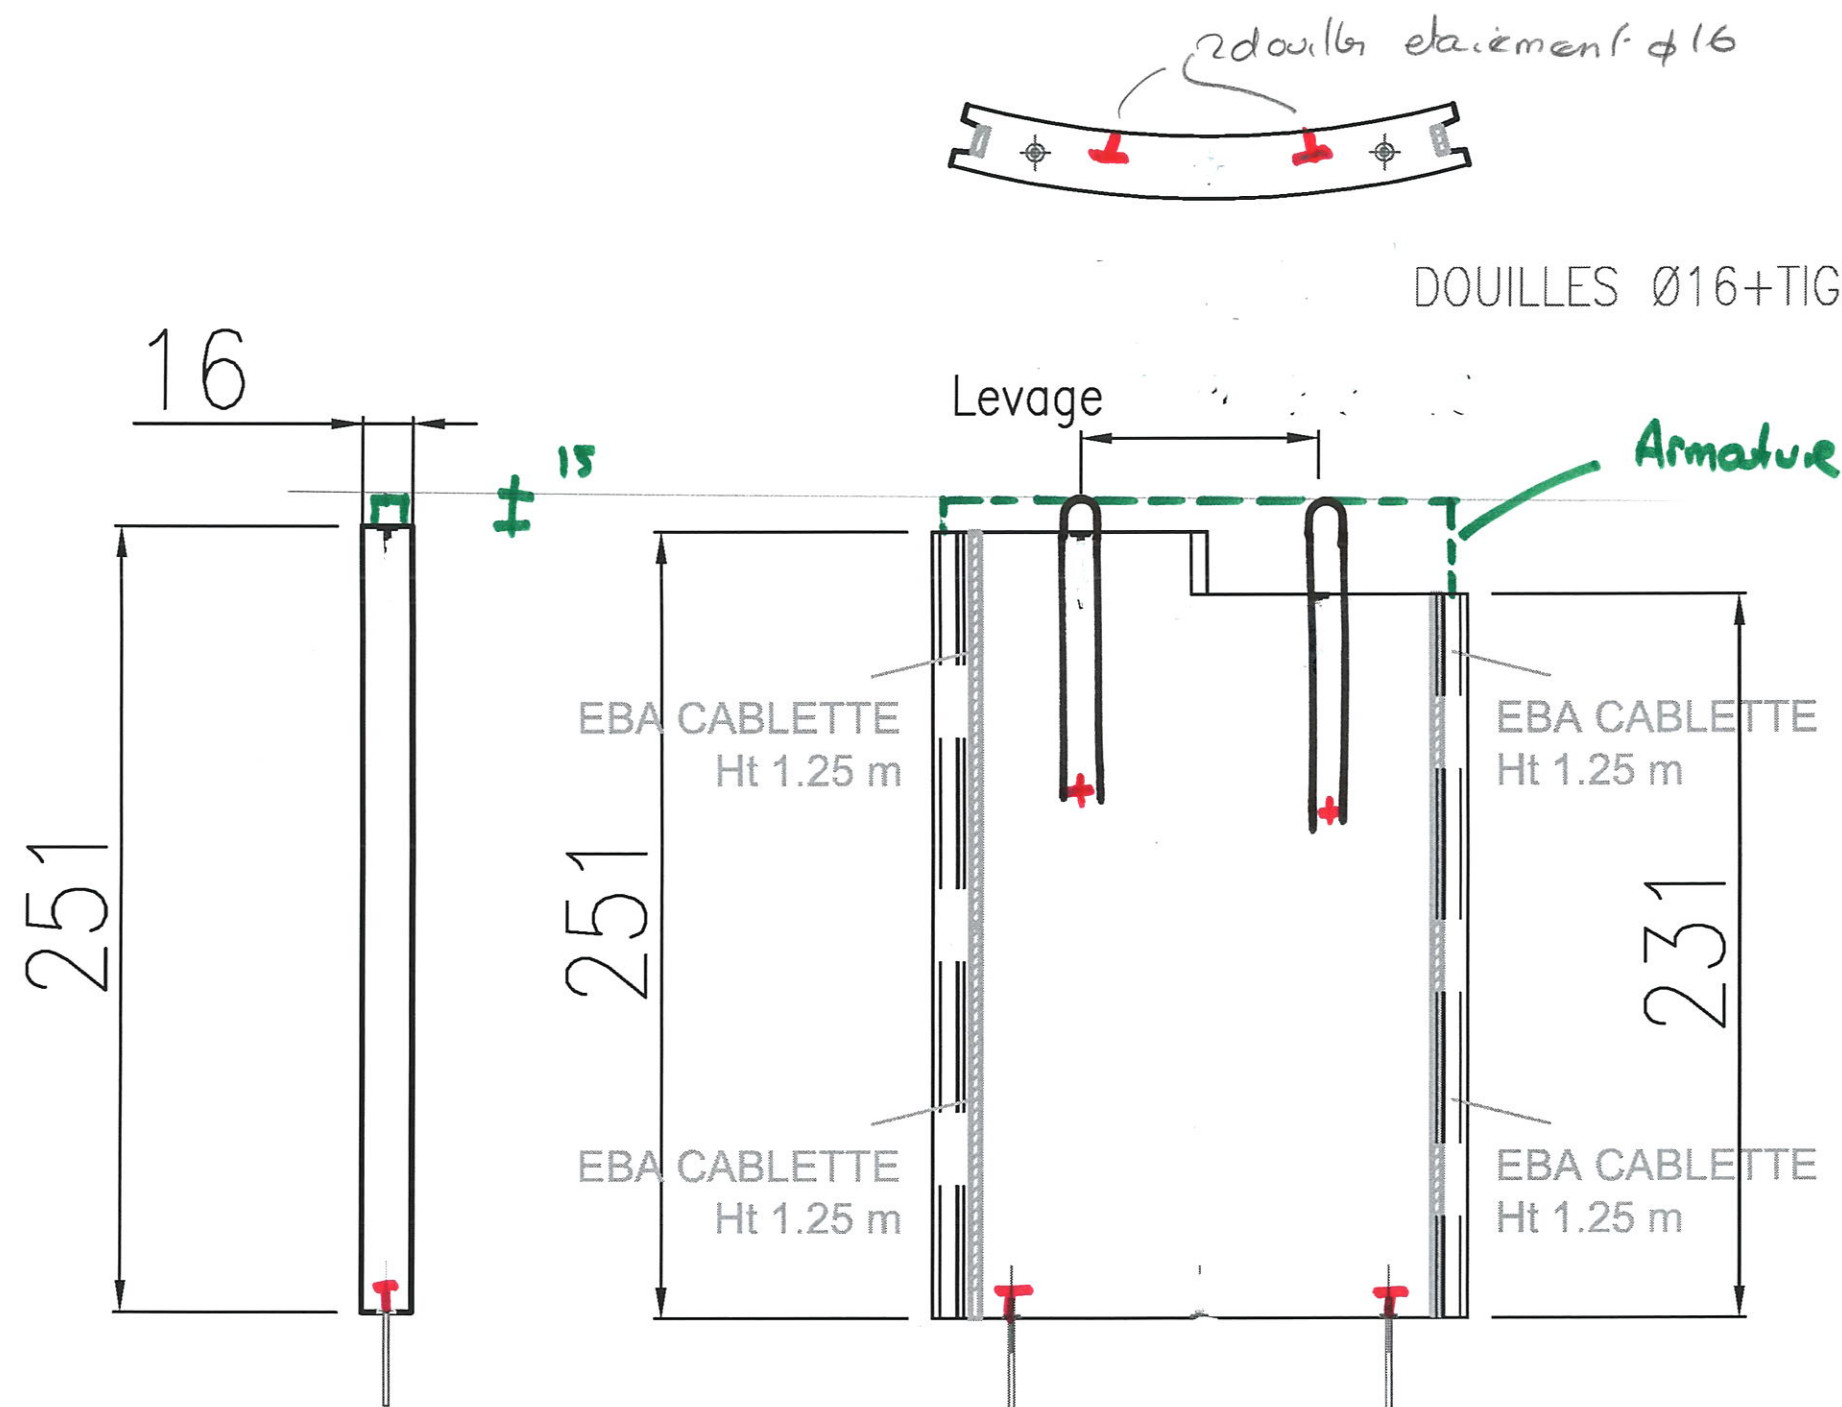


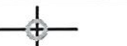LEVAGE		Douille Ø	INSERTS		Ancre Frimeda T	INSERTS		EBA	INSERTS		TP - JV	DATE: 02 / 12 / 2015	
		Douille Ø			Renfort Ø			Douille étalement			PVC Ø80	Plan N°	
		Renfort Ø dx			Trifer			Ankrobox Ø50			Tube garde-corps	Indice	

MOULE	N	NC	observations	CONTROLE	N	NC	observations	BETON	N	NC	observations	FICHE AUTO-CONTROLE	
Conformité moule				Dimensions				Conformité béton				Opérateur :	
Etat du moule				Armature				Mise en place				Responsable prod :	
Propreté et huilage				Inserts				Aspect de surface				Date :	

Ent. FONTANEL		Elément: PANNEAUX			FICHE DE FABRICATION	Surface: m²		POIDS	REPERE	Nbr
180°- LA MULATIERE		ARRONDIS					3.83 T	I10	1	
		coffrage				Volume: 1.60 m3				

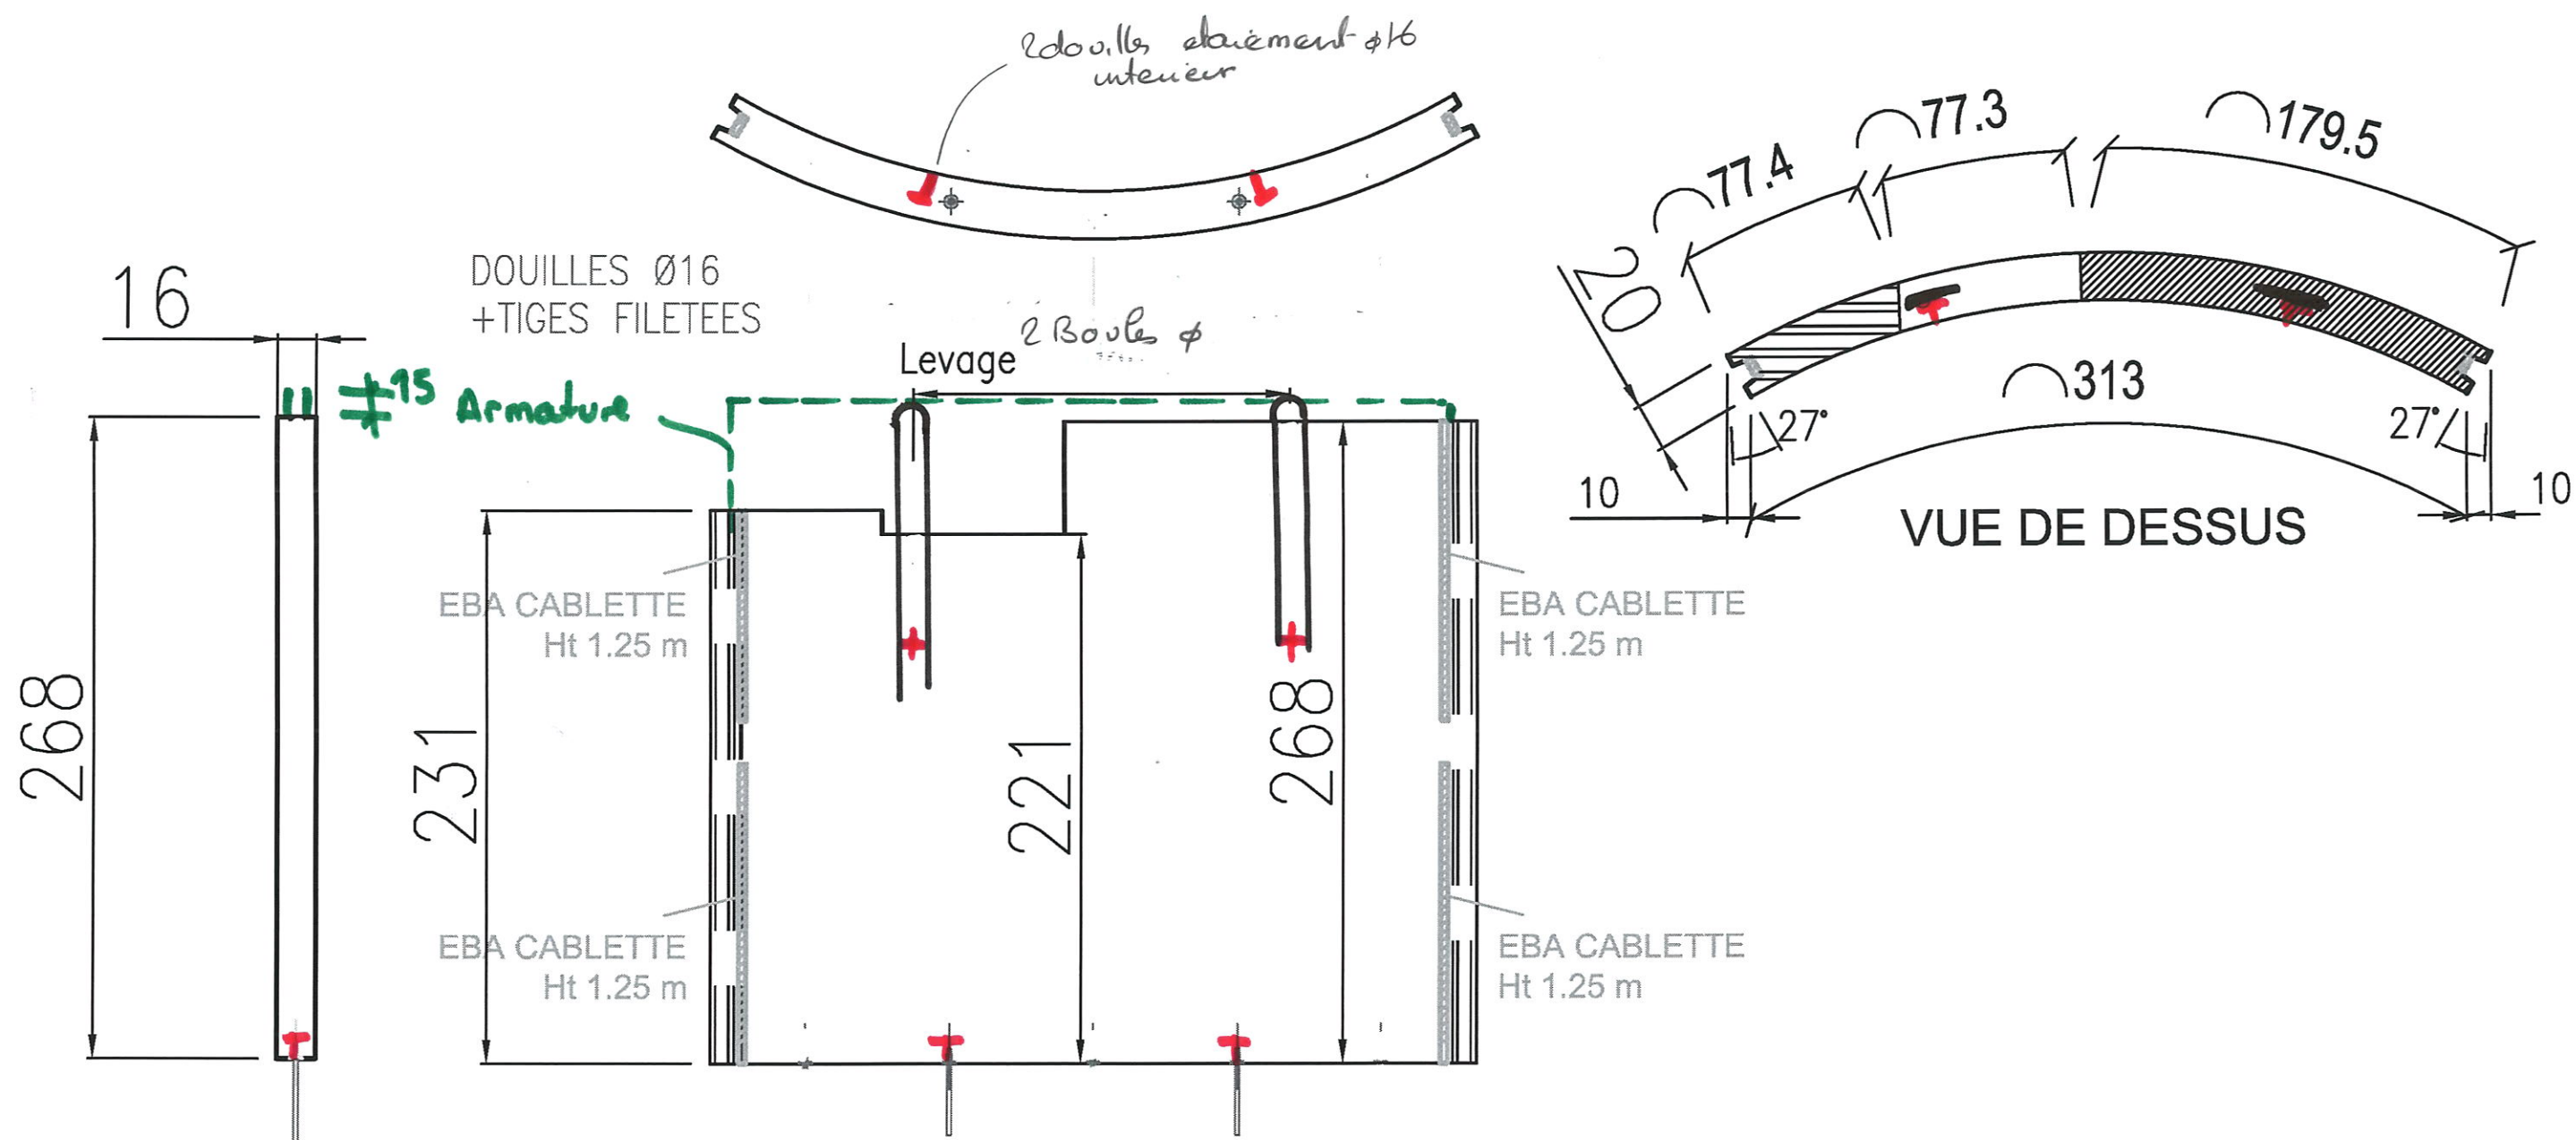

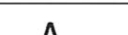LEVAGE		Douille Ø	INSERTS		Ancre Frimeda T	INSERTS		EBA	INSERTS		TP - JV	DATE: 02 / 12 / 2015	
		Douille Ø			Renfort Ø			Douille étalement			PVC Ø80	Plan N°	Page N°
		Renfort Ø dx			Trifer			Ankrobox Ø50			Tube garde-corps	Indice	