TABLEAU SEMELLES ISOLEES


Repère	Long. x Larg.	HT
S1	150 x 240	55
S2	120 x 240	55
S3		
S4	160 x 240	60
S5	110 x 400	50
S6	150 x 150	40

TABLEAU SEMELLES FILANTES


Repère	Larg.	HT
SF 50	50	30
SF 60		
SF 70	70	35
SFe 70	70	35

COUPES TYPES SEMELLES FILANTES


INTERIEURES

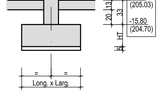

RIVES

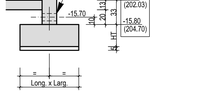

COUPES TYPES SEMELLES ISOLEES

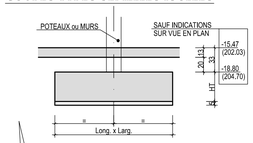

±0.00 = 220.50

NOAHO

Chemin de Fontanière - 69350 La Mulatière

Création de logements

Les entreprises réalisant les travaux devront tenir compte des derniers plans architecte lors de la réalisation des travaux
Les plans du be MATTE ne doivent servir qu'au corps d'état concerné et doivent être des plans d'exécution.

ARCHITECTE(S):	ATELIER DE LA PASSERELLE	MO DELEGUE:	
BET STRUCTURE:	MATTE SAS	MOE:	PSO Ingénierie
BET FLUIDES:	PRELEM	CSPS:	SUD EST COORDINATION
ECONOMISTE:	EXECO	OPC:	
BUREAU DE CONTROLE:	Bureau VERITAS	ENTREPRISE(S):	Fontanel-pbc

Bât: A
FONDATIONS au -5
Coffrage

DOE

Contrainte de sol: 8 bars ELS

Aciers HA (T) FeE500
Aciers Doux (Ø) FeE 235
Aciers TS FeE 500
Béton fc28 >= 25MPa
Enrobage = 3 cm


INDICE	DATE	MODIFICATIONS
A	29/09/2015	SUPPRIME BERLINOISE FILE 8
B	27/10/2015	MISE A JOUR SUIVANT B(dalle épr: 20 cm entre 7 et 8)

PLAN N°
A05 B
DATE : 3/09/2015

MATTÉ
BUREAU D'ETUDES
STRUCTURES ET FLUIDES
119 BOULEVARD STALINGRAD 69100 VILLEURBANNE
Tél. 04 72 44 02 87 Fax 04 72 44 26 59
E-mail : bet@matte.fr

Dessiné par : J.BO
Contrôlé par : S.BARRIERE
Echelle : 1/50"

Affaire N°
13.12.119

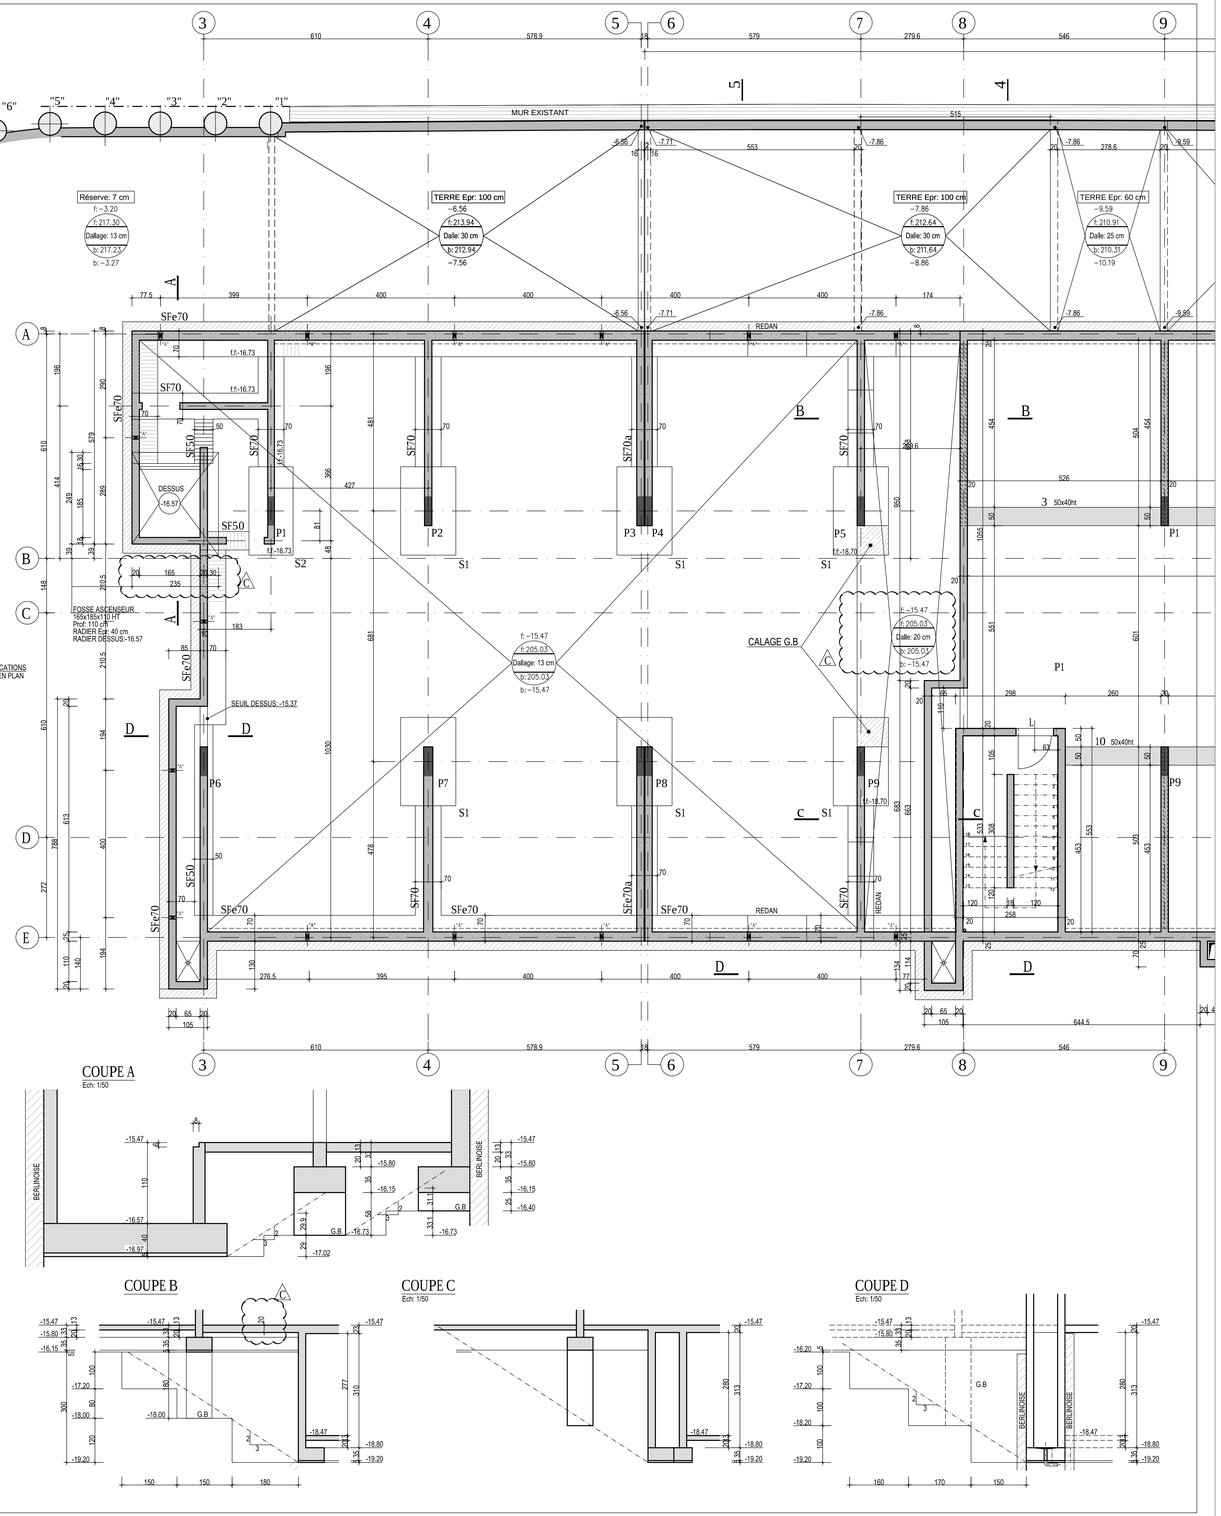

COUPE A
Ech: 1/50

COUPE B

COUPE C
Ech: 1/50

COUPE D
Ech: 1/50