DETAIL D'ABOUTS DE CHAINAGES INTERIEURS:

Position des équerres d'angles dans dalle 2 HA 14 x

vues en plan

chainage int. arrivant sur mur de façade

chainage int. arrivant sur mur int.

DETAIL D'ABOUTS DE CHAINAGES EN ANGLE SUR FACADES:

Position des équerres d'angles dans dalle 2 HA 14

coupe

vue en plan

RENFORTS RESERVATIONS JUSQU'A Ø200 mm

4HA10x1.50

Principe de renfort aux droits des gaines:

cote X

cote Y

2 HA 12 filants


2 HA 12 filants

NAPPE INFERIEURE ET SUPERIEURE

NOTA: Ces renforts sont en complément des aciers mis sur la vue en plan

PANNEAUX EN TIROIRS PREVOIR RECOUVREMENTS DECALES

EX: 1er Lit: 3 panneaux
2ème Lit: 1/2+2+1/2 panneaux
EN TIROIR

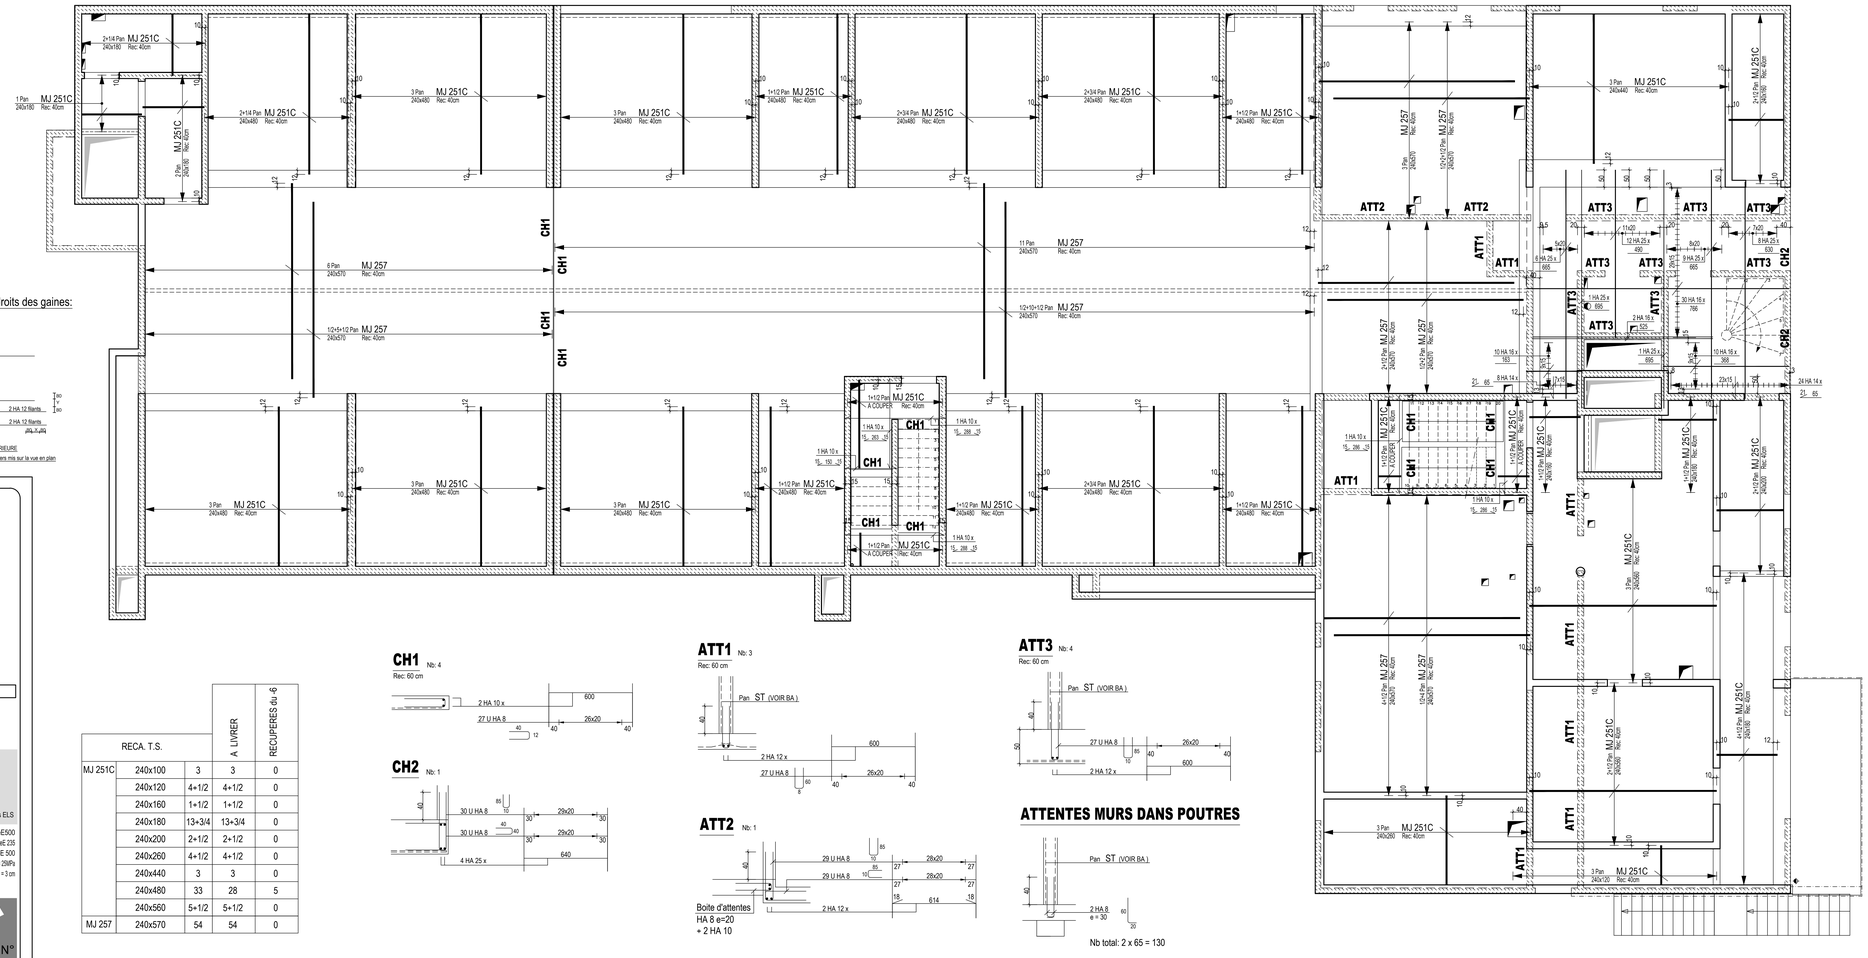

NOAHO

Chemin de Fontanière - 69350 La Mulatière

Création de logements

Les entreprises réalisant les travaux devront tenir compte des derniers plans architecte lors de la réalisation des travaux
Les plans du bx MATTE ne doivent servir qu'au corps d'état concerné et doivent être des plans d'exécution.

ARCHITECTE(S):	ATELIER DE LA PASSERELLE	MO DELEGUE:	
BET STRUCTURE:	MATTE SAS	MOE:	PSO Ingénierie
BET FLUIDES:	PRELEM	CSPS:	SUD EST COORDINATION
ECONOMISTE:	EXECO	OPC:	
BUREAU DE CONTROLE:	Bureau VERITAS	ENTREPRISE(S):	Fontanel-pbc

Bât: A

PLANCHER sur -5

Armatures Dalle Inf

DOE

Contrainte de sol: 8 bars ELS

Aciers HA (T) FeE500
Aciers Doux (D) FeE 235
Aciers TS FeE 500
Béton fc28 >= 25MPa
Enrobage = 3 cm

INDICE	DATE	MODIFICATIONS
A	01/11/2015	MISE A JOUR COMMANDE TS

PLAN N° A12 A

DATE : 29/10/2015

MATTÉ
BUREAU D'ETUDES
STRUCTURES ET FLUIDES
119 BOULEVARD STALINGRAD 69100 VILLEURBANNE
Tél. 04 72 44 02 87 Fax 04 72 44 26 59
E-mail : bet@matte.fr

Dessiné par : J.BO
Contrôlé par : P.LIN
Echelle : 1/50°

Affaire N° 13.12.119

	RECA. T.S.		A. LIVRER	RECUPERES ou -5
MJ 251C	240x100	3	3	0
	240x120	4+1/2	4+1/2	0
	240x160	1+1/2	1+1/2	0
	240x180	13+3/4	13+3/4	0
	240x200	2+1/2	2+1/2	0
	240x260	4+1/2	4+1/2	0
	240x440	3	3	0
	240x480	33	28	5
	240x560	5+1/2	5+1/2	0
MJ 257	240x570	54	54	0

CH1 Nb: 4
Rec: 60 cm

CH2 Nb: 1

ATT1 Nb: 3
Rec: 60 cm

ATT2 Nb: 1

Boite d'attentes
HA 8 e=20
+ 2 HA 10

ATT3 Nb: 4
Rec: 60 cm

ATTENTES MURS DANS POUTRES

Nb total: 2 x 65 = 130