DETAIL D'ABOUTS DE CHAINAGES INTERIEURS:

Position des équerres d'angles dans dalle 2 HA 14 x

100 / 100 à plat

vues en plan

chainage int. arrivant sur mur de façade



chainage int. arrivant sur mur int.



DETAIL D'ABOUTS DE CHAINAGES EN ANGLE SUR FACADES:


Position des équerres d'angles dans dalle 2 HA 14

x 100 / 100 à plat

coupe



vue en plan

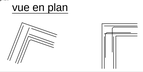


RENFORTS RESESERVATIONS JUSQU'A Ø200 mm

PANNEAUX EN TIROIRS PREVOIR RECOUVREMENTS DECALES

EX: 1er Lit: 3 panneaux
2ème Lit: 1/2+2+1/2 panneaux
} EN TIROIR

Principe de renfort aux droits des gaines:

NOTA: Ces renforts sont en complément des aciers mis sur la vue en plan

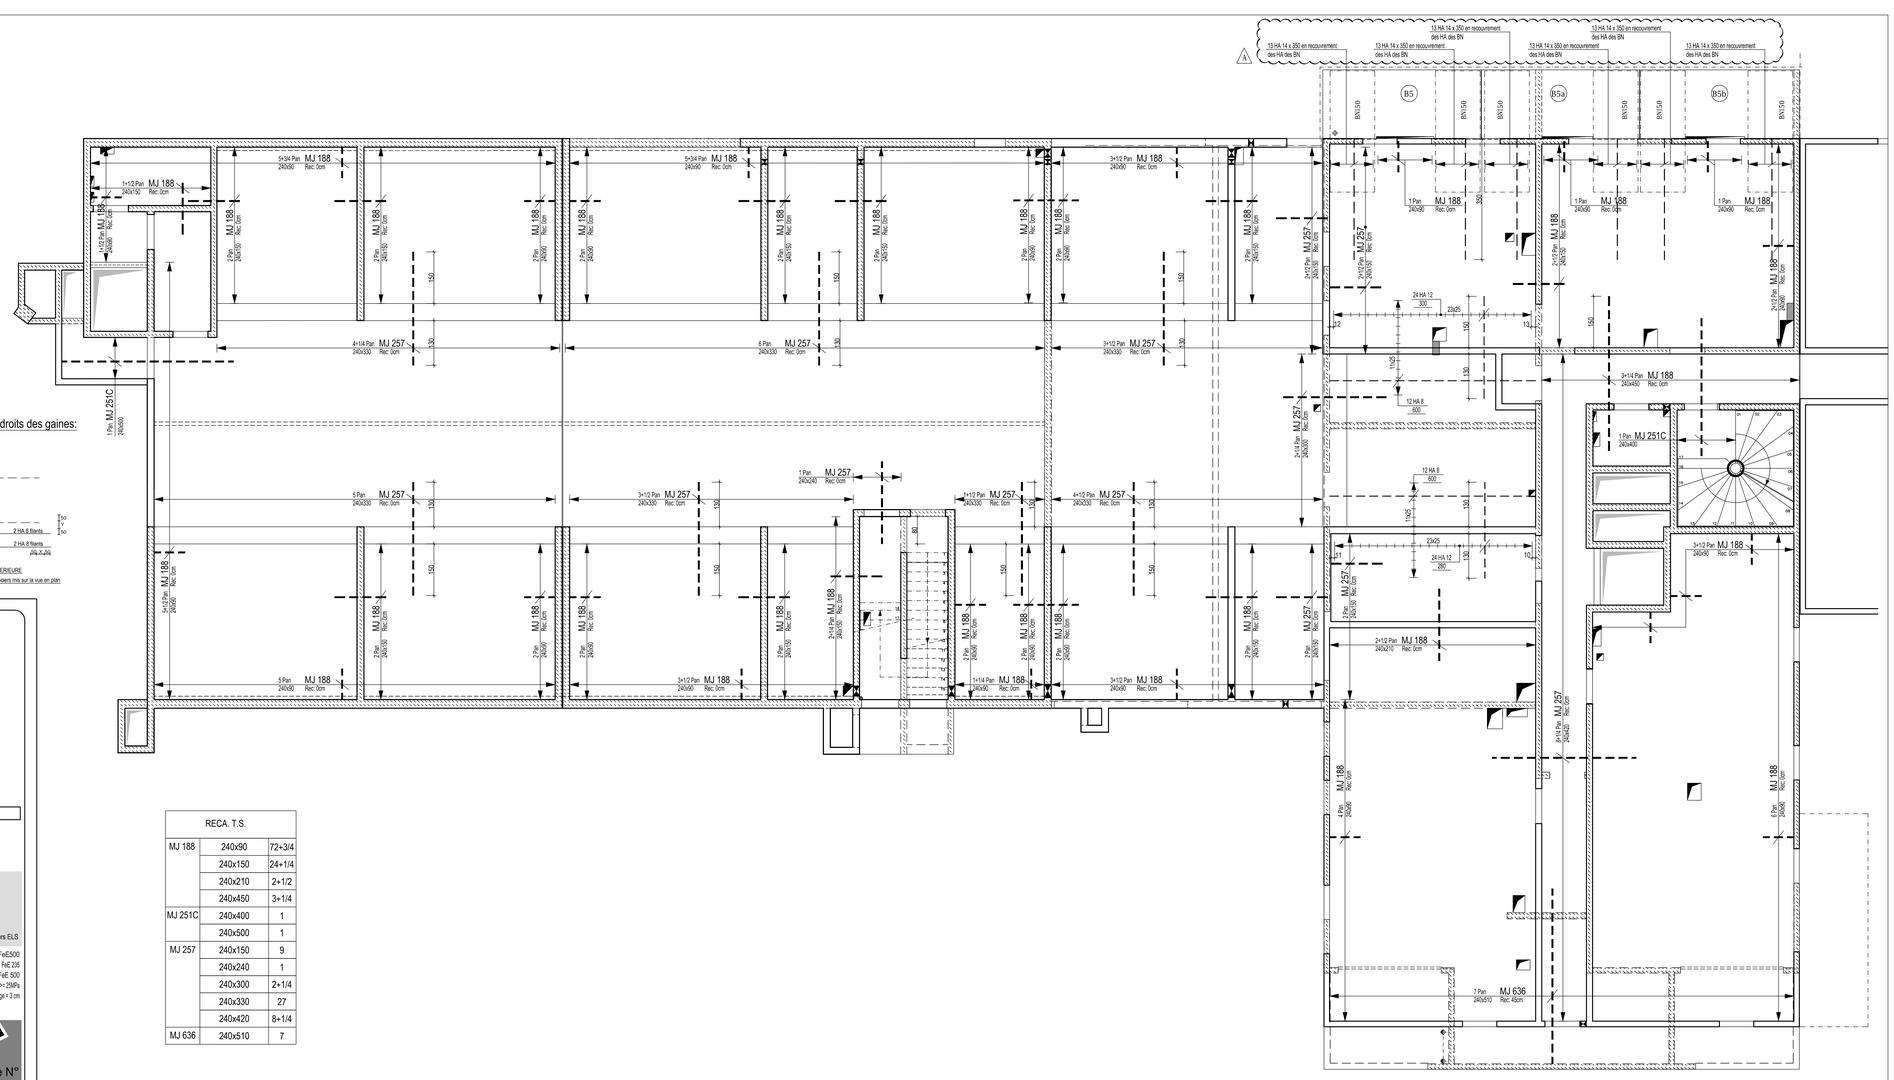

RECA. T.S.		
MJ 188	240x90	72+3/4
	240x150	24+1/4
	240x210	2+1/2
	240x450	3+1/4
MJ 251C	240x400	1
	240x500	1
MJ 257	240x150	9
	240x240	1
	240x300	2+1/4
	240x330	27
	240x420	8+1/4
MJ 636	240x510	7

NOAHO

Chemin de Fontanière - 69350 La Mulatière

Création de logements

Les entreprises réalisant les travaux devront tenir compte des derniers plans architecte lors de la réalisation des travaux.
Les plans du be MATTE ne doivent servir qu'au corps d'état concerné et doivent être des plans d'exécution.

ARCHITECTE(S):	ATELIER DE LA PASSERELLE	MO DELEGUE:	
BET STRUCTURE:	MATTE SAS	MOE:	PSO Ingénierie
BET FLUIDES:	PRELEM	CSPS:	SUD EST COORDINATION
ECONOMISTE:	EXECO	OPC:	
BUREAU DE CONTROLE:	Bureau VERITAS	ENTREPRISE(S):	Fontanel-pbc

Bât: A

PLANCHER sur -4

Armatures Dalle Sup

DOE

Contrainte de sol: 8 bars ELS

Aciers HA (T) FeE500
Aciers Doux (D) FeE 235
Aciers TS FeE 500
Béton fc28 >= 25MPa
Enrobage = 3 cm

PLAN N°
A18 A
DATE : 20/11/2015

INDICE	DATE	MODIFICATIONS
A	24/11/2015	MISE A JOUR SUIVANT A (ajouté HA 14 pour balcon)

MATTÉ
BUREAU D'ÉTUDES
STRUCTURES ET FLUIDES
119 BOULEVARD STALINGRAD 69100 VILLEURBANNE
Tél: 04 72 44 02 87 Fax 04 72 44 26 59
E-mail : bet@matte.fr

Dessiné par : J.BO
Contrôlé par : P.LIN
Echelle : 1/50°

Affaire N°
13.12.119