

ARMATURES SUPERIEURES

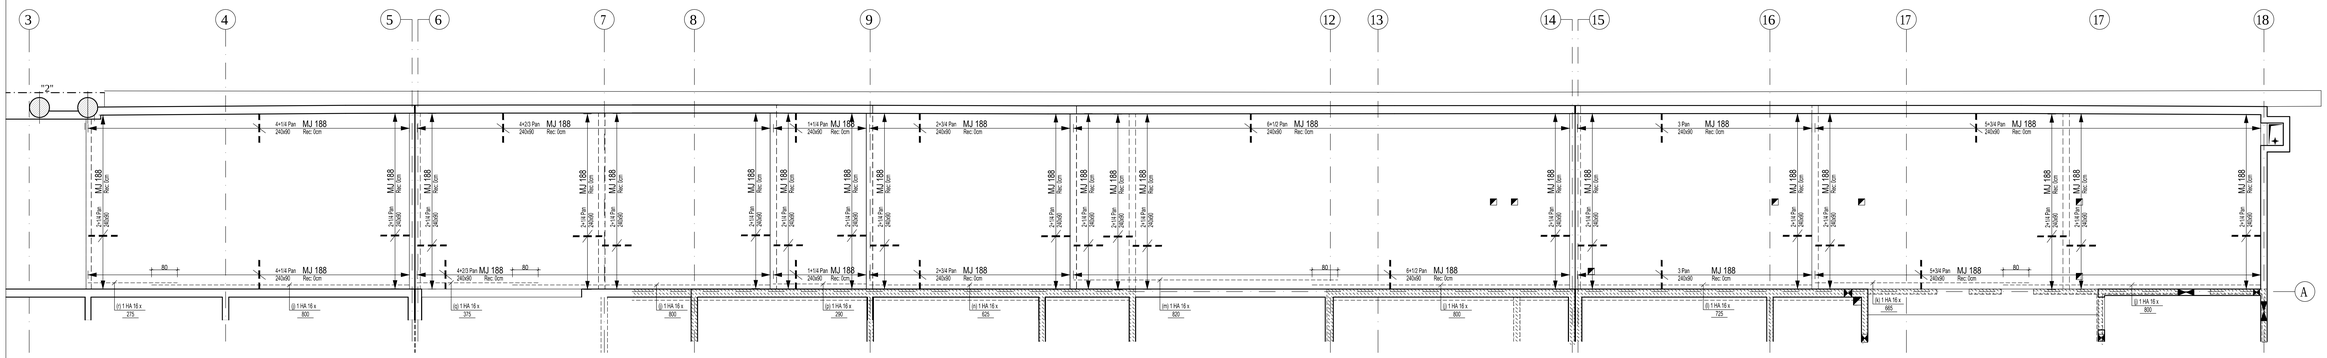


ARMATURES INFERIEURES

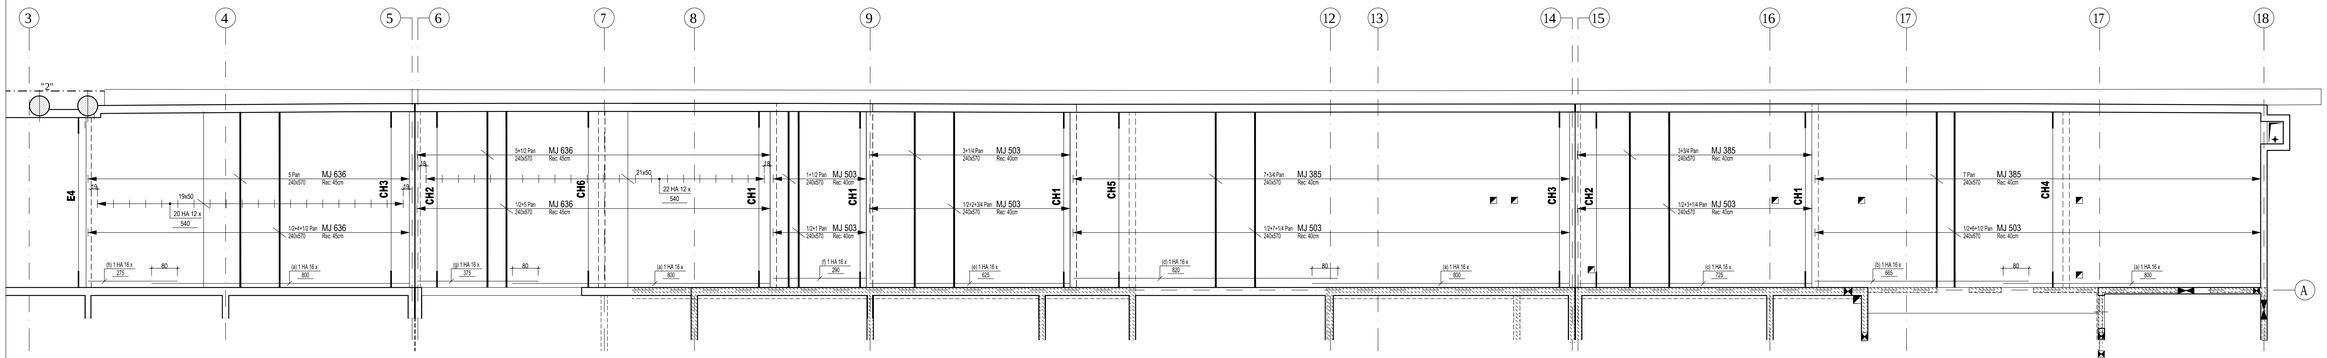


PANNEAUX EN TIROIRS PREVOIR RECOUVREMENTS DECALES
EX: 1er Lit: 3 panneaux
2ème Lit: 1/2+2+1/2 panneaux
EN TIROIR


CH1 Nb: 4

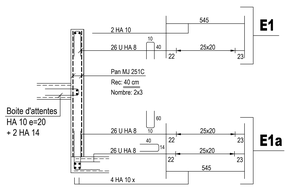


CH2 Nb: 2

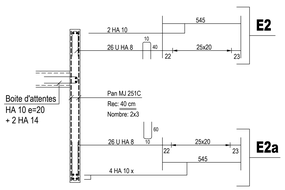


CH3 Nb: 2

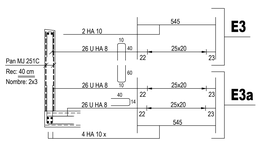


CH4 Nb: 1

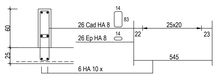


CH5 Nb: 1

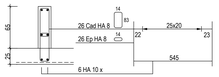

CH6 Nb: 1

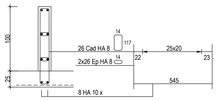

E4 Nb: 1

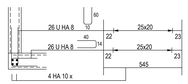

Détail aciers de renforts dans dalle



RENFORTS RESERVATIONS JUSQU'A Ø200 mm

Principe de renfort aux droits des gaines:



NOTA: Ces renforts sont en complément des aciers mis sur la vue en plan

DETAIL D'ABOUTS DE CHAINAGES INTERIEURS:

Position des équerres d'angles dans dalle 2 HA 14 x 100 à pied

vues en plan



DETAIL D'ABOUTS DE CHAINAGES EN ANGLE SUR FACADES:

Position des équerres d'angles dans dalle 2 HA 14 x 100 à pied

coupe vue en plan



NOAHO

Chemin de Fontanière - 69350 La Mulatière

Création de logements

Les entreprises réalisant les travaux devront tenir compte des derniers plans architecte lors de la réalisation des travaux
Les plans du bet MATTE ne doivent servir qu'au corps d'état concerné et doivent être des plans d'exécution.

ARCHITECTE(S):	ATELIER DE LA PASSERELLE	MO DELEGUE:	
BET STRUCTURE:	MATTE SAS	MOE:	PSO Ingénierie
BET FLUIDES:	PRELEM	CSPS:	SUD EST COORDINATION
ECONOMISTE:	EXECO	OPC:	
BUREAU DE CONTROLE:	Bureau VERITAS	ENTREPRISE(S):	Fontanel-pbc

Bât: B et A

DALLES sur RAMPE NORD

ARMATURES DALLE

DOE

Contrainte de sol: 8 bars ELS

Aciers HA (T) FeE500
Aciers Doux (Ø) FeE 235
Aciers TS FeE 500
Béton fc28 >= 25MPa
Enrobage = 3 cm

INDICE	DATE	MODIFICATIONS

PLAN N° B04 0

DATE : 09/10/2015

MATTÉ
BUREAU D'ÉTUDES
STRUCTURES ET FLUIDES
119 BOULEVARD STALINGRAD 69100 VILLEURBANNE
Tél. 04 37 44 02 87 Fax 04 72 44 28 00
E-mail : bet@matte.fr

Dessiné par : J.BO
Contrôlé par : P.LIN
Echelle 1/50°

Affaire N° 13.12.119