RECA. T.S.

MJ 131	150x240	0
	180x240	0
	210x240	0
MJ 188	390x240	0
	510x240	0
	540x240	0
	90x240	0
	150x240	0
	210x240	0
	300x240	0
	450x240	0
MJ 257	450x240	0
	520x240	0
	600x240	0
MJ 2510	330x240	0
	480x240	0
	620x240	0

DETAIL D'ABOUTS DE CHAINAGES INTERIEURS:

Position des équerres d'angles dans dalle 2 HA 14 x 100 / 100 à plat

vues en plan

chaînage int. arrivant sur mur de façade



chaînage int. arrivant sur mur int.




DETAIL D'ABOUTS DE CHAINAGES EN ANGLE SUR FACADES:

Position des équerres d'angles dans dalle 2 HA 14

x 100 / 100 à plat


coupe

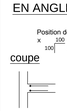


vue en plan



RENFORTS RESESERVATIONS JUSQU'A Ø200 mm

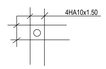

Principe de renfort aux droits des gaines:

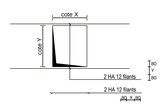


PANNEAUX EN TIROIRS PREVOIR RECOUVREMENTS DECALES

EX: 1er Lit: 3 panneaux
2ème Lit: 1/2+2+1/2 panneaux
EN TIROIR

NAPPE INFERIEURE ET SUPERIEURE

NOTA: Ces renforts sont en complément des aciers mis sur la vue en plan

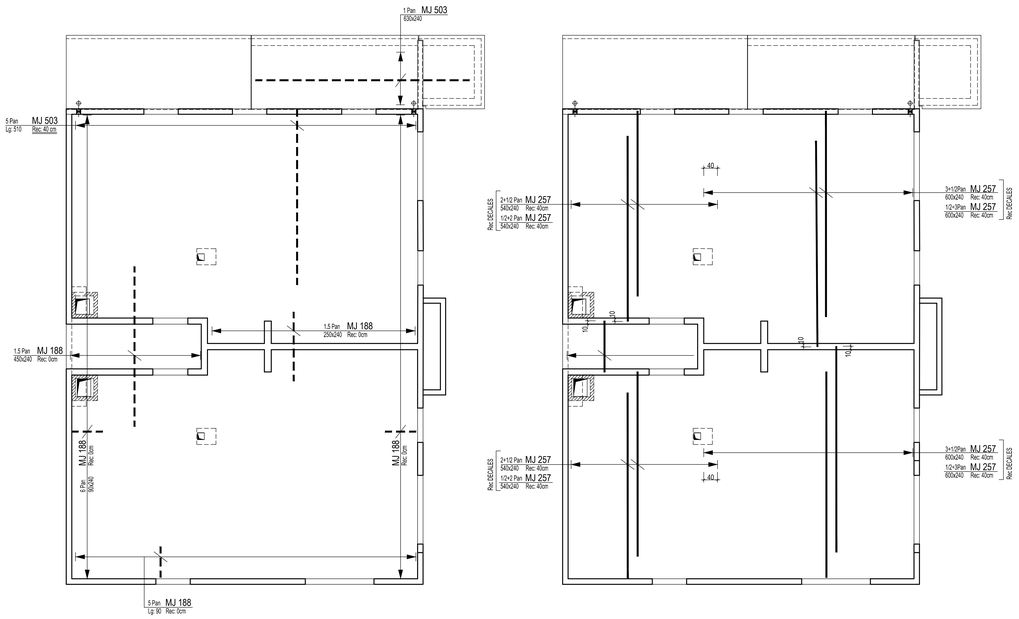

NOAHO

Chemin de Fontanière - 69350 La Mulatière

Création de logements

Les entreprises réalisant les travaux devront tenir compte des derniers plans architecte lors de la réalisation des travaux
Les plans du be MATTE ne doivent servir qu'au corps d'état concerné et doivent être des plans d'exécution.

ARCHITECTE(S):	ATELIER DE LA PASSERELLE	MO DELEGUE:	
BET STRUCTURE:	MATTE SAS	MOE:	PSO Ingénierie
BET FLUIDES:	PRELEM	CSPS:	SUD EST COORDINATION
ECONOMISTE:	EXECO	OPC:	
BUREAU DE CONTROLE:	Bureau VERITAS	ENTREPRISE(S):	Fontanel-pbc

Bât: A

PLANCHER sur -1 entre files 14 et 19

Armatures dalle

DOE

Contrainte de sol 8 bars ELS

Aciers HA (T) FeE500
Aciers Doux (Ø) FeE 235
Aciers TS FeE 500
Béton fc28 >= 25MPa
Enrobage = 3 cm

INDICE	DATE	MODIFICATIONS

PLAN N°

B 39 0

DATE : 31/03/2016

MATTÉ

BUREAU D'ETUDES

STRUCTURES ET FLUIDES

119 BOULEVARD STALINGRAD 69100 VILLEURBANNE
Tél. 04 72 44 02 87 Fax 04 72 44 26 59
E-mail : bet@matte.fr

Dessiné par : J.BO
Contrôlé par : P.LIN
Echelle : 1/50°

Affaire N°
13.12.119