


COUPE 4
Ech: 1/50

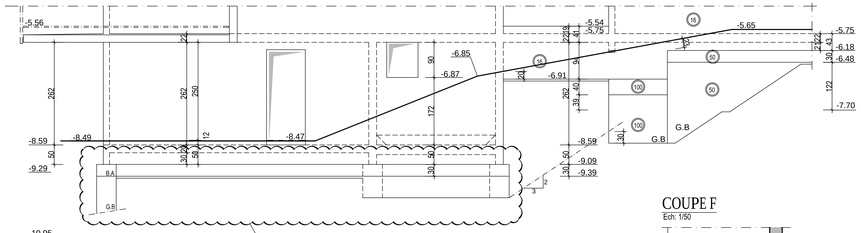


COUPE 3
Ech: 1/50

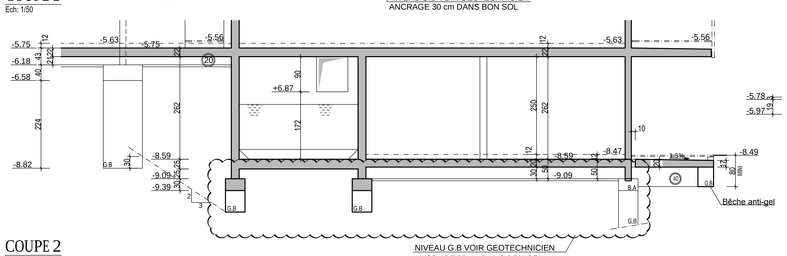


COUPE 2
Ech: 1/50

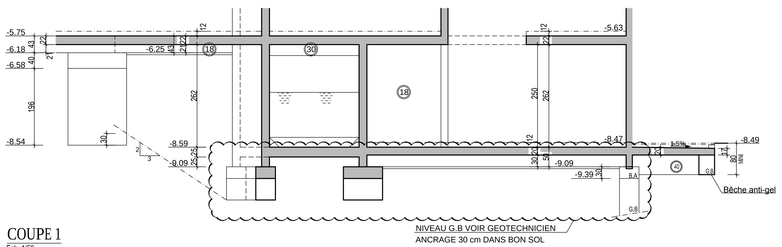


COUPE 1
Ech: 1/50

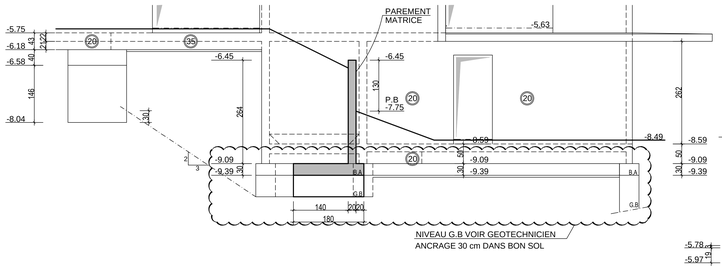

COUPE F
Ech: 1/50

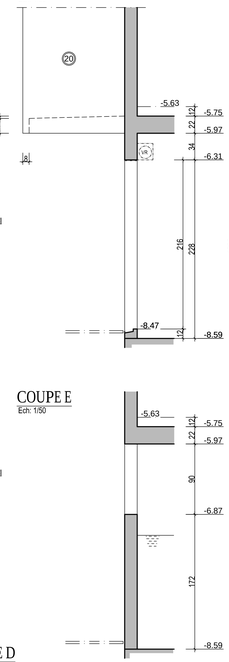


COUPE E
Ech: 1/50

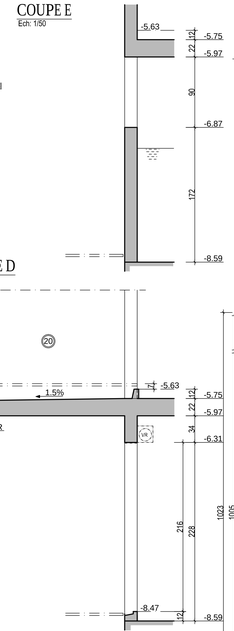


COUPE D
Ech: 1/50


COUPE A
Ech: 1/50

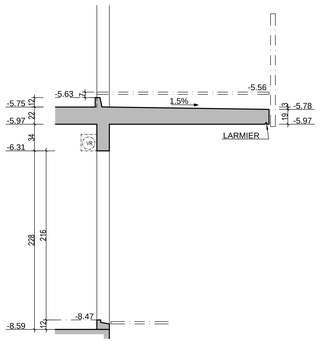

COUPE B
Ech: 1/50

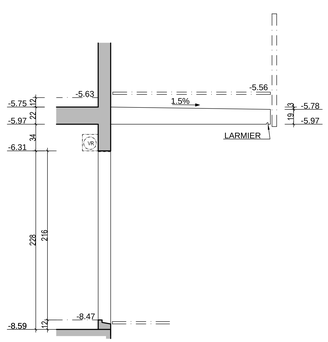


COUPE C
Ech: 1/50

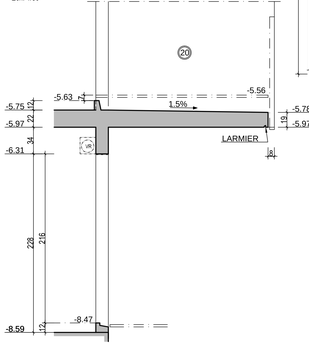

VUE EN PLAN PLANCHER sur -3
Ech: 1/50

DALLES


○	FINI: -5.63=198.82 DALLE BA Epr: 22 cm DESSUS BRUT:-5.75 RESERVE: 12 cm	① FINI: -5.56=198.89 DALLE BA Epr: 22 à 19 cm DESSUS BRUT:-5.75 à -5.78 RESERVE: 19 à 22 cm

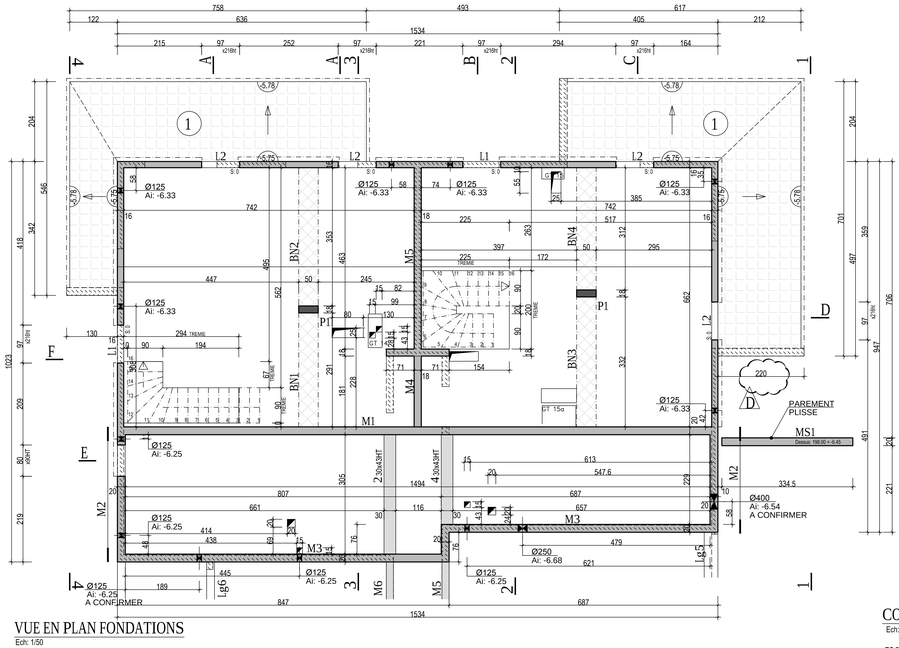

VUE EN PLAN FONDATIONS
Ech: 1/50

DALLES

○	FINI: -8.47=195.98 DALLE BA Epr: 20 cm DESSUS BRUT:-8.59 RESERVE: 12 cm	①	FINI: -8.59=195.86 DALLE BA Epr: 25 cm DESSUS BRUT:-8.59 RESERVE: 0 cm	②	FINI: -5.63=198.82 DALLE BA Epr: 22 cm DESSUS BRUT:-5.75 RESERVE: 12 cm	③	FINI: -5.56=198.89 DALLE BA Epr: 22 cm DESSUS BRUT:-5.75 RESERVE: 19 cm	④	FINI: -8.49=195.96 DALLE BA Epr: 20 à 17 cm DESSUS BRUT:-8.59 à -8.62 RESERVE: 12 à 15 cm

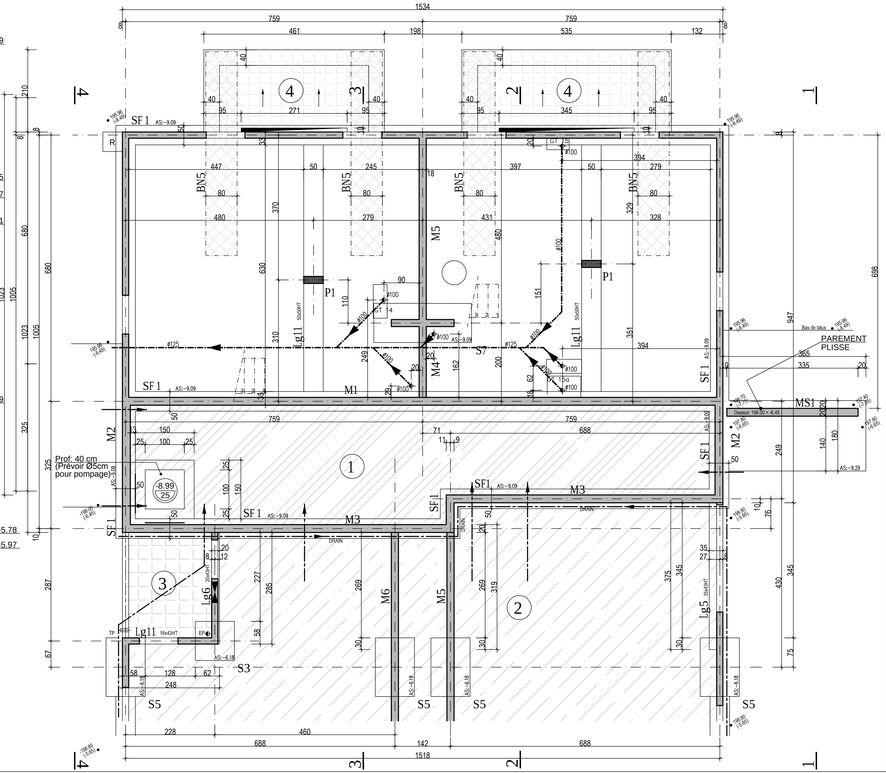

COUPES TYPES SEMELLES ISOLEES
Ech: 1/25

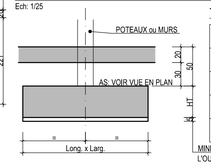


TABLEAU SEMELLES ISOLEES

Repère	Long. x Larg.	HT
S3	100 x 100	40
S5	100 x 150	40
S6	120 x 120	40
S7	100 x 250	40

MINI A ADAPTER A L'OUVERTURE DES FOUILLES

COUPES TYPES SEMELLES FILANTES
Ech: 1/25 Ech: 1/25

INTERIEURES EXTERIEURES

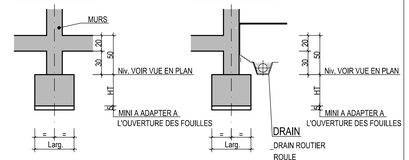


TABLEAU SEMELLES FILANTES

Repère	Larg.	HT
SF 1	50	30

±0.00 = 204.45 = NIVEAU FINI du REZ de CHAUSSEE Bât: C

NOAHO

Chemin de Fontanière - 69350 La Mulatière

Création de logements

Les entreprises réalisant les travaux devront tenir compte des derniers plans architecte lors de la réalisation des travaux.
Les plans du be MATTE ne doivent servir qu'au corps d'état concerné et doivent être des plans d'exécution.

ARCHITECTE(S):	Atelier D'IS	MO DELEGUE:	
BET STRUCTURE:	MATTE SAS	MOE:	PSO Ingénierie
BET FLUIDES:	PRELEM	CSPS:	SUD EST COORDINATION
ECONOMISTE:	EXECO	OPC:	
BUREAU DE CONTROLE:	Bureau VERITAS	ENTREPRISE(S):	Fontanel-pbc

Bât: C Aile EST
FONDATIONS au -3 et Plancher sur -3
Coffrage

EXE
Contrainte de sol: 8 bars ELS
Aciers HA (T) FeE500
Aciers Doux (Ø) FeE 235
Aciers TS FeE 500
Béton fc28 >= 20MPa
Enrobage = 3 cm

INDICE	DATE	MODIFICATIONS
A	27/05/2015	MISE A JOUR FONDATIONS(Suppression semelles isolée)
B	09/06/2015	COMPLETE RESERVATIONS et TERRASSES EXTERIEURES
C	11/06/2015	AJOUTE REGARD.MAJ G.B.Raccourci murs 75 à 71 cm
D	16/06/2015	MODIFIE LARGEUR BALCON SUIVANT D

PLAN N° C01 D
DATE : 12/05/2015

MATTÉ
BUREAU D'ÉTUDES
STRUCTURES ET FLUIDES
119 BOULEVARD STALINGRAD 69100 VILLEURBANNE
Tél. 04 72 44 10 87 Fax 04 72 44 26 99
E-mail : bet@matte.fr

Dessiné par : J.BO
Contrôlé par : P.LIN
Echelle : 1/50°

Affaire N° 13.12.119