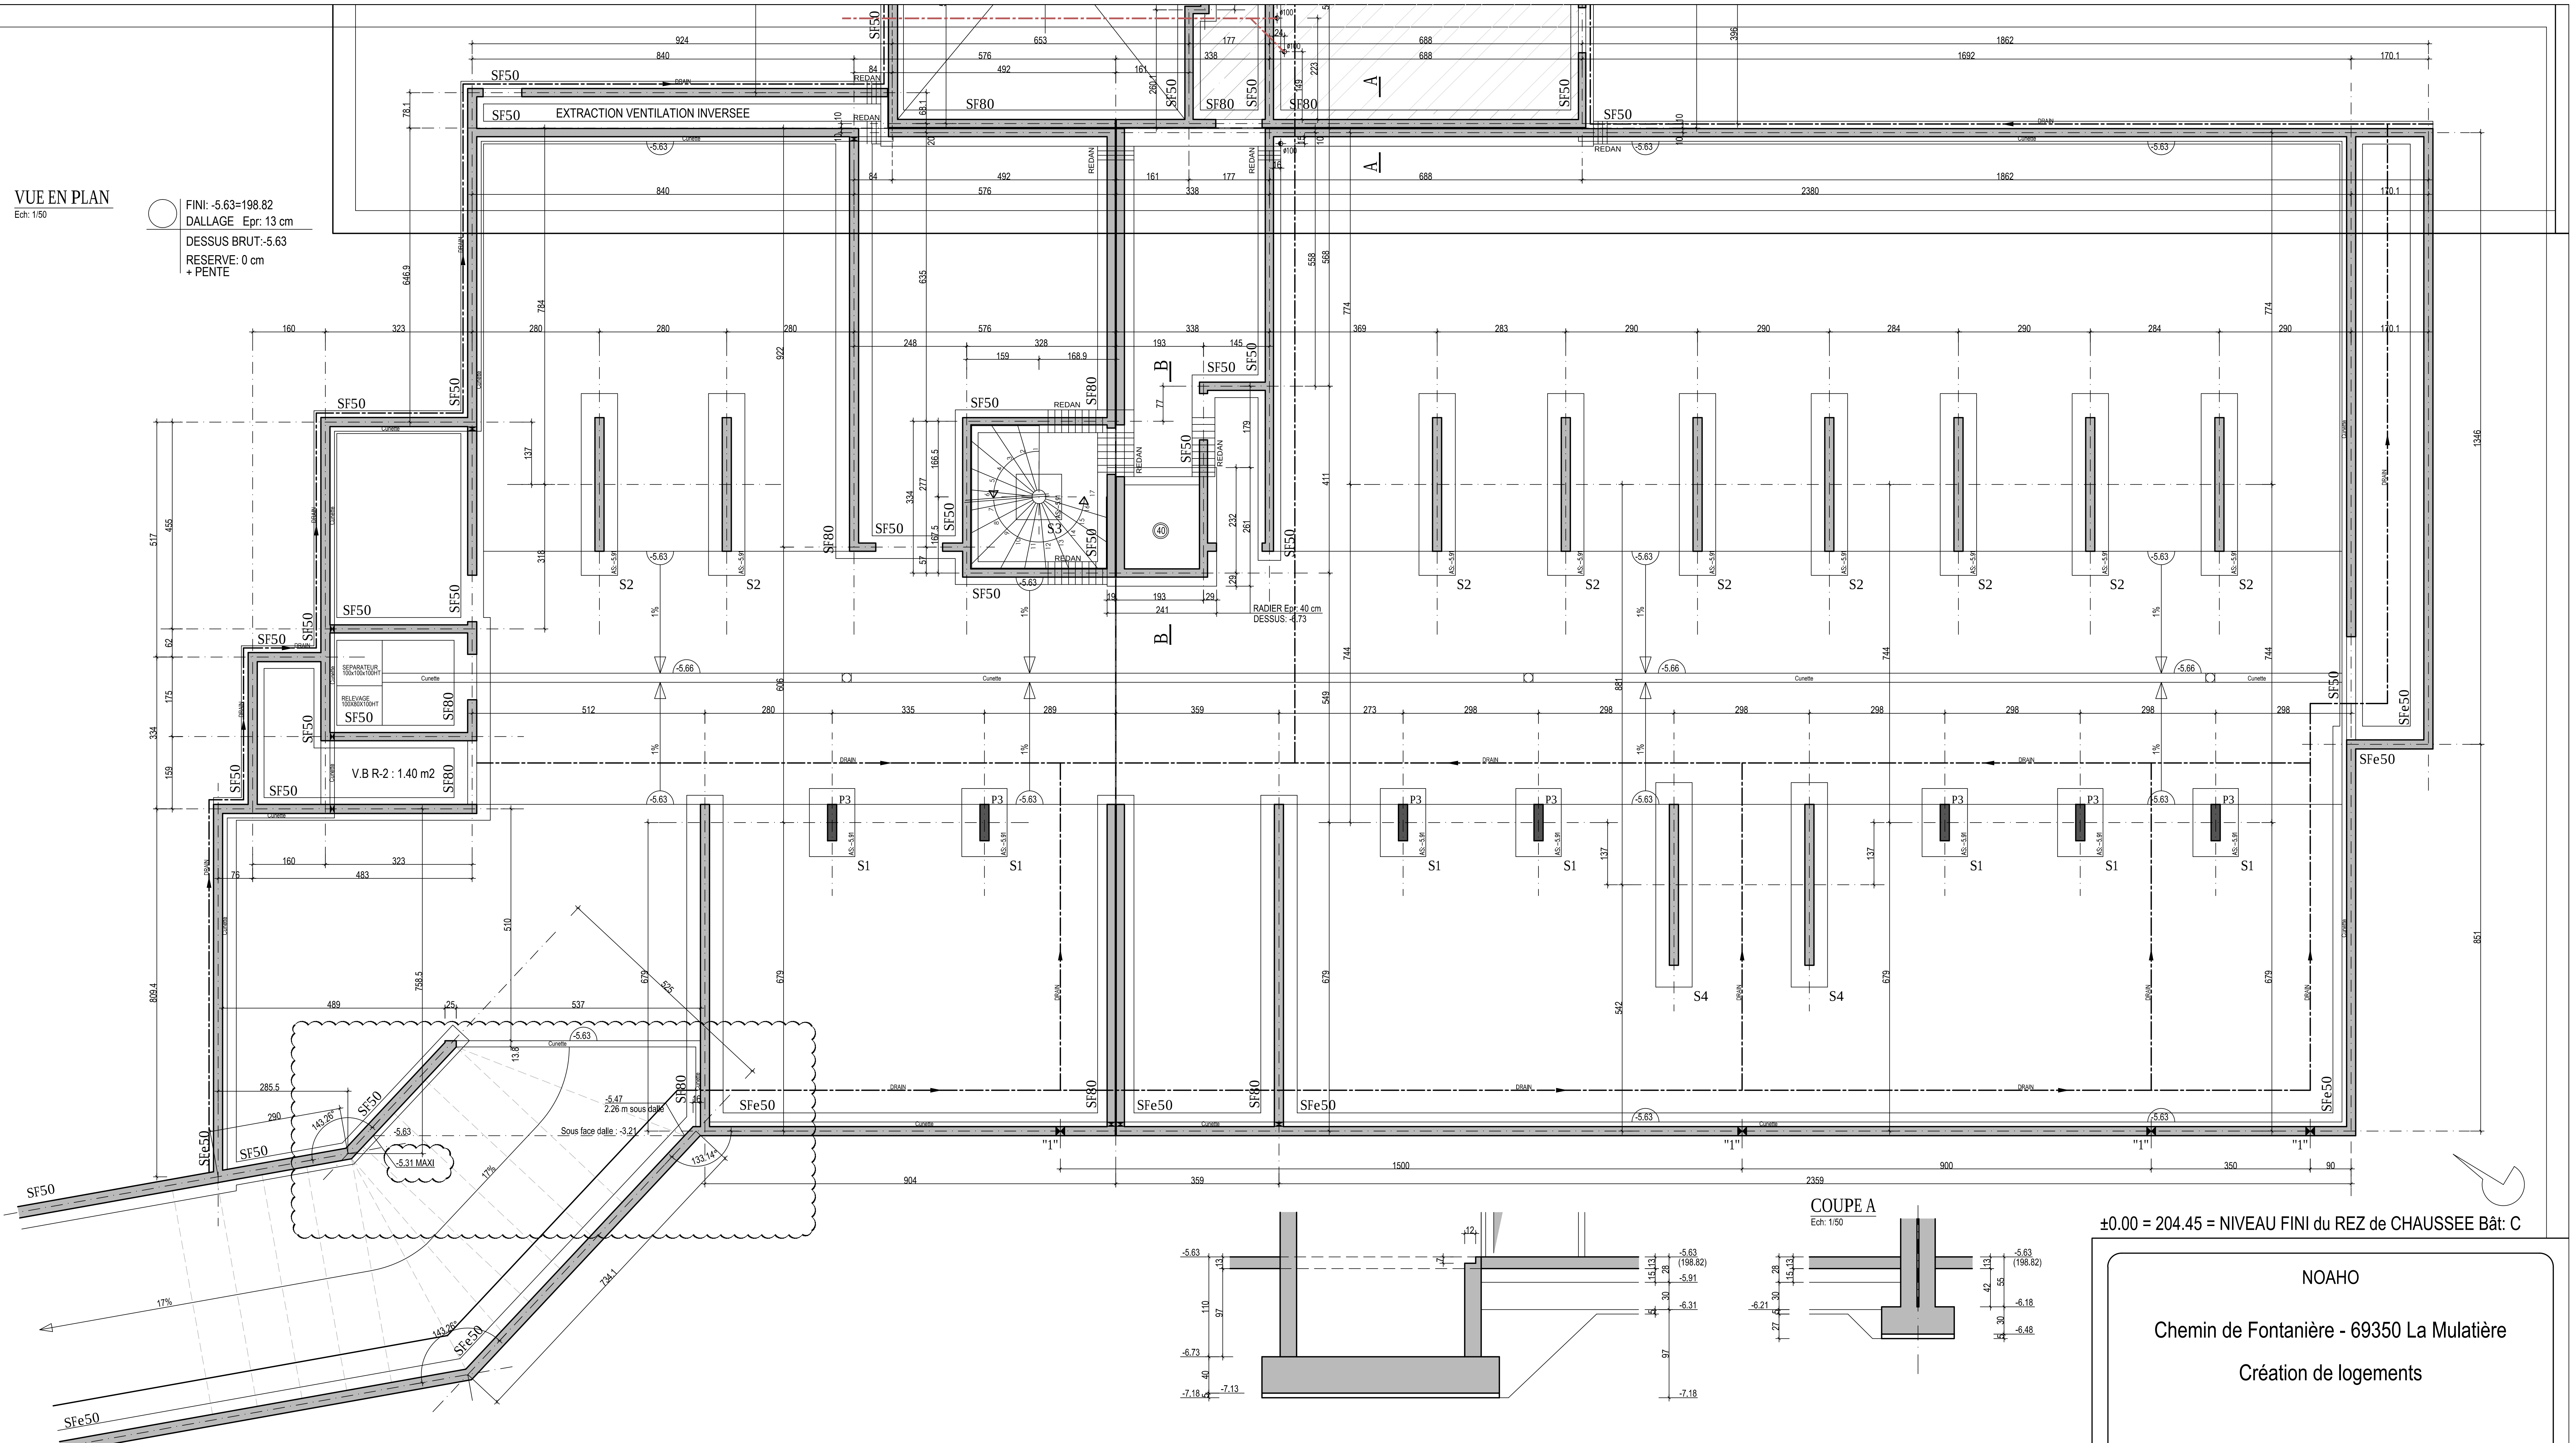

±0.00 = 204.45 = NIVEAU FINI du REZ de CHAUSSEE Bât: C

COUPES TYPES SEMELLES FILANTES

Ech: 1/25

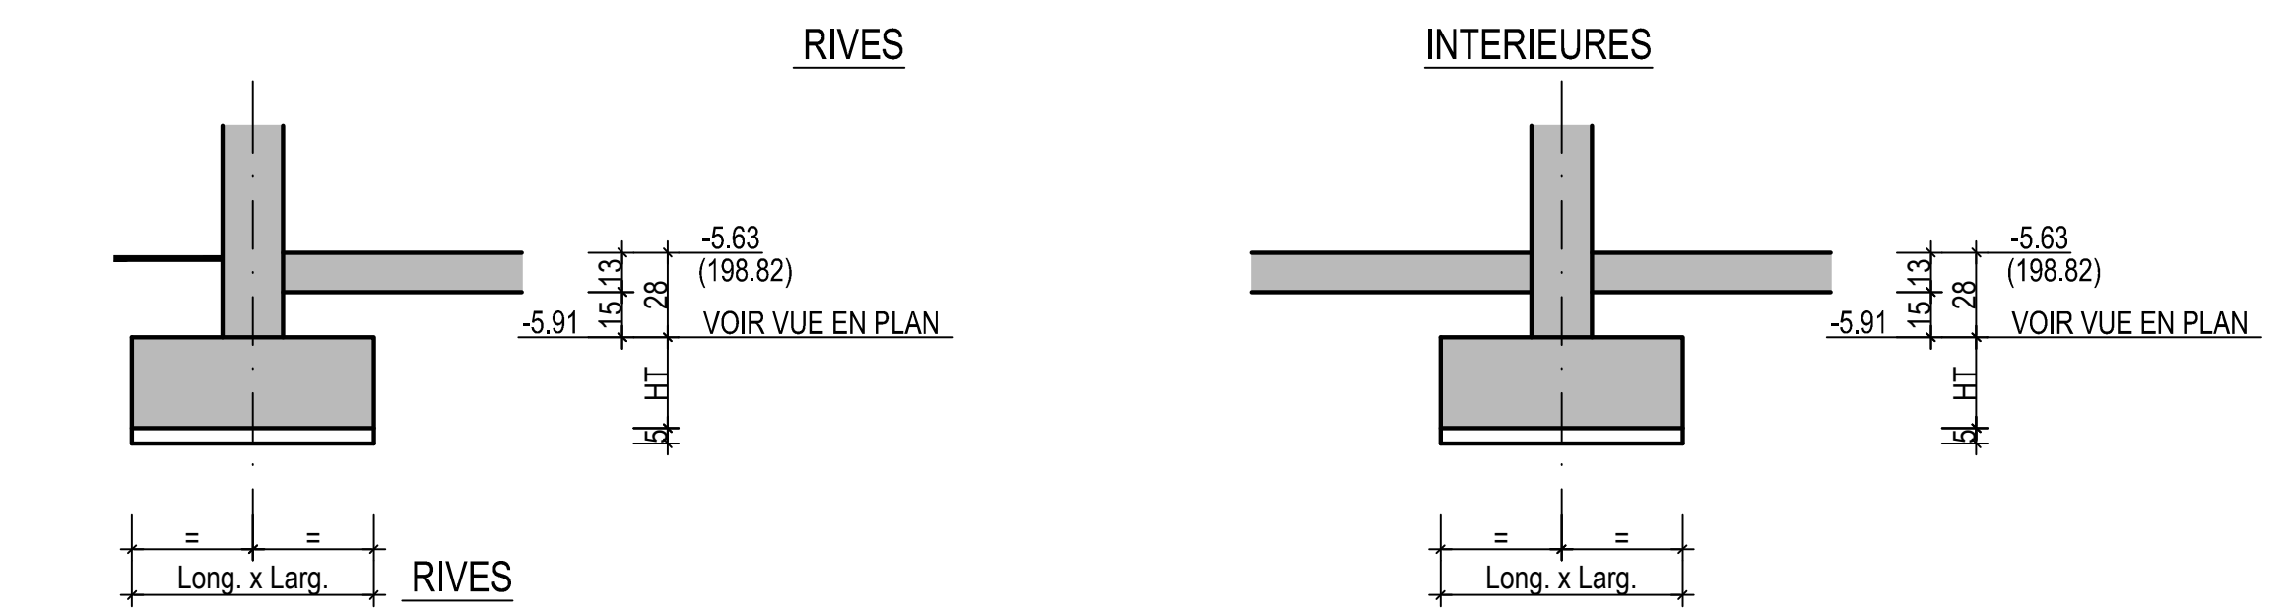

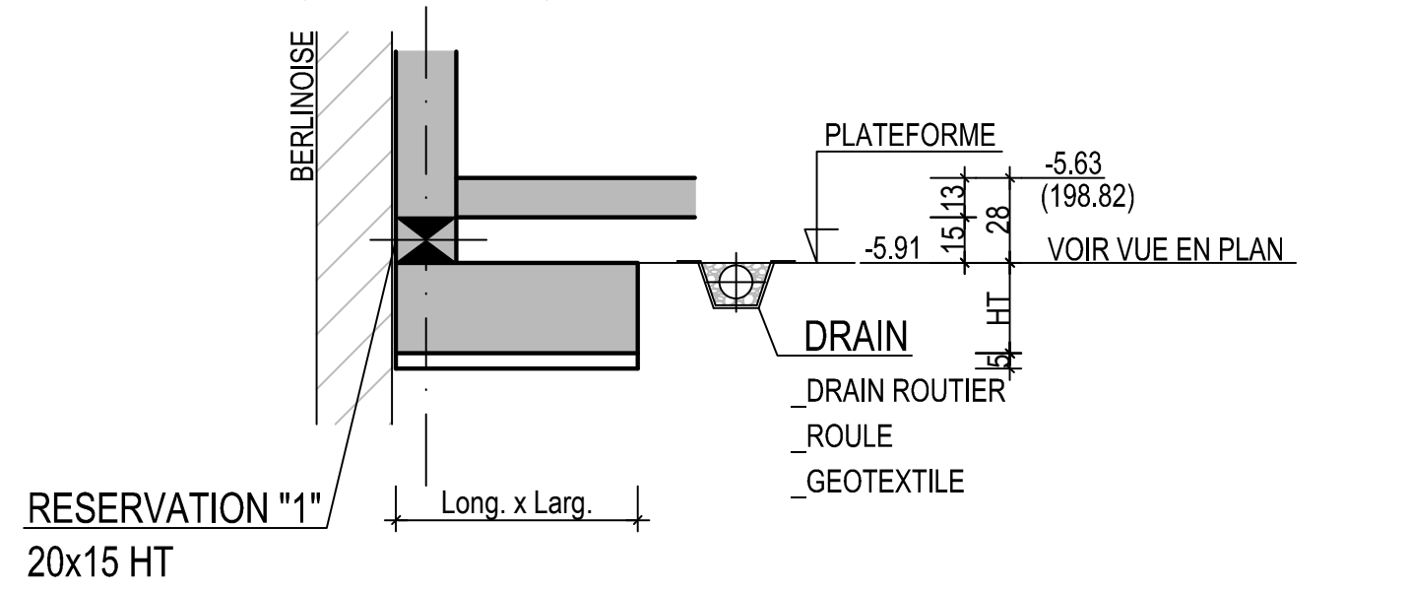

COUPES TYPES SEMELLES ISOLEES

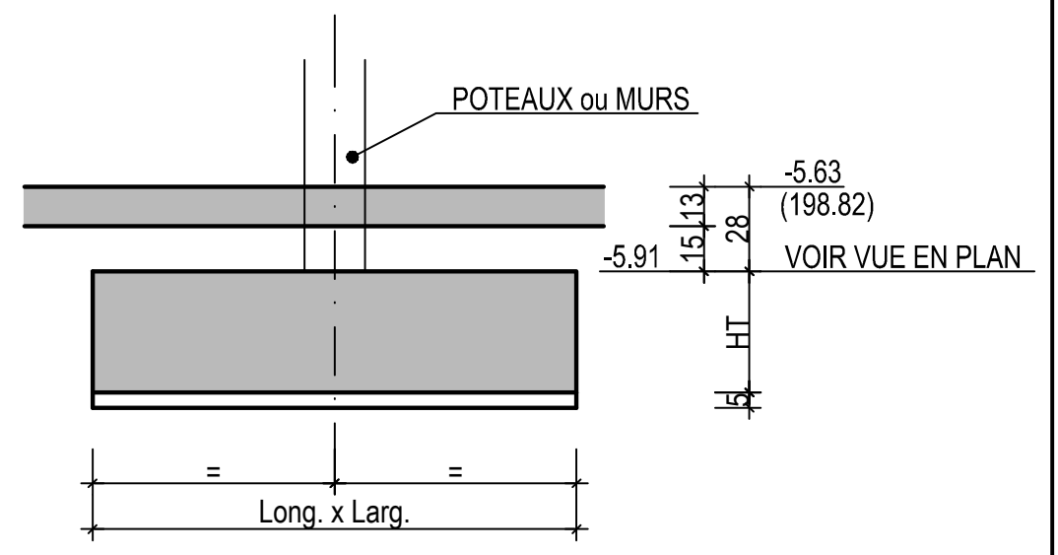

TABLEAU SEMELLES FILANTES

Repère	Larg.	HT
SF 50	50	30
SF 60		
SF 70		
SF 80	80	30

TABLEAU SEMELLES ISOLEES

Repère	Long. x Larg.	HT
S1	100 x 150	40
S2	80 x 400	30
S3	100 x 100	40
S4	80x 450	30
S5	100 x 150	40

NOAHO

Chemin de Fontanière - 69350 La Mulatière

Création de logements

Les entreprises réalisant les travaux devront tenir compte des derniers plans architecte lors de la réalisation des travaux
Les plans du be MATTE ne doivent servir qu'au corps d'état concerné et doivent être des plans d'exécution.

ARCHITECTE(S): Atelier D'IS
BET STRUCTURE: MATTE SAS
BET FLUIDES: PRELEM
ECONOMISTE: EXECO
BUREAU DE CONTROLE: Bureau VERITAS
MO DELEGUE:
MOE: PSO Ingéniérie
CSPS: SUD EST COORDINATION
OPC:
ENTREPRISE(S): Fontanel-pbc

Bât: C Aile OUEST
FONDATIONS au -2
Coffrage

EXE

Contrainte de sol: 8 bars ELS

Aciers HA (T) FeE500
Aciers Doux (Ø) FeE 235
Aciers TS FeE 500
Béton fc28 >= 25MPa
Enrobage = 3 cm

INDICE	DATE	MODIFICATIONS
A	18/05/2015	COMPLETE

PLAN N°
C04 A
DATE : 12/05/2015

MATTÉ
BUREAU D'ÉTUDES
STRUCTURES ET FLUIDES
119 BOULEVARD STALINGRAD 69100 VILLEURBANNE
Tél. 04 72 44 02 87 Fax 04 72 44 26 59
E-mail : bet@matte.fr

Dessiné par : J.BO
Contrôlé par : P.LIN
Echelle : 1/50°

Affaire N°
13.12.119