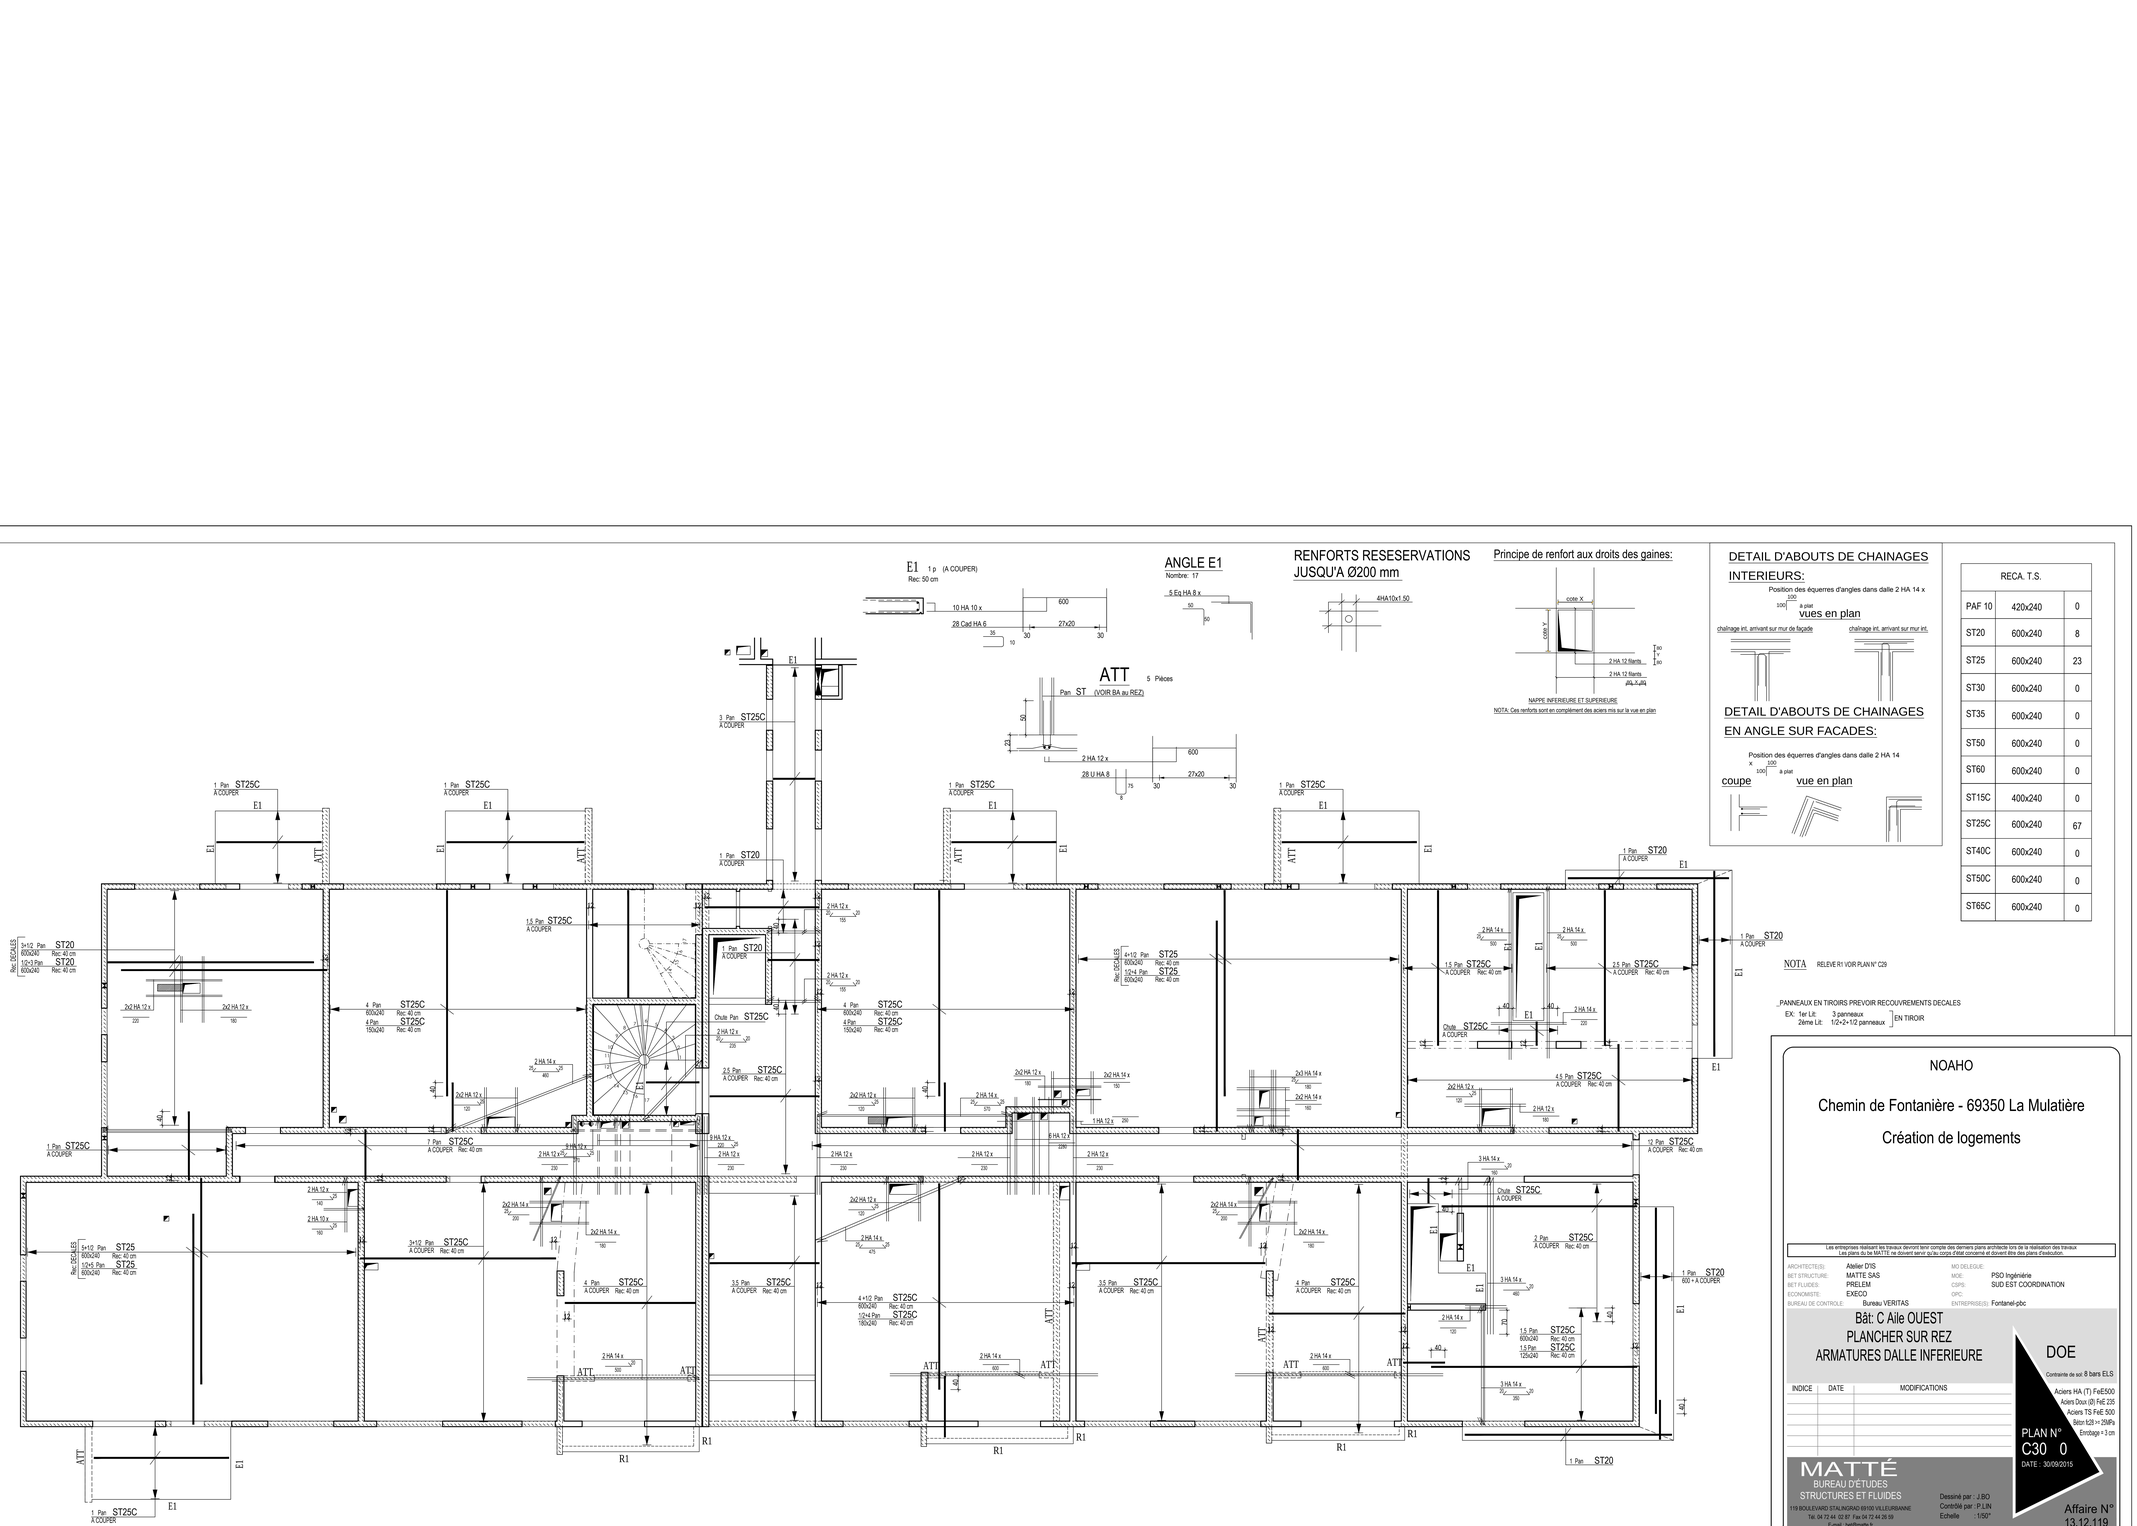


RECA. T.S.		
PAF 10	420x240	0
ST20	600x240	8
ST25	600x240	23
ST30	600x240	0
ST35	600x240	0
ST50	600x240	0
ST60	600x240	0
ST15C	400x240	0
ST25C	600x240	67
ST40C	600x240	0
ST50C	600x240	0
ST65C	600x240	0

NOAHO

Chemin de Fontanière - 69350 La Mulatière

Création de logements

Les entreprises réalisant les travaux devront tenir compte des derniers plans architecte lors de la réalisation des travaux
Les plans du be MATTE ne doivent servir qu'au corps d'état concerné et doivent être des plans d'exécution.

ARCHITECTE(S):	Atelier D'IS	MO DELEGUE:	
BET STRUCTURE:	MATTE SAS	MOE:	PSO Ingénierie
BET FLUIDES:	PRELEM	CSPS:	SUD EST COORDINATION
ECONOMISTE:	EXECO	OPC:	
BUREAU DE CONTROLE:	Bureau VERITAS	ENTREPRISE(S):	Fontanel-pbc

Bât: C Aile OUEST
PLANCHER SUR REZ
ARMATURES DALLE INFERIEURE

DOE

Contrainte de sol: 8 bars ELS

Aciers HA (T) FeE500
Aciers Doux (Ø) FeE 235
Aciers TS FeE 500
Béton fc28 >= 25MPa
Enrobage = 3 cm

INDICE	DATE	MODIFICATIONS

PLAN N° C30 0
DATE : 30/09/2015

MATTÉ
BUREAU D'ETUDES
STRUCTURES ET FLUIDES
119 BOULEVARD STALINGRAD 69100 VILLEURBANNE
Tel. 04 72 44 02 87 Fax 04 72 44 26 09
E-mail : bet@matte.fr

Dessiné par : J.BO
Contrôlé par : P.LIN
Echelle : 1/50°

Affaire N° 13.12.119