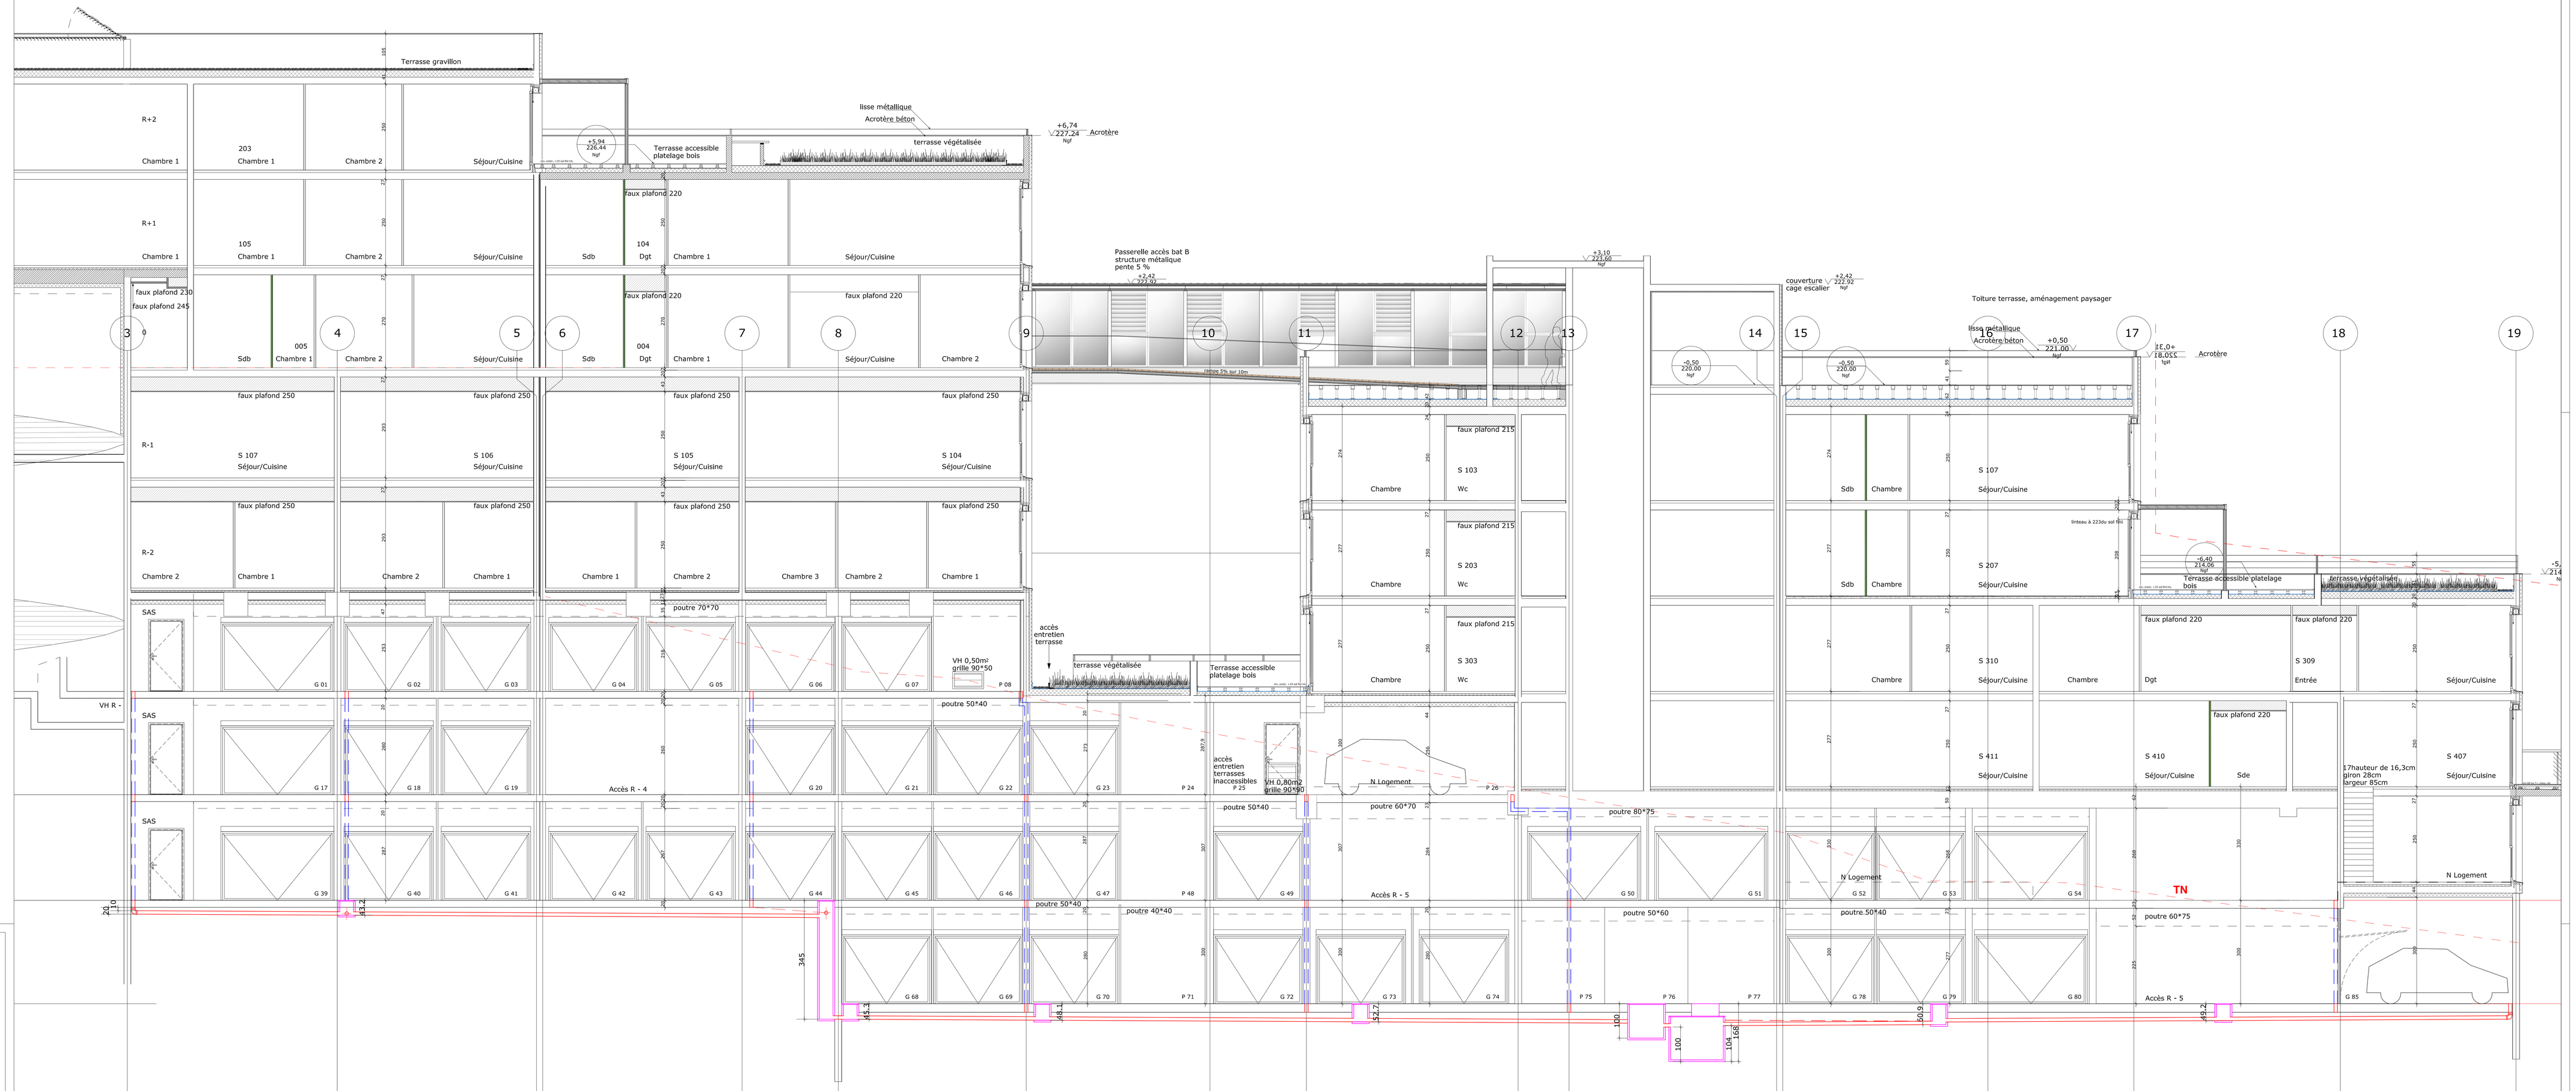


LE 180°

Construction de 106 logements

255, Chemin de Fontanières
69350 LA MULATIERE

MAITRE D'OUVRAGE	SCI NOAHO Résidence	23, Avenue de Pourpoint 69667 CALUIRE ET CUIRE
ARCHITECTE	Atelier de la Passerelle	30, Rue Sergent Blandan 69001 LYON
MAITRE D'OEUVRE	PSO Ingénierie	BP 21 07340 SERRIERES
SPS	SUD et COORDINATION	17, Chemin Louis Chirpaz 69130 ECULLY

PLAN DU RESEAU SOUS DALLAGE COUPE

IND	DATE	REMARQUES	REDI/VERIF
0	14/09/2015	PREMIERE DIFFUSION	FL/SP

FONTANEL
La qualité se construit

Parc d'Activité Le Chuel
Route de CHASSELAY
69650 QUINCIEUX

Tél. : 04.72.26.39.70
Fax. : 04.78.91.18.93
Site Internet : www.fontanel-sa.fr

ECHELLE : 1/200	FORMAT : A1/ISO	DATE : 14/09/2015						
LOT	EMETTEUR	PHASE	TYPE DOC	ZONE	NIVEAU			NUMERO / INDICE
GO	FON	EXE	RSD	TZ	TN			03.010 0