

Création de logements La Mulatière

Chemin de Fontanière - 69350 La Mulatière
Affaire n° 280

Maître d'ouvrage

NOAHO
23 Avenue de Proumeyrol
69300 Caluire-et-Cuire
Tél : 04.78.39.20.52 Fax : 04.78.39.33.91


Architecte

Atelier d'YS
51, rue Dufour 69004 LYON
Tél : 04.78.39.20.52 Fax : 04.78.39.33.91
Mail : atelierdys@atelierdys.com

PAYSAGISTE / BET VRD SYMBIOSE	Adresse : 440 rue Berthollet - 69000 LYON Tél : 04.78.39.20.52 Fax : 04.78.39.33.91 Mail : symbiose@sybio.com
BET ECONOMIE EXCO	Adresse : 259 rue Crémieux - LYON Tél : 04.78.37.55.04 Fax : 04.78.37.19.18 Mail : economie@exco.com
BET FLUIDES PRELEM	Adresse : 110 boulevard du Rhône - 69001 LYON Tél : 04.78.59.91.77 Fax : 04.78.59.91.01 Mail : prelem@prelem.com
BET STRUCTURE MATTE	Adresse : 119 boulevard du Rhône - 69001 LYON Tél : 04.78.59.91.77 Fax : 04.78.59.91.01 Mail : matte@matte.com
BUREAU DE CONTROLE VERITAS	Adresse : 16 chemin du Jolim EP 26 - 69571 DARDILLY Tél : 04.72.29.70.70 Fax : 04.78.35.53.10 Mail : bureau@veritas.com

PLANS - COUPES - FAÇADES - PROJET BÂTIMENT C

Phase : MARCHÉ
Bâtiment : C
Niveau : NIVEAU -1_Aile Ouest
Coupes - Façades :
Plan n° : 04
Indice : A
Date : AVRIL 2015
Échelle : 1/50

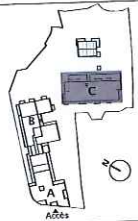


ISOOTHERM

$R = 2,90$ épaisseur $U3$ mm

A.3

A.3

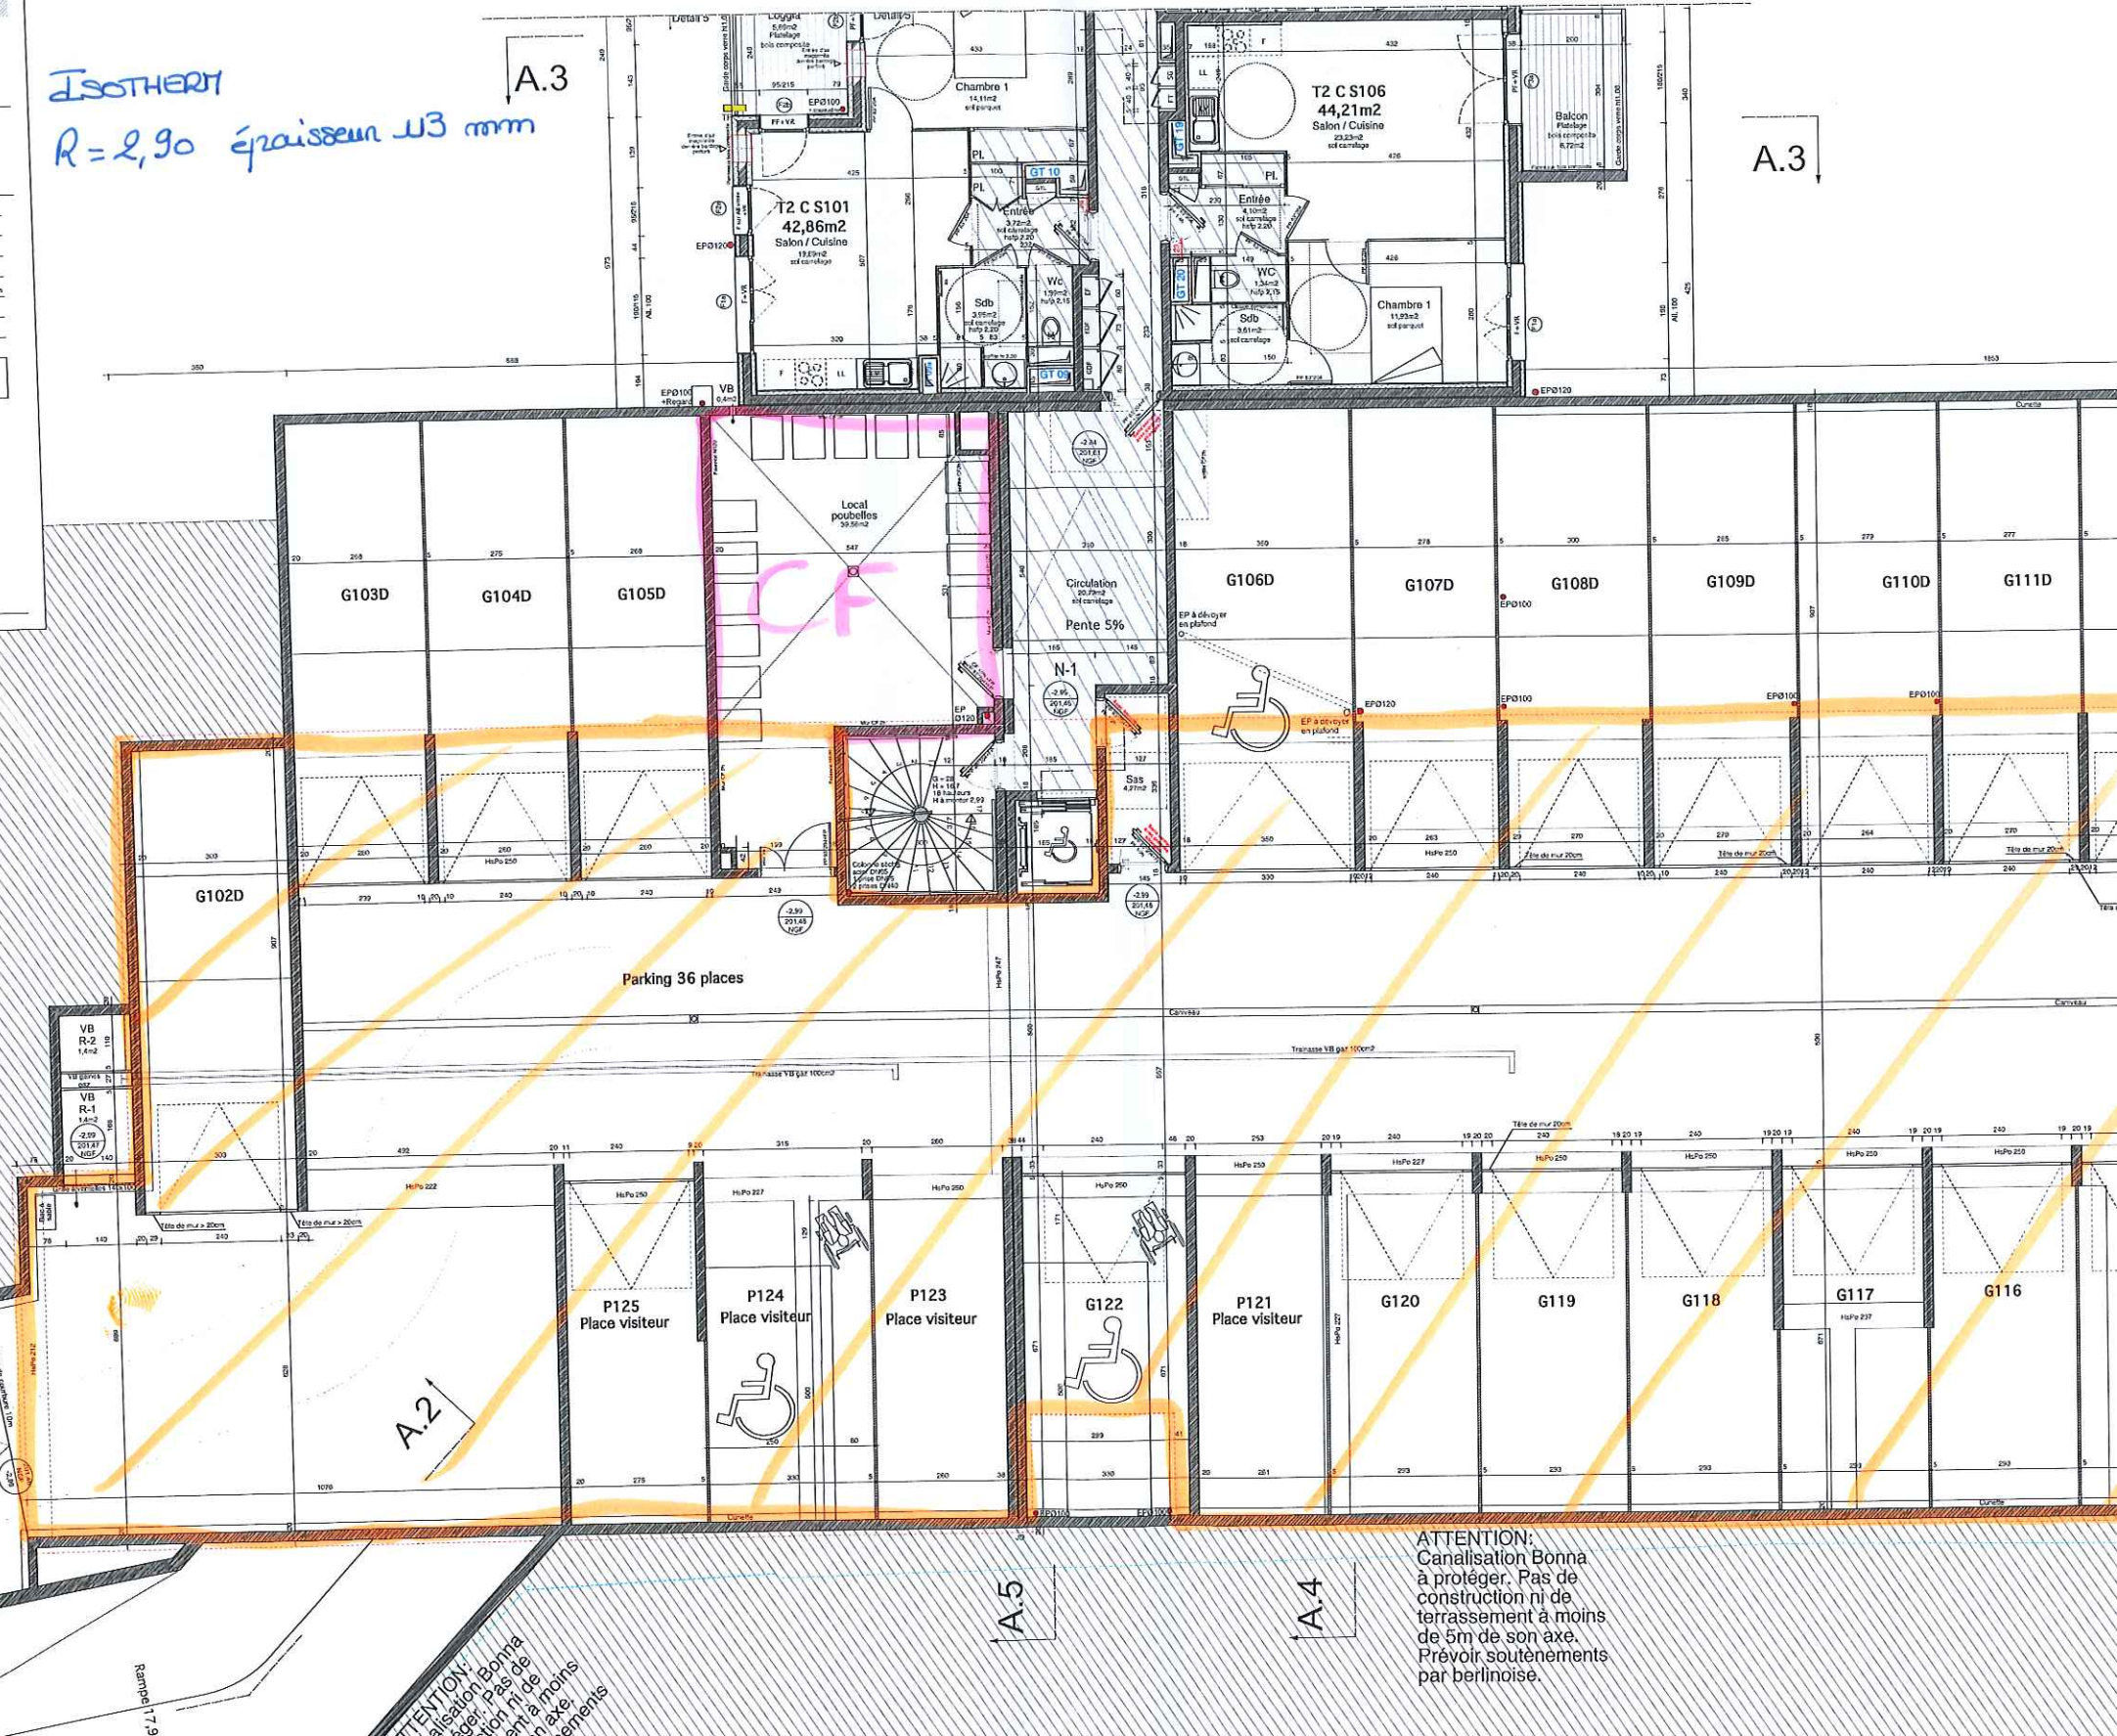

ATTENTION:
Canalisation Bonna
à protéger. Pas de
construction ni de
terrassament à moins
de 5m de son axe.
Prévoir soutènements
par berlinoise.