

Création de logements
La Mulatière
 Chemin de Fontanière - 69350 La Mulatière
 Affaire n° 280

Maître d'ouvrage

NOAHO
 23 Avenue de Pommeyrol
 69300 Caluire-et-Cuire
 Tél : 04 78 30 33 99 Fax : 04 78 30 33 91

Architecte

Atelier d'IS
 51, rue Delavre 69004 LYON
 Tél : 04 78 29 26 52 Fax : 09 78 04 38 67
 Mail : atelierd@atelierd.com

PAYSAGISTE / BET VRD SYMBOSE

BET ECONOMIE EXECO

BET FLUIDES PRELEM

BET STRUCTURE MATTE

BUREAU DE CONTROLE VERITAS

PLANS - COUPES - FAÇADES - PROJET
BÂTIMENT C

Phase : MARCHÉ

Bâtiment : C

Niveau : NIVEAU 0_ Aile Ouest



Coups - Façades :

Plan n° : 06

Indice : A

Date : AVRIL 2015

Échelle : 1/50

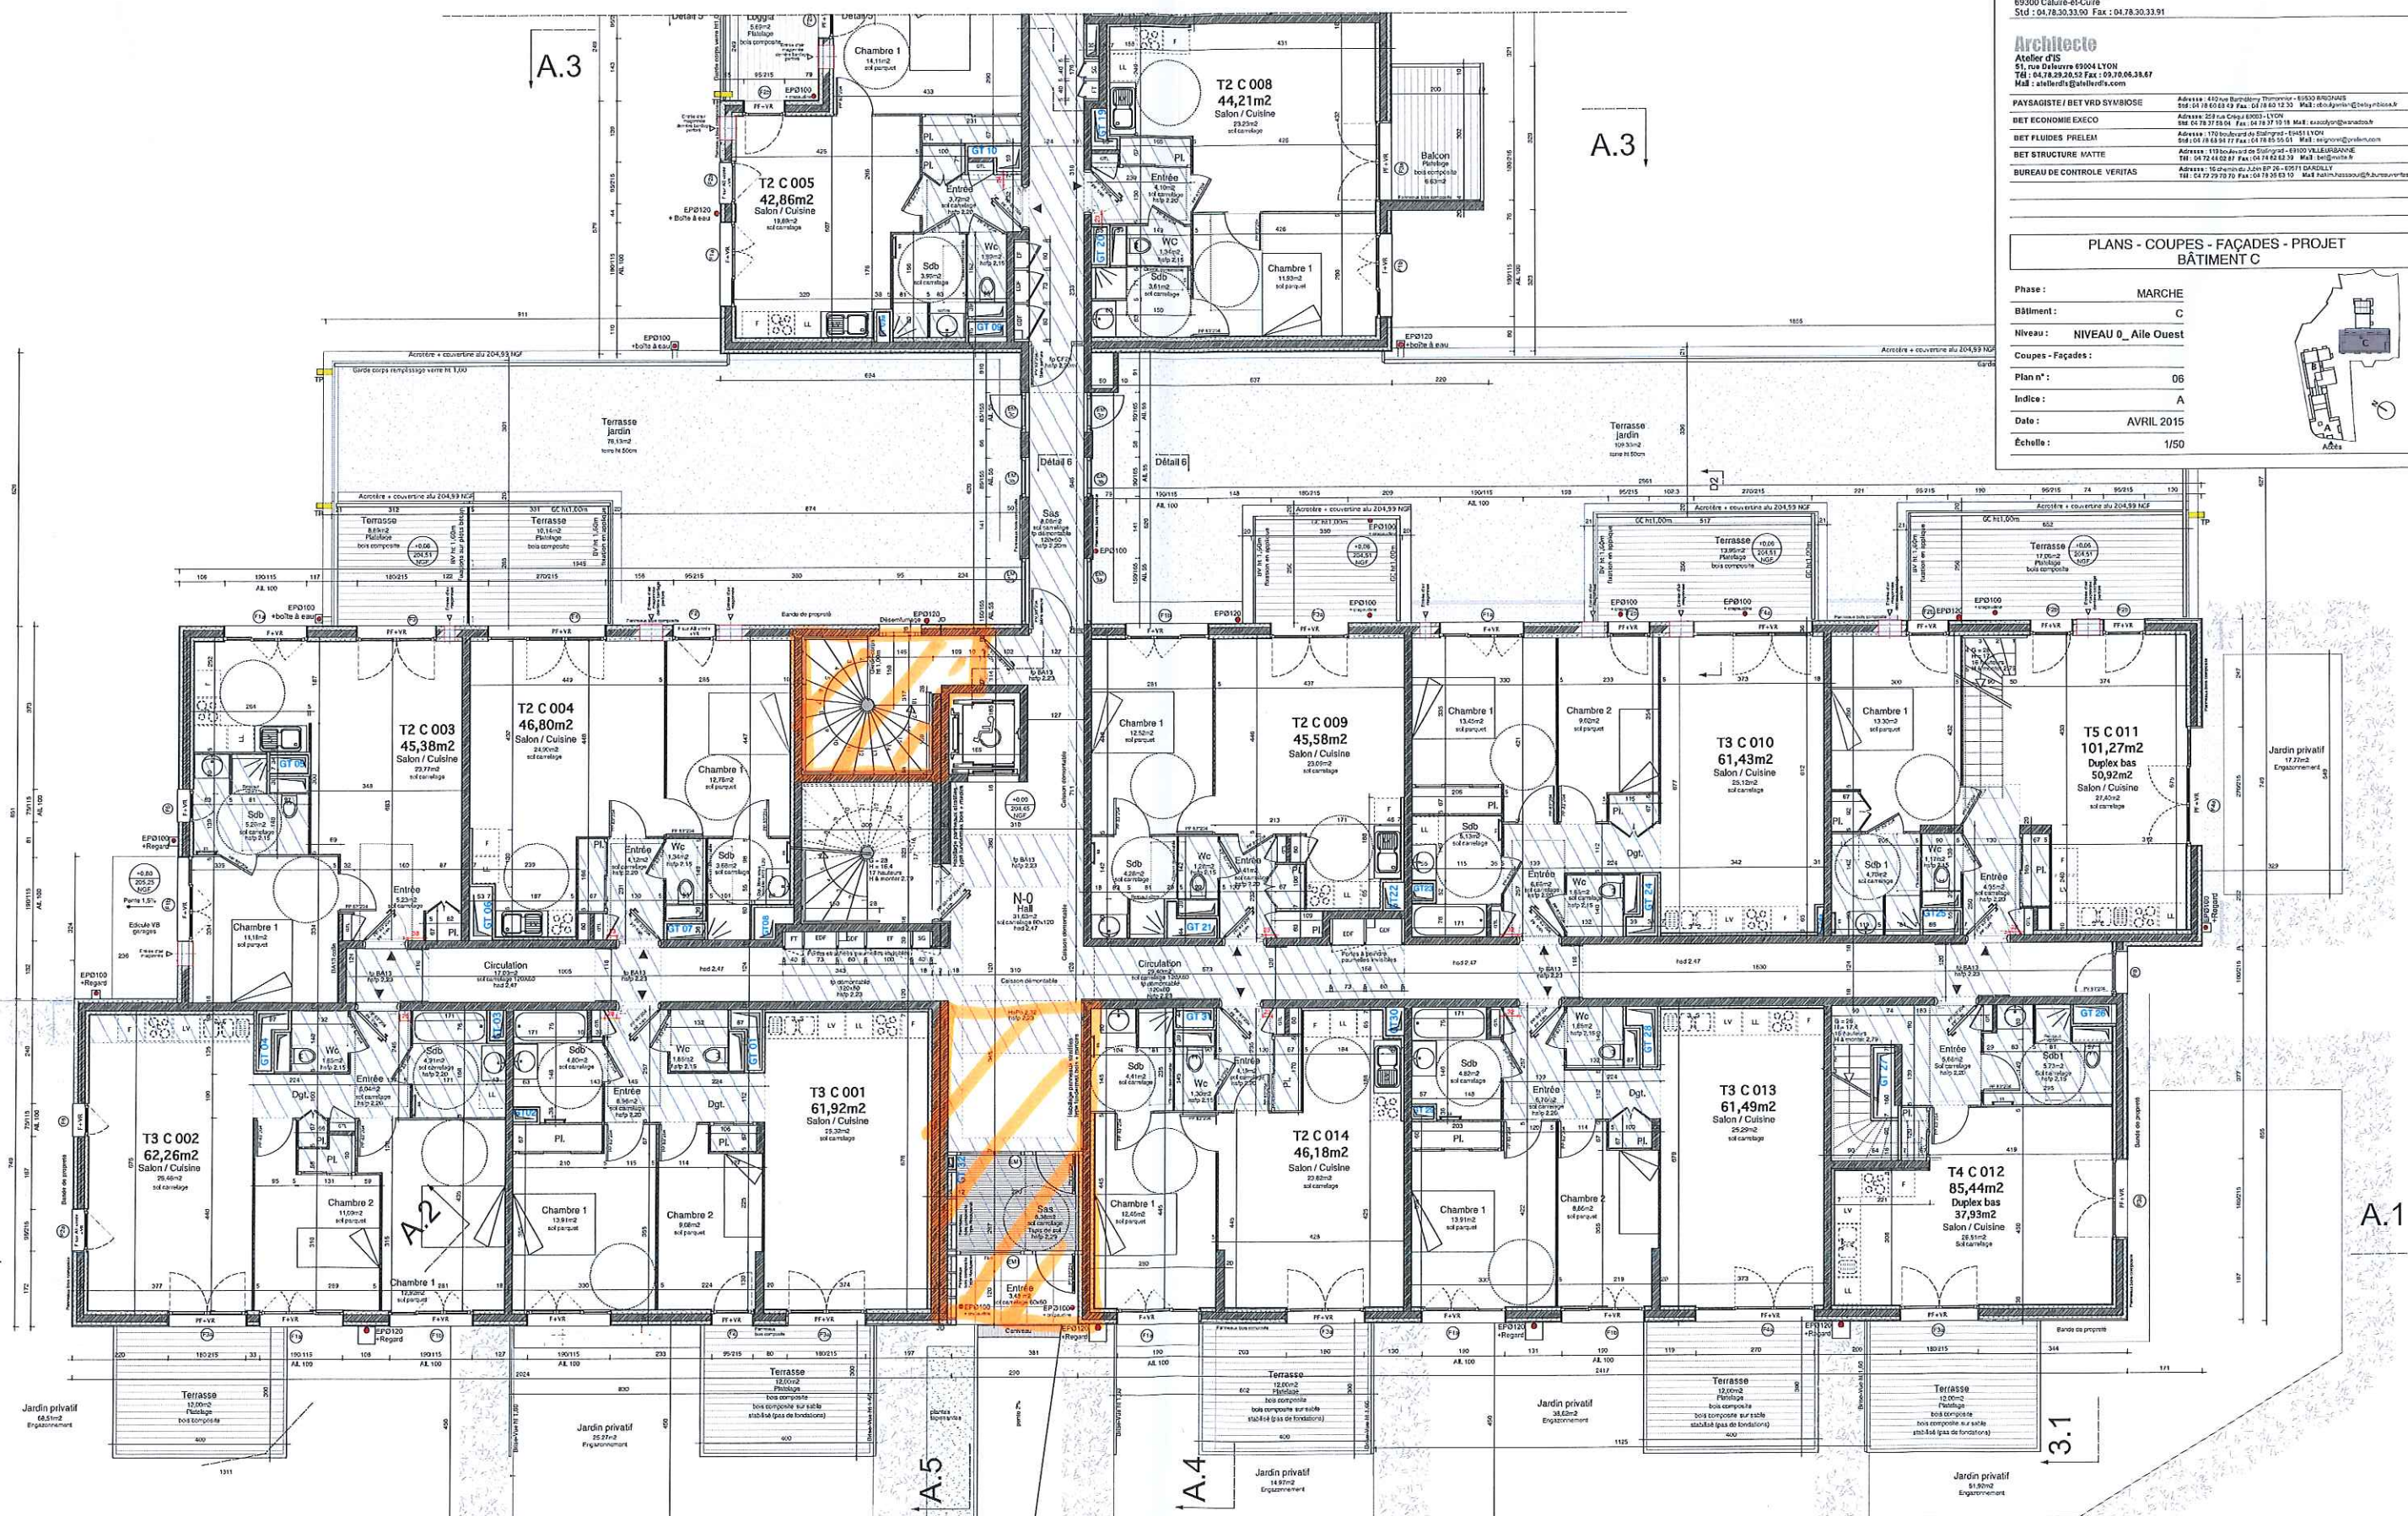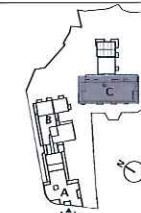

2.30THER7

R = 2,9 épaisseur : 113 mm