
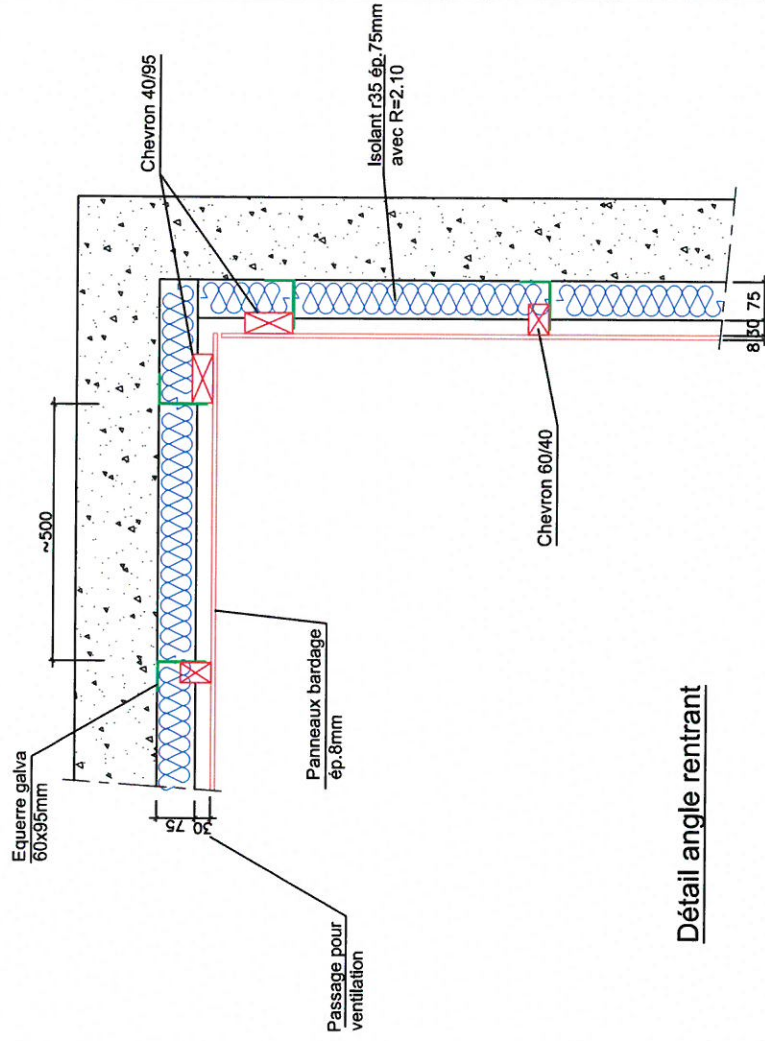


[illegible]

Pied de bardage RDC

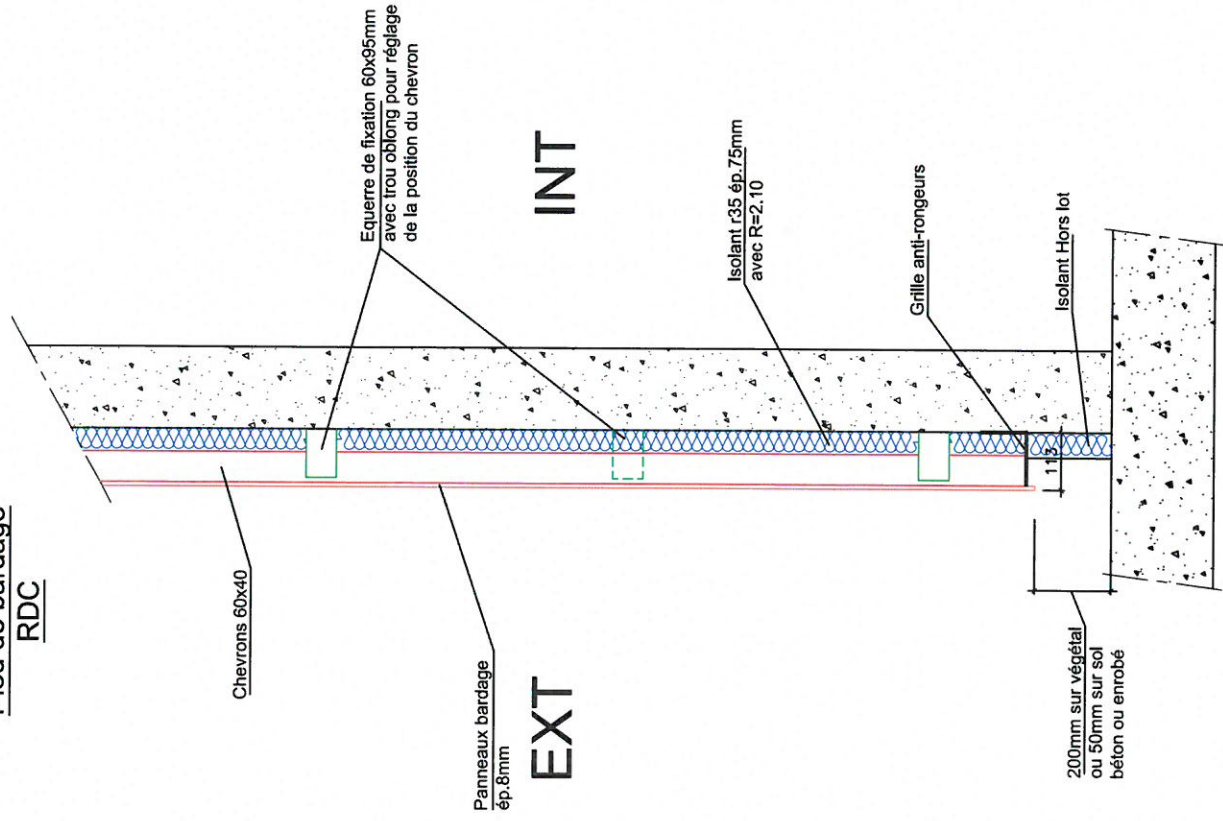

Détail angle rentrant

Création de logements La Mulaière



Chemin de Fontanière
69350 LA MULATIERE

Plan de principe
Bardage Bat. C


Vêtur&Co

2 Imp de l'Echangeur
39300 BOURGOIN-JALLIEU
Tél : 04 74 93 93 08
Fax : 04 74 93 05 71

Vue de dessus

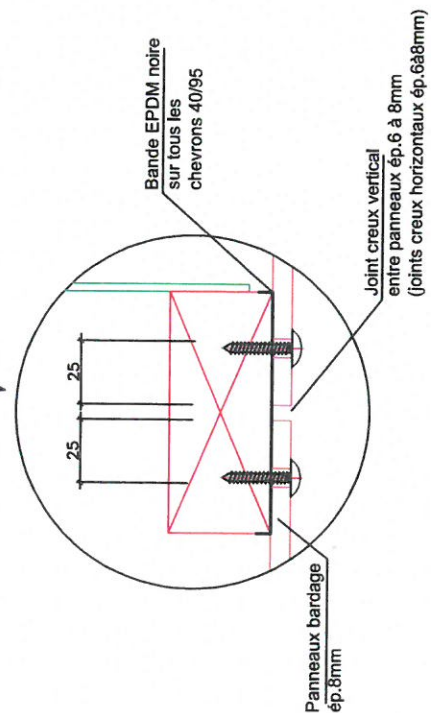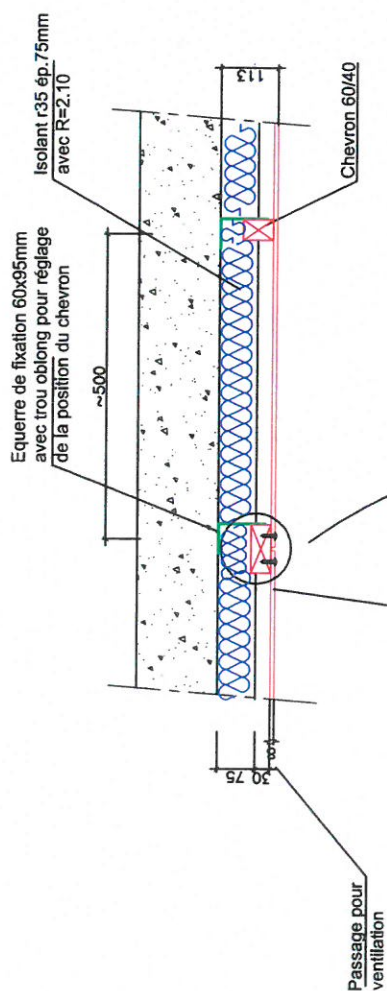

Détail angle sortant

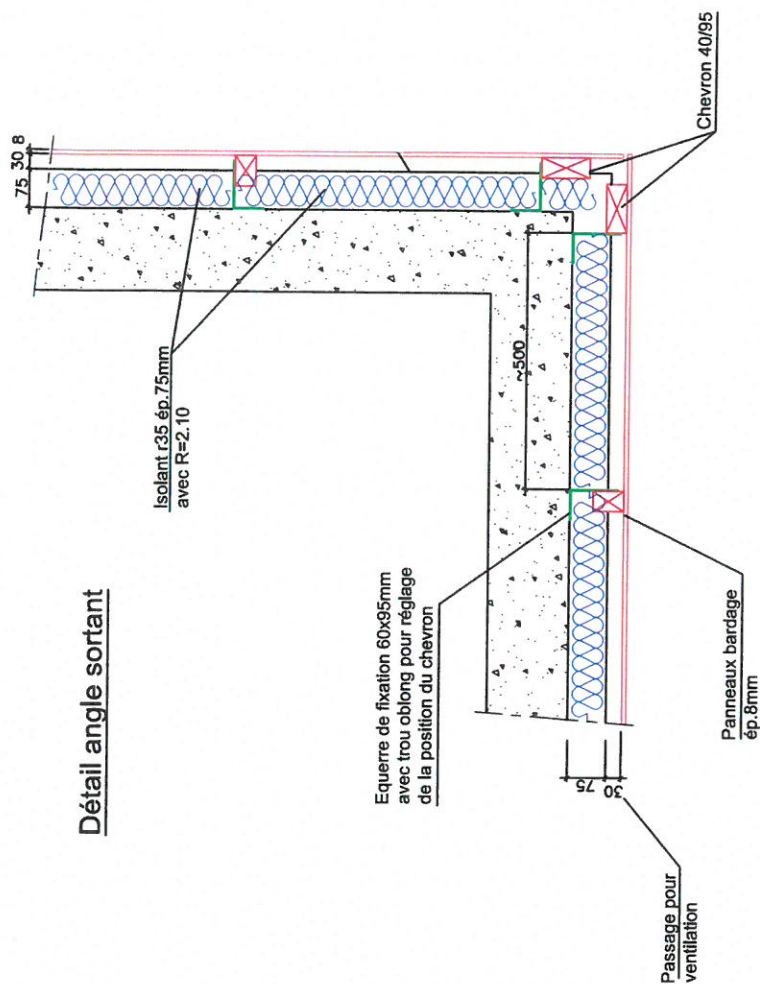

Création de logements La Mulatière





Chemin de Fontanière
69350 LA MULATIERE

Plan de principe
Bardage Bat. C

Vêtur&Co

2 Imp de l'Echangeur
38300 BOURGOIN-JALLIEU
Tel : 04.74.93.93.06
Fax : 04.74.93.05.71

Détail de principe des embrasures

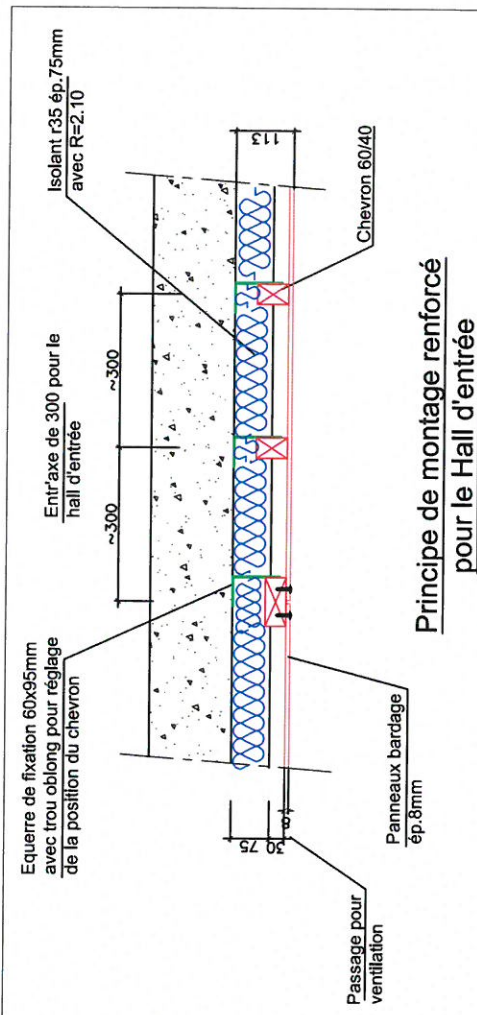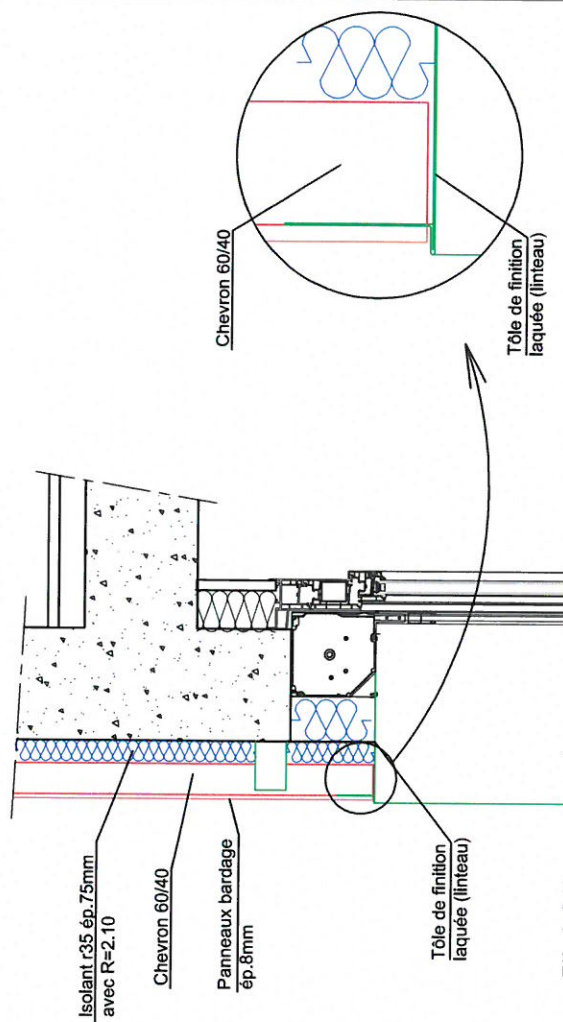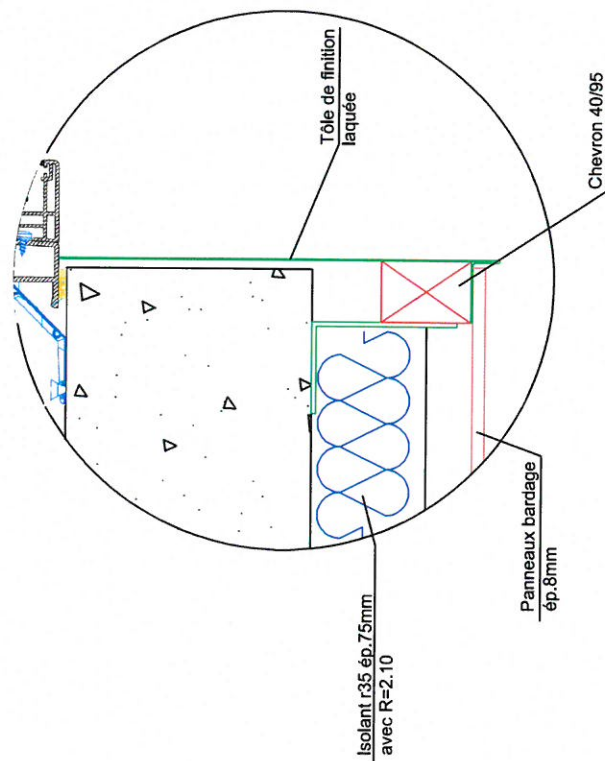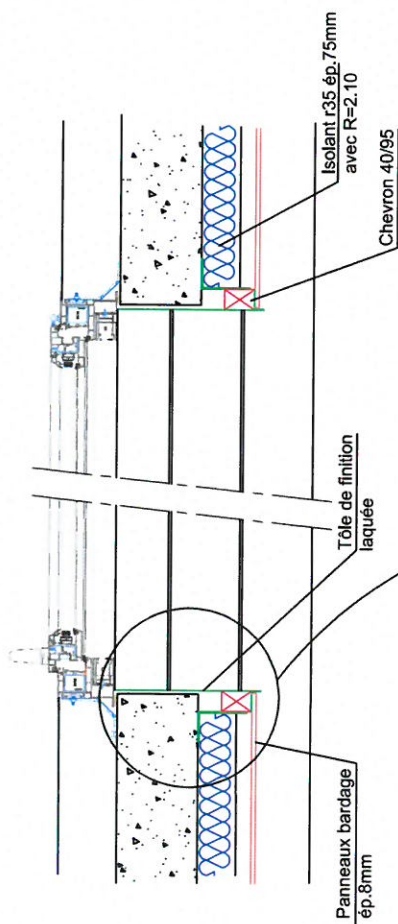

Principe de montage renforcé pour le Hall d'entrée


Création de logements La MulaTière

Chemin de Fontanière
69350 LA MULATIERE

Plan de principe
Bardage Bat. C

Vétur&Co
2 Imp de l'Echangeur
38300 BOURGOIN-JAILLIEU
Tel : 04 74 93 93 08
Fax : 04 74 93 05 71

Coupe sur balcons

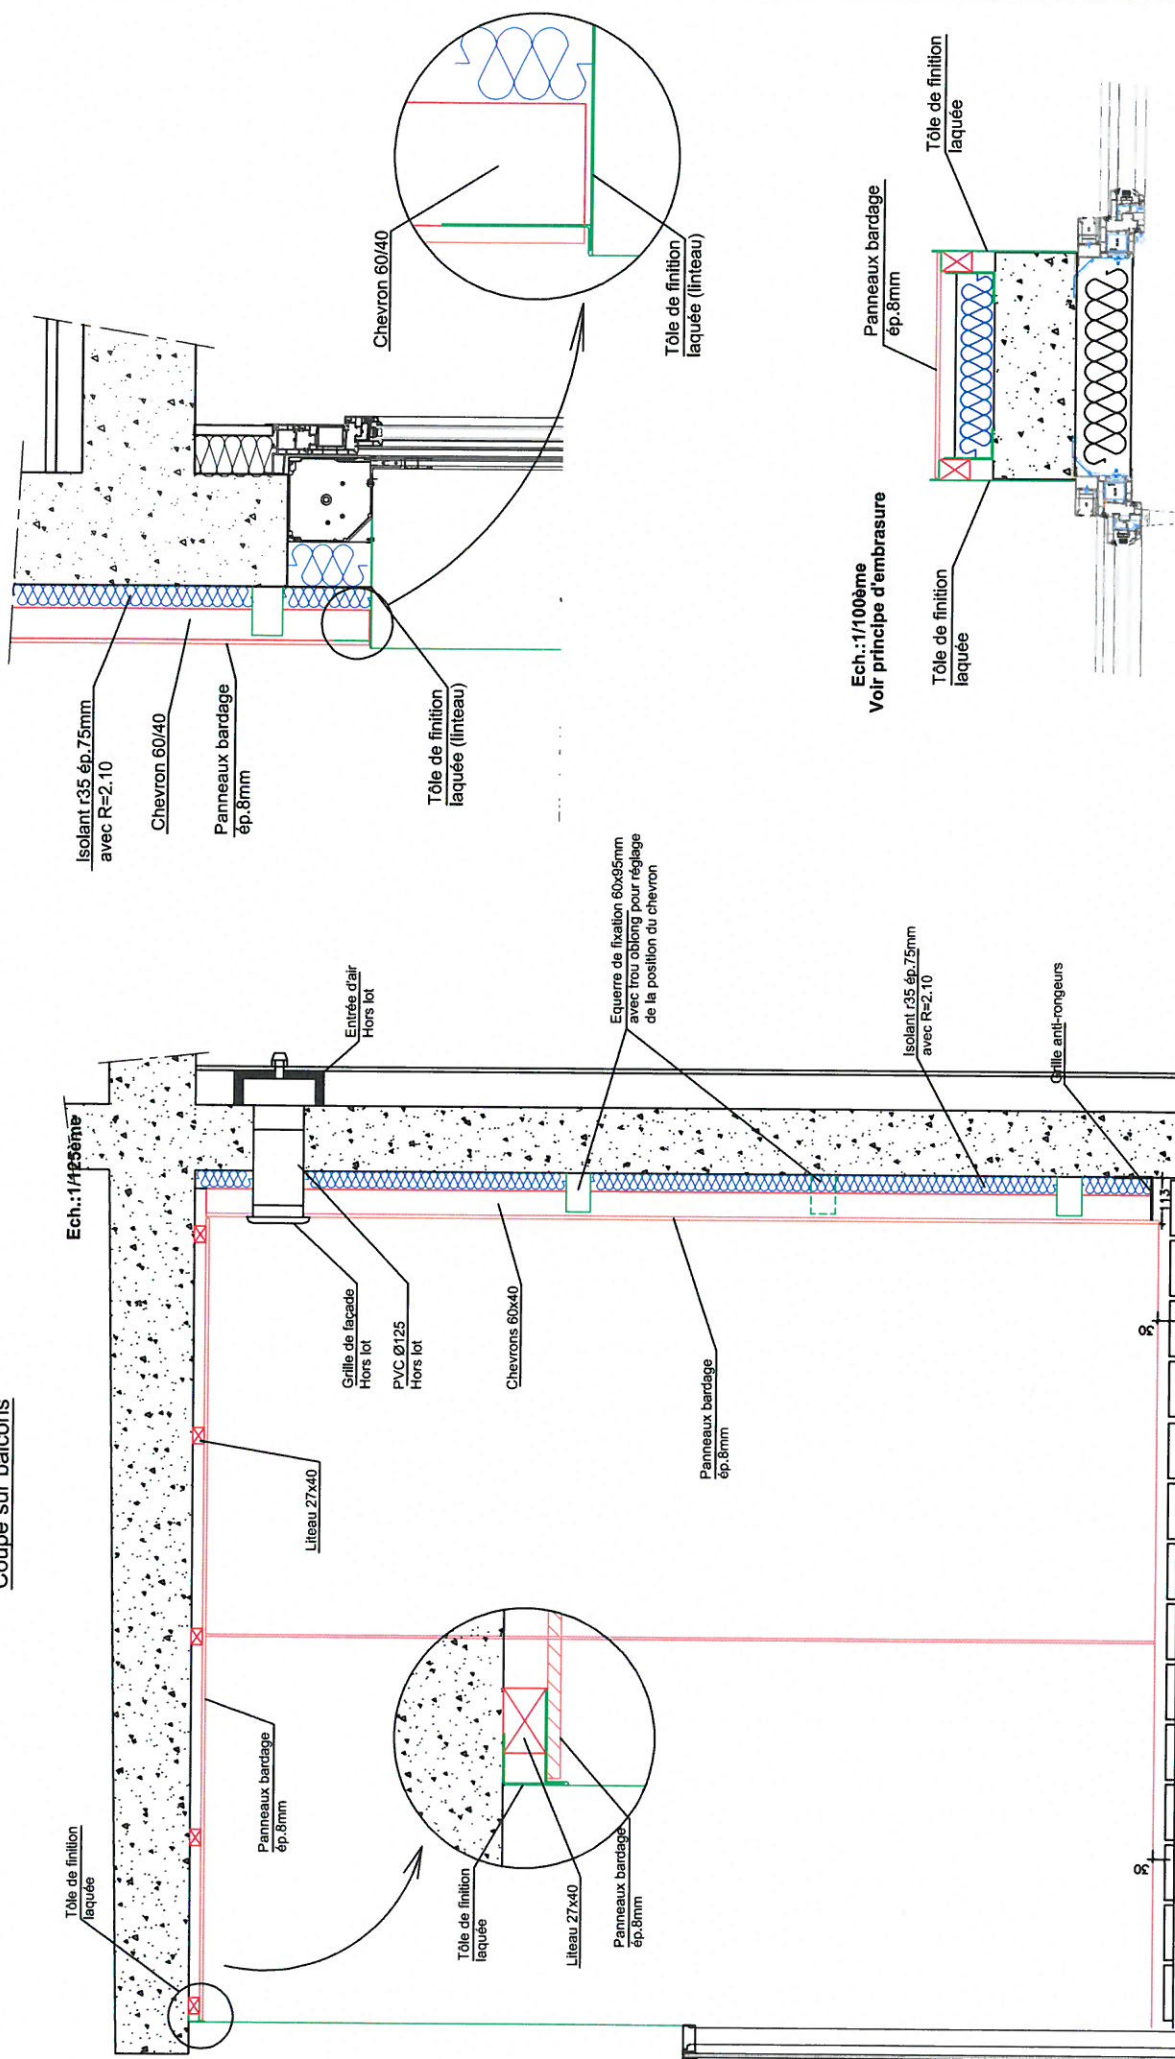

Ech.: 1/100ème
Voir principe d'embrasure

Création de logements La Mulâtère


**Chemin de Fontanière
69350 LA MULATIERE**

Plan de principe Bardage Bat. C

Vétur&Co
2 Imp de l'Echangeur
38300 BOURGOIN-JALLIEU
Tel : 04.74.93.93.08
Fax : 04.74.93.05.71

Coupe sur Loggia

Ech.: 1/125ème

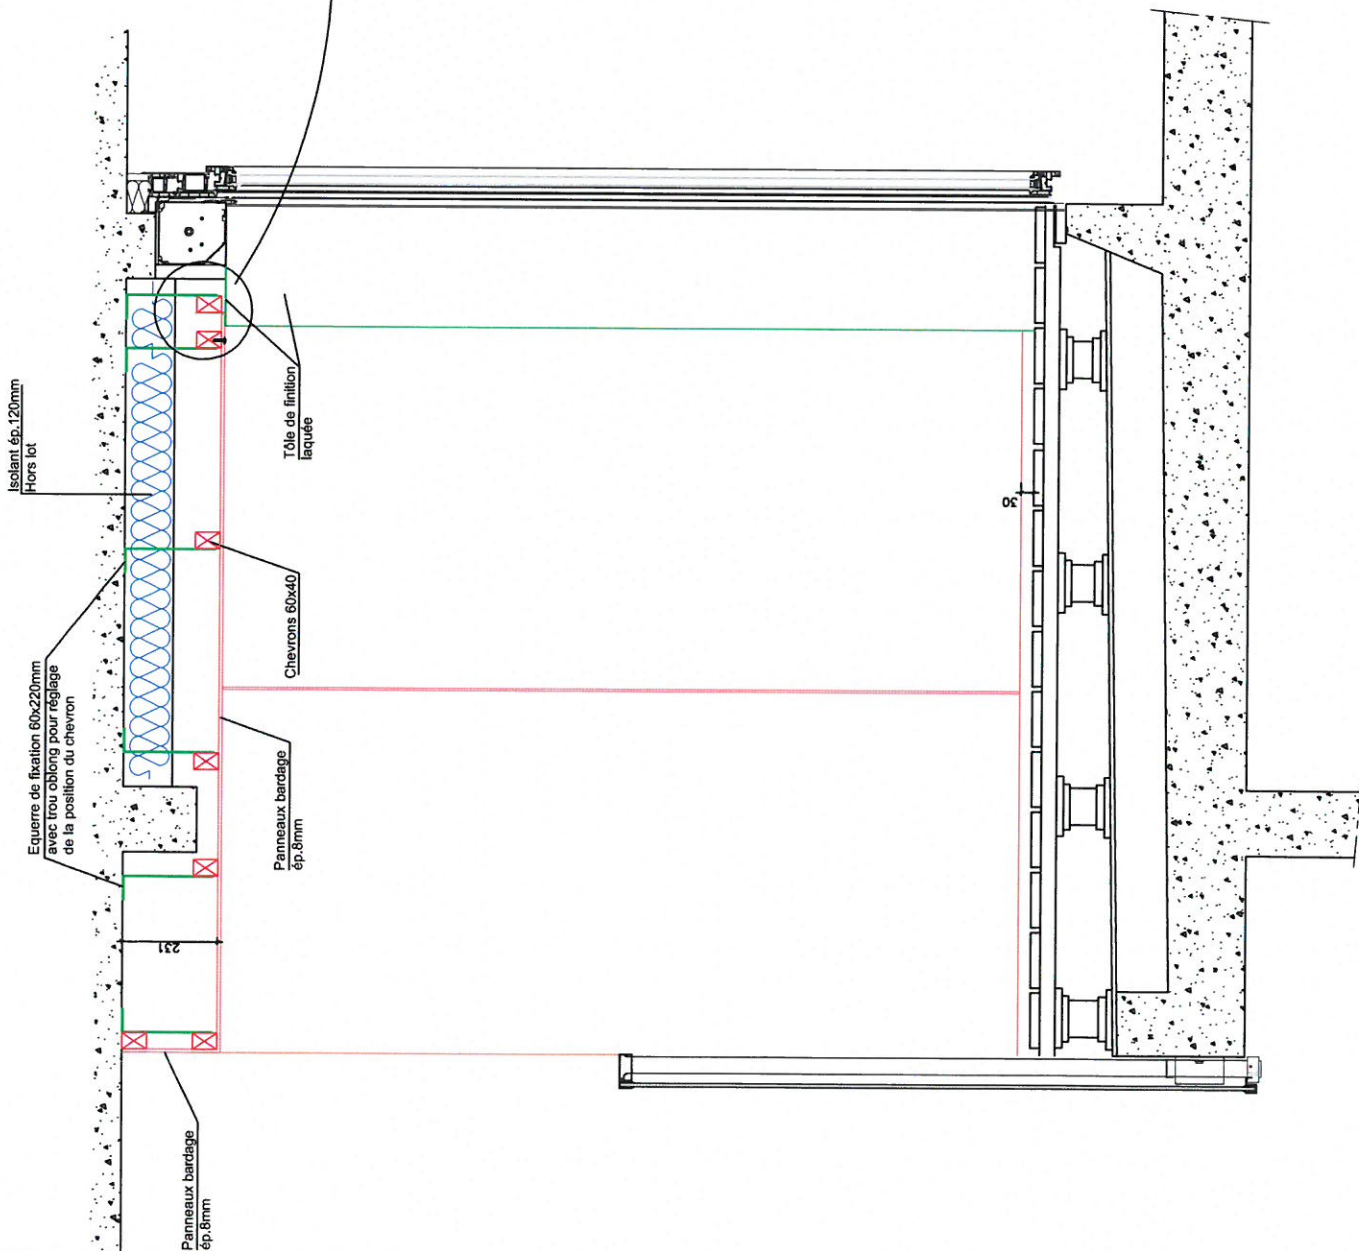


Création de logements La Mulatière

Chemin de Fontanière
69350 LA MULATIERE

Plan de principe
Bardage Bat. C

Vêtur&Co
2 Imp de l'Echangeur
38300 BOURGOIN-JALLIEU
Tél : 04 74 93 93 08
Fax : 04 74 93 05 71

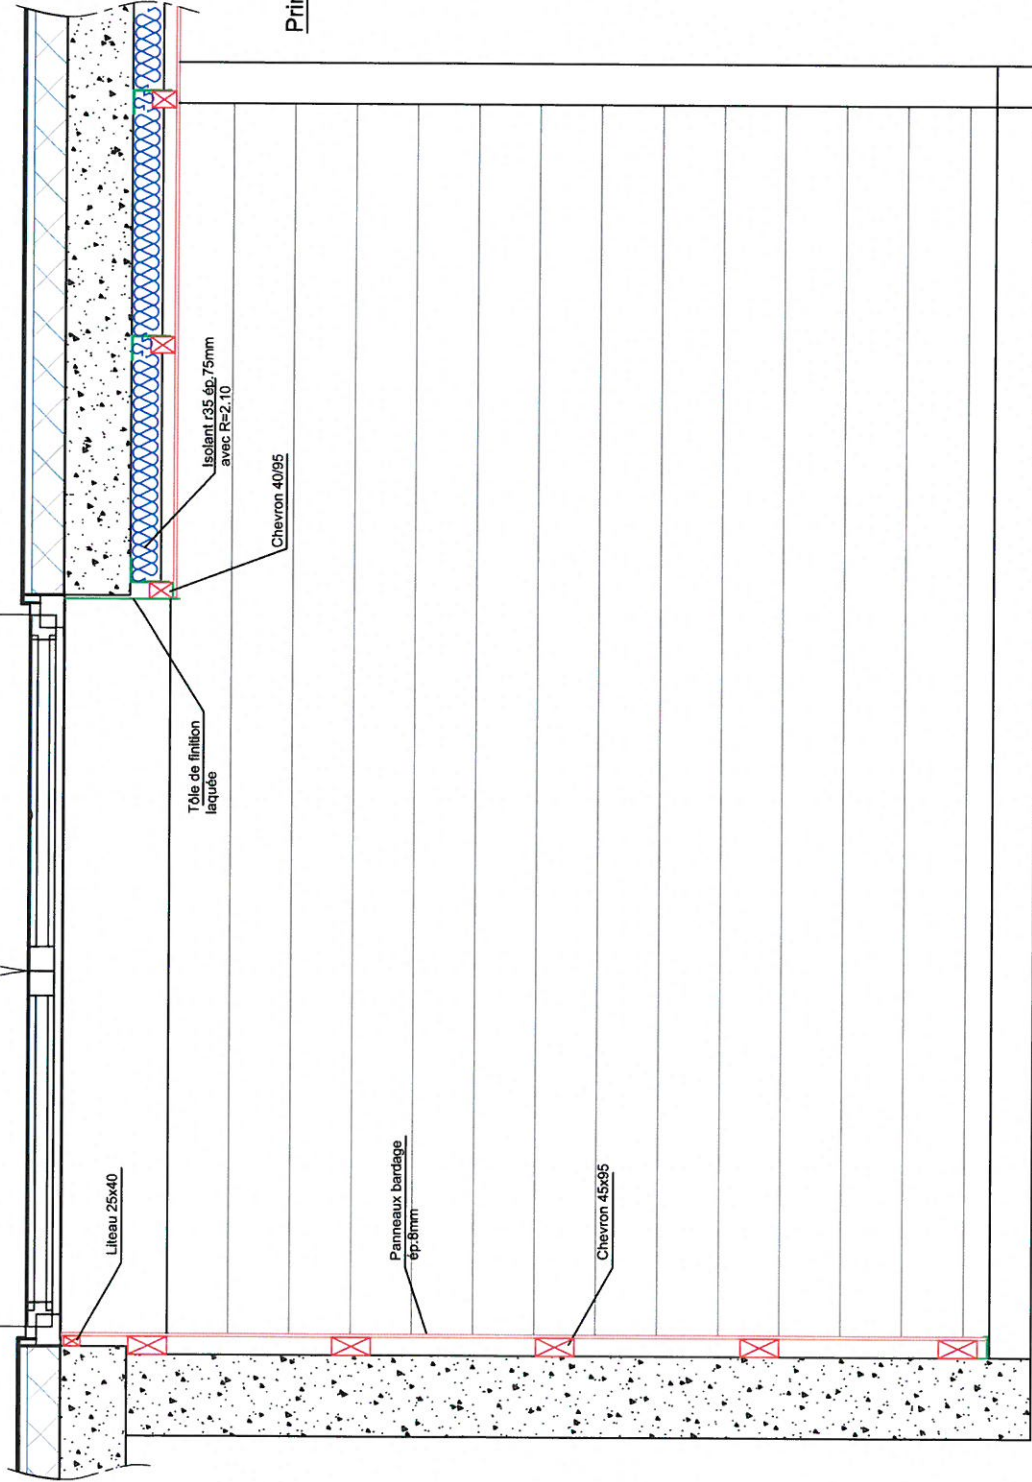

Principe d'habillage d'embrasure
sur balcon

Ech.: 1/125ème

Création de logements La Mulatière

Chemin de Fontanière


69350 LA MULATIERE

Plan de principe
Bardage Bat. C


Vêtur&Co

2 Imp de l'Echangeur
38300 BOURGOIN-JALLIEU
Tél : 04 74 93 93 08
Fax : 04 74 93 05 71

Raccordement Bardage-ITE

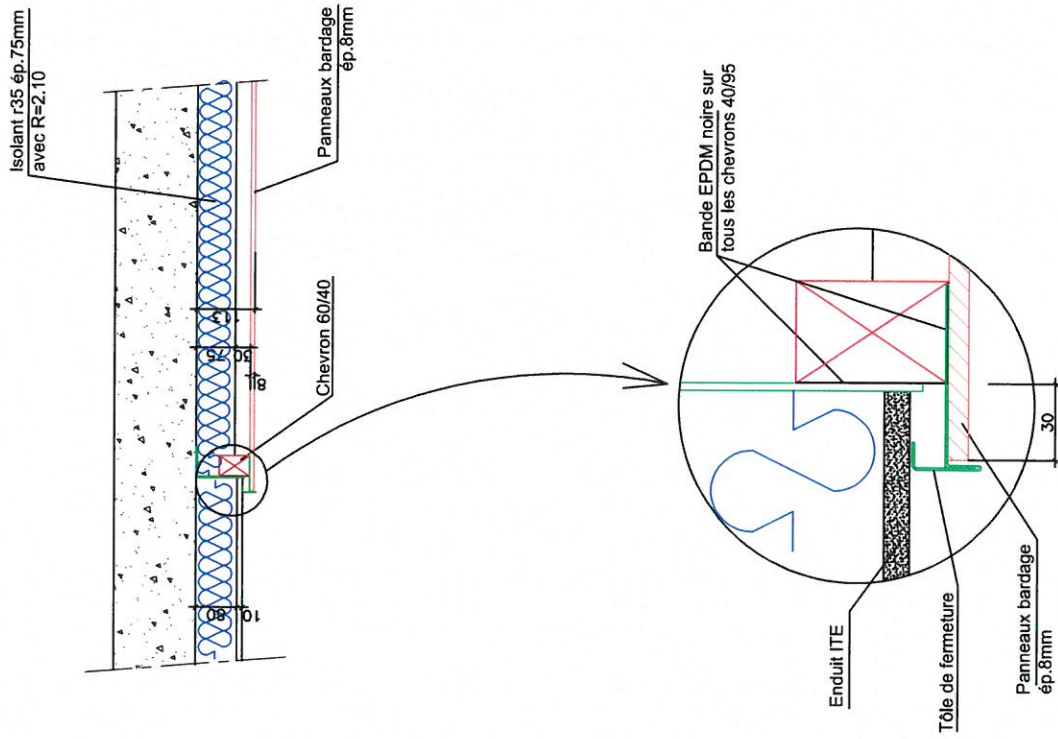

Détail liaison Nez de dalle/Sous face

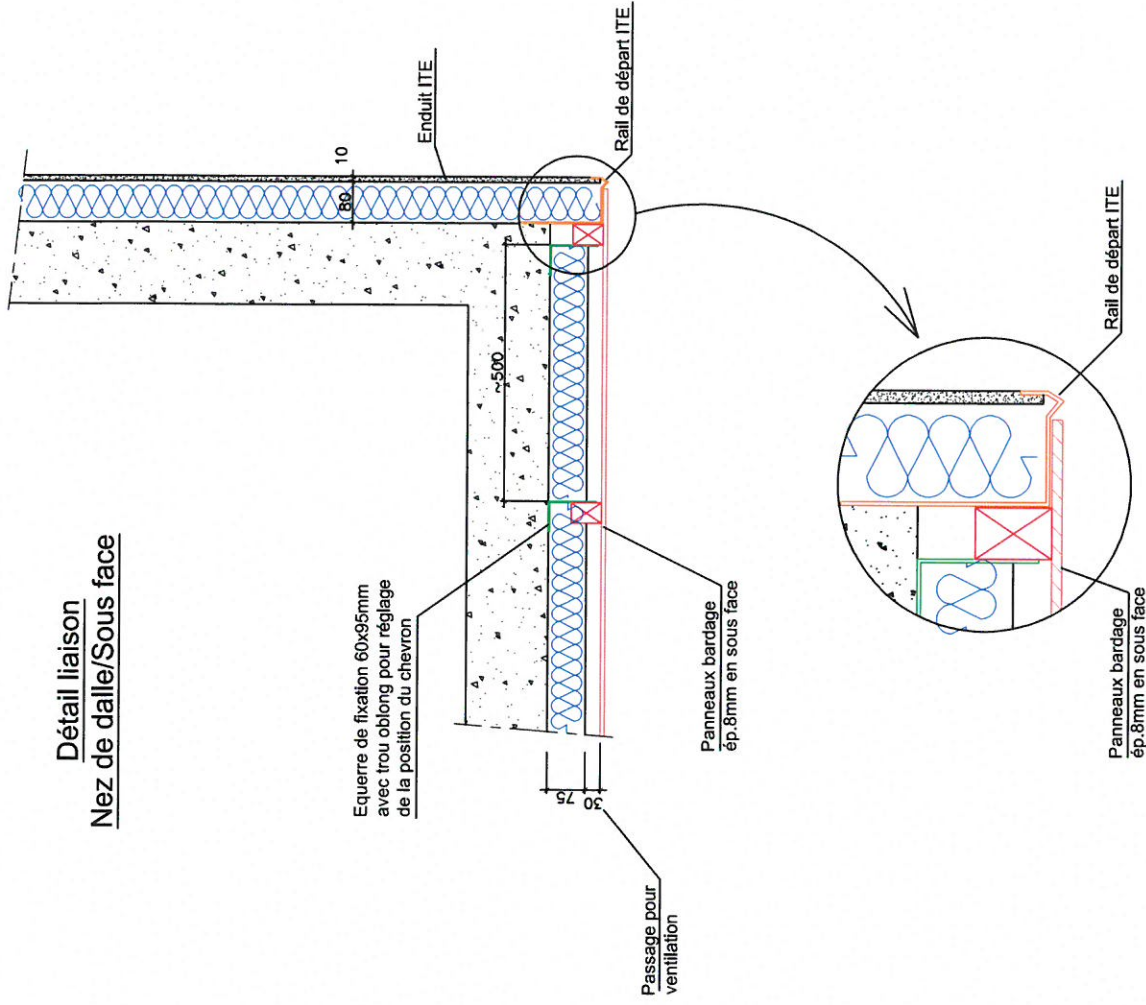


Création de logements La Muliatière

Chemin de Fontanière
69350 LA MULATIÈRE

Plan de principe
Bardage Bat. C

Vêtur&Co

2 Imp de l'Echangeur
38300 BOURGOIN-JALLIEU
Tél : 04 74 93 93 08
Fax : 04 74 93 05 71

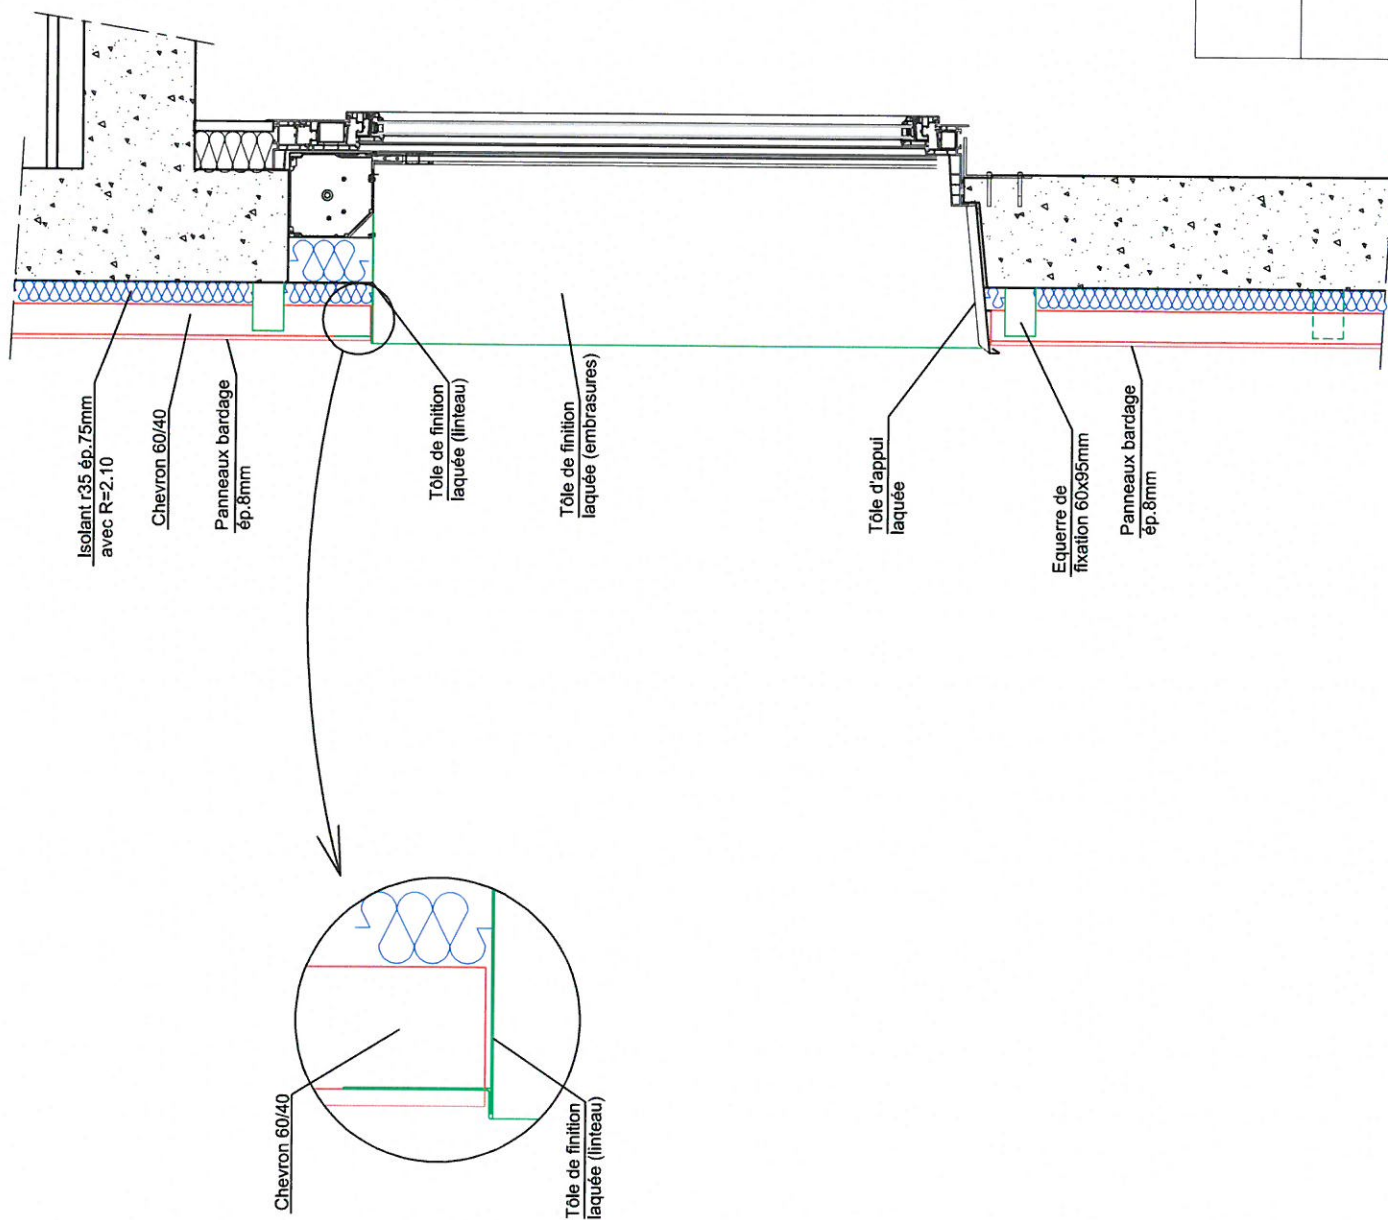

Principe de montage de l'encadrement des ouvertures

Création de logements La Mulatière

Chemin de Fontanière
69350 LA MULATIERE

Plan de principe
Bardage Bat. C

Vétur&Co
2 Imp de l'Echangeur
38300 BOURGOIN-JALLIEU
Tel : 04 74 93 93 08
Fax : 04 74 93 05 71