
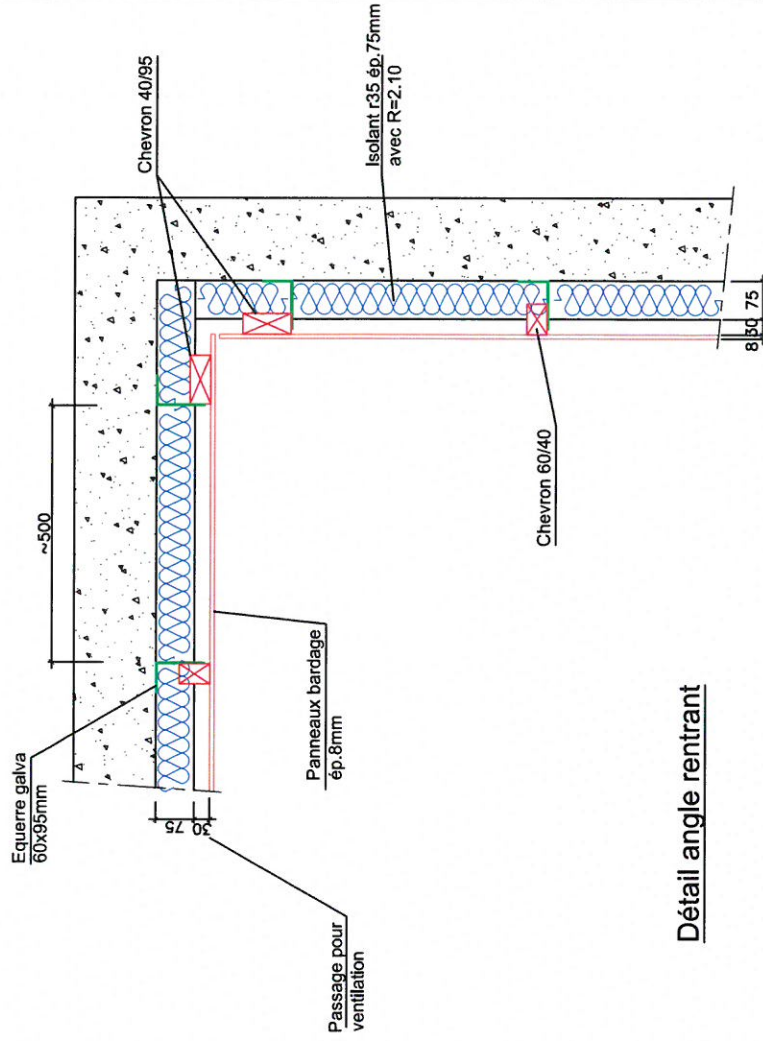


Pied de bardage RDC

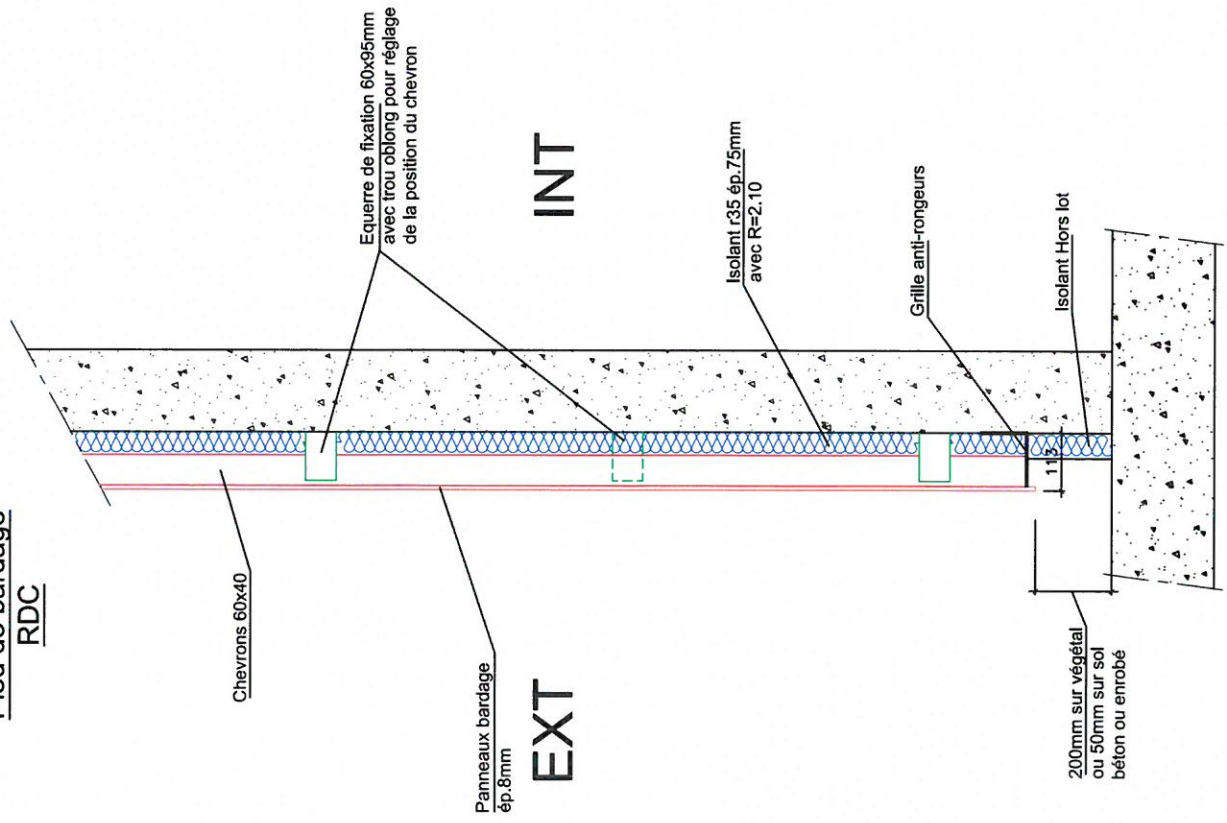

Détail angle rentrant



Création de logements La Mulière

Chemin de Fontanière
69350 LA MULATIERE


Plan de principe
Bardage Bat. C

Vêtur&Co
2 imp de l'Echangeur
38300 BOURGOIN-JALLIEU
Tel : 04.74.93.93.08
Fax : 04.74.93.05.71

Vue de dessus

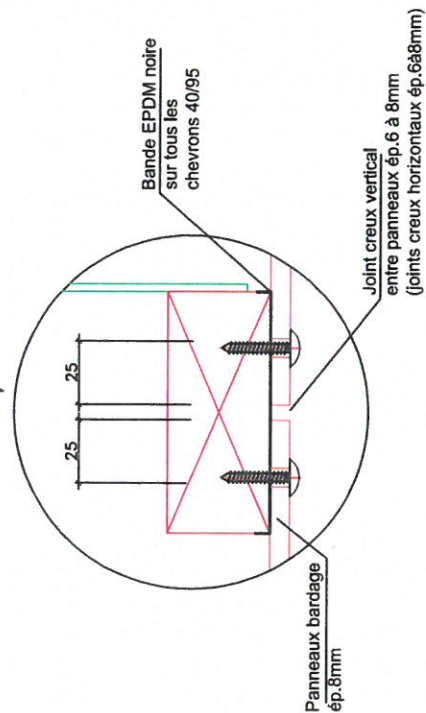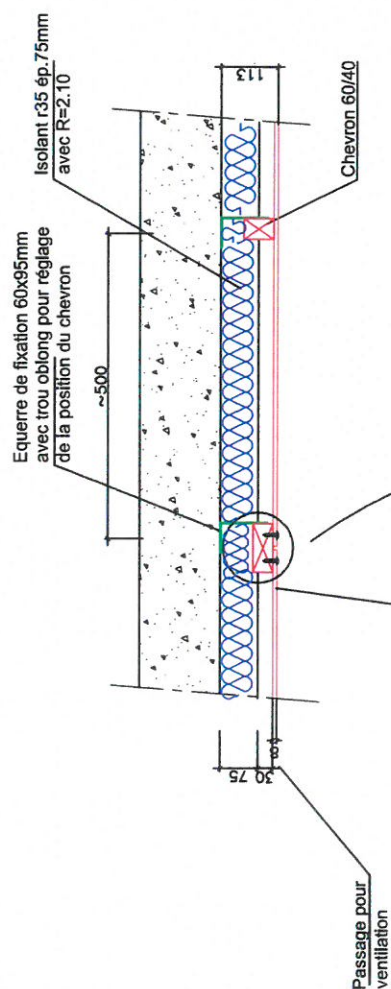

Détail angle sortant

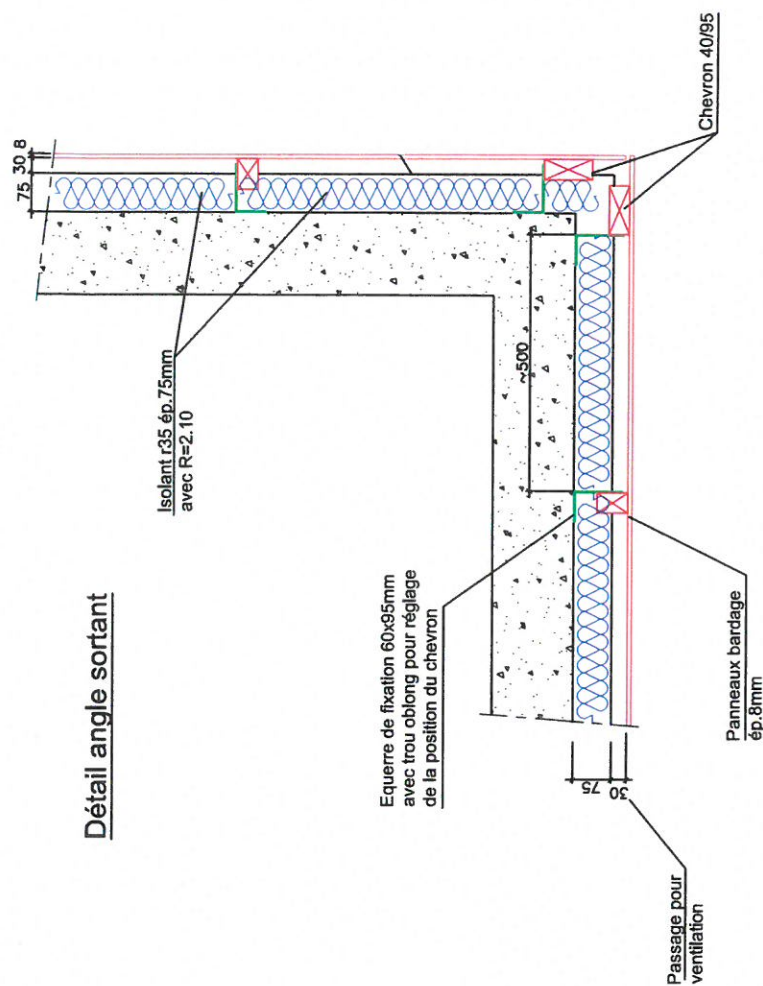

Création de logements La Mulatière





Chemin de Fontanière
69350 LA MULATIERE

Plan de principe
Bardage Bat. C

Vêtur&Co

2 Imp de l'Echangeur
38300 BOURGOIN-JALLIEU
Tél : 04.74.93.93.08
Fax : 04.74.93.05.71

Détail de principe des embrasures

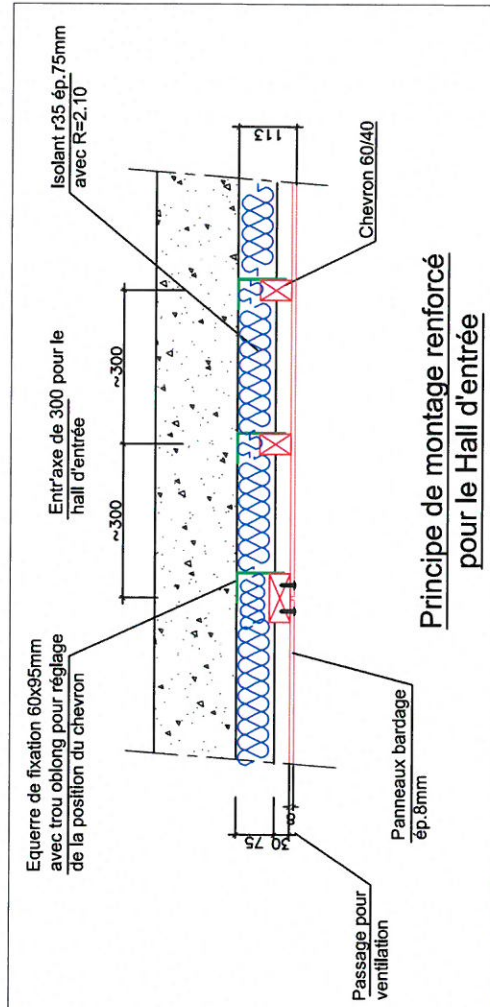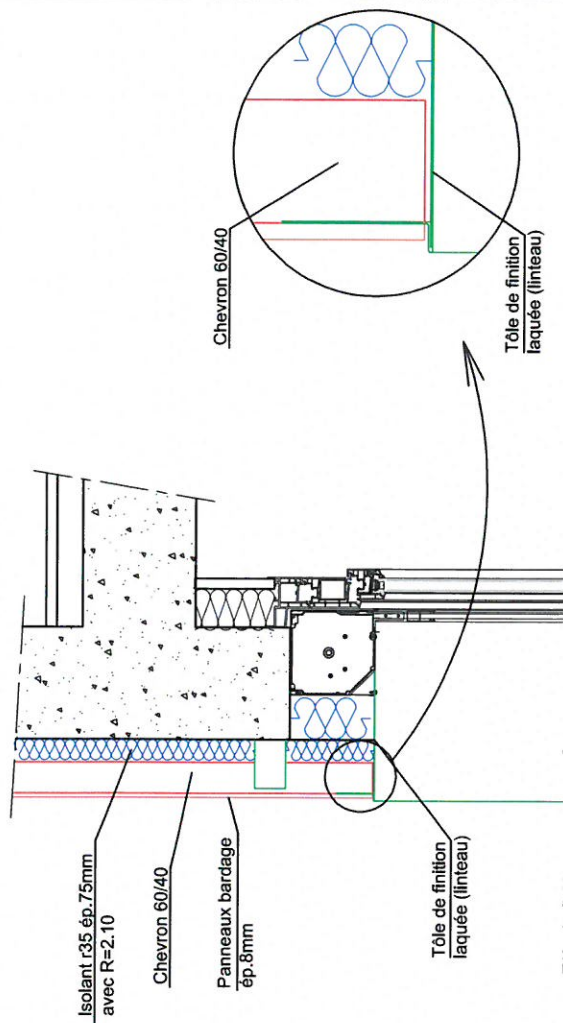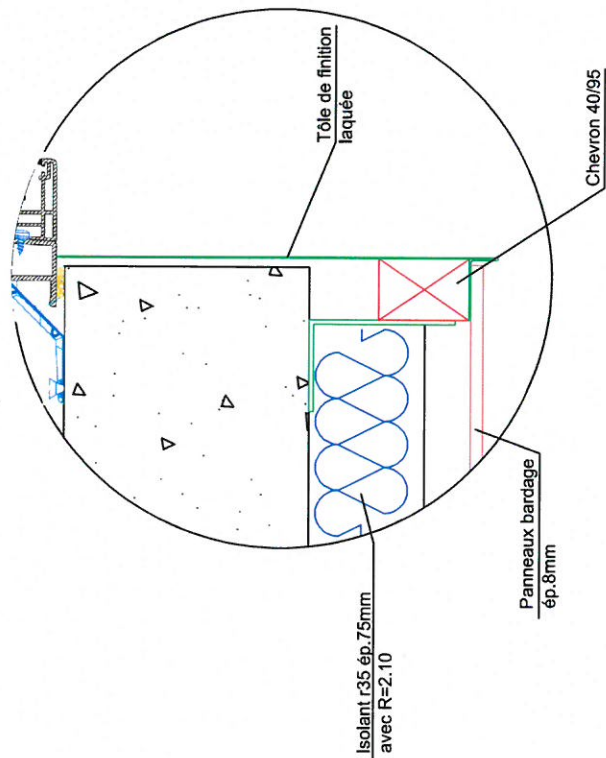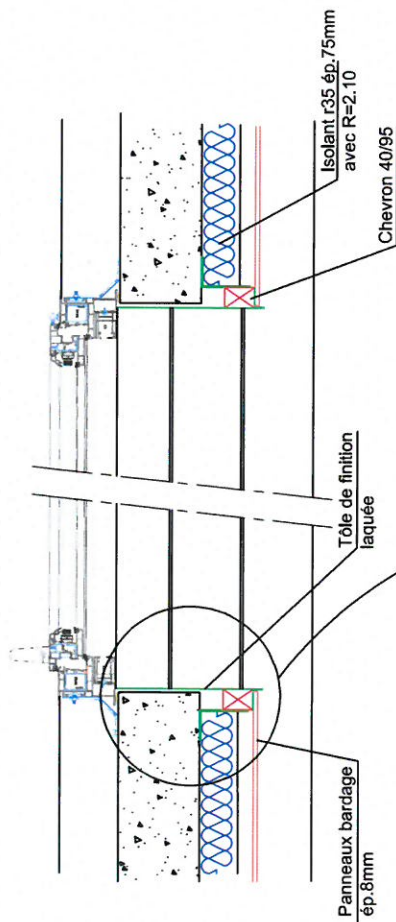


Création de logements La Mulatière

Chemin de Fontanière
69350 LA MULATIERE



Plan de principe
Bardage Bat. C

Vêtur&Co
2 Imp de l'Echangeur
38300 BOURGOIN-JALLIEU
Tel : 04 74 93 93 08
Fax : 04 74 93 05 71

Coupe sur balcons

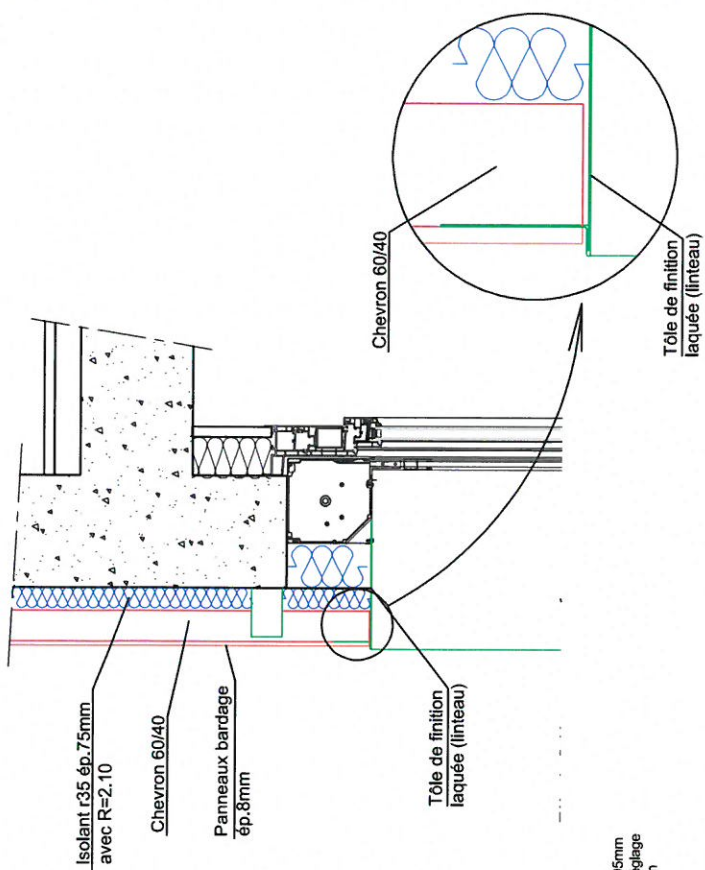

Ech.: 1/100ème
Voir principe d'embrasure

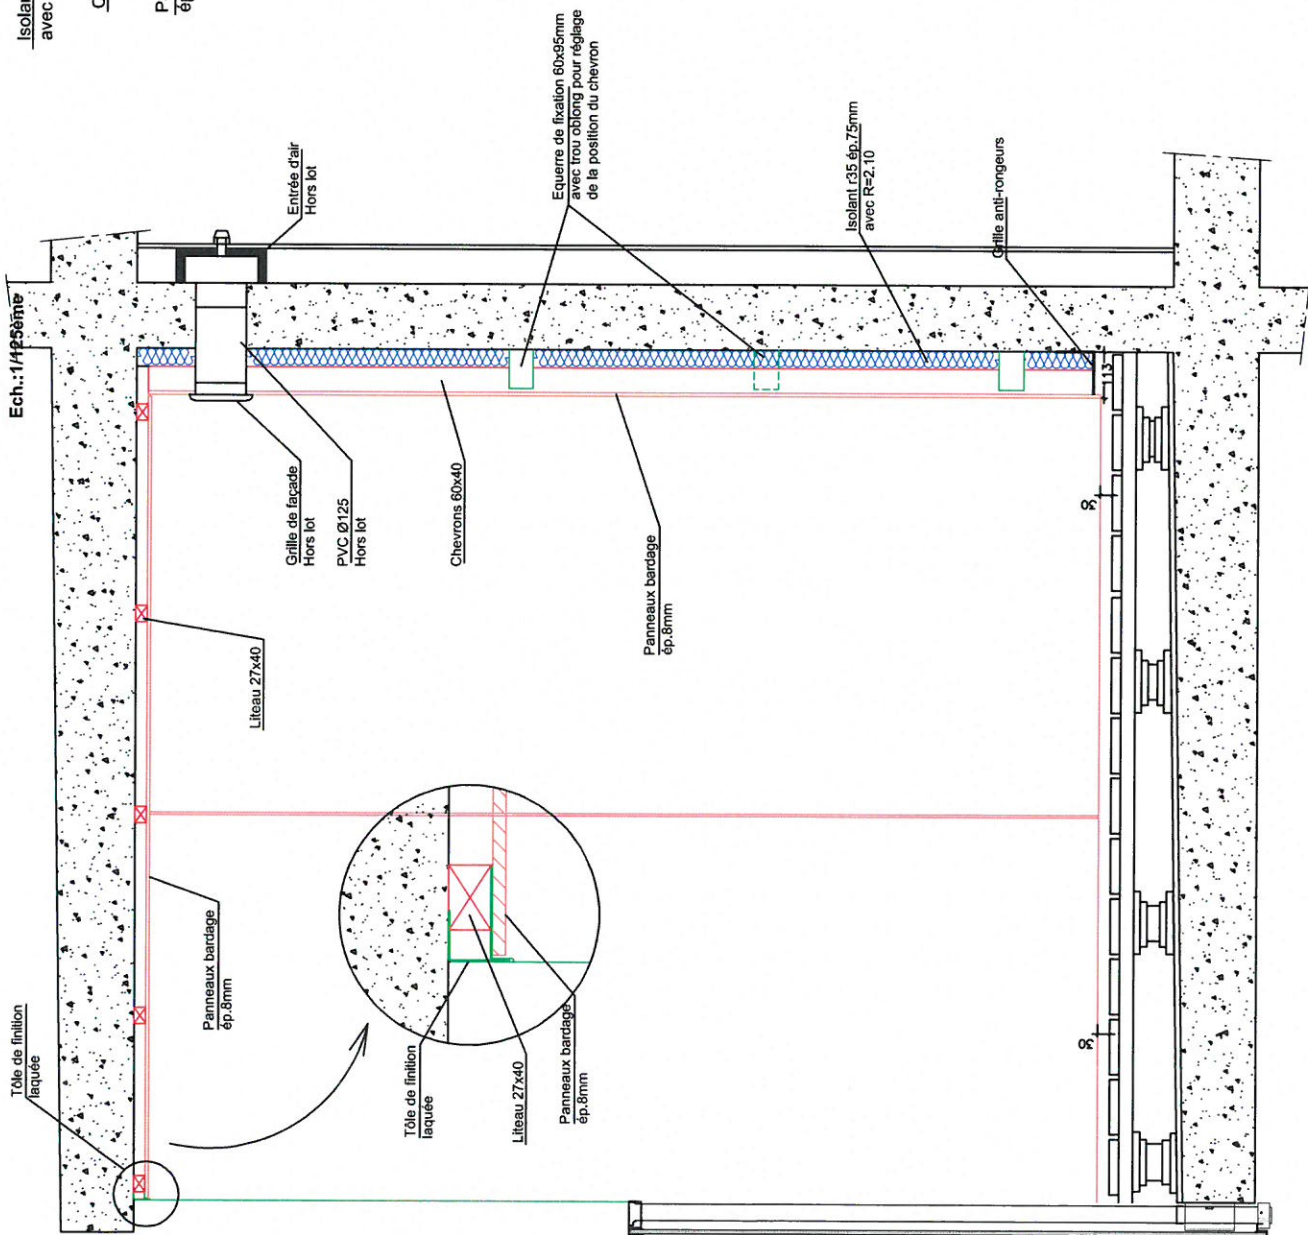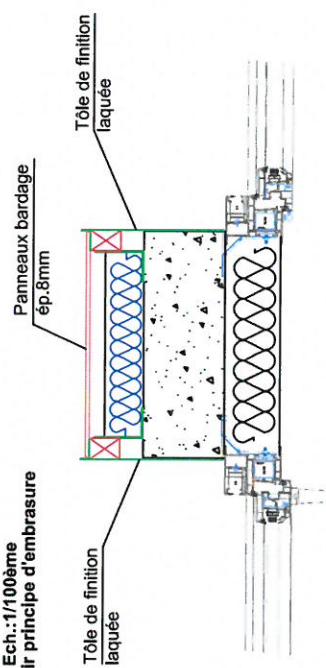

Création de logements La Mulatière


Chemin de Fontanière
69350 LA MULATIERE

Plan de principe
Bardage Bat. C

Vêtur&Co
2 Imp de l'Echangeur
38300 BOURGOIN-JALLIEU
Tel : 04 74 93 93 08
Fax : 04 74 93 05 71

Coupe sur Loggia


Ech.: 1/125ème

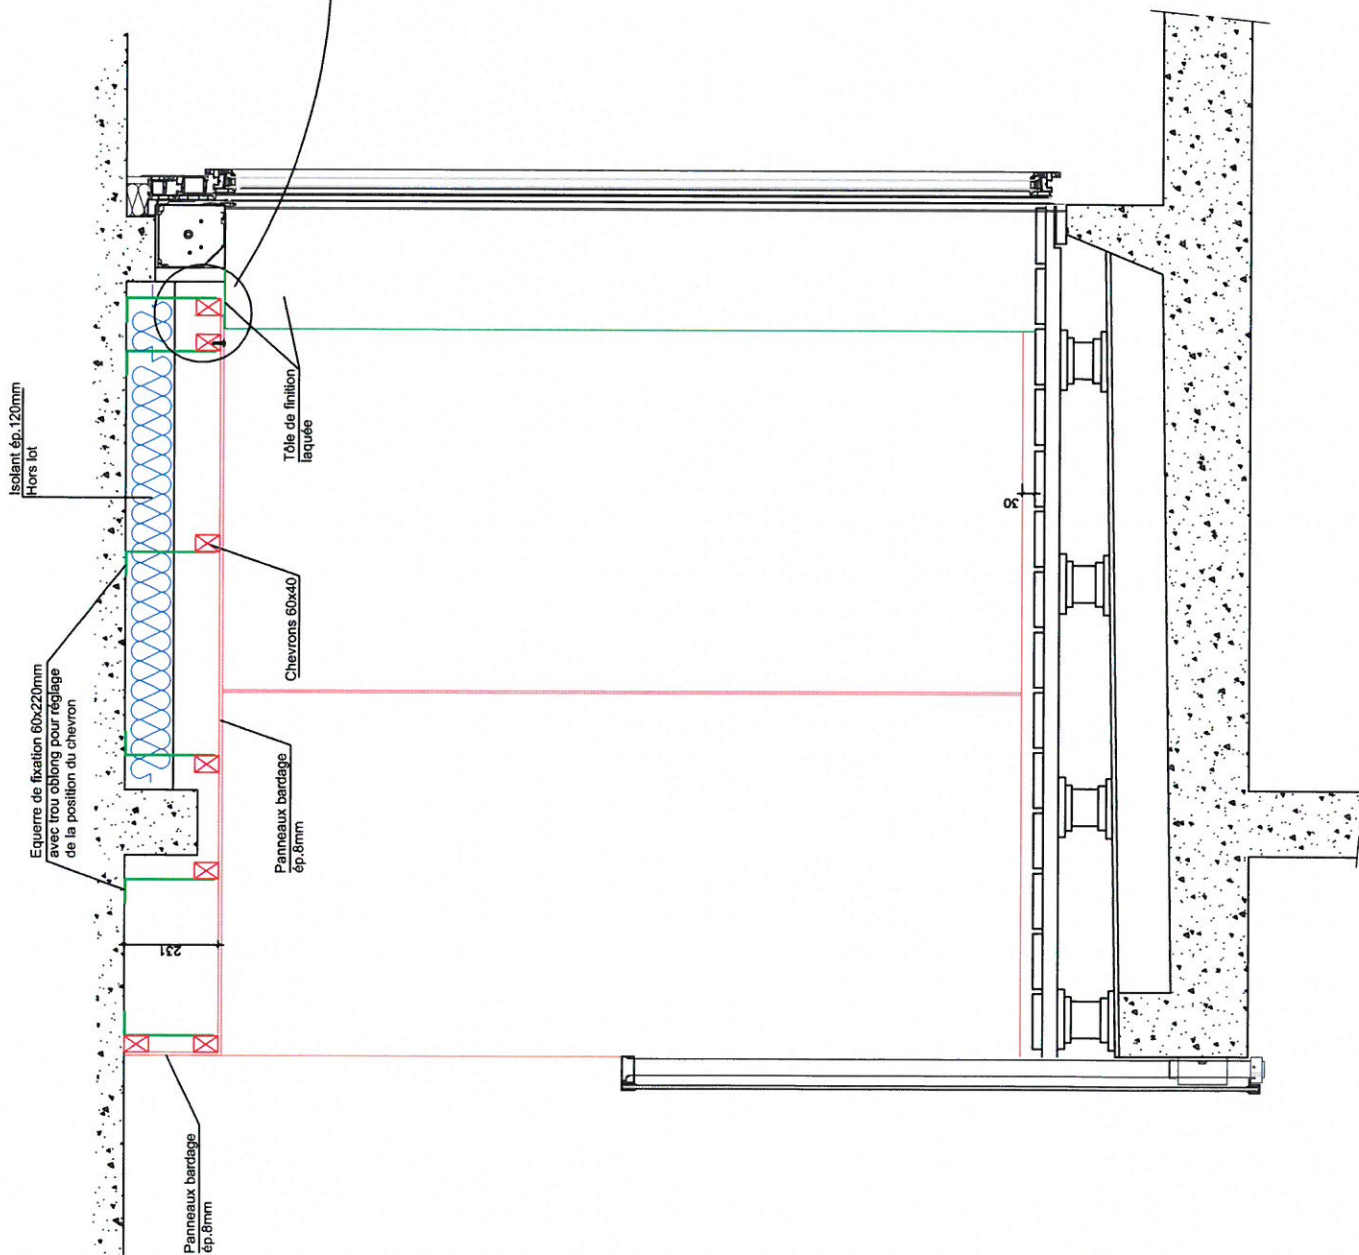

Création de logements La Mulatière
Chemin de Fontanière
69350 LA MULATIERE

Plan de principe
Bardage Bat. C

Vêtur&Co
2 Imp de l'Echangeur
38300 BOURGOIN-JALLIEU
Tel : 04 74 93 93 08
Fax : 04 74 93 05 71

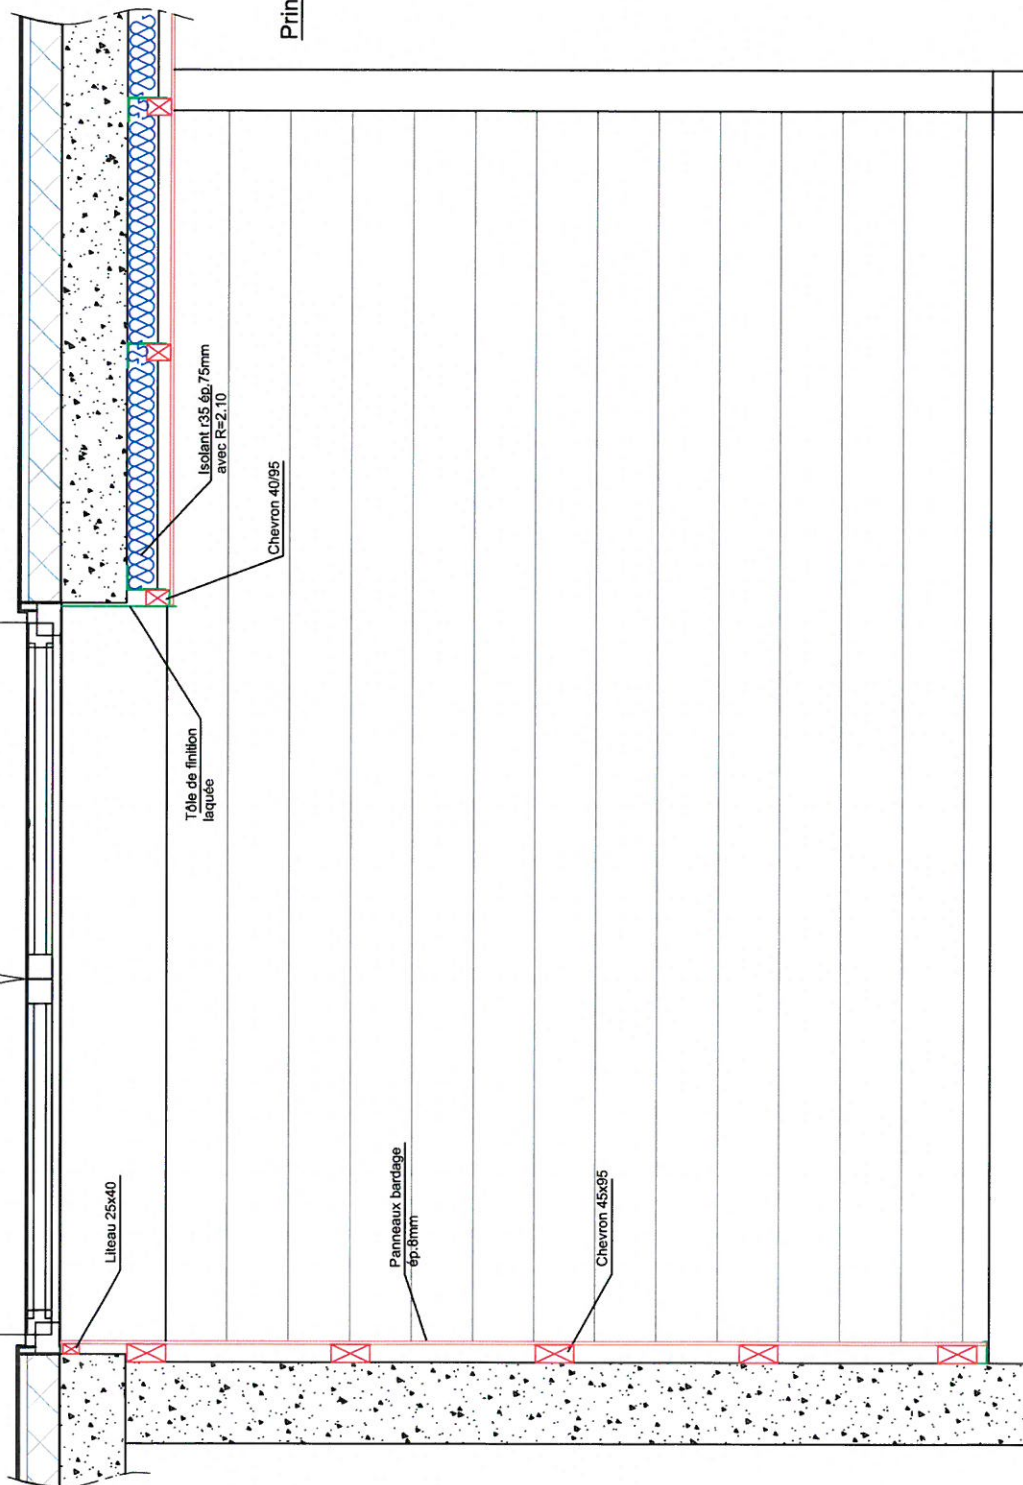

Principe d'habillage d'embrasure sur balcon

Ech.: 1/125ème

Création de logements La Mulatière

Chemin de Fontanière

69350 LA MULATIERE


Plan de principe
Bardage Bat. C

Vêtur&Co


2 Imp de l'Echangeur
38300 BOURGOIN-JALLIEU
Tél : 04 74 93 93 08
Fax : 04 74 93 05 71

Page: 7/9

Raccordement Bardage-ITE

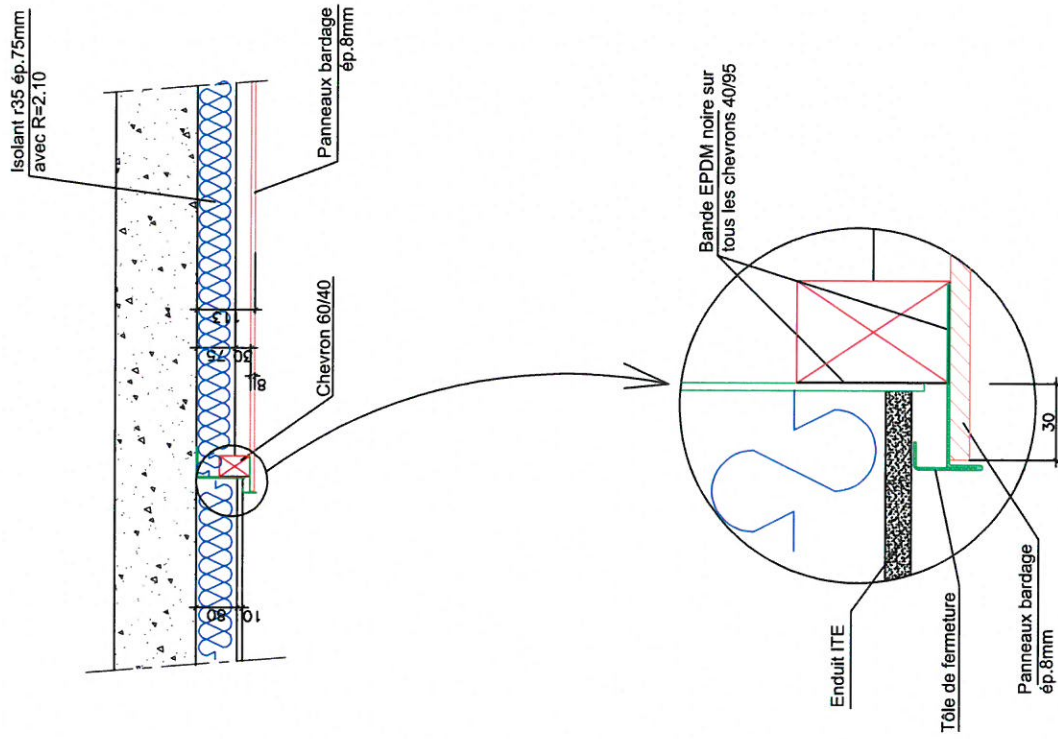

Détail liaison Nez de dalle/Sous face

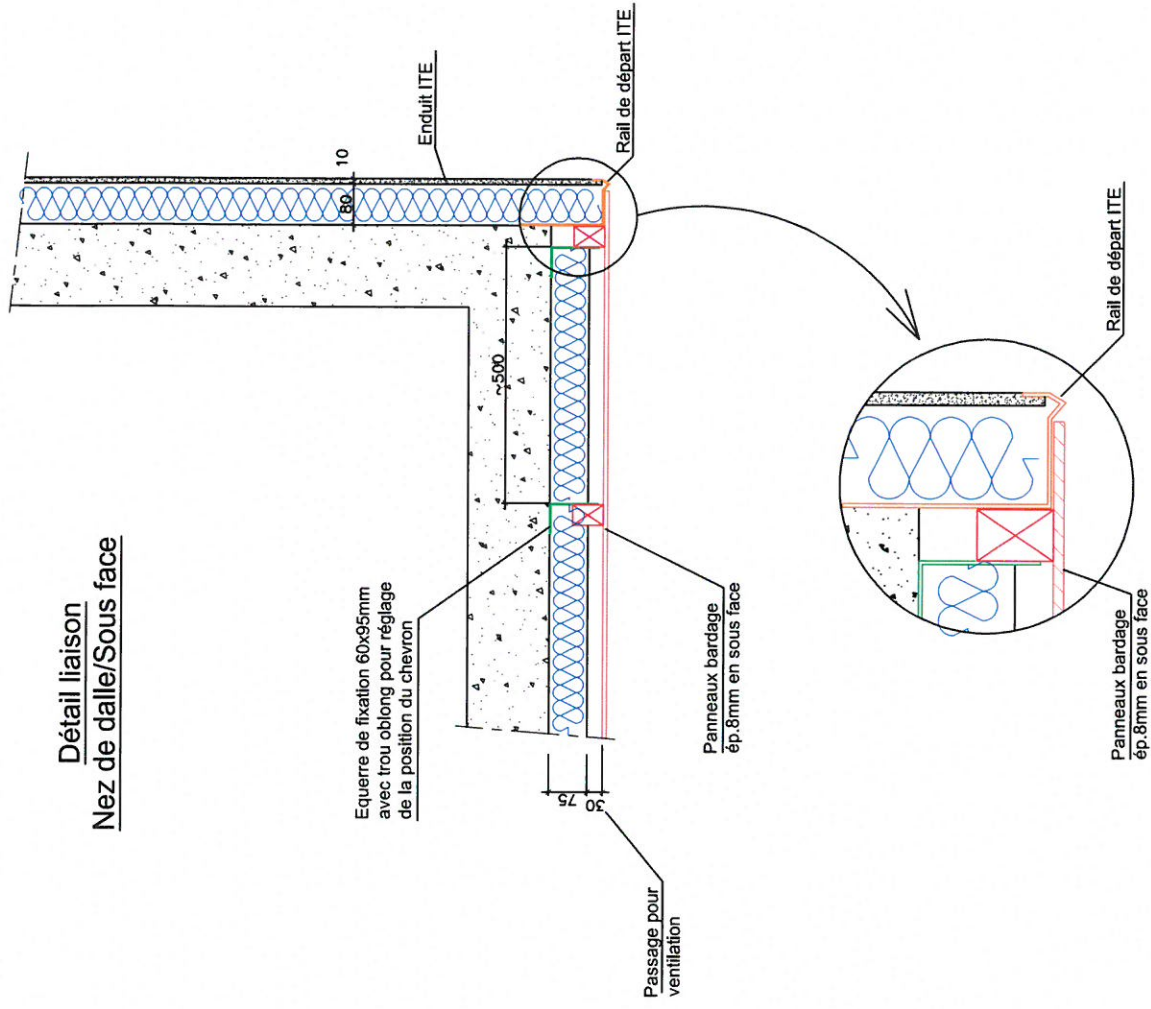

Création de logements La Mulatière

Chemin de Fontanière
69350 LA MULATIERE


Plan de principe
Bardage Bat. C

Vêtur&Co

2 Imp de l'Echangeur
38300 BOURGOIN-JALLIEU
Tel : 04 74 93 93 08
Fax : 04 74 93 05 71

Page: 8/9

Principe de montage de l'encadrement des ouvertures

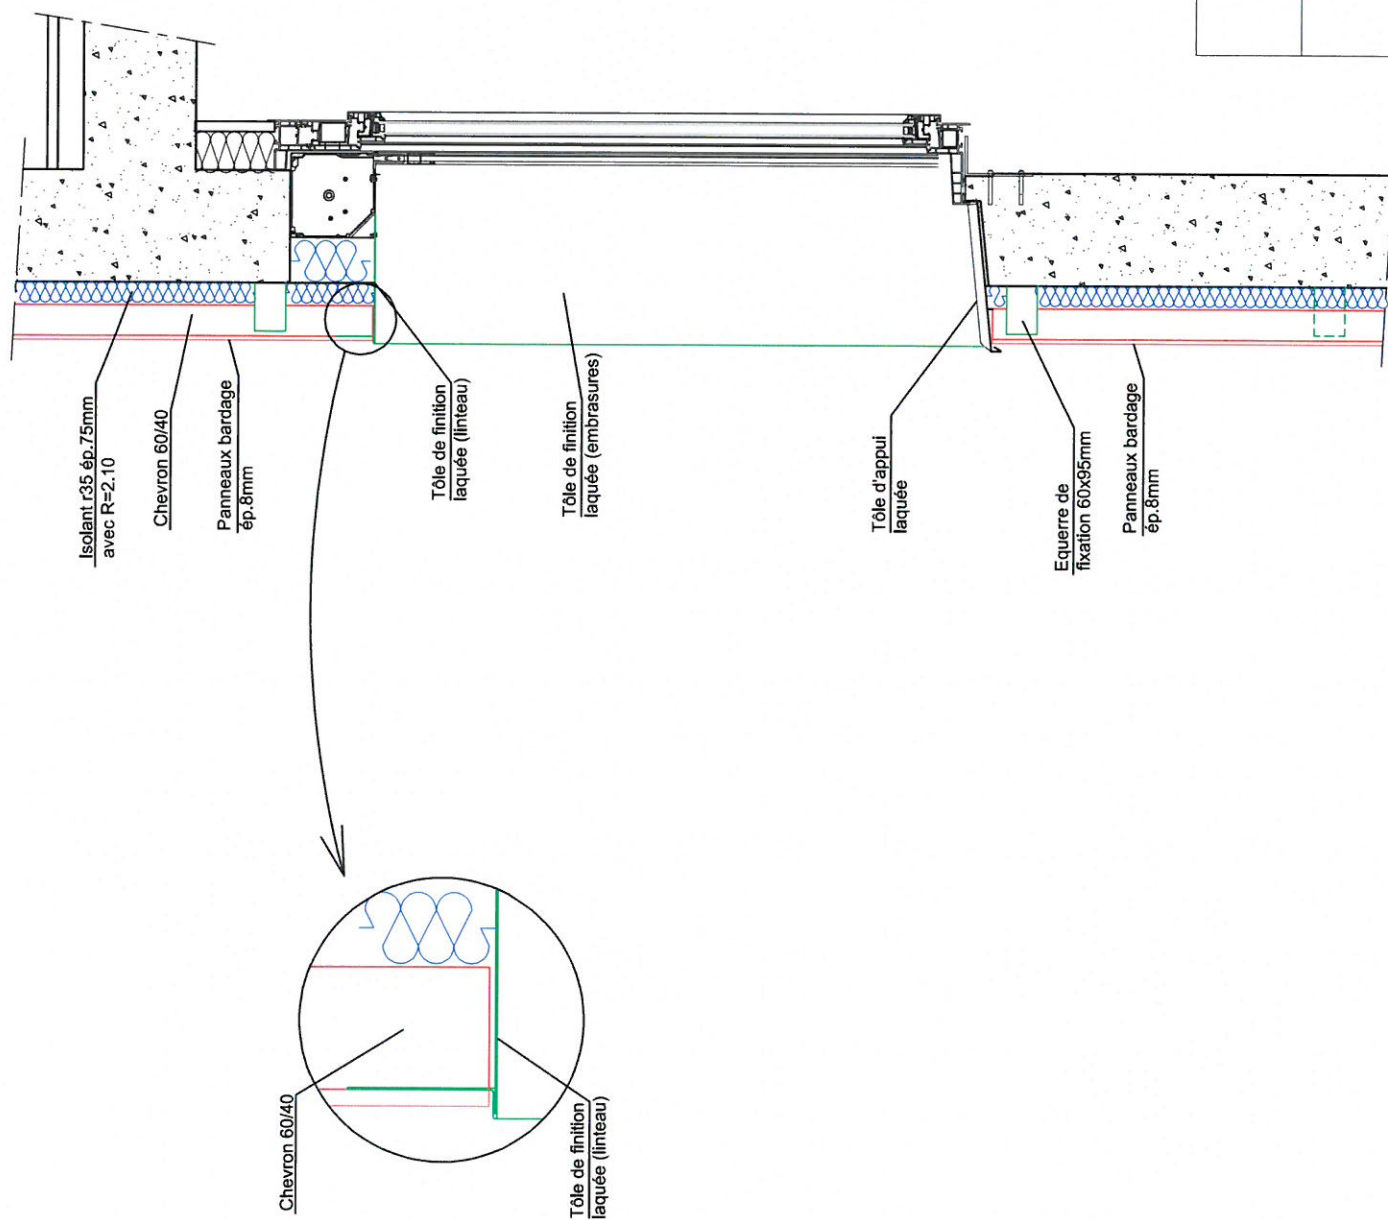

Création de logements La Mulatière

Chemin de Fontanière
69350 LA MULATIERE

Plan de principe
Bardage Bat. C

Vétur&Co
2 Imp de l'Echangeur
38300 BOURGOIN-JALLEU
Tel : 04.74.93.93.08
Fax : 04.74.93.05.71