

LA MULATIERE (69) 15L001 - Le 180 (Bât A et B)

Maître d'ouvrage : SCI NOAHO Résidence Tel : 04 78 30 33 90 David JANIN d.janin@noaho.fr Martial ANIZOT m.anizot@noaho.fr	Architecte : ATELIER DE LA PASSERELLE (Bât A et B) Tel : 04 78 59 59 00 Adeline GUELLAFF a.guellauff.passerelle@orange.fr ATELIER D'IS (Bât C) atelierdis@atelierdis.com T. PANISSET - 04 78 29 20 52	(OPC - MOE) : PSO INGENIERIE Tel : 04 74 84 37 27 Paul SOLIGNAC - 06 60 08 28 26 paul.solignac@ps-engineierie.fr Thomas PARRA - 06 62 72 02 70 thomas.parra@ps-engineierie.fr
Bureau de contrôle : VERITAS Tel : 04 72 29 70 70 Rémi BUGAUD remi.bugaud@fr.bureauveritas.com	BET Structure : MATTE Tel : 04 72 69 86 08 Phala LIN - 06 73 47 87 27 lin@matte.fr Jacques BONDETTI - 06 07 29 31 90 bondetti@matte.fr	Maçon : FONTANEL Tel : 04 72 26 39 70 Sullivan PONTET - 06 17 32 25 84 s.pontet@fontanel-sa.fr PB Construction (Bât C) Tel : 04 78 73 49 71 - pbc@pb-constructions.fr Jean Claude BONI Rémi SORIANO - 06 03 62 38 36

Carnet de plans

(**38** pages entête comprise)


Rue des bouleaux
01460 PORT
Tel : 04 74 76 26 66
Fax : 04 74 76 28 26

Nos réservations en gros oeuvre sont établies sur la base des plans architecte utilisés pour les plans de repérage ci-joint.

Sans remarque écrite sous 8 jours, ces plans seront considérés comme approuvés.

Les cotes tableau Brut et épaisseur d'isolant sont données en fonction de notre marché et conformément aux plans architecte. Cependant, certaines peuvent être modifiées pour respecter des normes ou réglementations. Ces cotes étant contractuelles, nous déclinons toute responsabilité dans le cas où des modifications seraient apportées sans avis.

Interlocuteur PORALU : Franck Boudier GSM : 06 16 95 58 39 Tel : 04 72 79 09 94 Fax : 04 72 79 09 91 Email : f.boudier@poralu.fr	Indice	Date	Dessinateur	Descriptif des modifications
	A	22/06/2015	M. Branchu	Première diffusion pour validation
Observations & Commentaires : Volr notes d'observations et de commentalres en page 2 .	B	17/09/2015	M. Branchu	Mise à jour des Rep. L, M, Q et R conforme aux plans d'étanchéité. Bât.A R+1 : K1 et K3 -> L1 et L2. Bât.A R-1 : Ajout d'un Rep.D2. Rectif. couleur châssis => Bât.B R-4 : J4 -> J3 et R-5 : O2 -> O1. ATTENTION : Cotes brutes = Cotes finies (finition grésé).
	C	25/09/2015	M. Branchu	Bât. A au R+1 : Réserve sol 12cm sur logts 106, 107, 108 et 109 (rep I->N, J->O et L->Q). Bât. B au R-3 : Réserve sol 12cm sur logts S303 et S304 (rep K->P et R->G).
				Bât. B au R-4 : Reprise hauteur seuil sur terrasse non accessible (rep O1->N2).



Rue des bouleaux
01460 PORT
Tel : 04 74 76 26 66
Fax : 04 74 76 28 26

Notes d'observations et de commentaires

Le 17/06/2015

Affaire : LA MULATIERE (69) 15L001 - Le 180 (Bât A et B)

Ce carnet de réservations a été réalisé avec les plans **MARCHÉ** indice B (du 06/2015).

Ce carnet de plans présente des coupes et réservations dites de principe. Les cotes L, H, ALL, S et RET sont des dimensions finies.

Le 22/06/2015

Indice A :

Pose des menuiseries VR monobloc en applique intérieur.

A. Bâtiment A

A.A. R-2 (logt 103) Ch.3 : Châssis 100x220 noté OF1/AFV sur plan de niv. et DPGF et PF1 sur façade!? Vu, ok pour OF1/AFV.

A.B. R+1 (logt 109) façade S-O Accès balcon : La hauteur des châssis est différente sur le même balcon Ch.1 (ht 208 soit un seuil de 12cm) et séjour (ht 220 soit un seuil à 0). Partis en ht 220 car balcon donnant au-dessus des accès garages et local technique. Serait-il possible d'éclaircir ce point.

B. Bâtiment B

B.A. Lorsque des châssis de valeur acoustique différente se trouvent dans une même pièce, la valeur la plus haute s'applique sur l'ensemble des menuiseries.

Le 17/09/2015



Indice B :

ATTENTION : Cotes brutes = Cotes finies (finition grésé => épaisseur négligeable).


(Pour des raisons de simplification l'épaisseur de l'enduit sur les coupes n'a pas été supprimée. Le tableau quantitatif, quand à lui, a été rectifié).

Voir l'annexe au CCTP/DPGF en fin de DPGF (mémoire technique).


Rappel : Ce carnet est à valider.

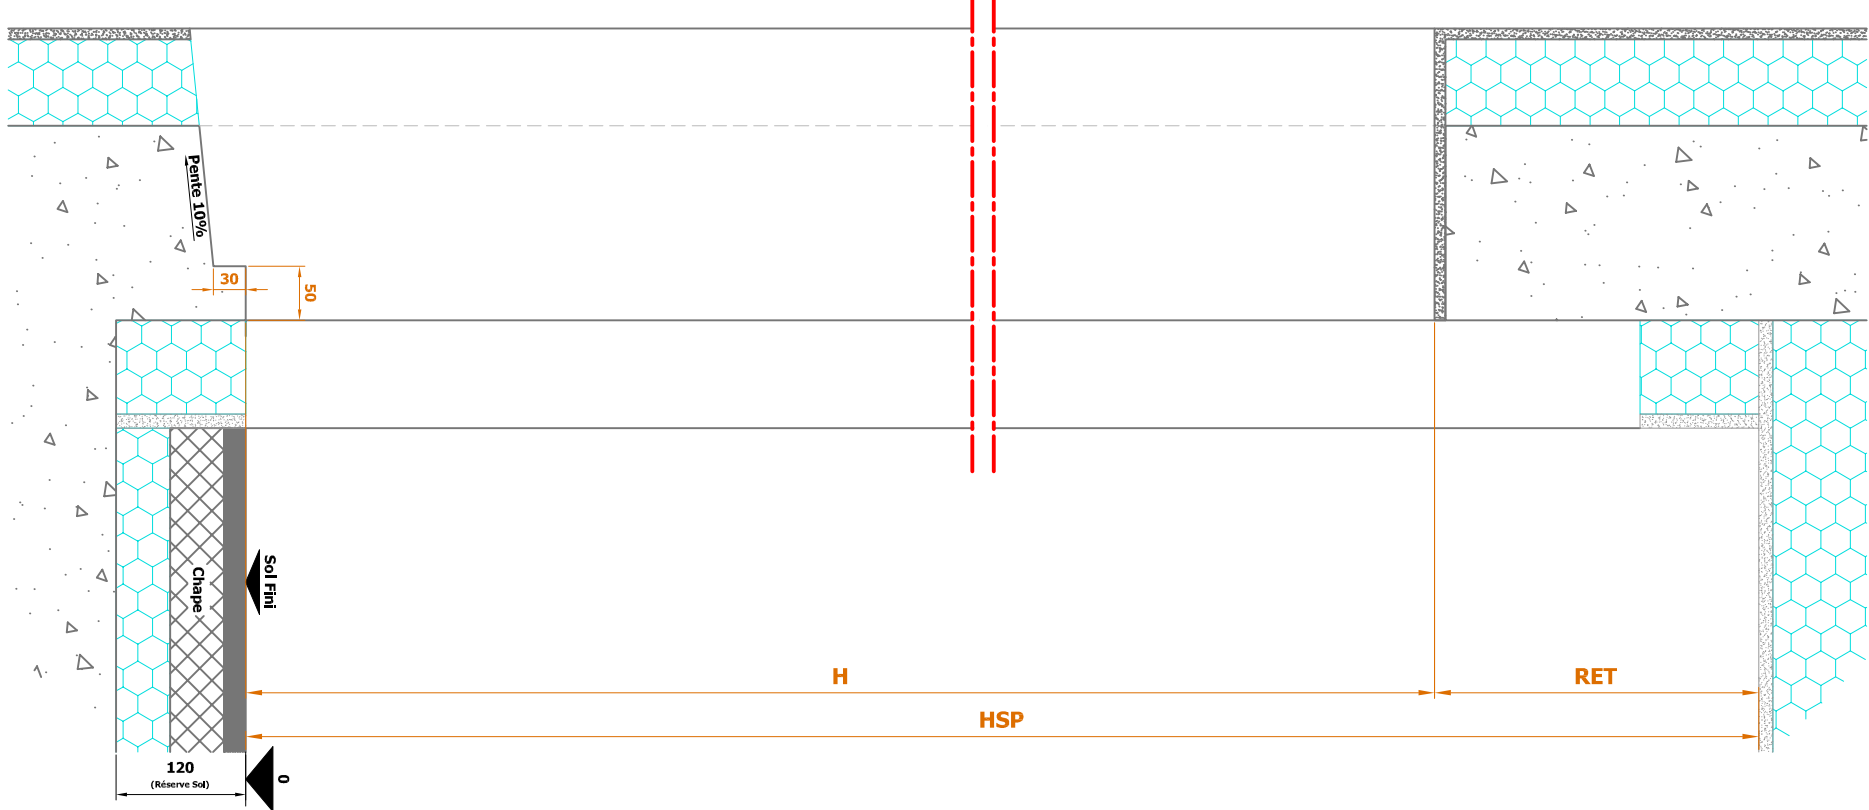
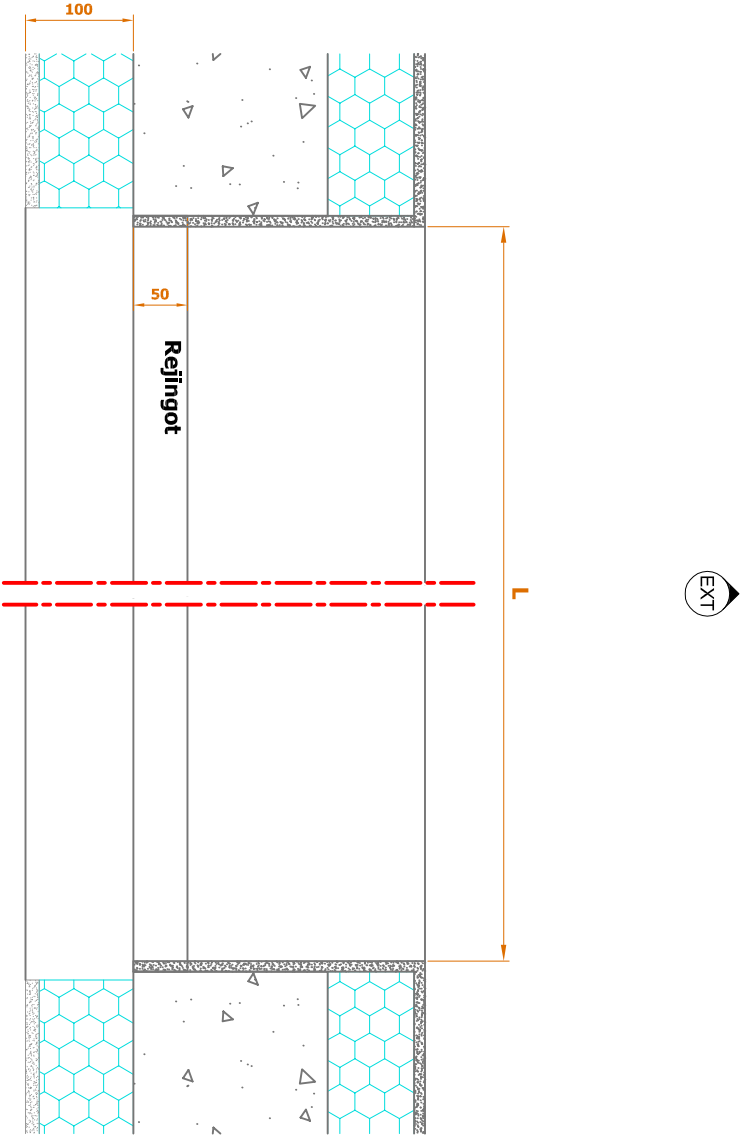


- Lexique :
- L : Largeur
 - H : Hauteur
 - S : Seuil
 - ALL : Allège
 - RET : Retombé de linteau
 - HSP : Hauteur Sous Plafond
 - HSD : Hauteur Sous Dalle
 - HSL : Hauteur Sous Linteau
 - AP : Axe de Poignée
 - A : Entraxe
 - AM : Axe du Meneau
 - AT : Axe de la Traverse
 - LO : Largeur hors tout Ouvrant
 - HO : Largeur hors tout Ouvrant
 - AB : Axe de Battement d'ouvrant
 - PL : Passage Libre
 - CA : Cote Architecte


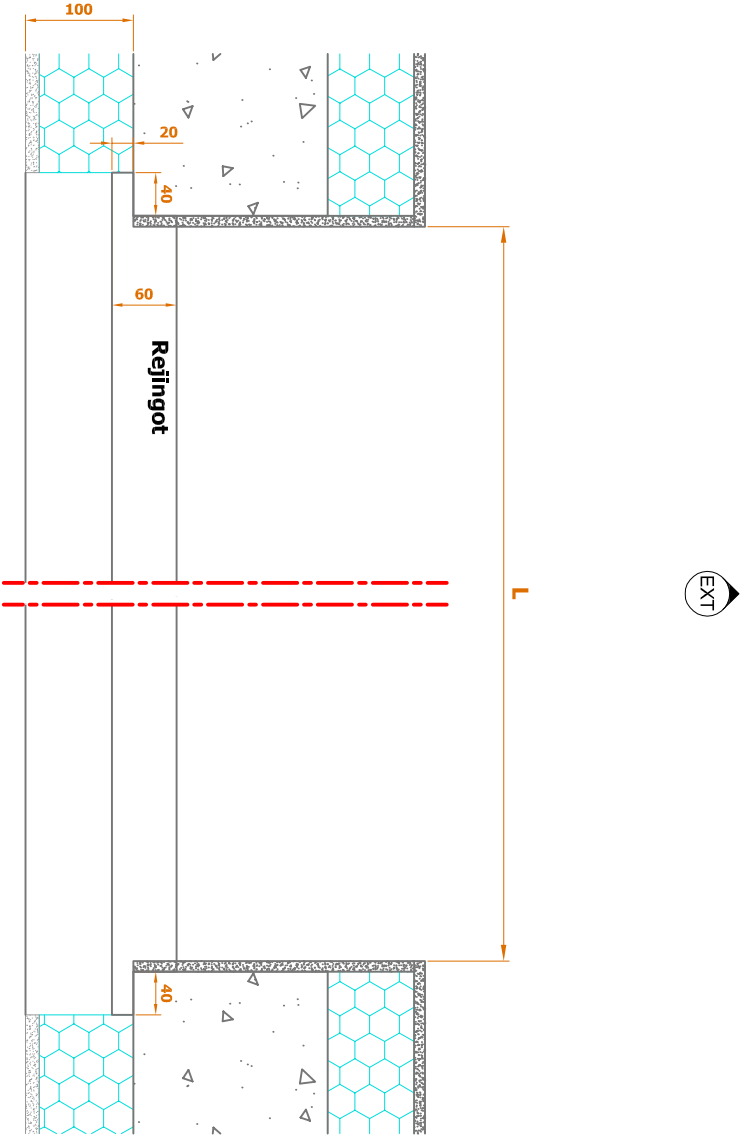


Lexique :
L : Largeur
H : Hauteur
S : Seuil
ALL : Allège
RET : Retombé de linteau
HSP : Hauteur sous Plafond
HSD : Hauteur sous Dalle
HSL : Hauteur sous Linteau
AP : Axe de Poignée
A : Entraxe
AM : Axe du Meneau
AT : Axe de la Traverse
LO : Largeur hors tout Ouvrant
HO : Largeur hors tout Ouvrant
AB : Axe de Battement d'ouvrant
PL : Passage Libre
CA : Cote Architecte


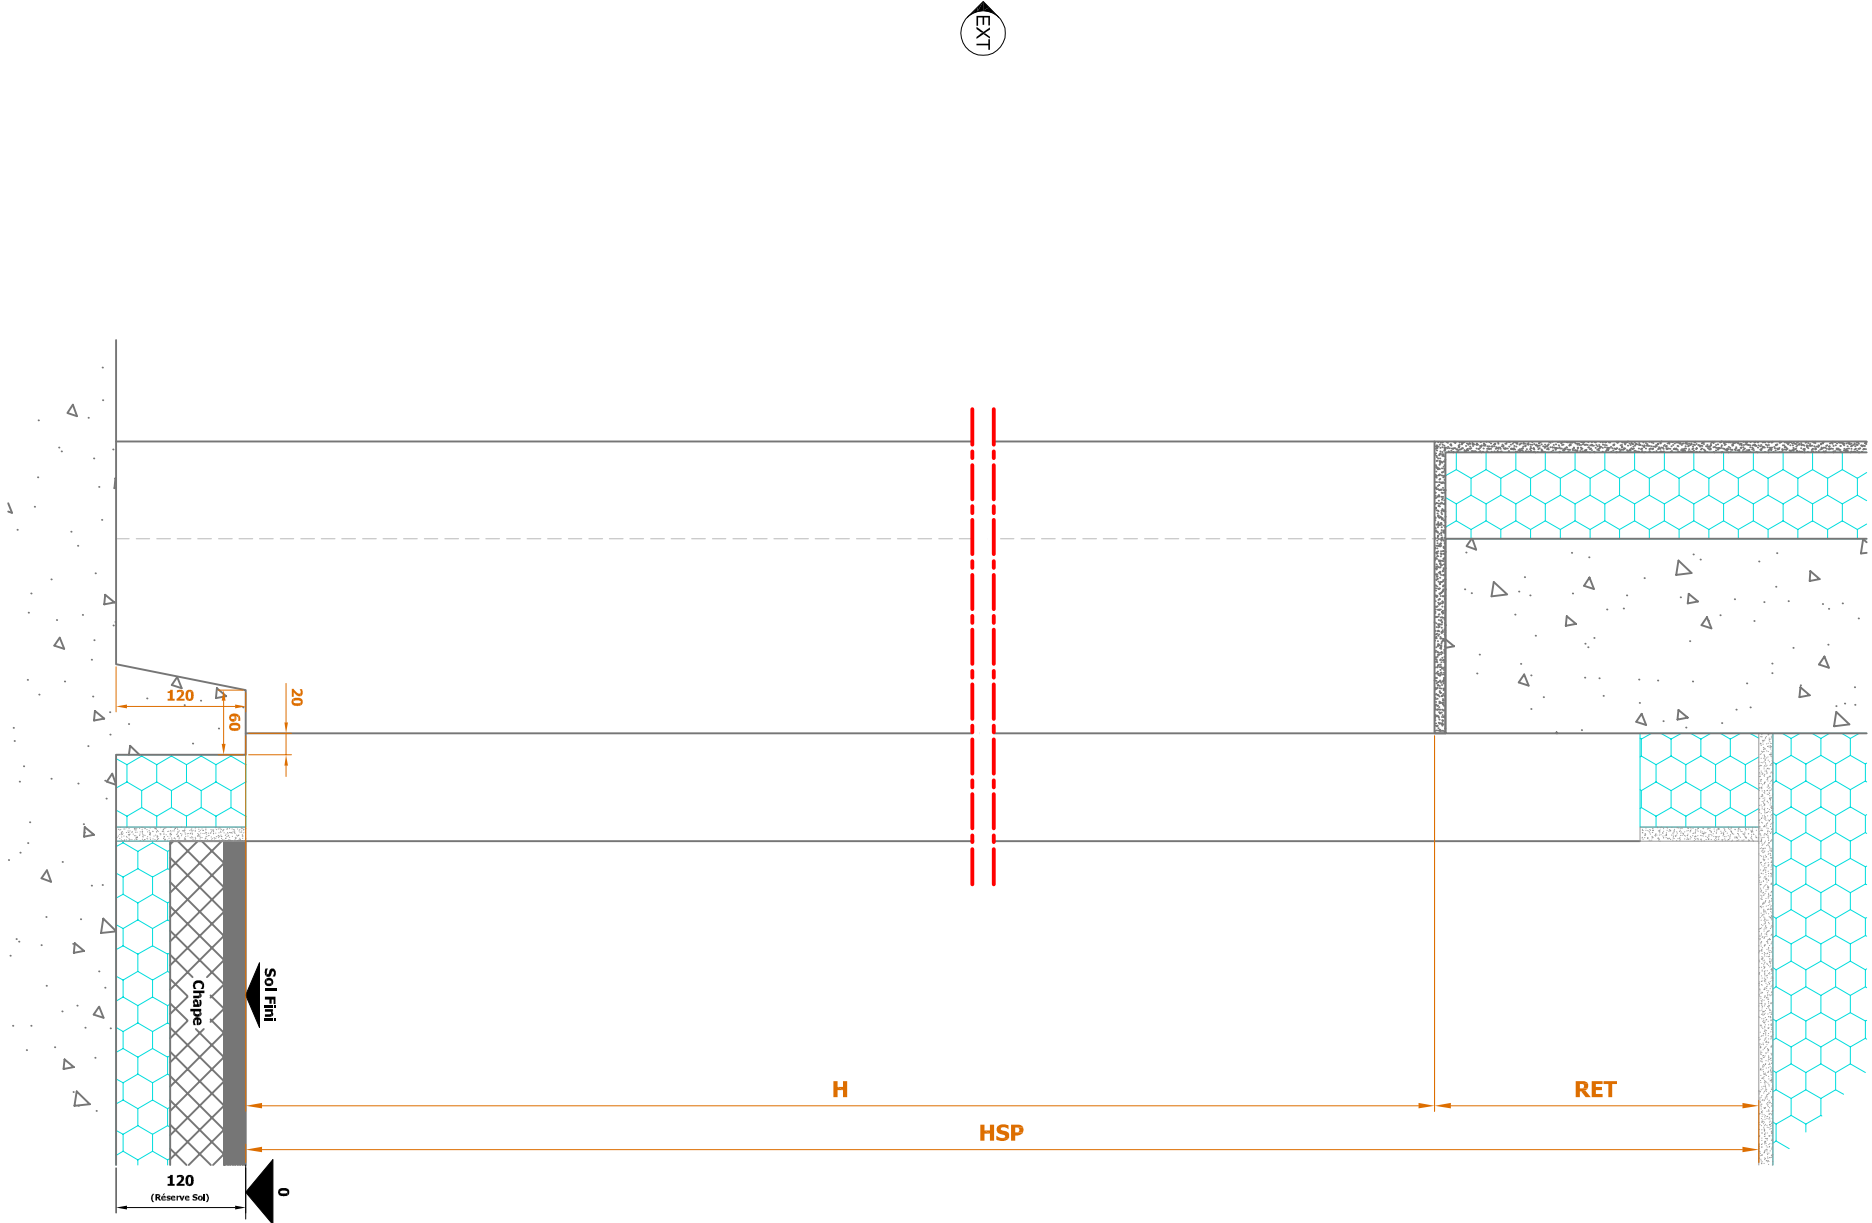


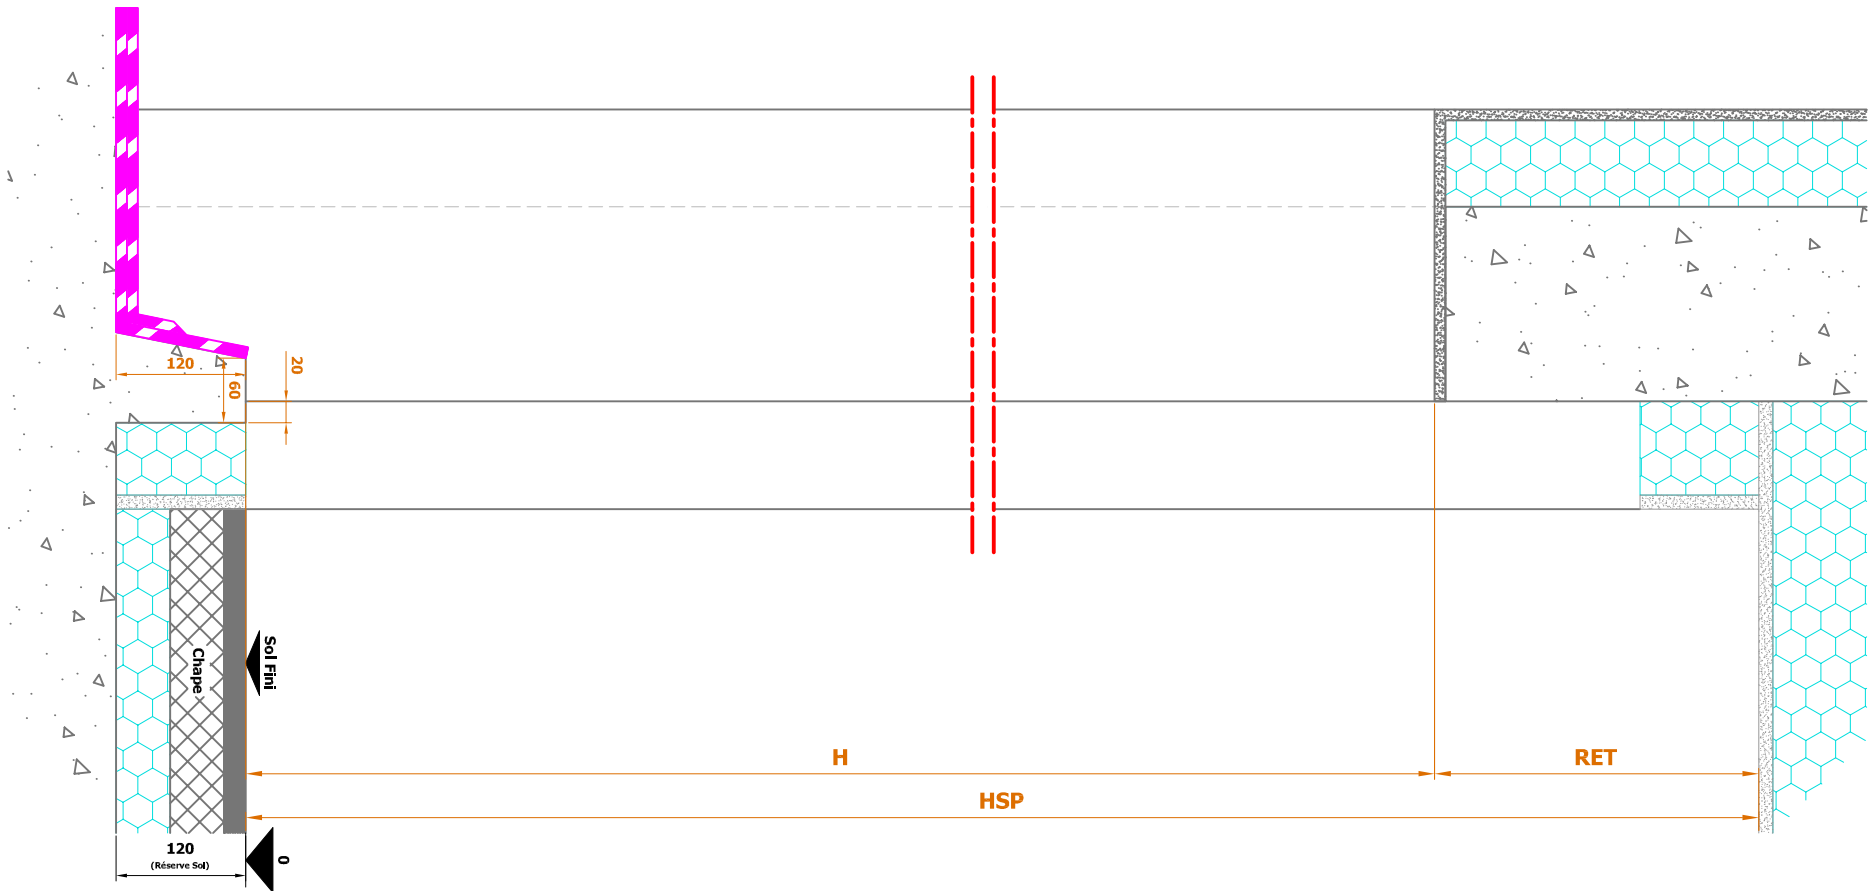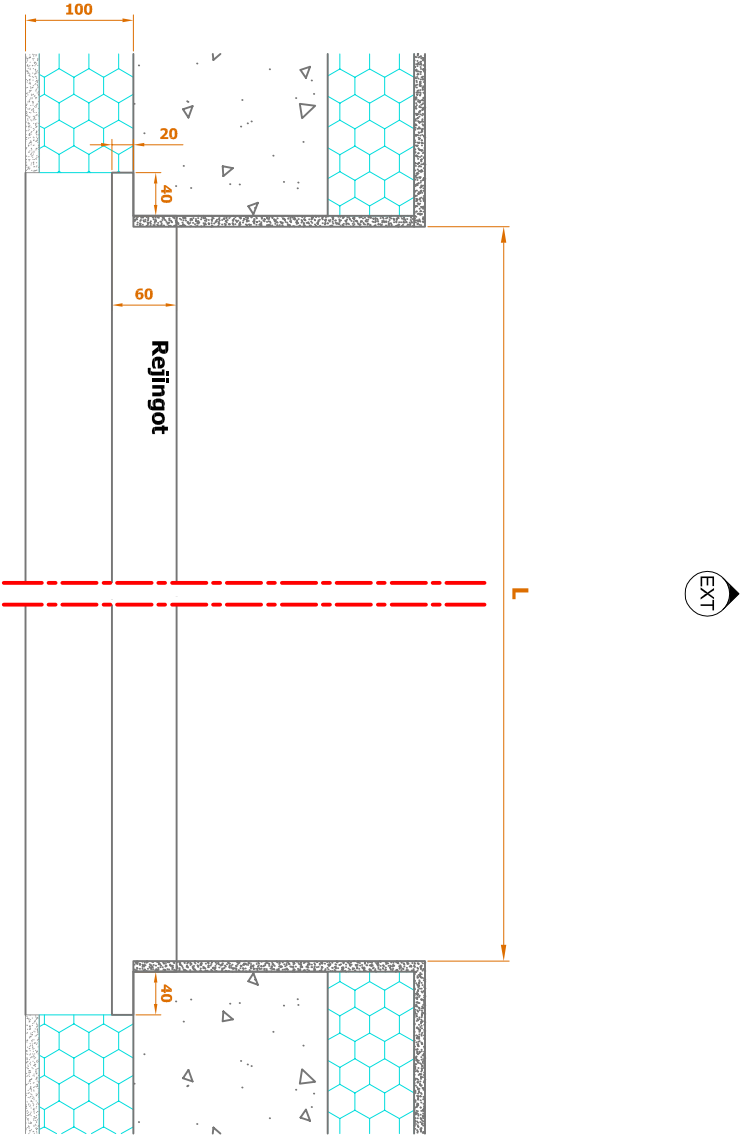



Lexique :
L : Largeur
H : Hauteur
S : Seuil
ALL : Allège
RET : Retombé de linteau
HSP : Hauteur sous Plafond
HSD : Hauteur sous Dalle
HSL : Hauteur sous Linteau
AP : Axe de Poignée
A : Entraxe
AM : Axe du Meneau
AT : Axe de la Traverse
LO : Largeur hors tout Ouvrant
HO : Largeur hors tout Ouvrant
AB : Axe de Battement d'ouvrant
PL : Passage Libre
CA : Cote Architecte

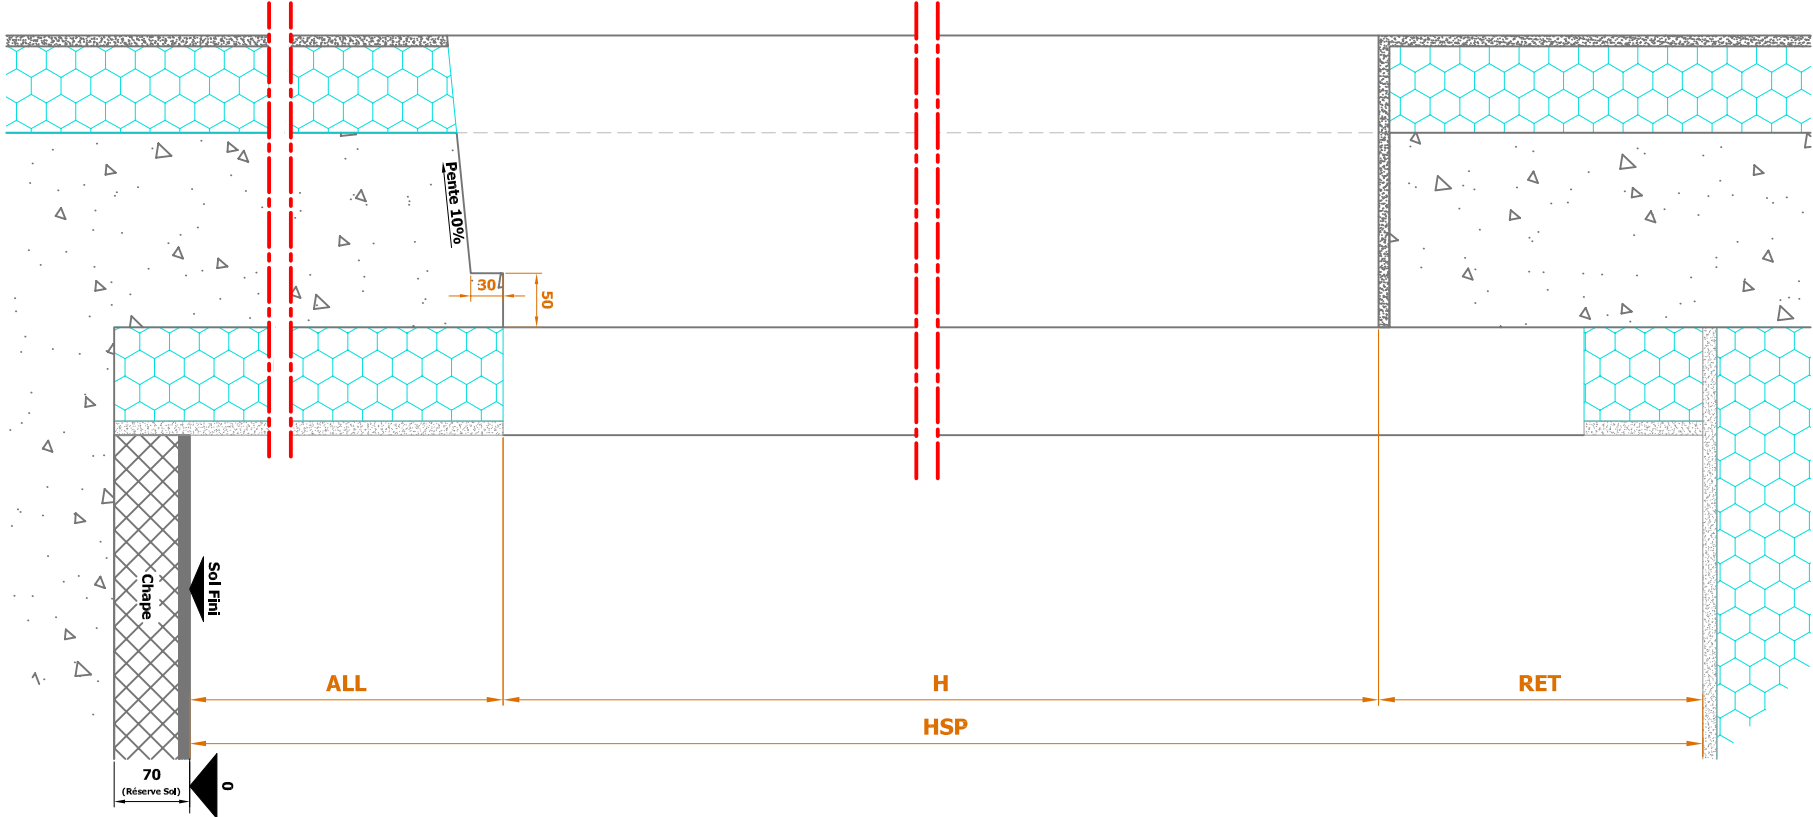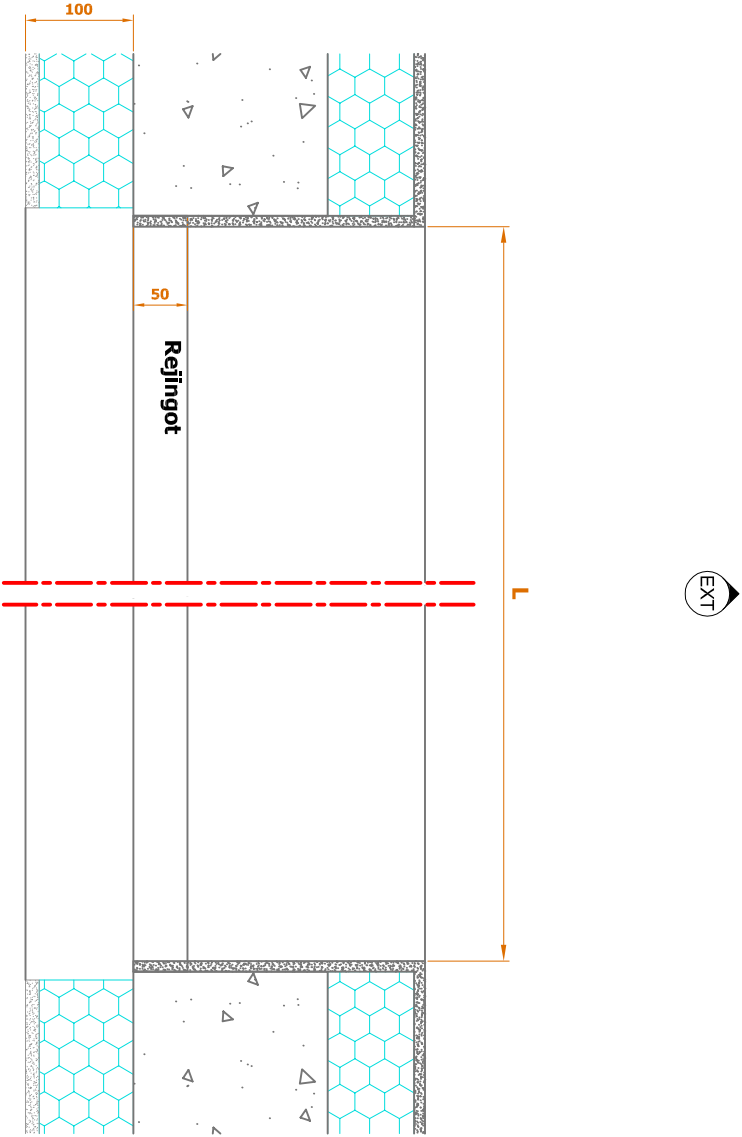



- Lexique :
- L : Largeur
 - H : Hauteur
 - S : Seuil
 - ALL : Allège
 - RET : Retombé de linteau
 - HSP : Hauteur sous Plafond
 - HSD : Hauteur Sous Dalle
 - HSL : Hauteur Sous Linteau
 - AP : Axe de Poignée
 - A : Entraxe
 - AM : Axe du Meneau
 - AT : Axe de la Traverse
 - LO : Largeur hors tout Ouvrant
 - HO : Largeur hors tout Ouvrant
 - AB : Axe de Battement d'ouvrant
 - PL : Passage Libre
 - CA : Cote Architecte

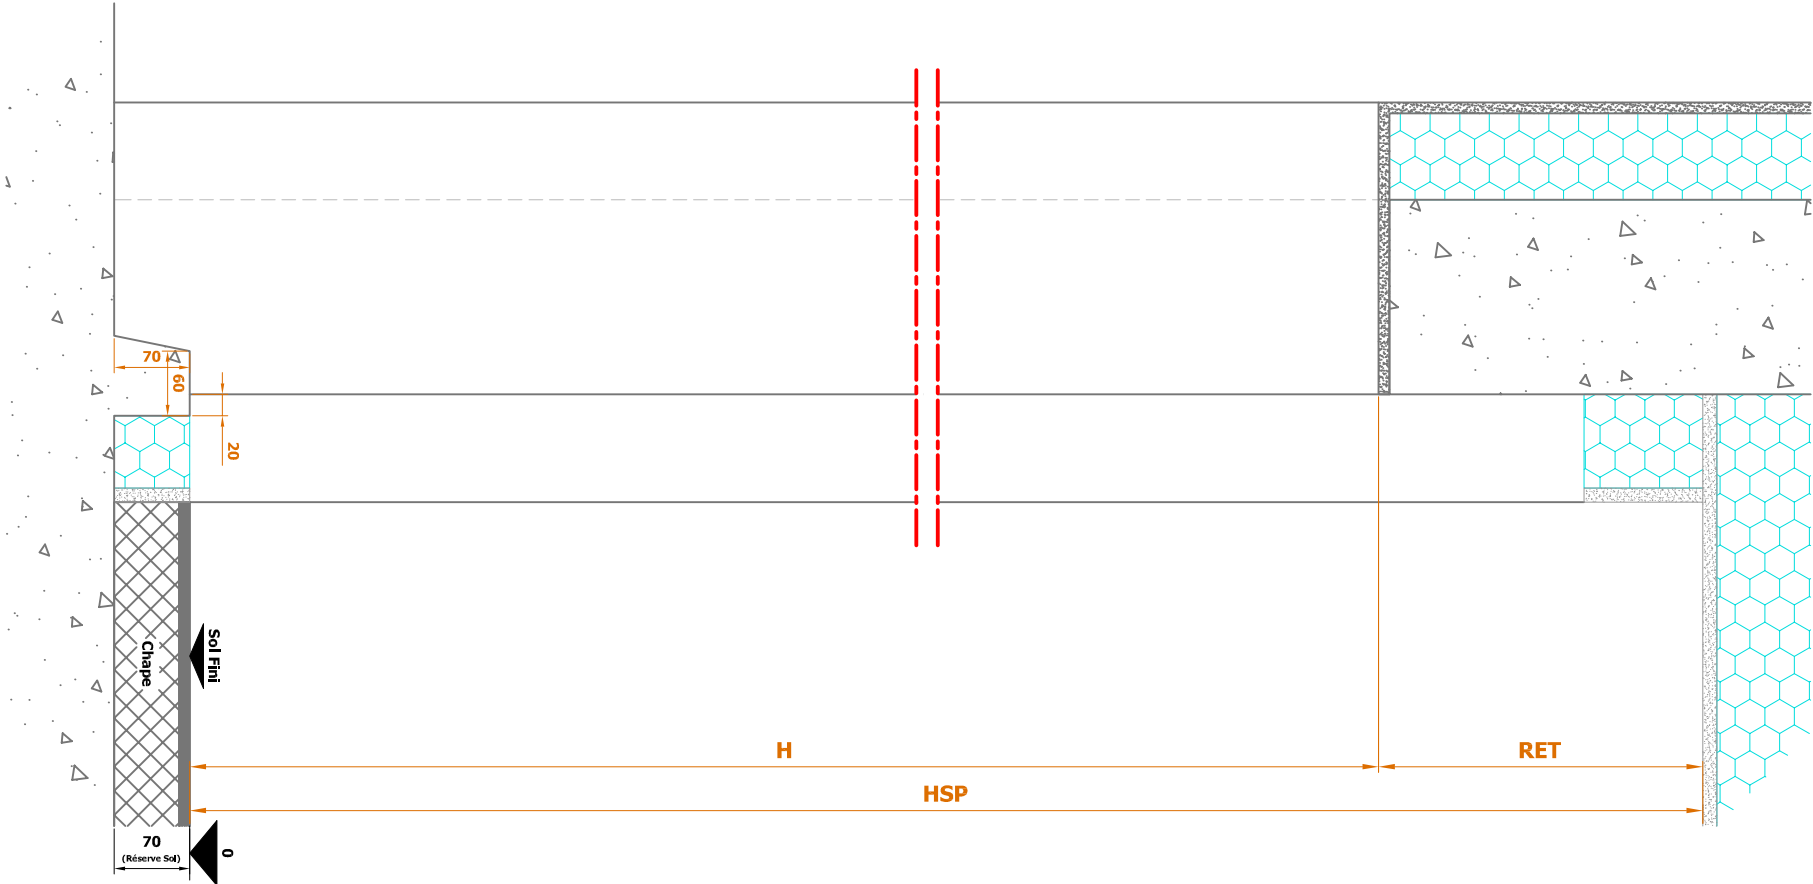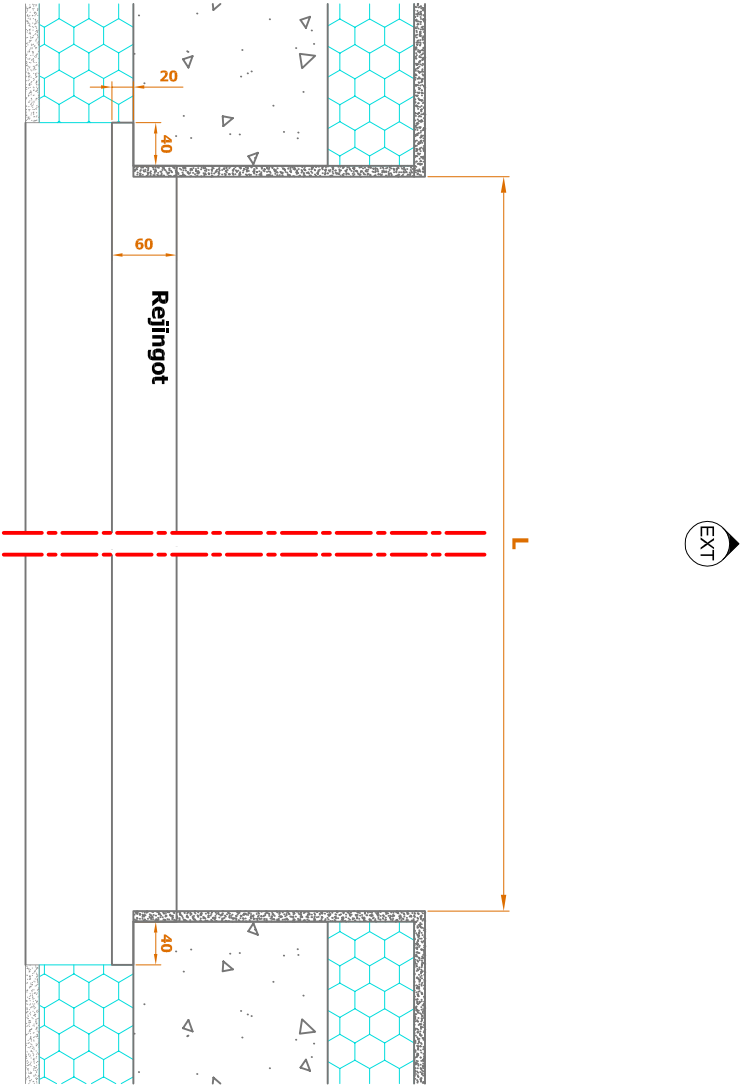



- Lexique :
- L : Largeur
 - H : Hauteur
 - S : Seuil
 - ALL : Allège
 - RET : Retombé de linteau
 - HSP : Hauteur sous Plafond
 - HSD : Hauteur Sous Dalle
 - HSL : Hauteur Sous Linteau
 - AP : Axe de Poignée
 - A : Entraxe
 - AM : Axe du Meneau
 - AT : Axe de la Traverse
 - LO : Largeur hors tout Ouvrant
 - HO : Largeur hors tout Ouvrant
 - AB : Axe de Battement d'ouvrant
 - PL : Passage Libre
 - CA : Cote Architecte

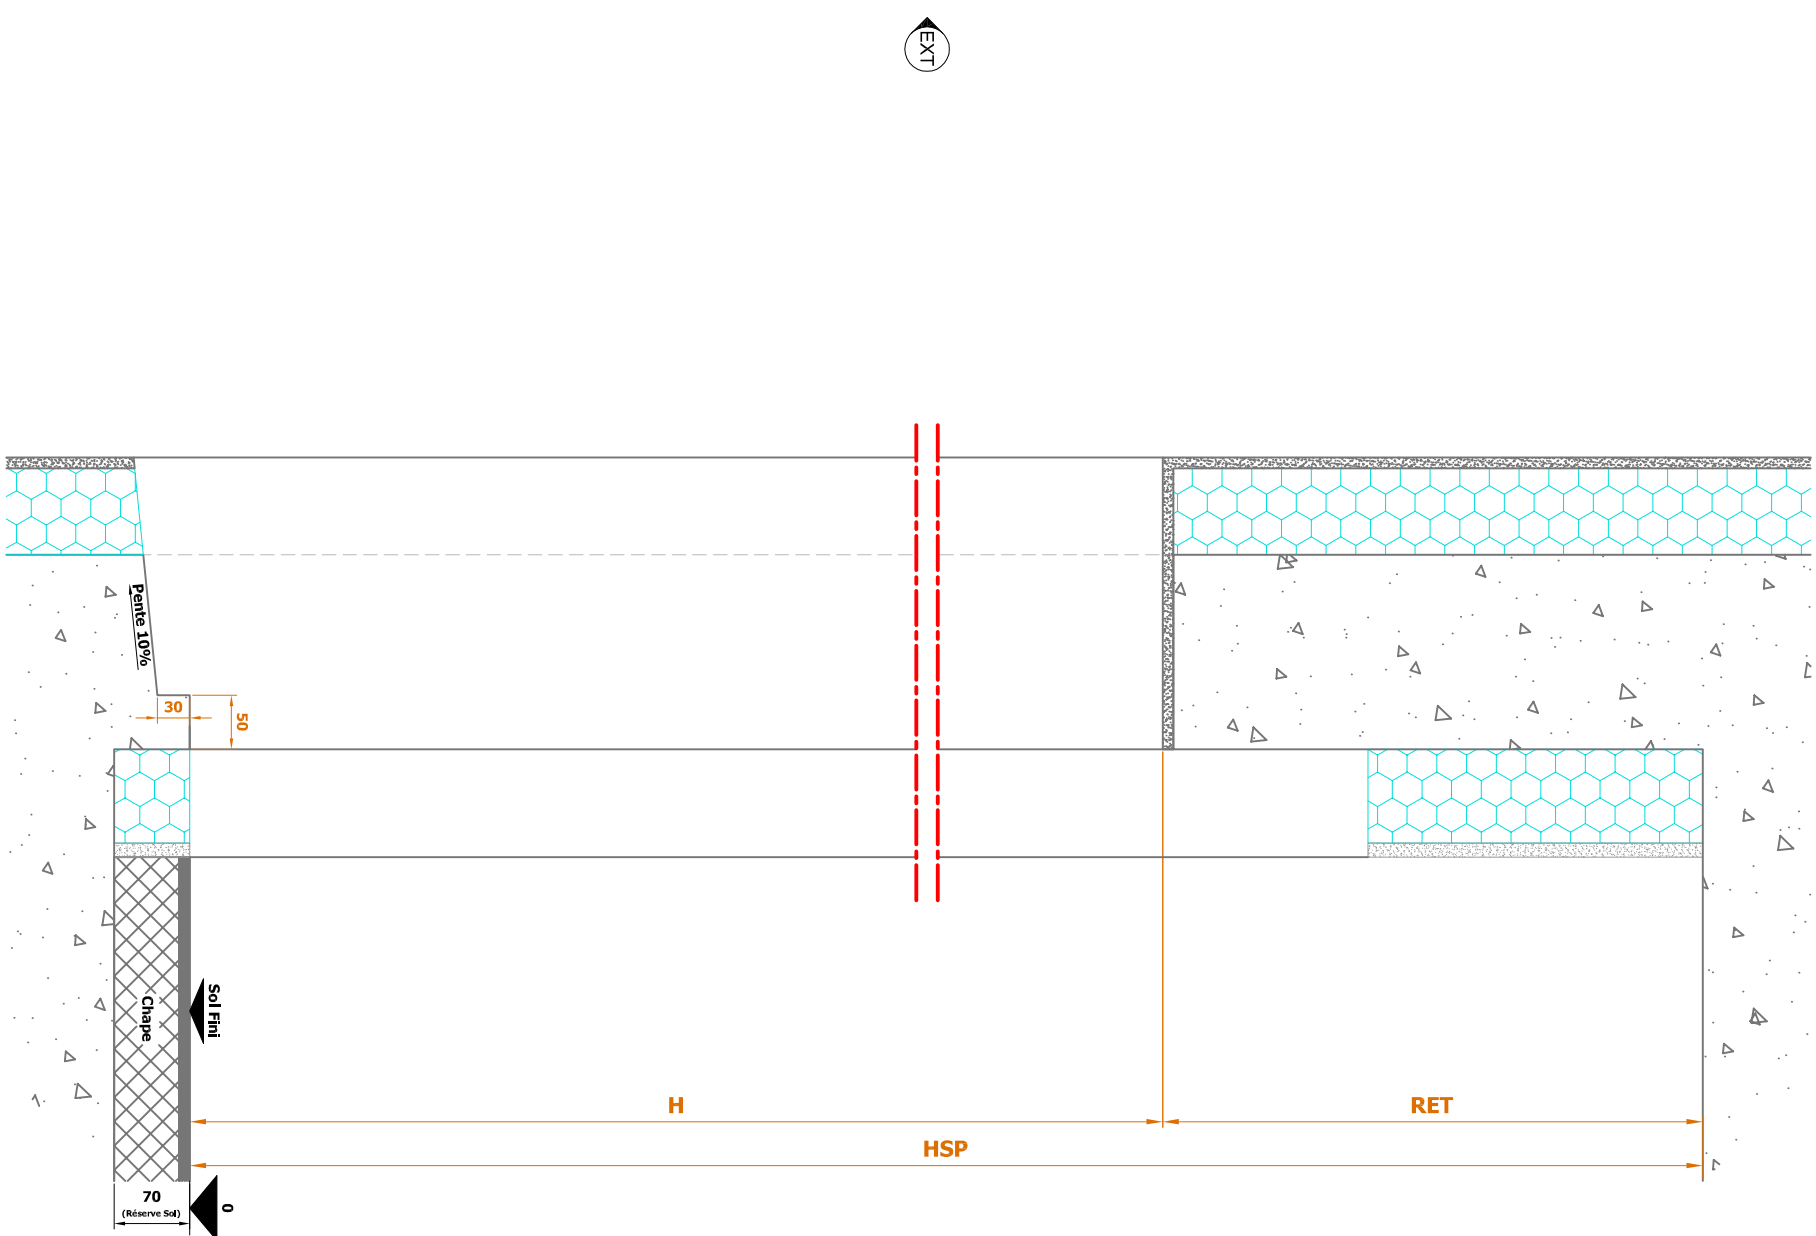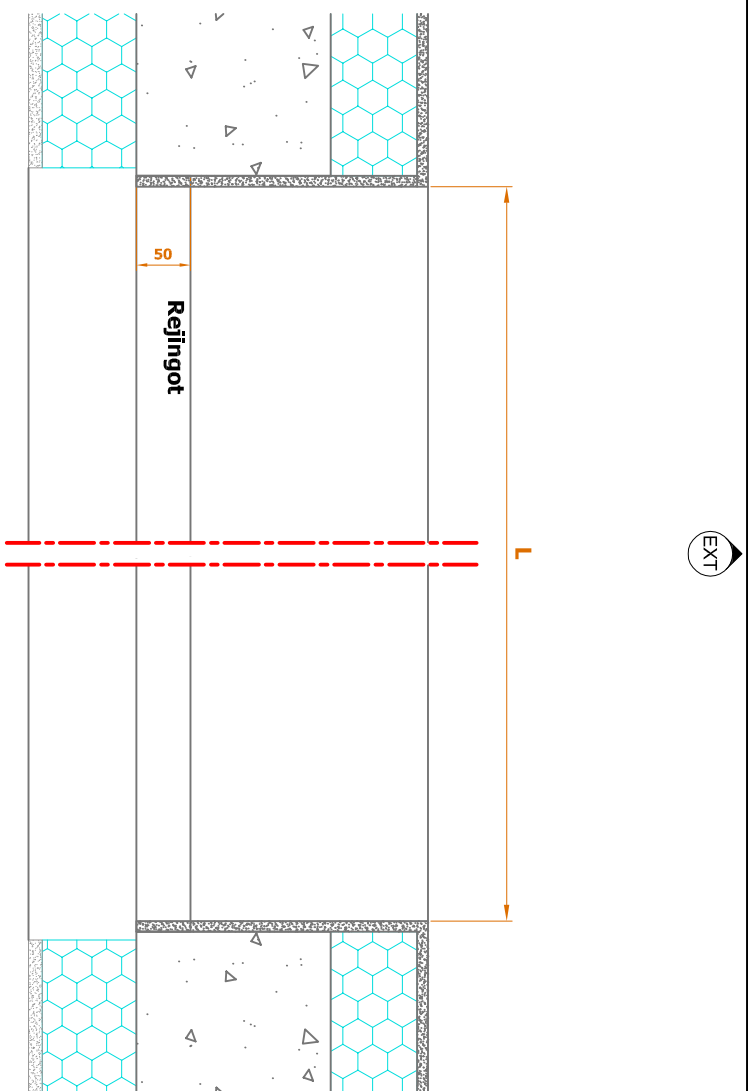



L	: Largeur
H	: Hauteur
S	: Seuil
ALL	: Allège
RET	: Retombé de linteau
HSP	: Hauteur Sous Plafond
HSD	: Hauteur Sous Dalle
HSL	: Hauteur Sous Linteau
AP	: Axe de Poinçne
A	: Entraxe
AM	: Axe du Meneau
AT	: Axe de la Traverse
NO	: Largeur hors tout Ouvrant
HO	: Largeur hors tout Ouvrant
AB	: Axe de Battement d'Ouvrant
PL	: Passage Libre
CA	: Cote Architecte

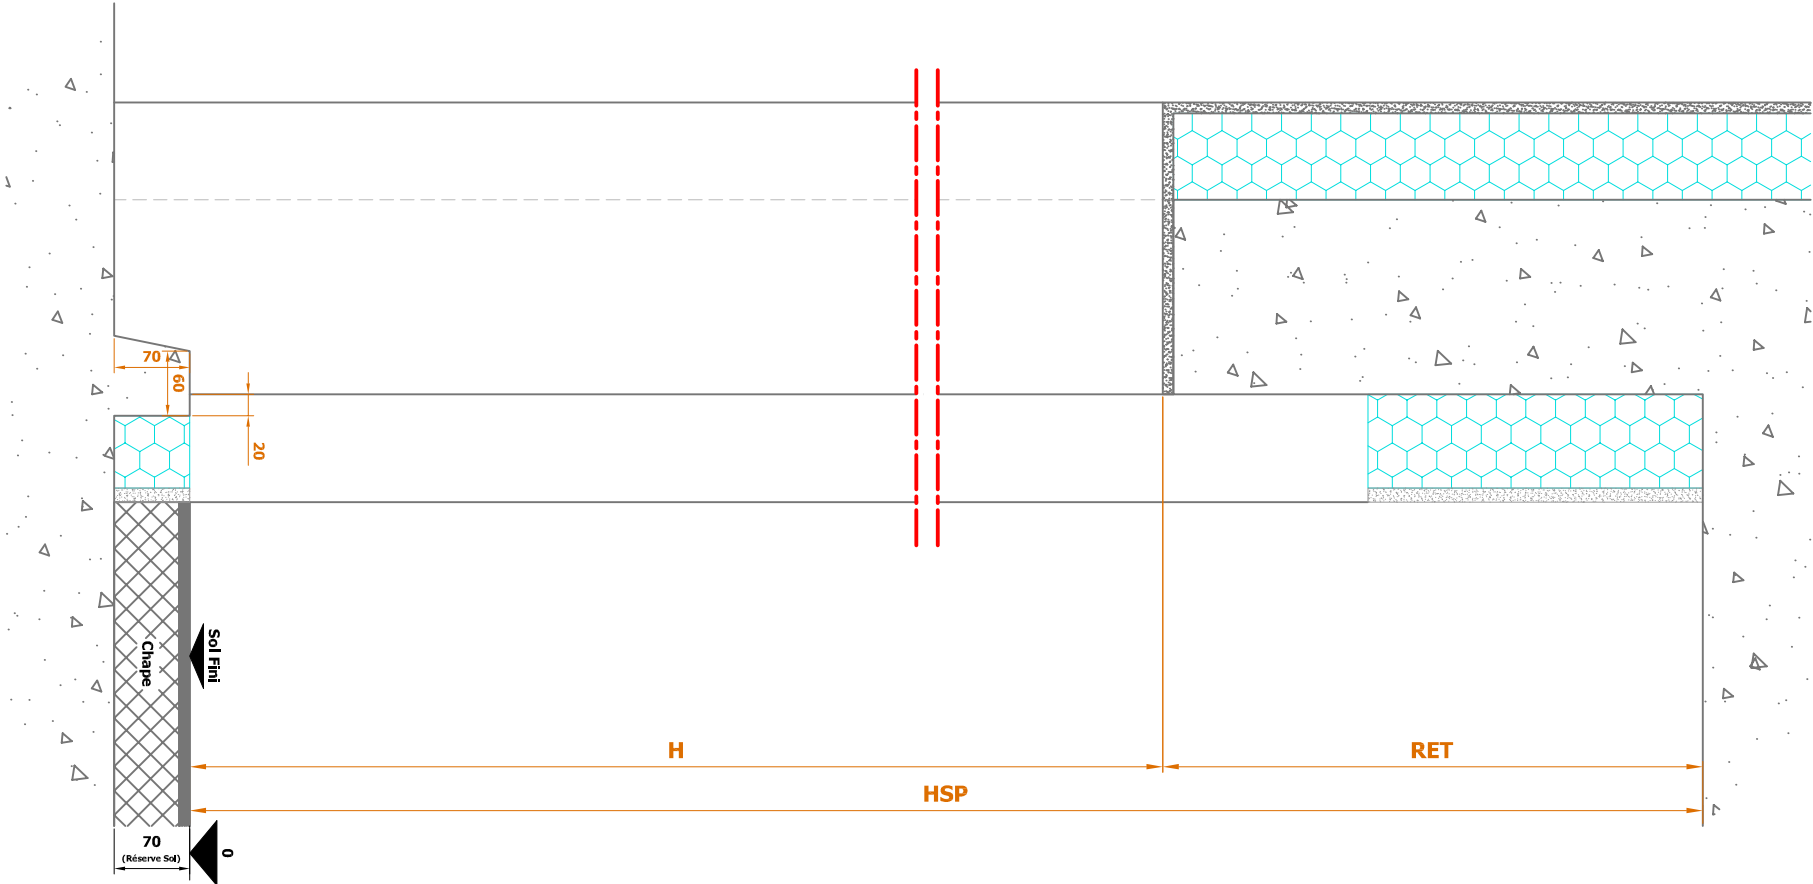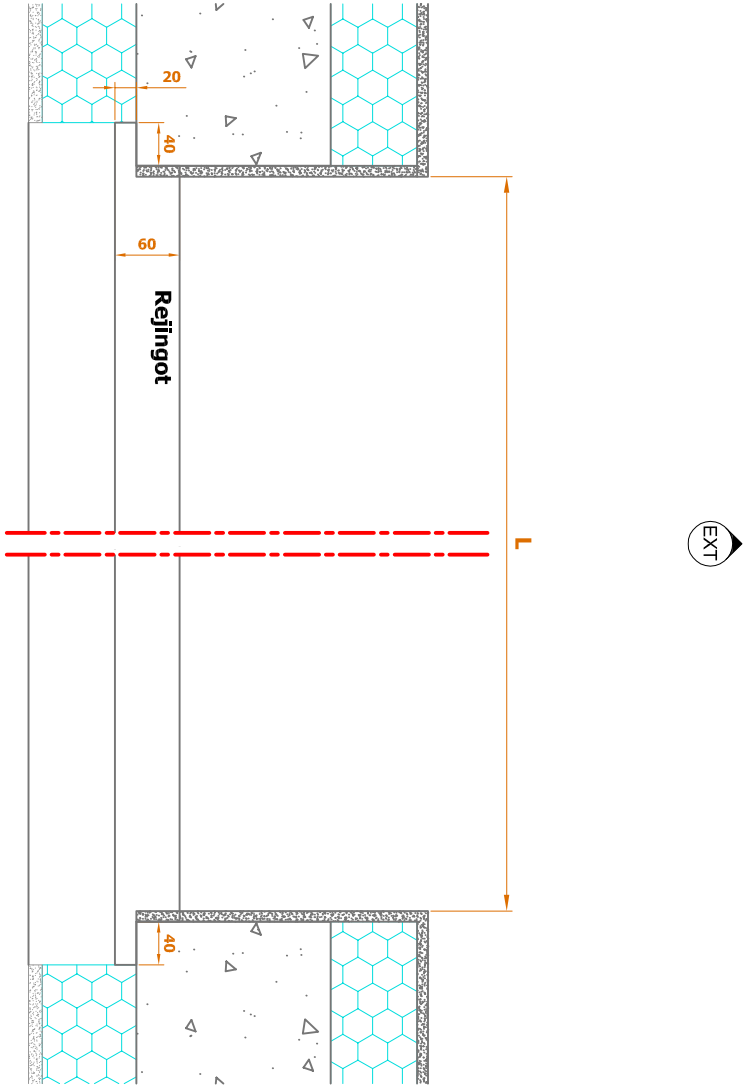



Lexique :
L : Largeur
H : Hauteur
S : Seuil
ALL : Allège
RET : Retombé de linteau
HSP : Hauteur sous Plafond
HSD : Hauteur sous Dalle
HSL : Hauteur sous Linteau
AP : Axe de Poignée
A : Entraxe
AM : Axe du Meneau
AT : Axe de la Traverse
LO : Largeur hors tout Ouvrant
HO : Largeur hors tout Ouvrant
AB : Axe de Battement d'ouvrant
PL : Passage Libre
CA : Cote Architecte

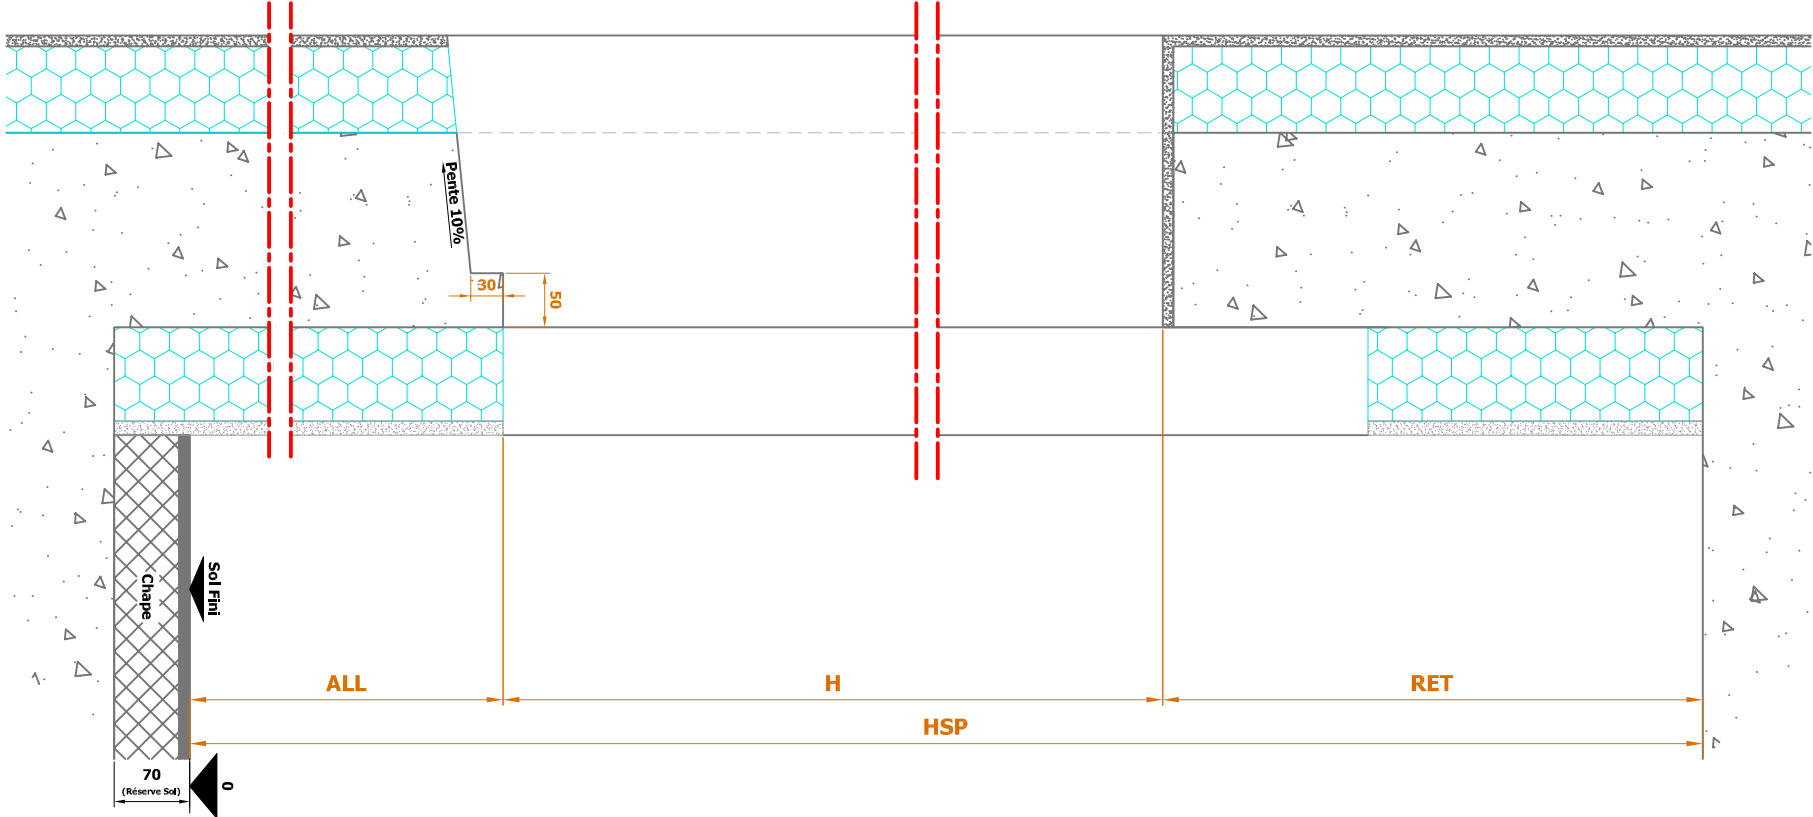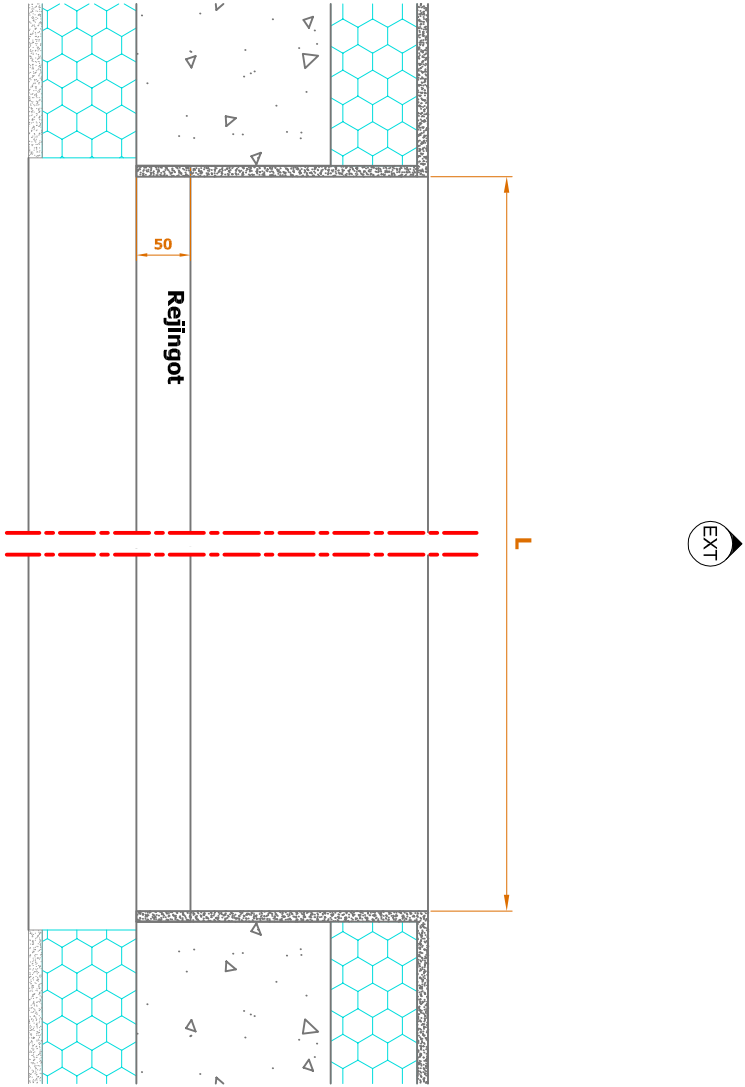



Lexique :
L : Largeur
H : Hauteur
S : Seuil
ALL : Allège
RET : Retombé de linteau
HSP : Hauteur sous Plafond
HSD : Hauteur sous Dalle
HSL : Hauteur sous Linteau
AP : Axe de Poignée
A : Entraxe
AM : Axe du Meneau
AT : Axe de la Traverse
LO : Largeur hors tout Ouvrant
HO : Hauteur hors tout Ouvrant
AB : Axe de Battement d'ouvrant
PL : Passage Libre
CA : Cote Architecte

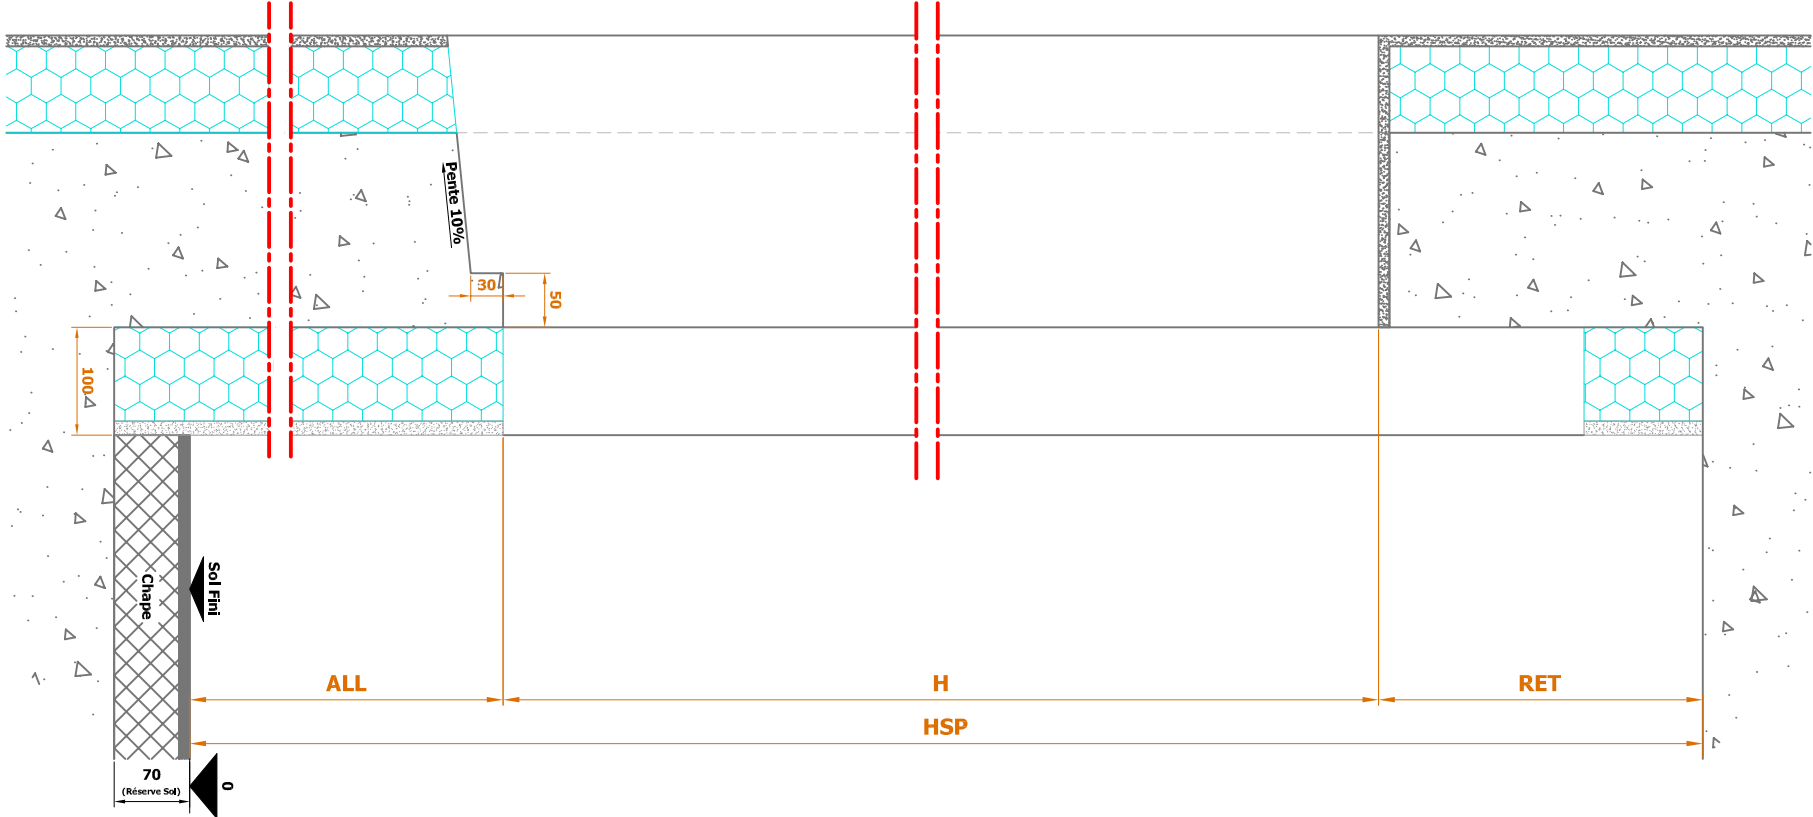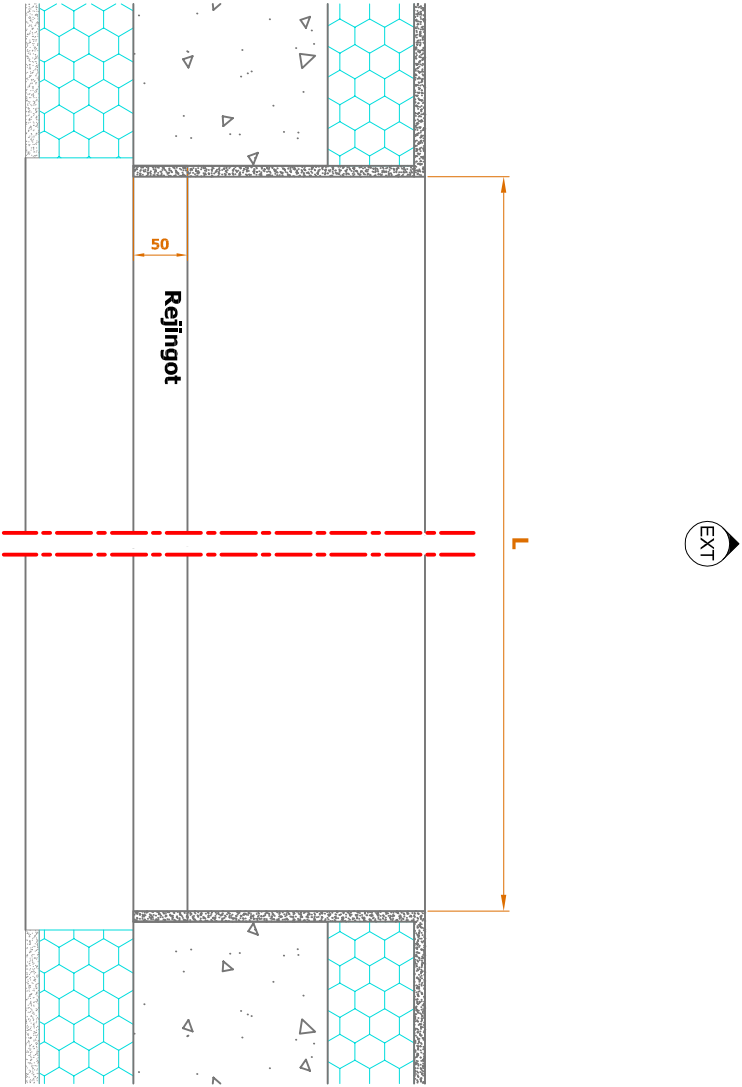


- Lexique :
- L : Largeur
 - H : Hauteur
 - S : Seuil
 - ALL : Allège
 - RET : Retombé de linteau
 - HSP : Hauteur sous Plafond
 - HSD : Hauteur sous Dalle
 - HSL : Hauteur sous Linteau
 - AP : Axe de Poignée
 - A : Entraxe
 - AM : Axe du Meneau
 - AT : Axe de la Traverse
 - LO : Largeur hors tout Ouvrant
 - HO : Largeur hors tout Ouvrant
 - AB : Axe de Battement d'ouvrant
 - PL : Passage Libre
 - CA : Cote Architecte

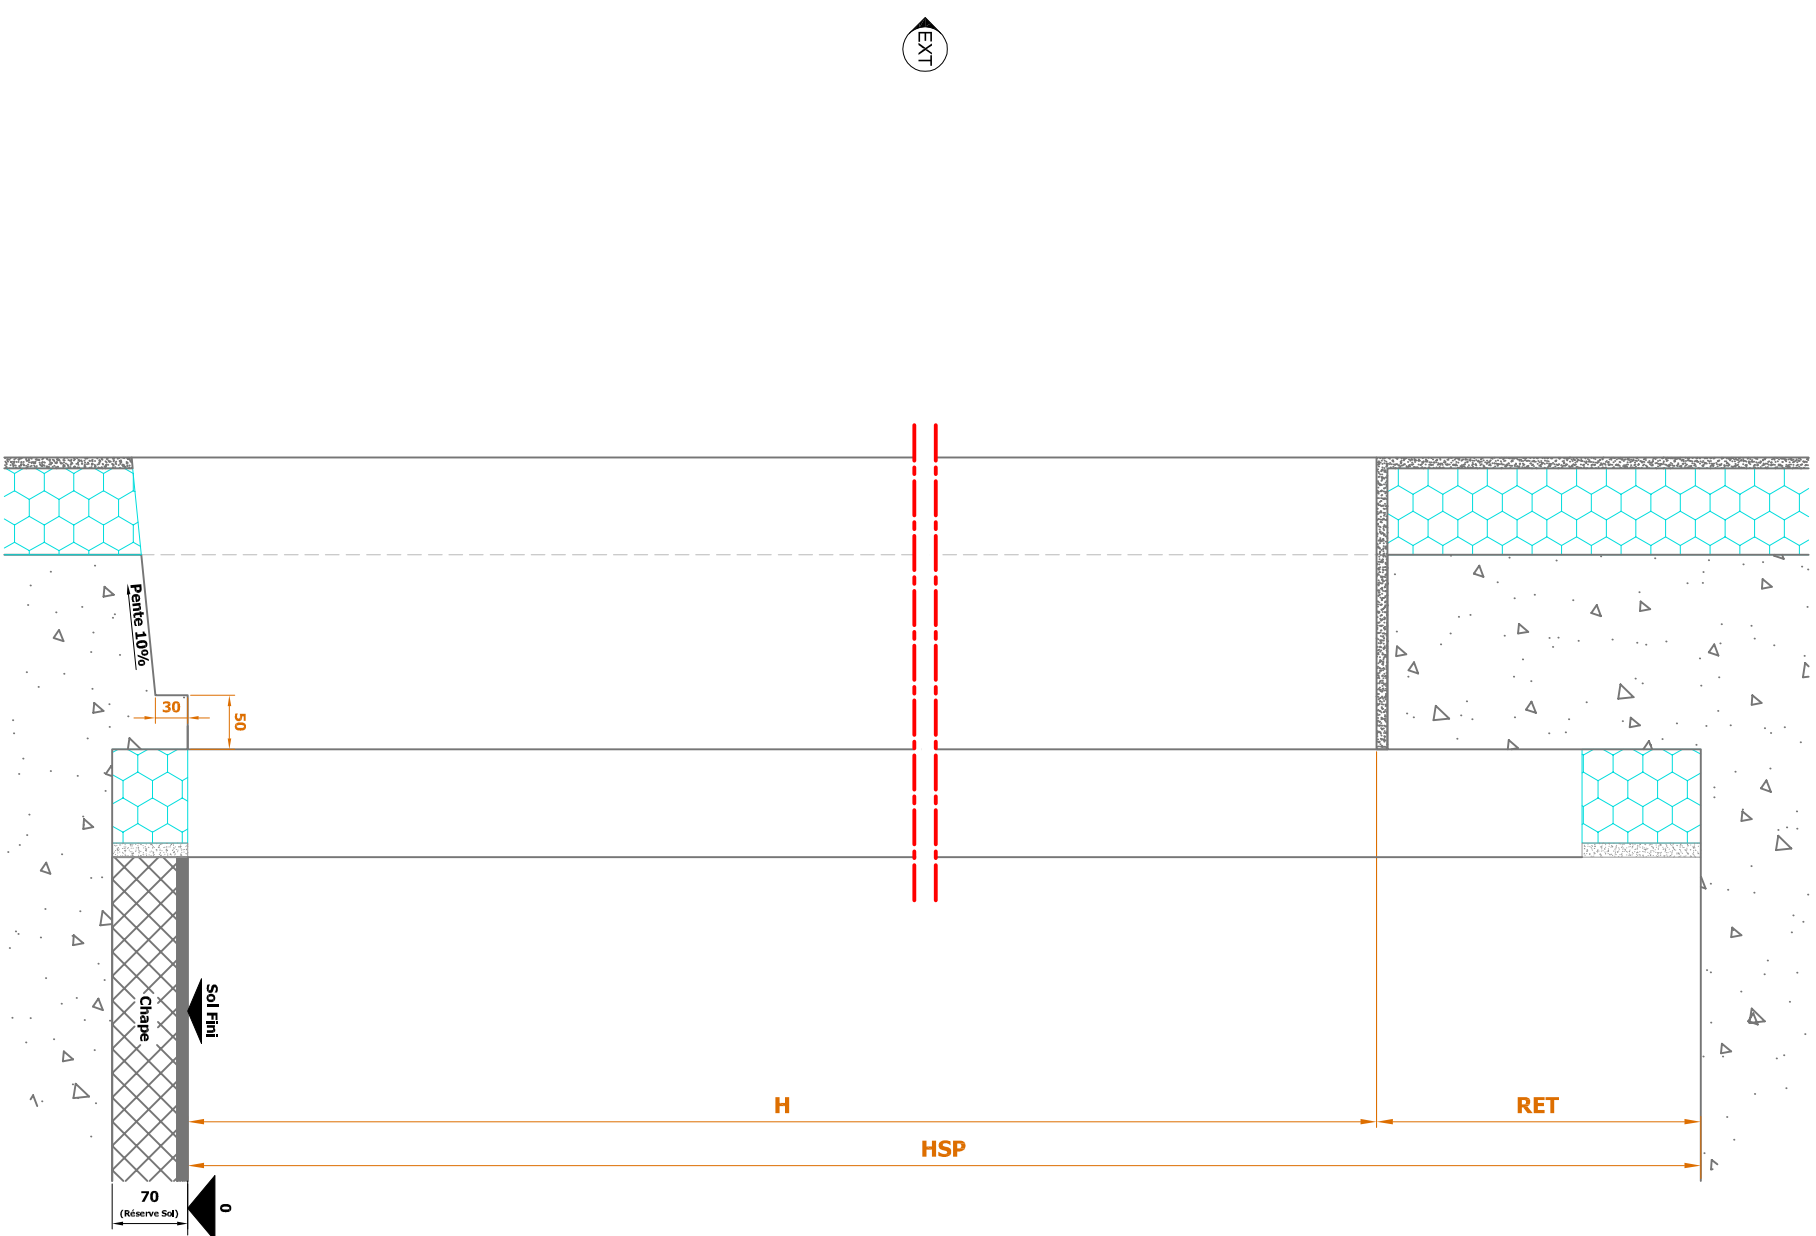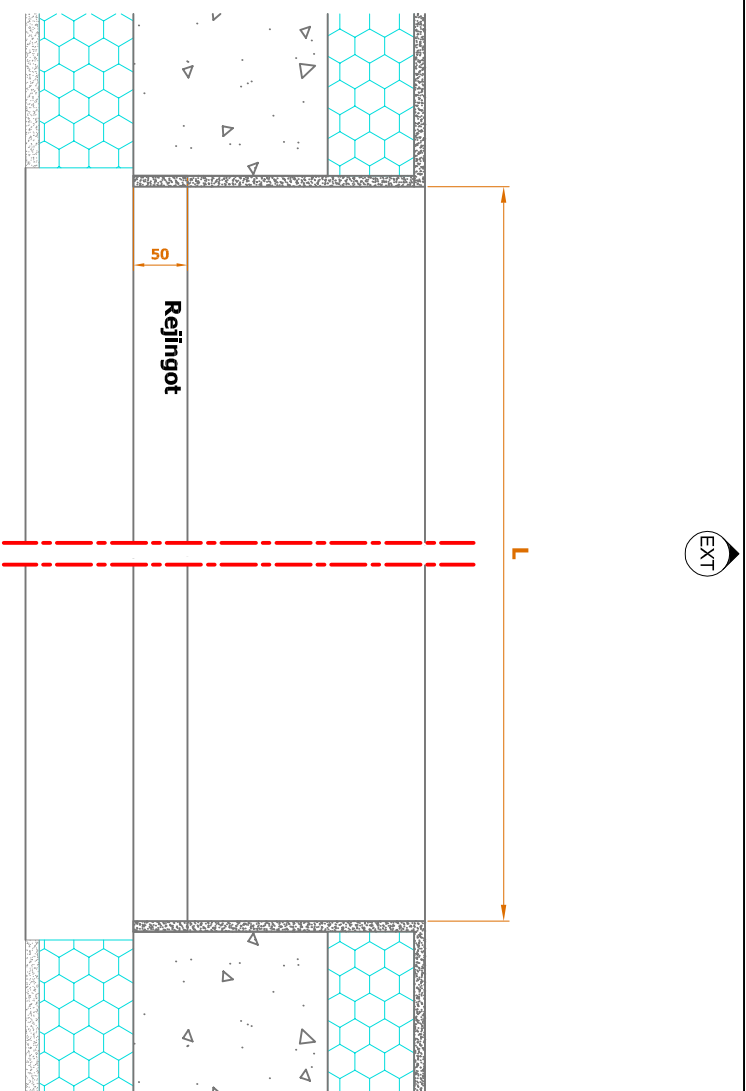

L	Lexique :
L	: Largeur
H	: Hauteur
S	: Seuil
ALL	: Allège
RET	: Retourbé de linteau
HSP	: Hauteur Sous Plafond
HSD	: Hauteur Sous Dalle
HSL	: Hauteur Sous Linteau
A	: Axe de Poignée
A	: Entraxe
AM	: Axe du Meneau
AT	: Axe de la Traverse
LO	: Largeur hors tout Ouvrant
HO	: Largeur hors tout Ouvrant
AB	: Axe de Battement d'Ouvrant
PL	: Passage Libre
CA	: Cote Architecte

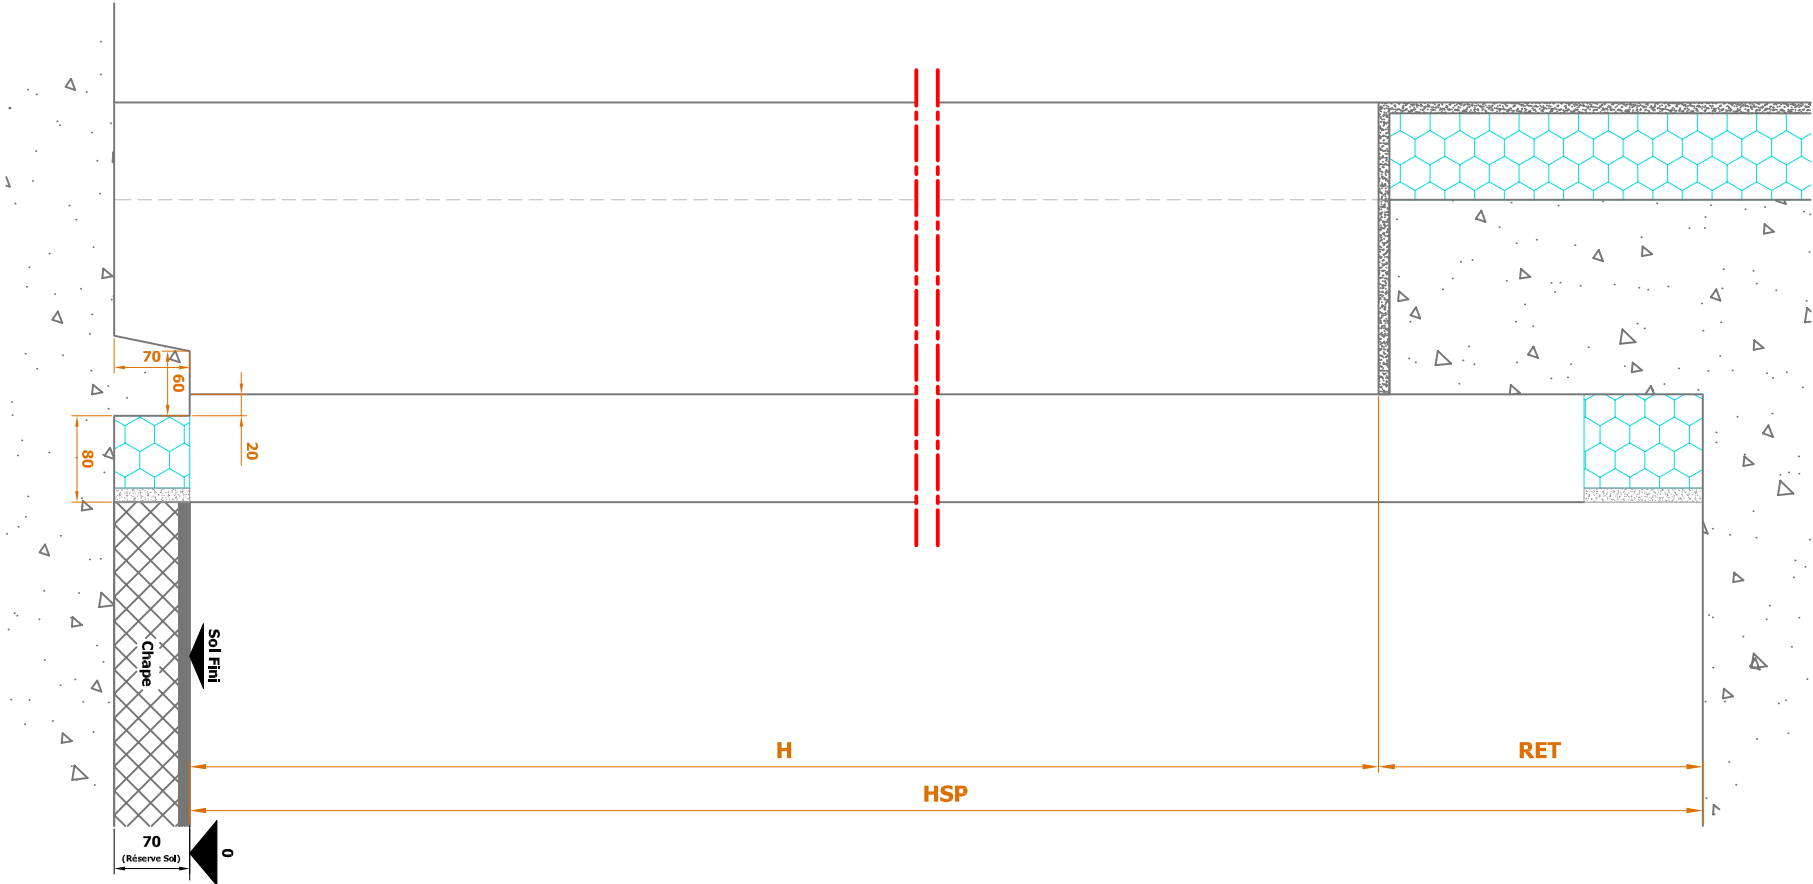
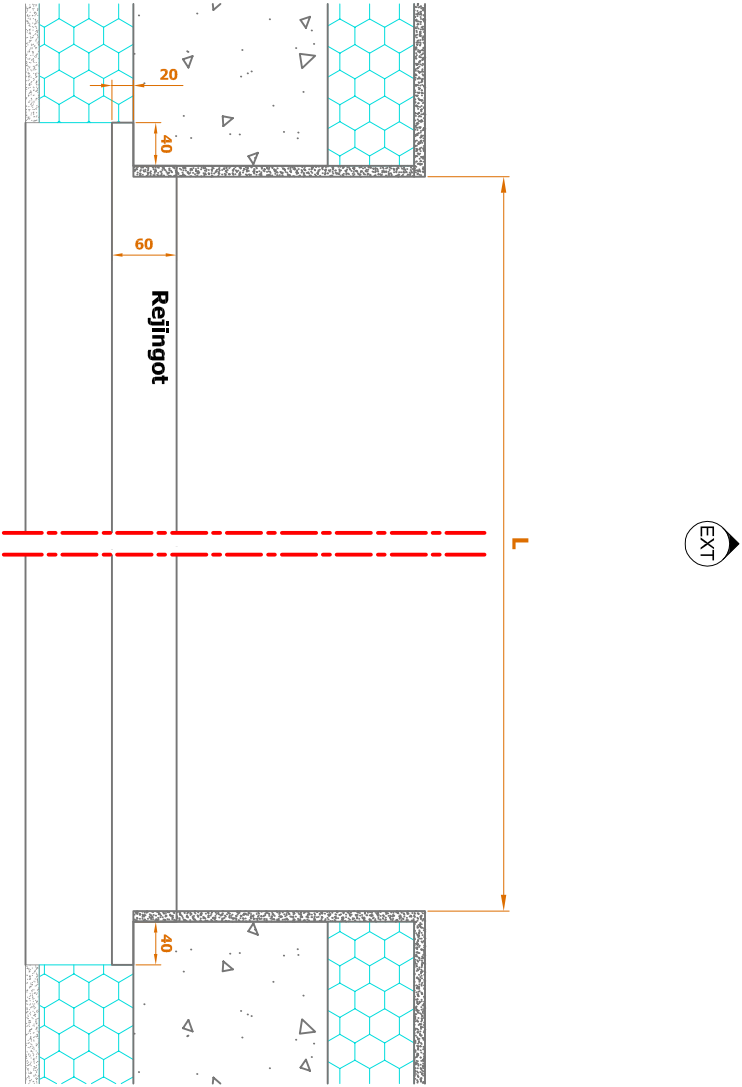


Lexique :
L : Largeur
H : Hauteur
S : Seuil
ALL : Allège
RET : Retombé de linteau
HSP : Hauteur sous Plafond
HSD : Hauteur sous Dalle
HSL : Hauteur sous Linteau
AP : Axe de Poignée
A : Entraxe
AM : Axe du Meneau
AT : Axe de la Traverse
LO : Largeur hors tout Ouvrant
HO : Largeur hors tout Ouvrant
AB : Axe de Battement d'ouvrant
PL : Passage Libre
CA : Cote Architecte

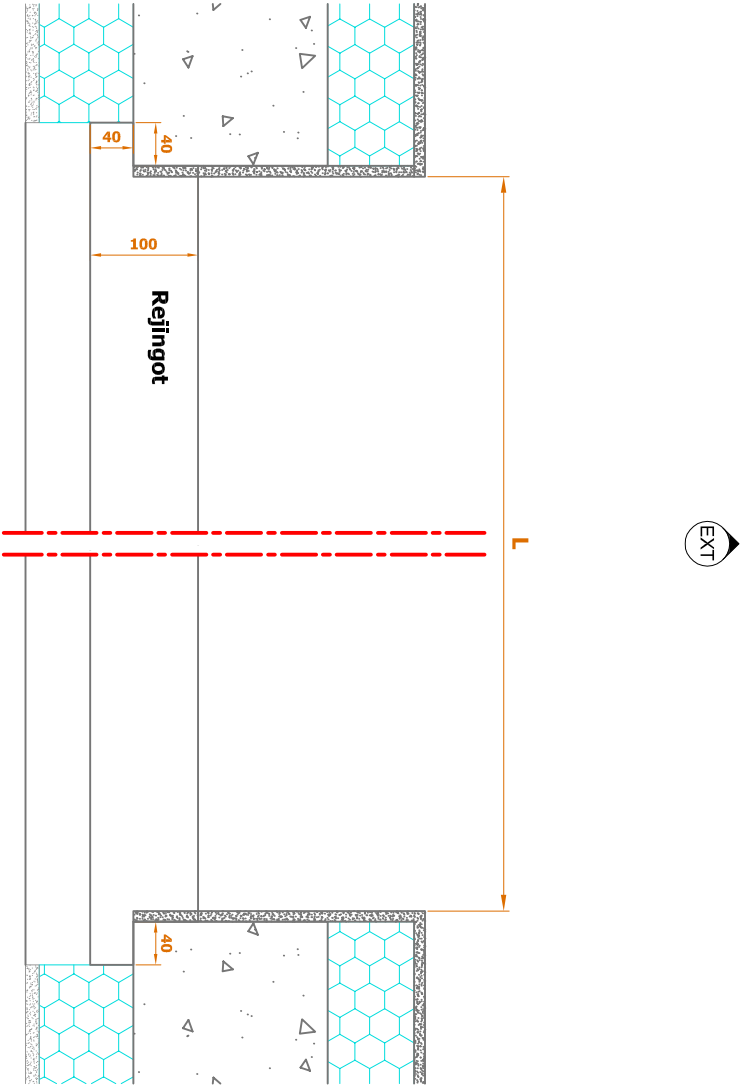


Lexique :
L : Largeur
H : Hauteur
S : Seuil
ALL : Allège
RET : Retombé de linteau
HSP : Hauteur sous Plafond
HSD : Hauteur Sous Dalle
HSL : Hauteur Sous Linteau
AP : Axe de Poignée
A : Entraxe
AM : Axe du Meneau
AT : Axe de la Traverse
LO : Largeur hors tout Ouvrant
HO : Largeur hors tout Ouvrant
AB : Axe de Battement d'ouvrant
PL : Passage Libre
CA : Cote Architecte





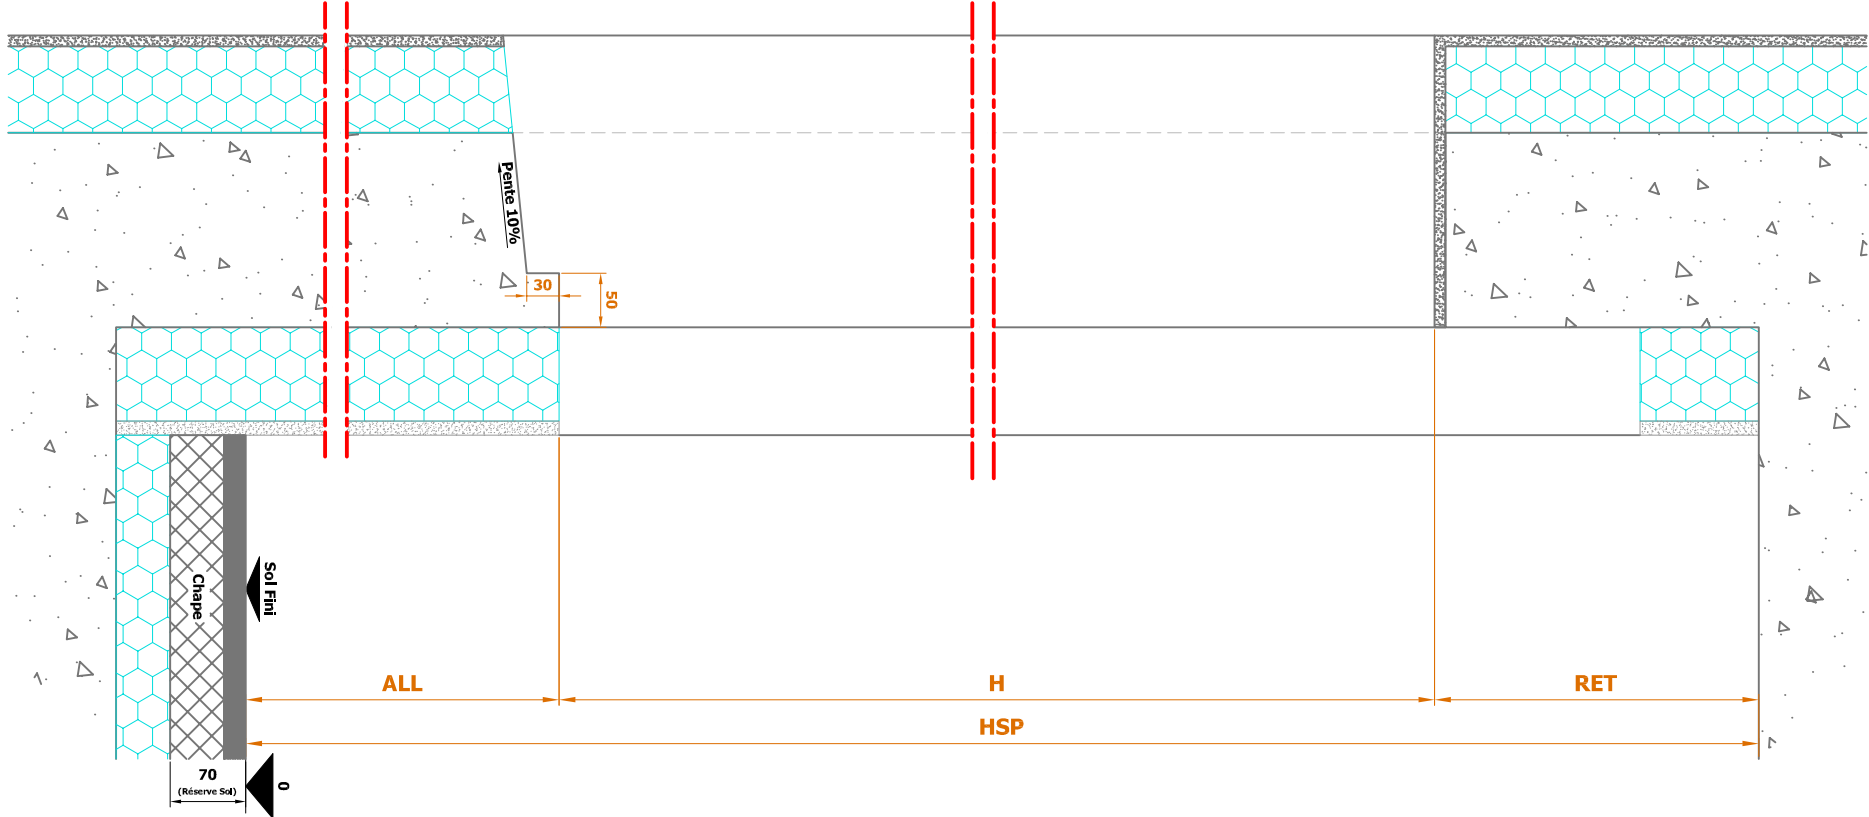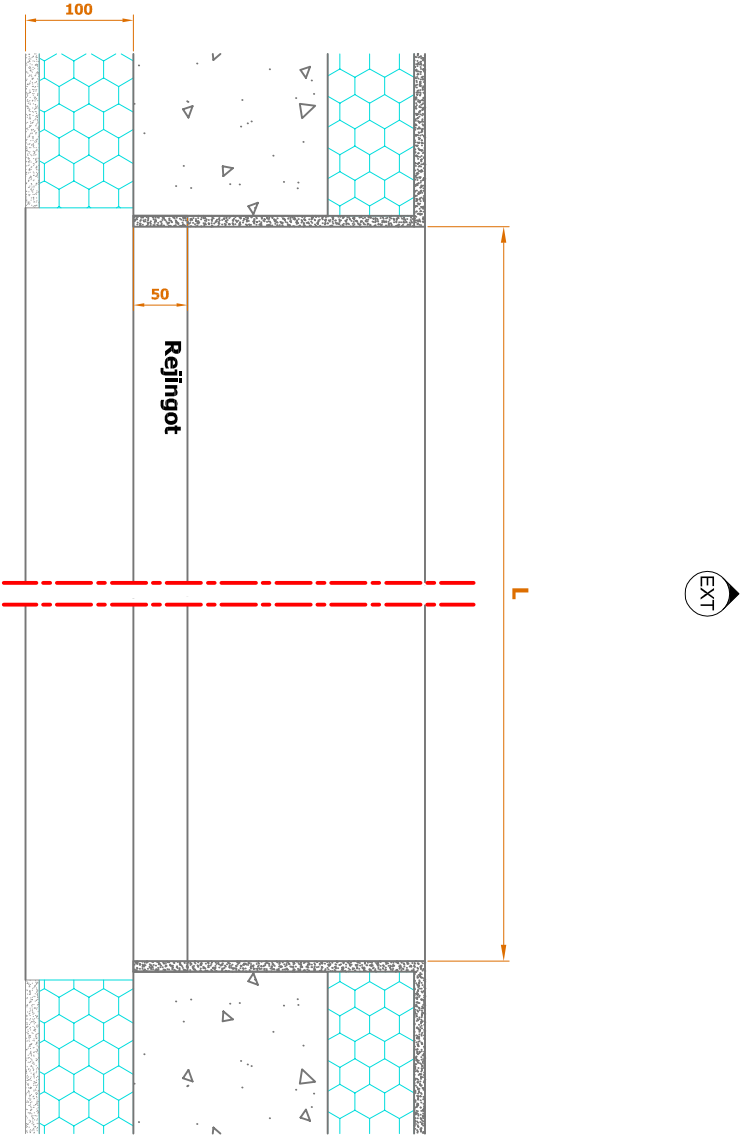



- Lexique :
- L : Largeur
 - H : Hauteur
 - S : Seuil
 - ALL : Allège
 - RET : Retombé de linteau
 - HSP : Hauteur sous Plafond
 - HSD : Hauteur Sous Dalle
 - HSL : Hauteur Sous Linteau
 - AP : Axe de Poignée
 - A : Entraxe
 - AM : Axe du Meneau
 - AT : Axe de la Traverse
 - LO : Largeur hors tout Ouvrant
 - HO : Largeur hors tout Ouvrant
 - AB : Axe de Battement d'ouvrant
 - PL : Passage Libre
 - CA : Cote Architecte

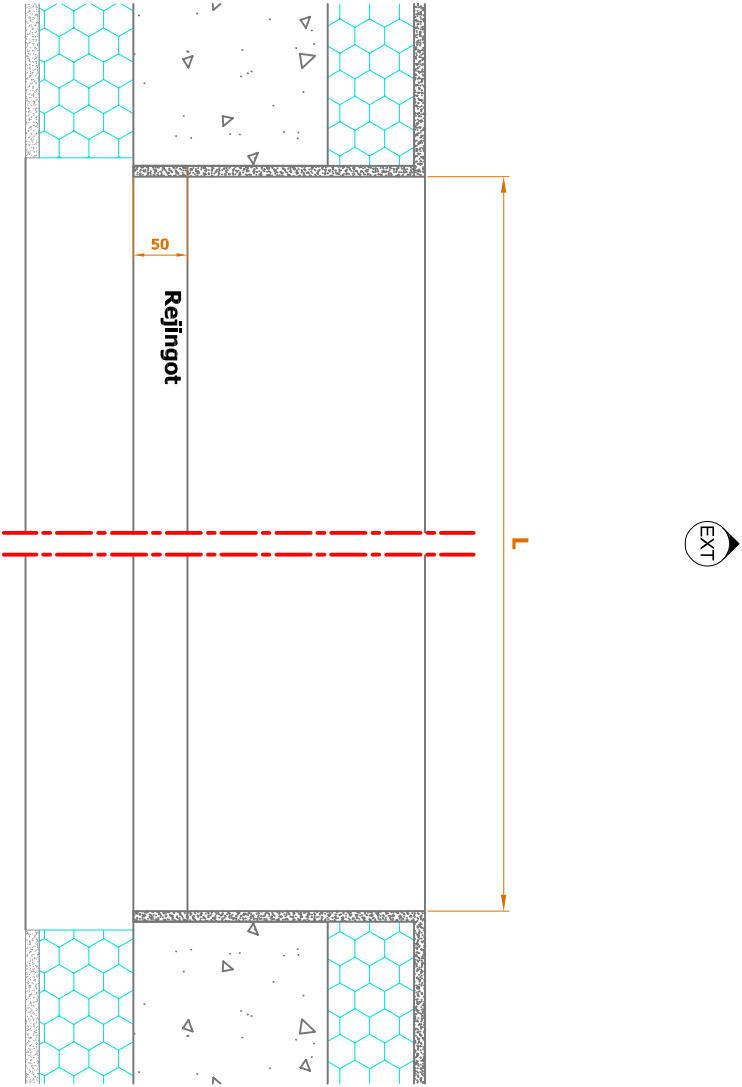



- Lexique :
- L : Largeur
 - H : Hauteur
 - S : Seuil
 - ALL : Allège
 - RET : Retombé de linteau
 - HSP : Hauteur Sous Plafond
 - HSD : Hauteur Sous Dalle
 - HSL : Hauteur Sous Linteau
 - AP : Axe de Poignée
 - A : Entraxe
 - AM : Axe du Meneau
 - AT : Axe de la Traverse
 - LO : Largeur hors tout Ouvrant
 - HO : Largeur hors tout Ouvrant
 - AB : Axe de Battement d'ouvrant
 - PL : Passage Libre
 - CA : Cote Architecte

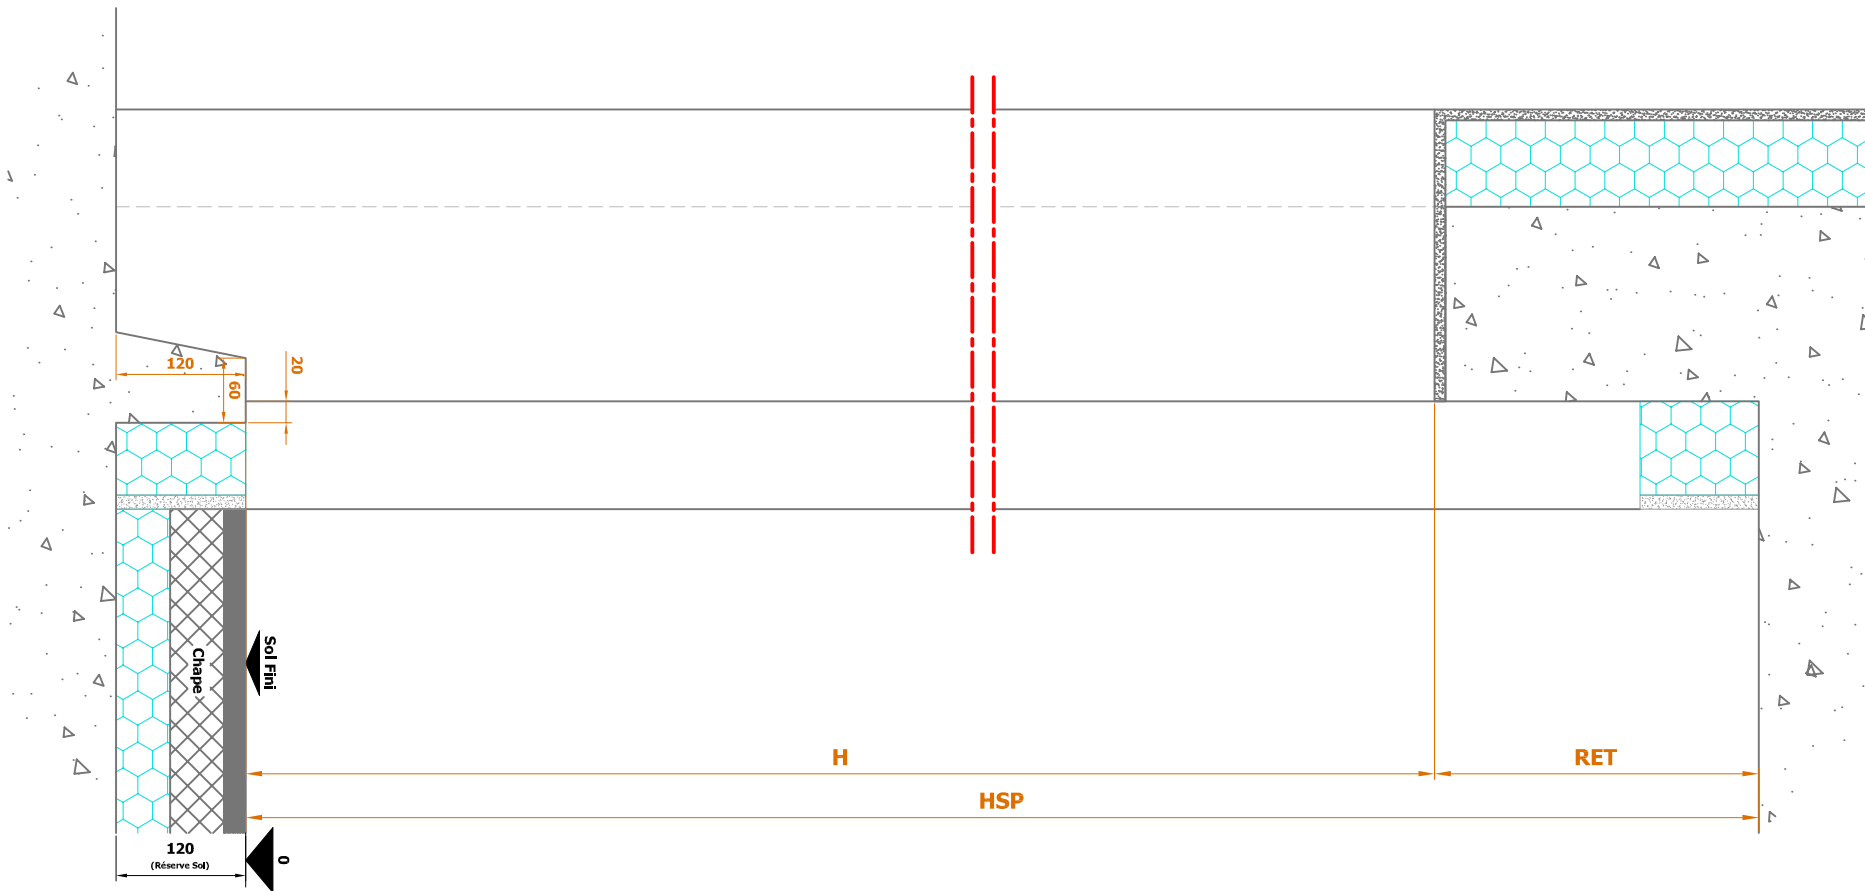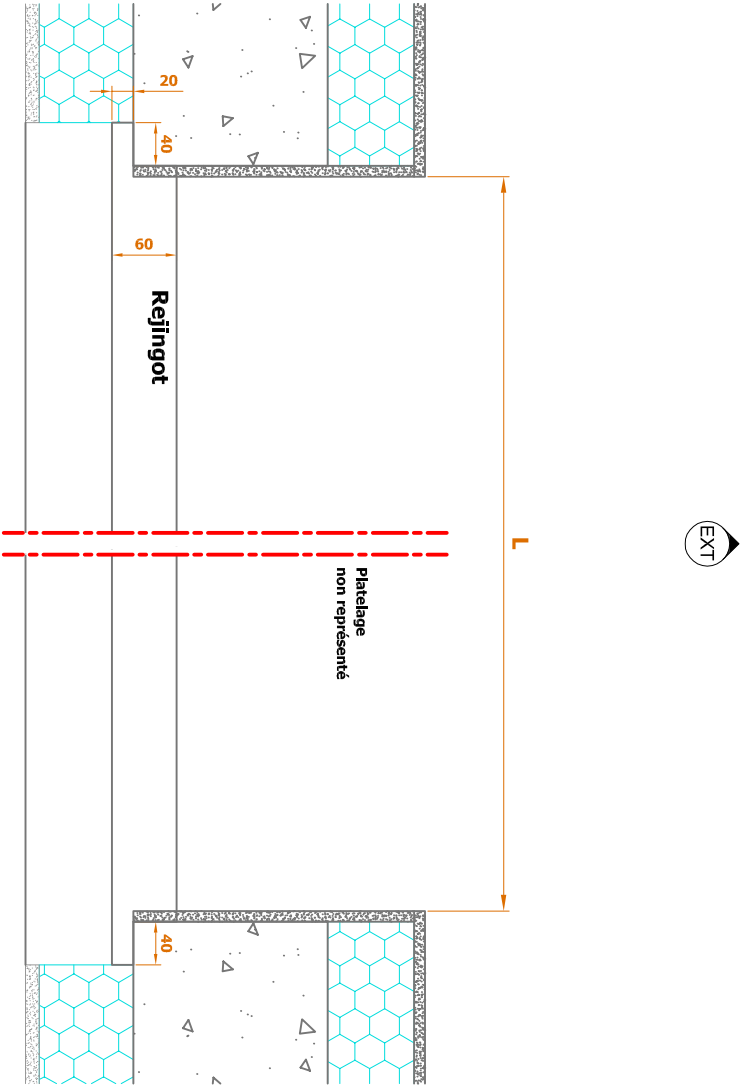

- Lexique :
- L : Largeur
 - H : Hauteur
 - S : Seuil
 - ALL : Allège
 - RET : Retombé de linteau
 - HSP : Hauteur Sous Plafond
 - HSD : Hauteur Sous Dalle
 - HSL : Hauteur Sous Linteau
 - AP : Axe de Poignée
 - A : Entraxe
 - AM : Axe du Meneau
 - AT : Axe de la Traverse
 - LO : Largeur hors tout Ouvrant
 - HO : Largeur hors tout Ouvrant
 - AB : Axe de Battement d'ouvrant
 - PL : Passage Libre
 - CA : Cote Architecte

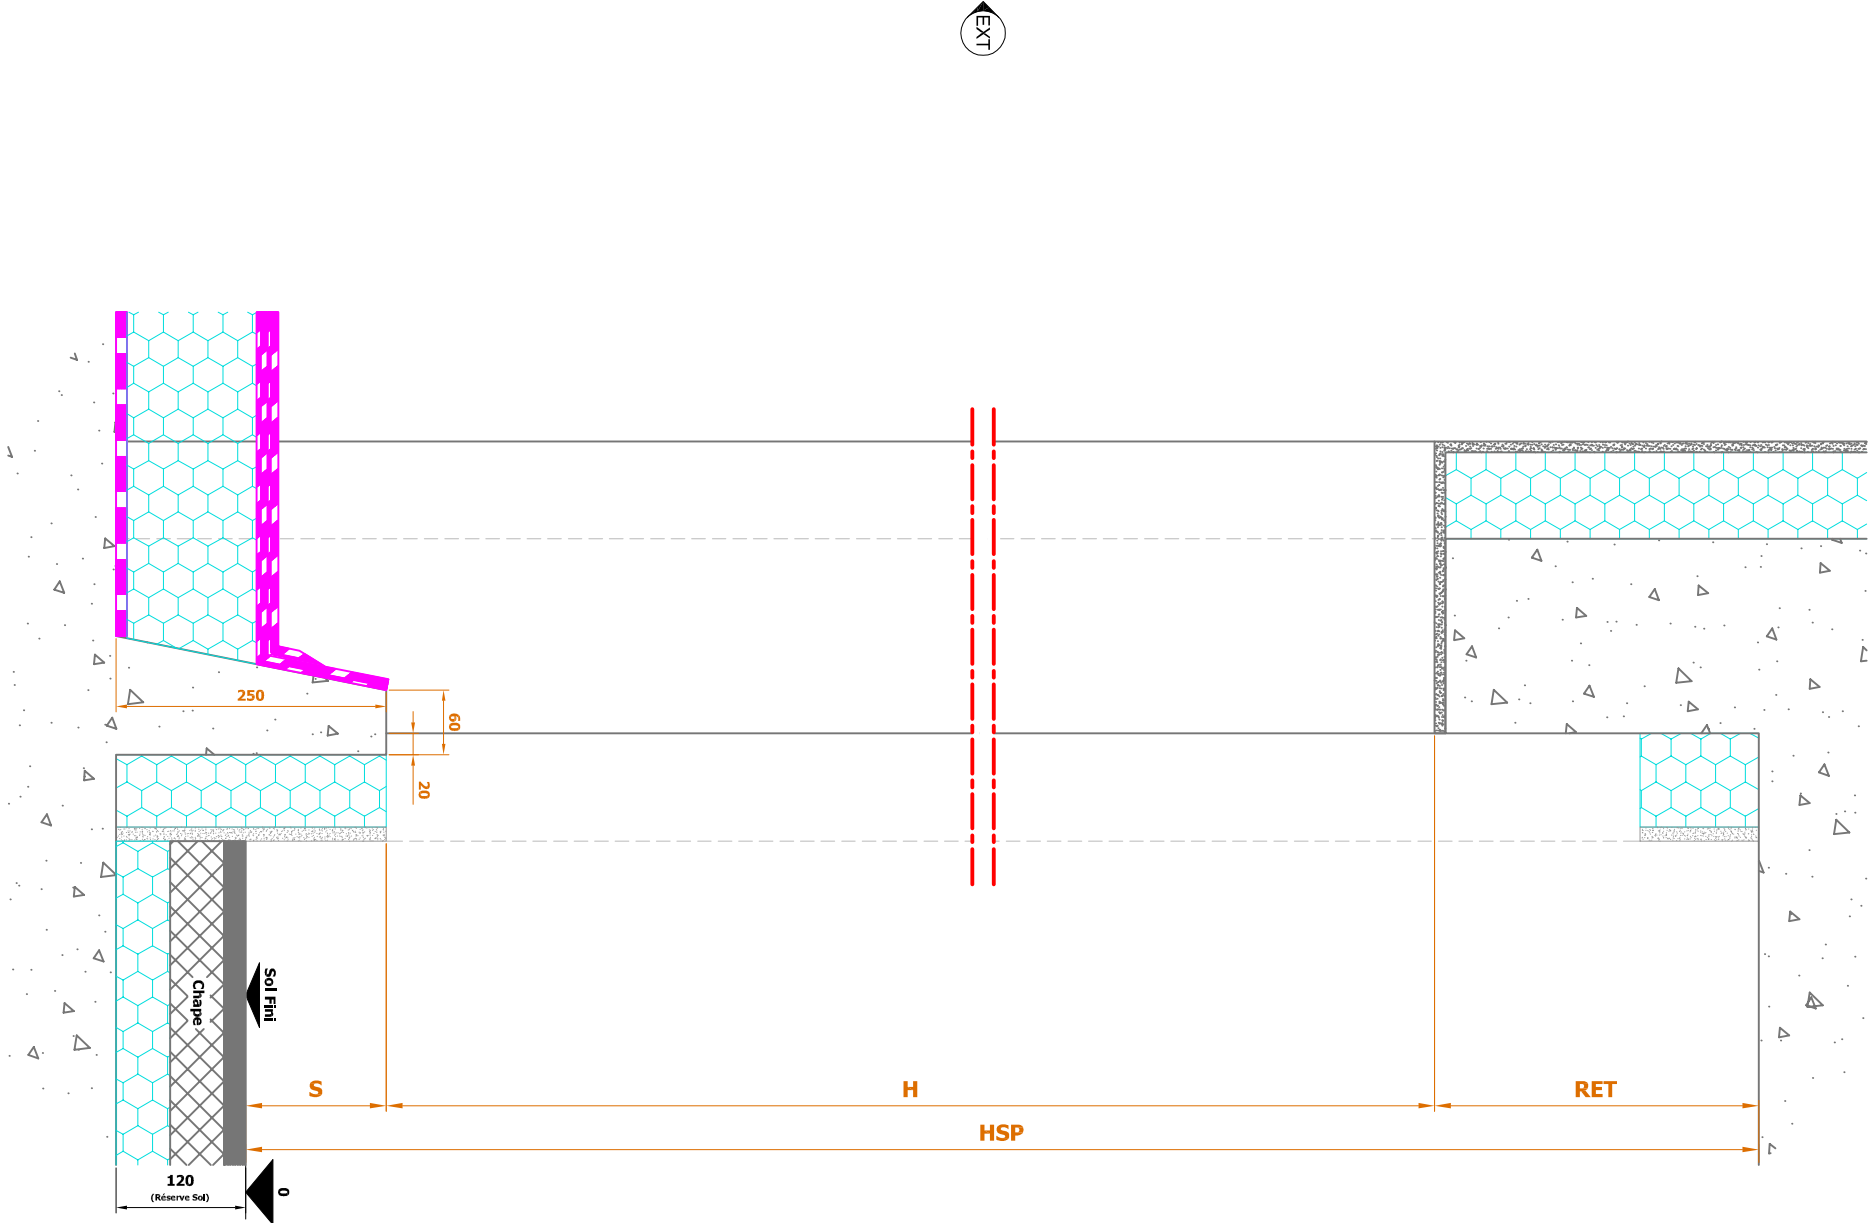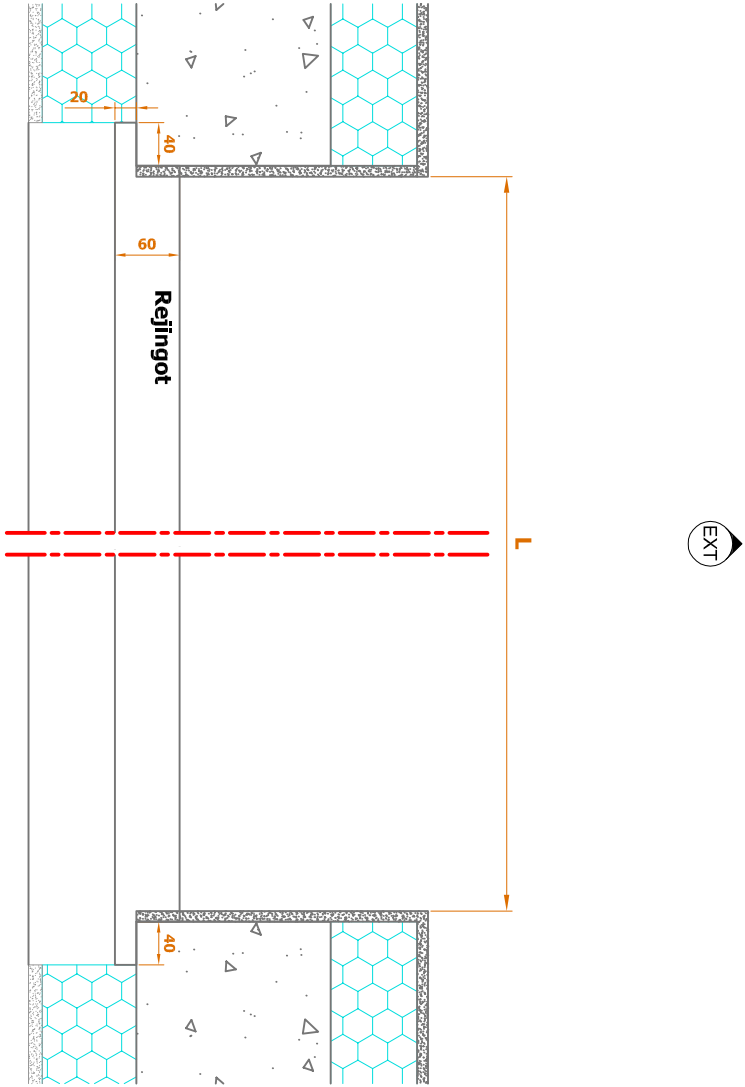


Lexique :
L : Largeur
H : Hauteur
S : Seuil
ALL : Allège
RET : Retombé de linteau
HSP : Hauteur sous Plafond
HSD : Hauteur sous Dalle
HSL : Hauteur sous Linteau
AP : Axe de Poignée
A : Entraxe
AM : Axe du Meneau
AT : Axe de la Traverse
LO : Largeur hors tout Ouvrant
HO : Largeur hors tout Ouvrant
AB : Axe de Battement d'ouvrant
PL : Passage Libre
CA : Cote Architecte

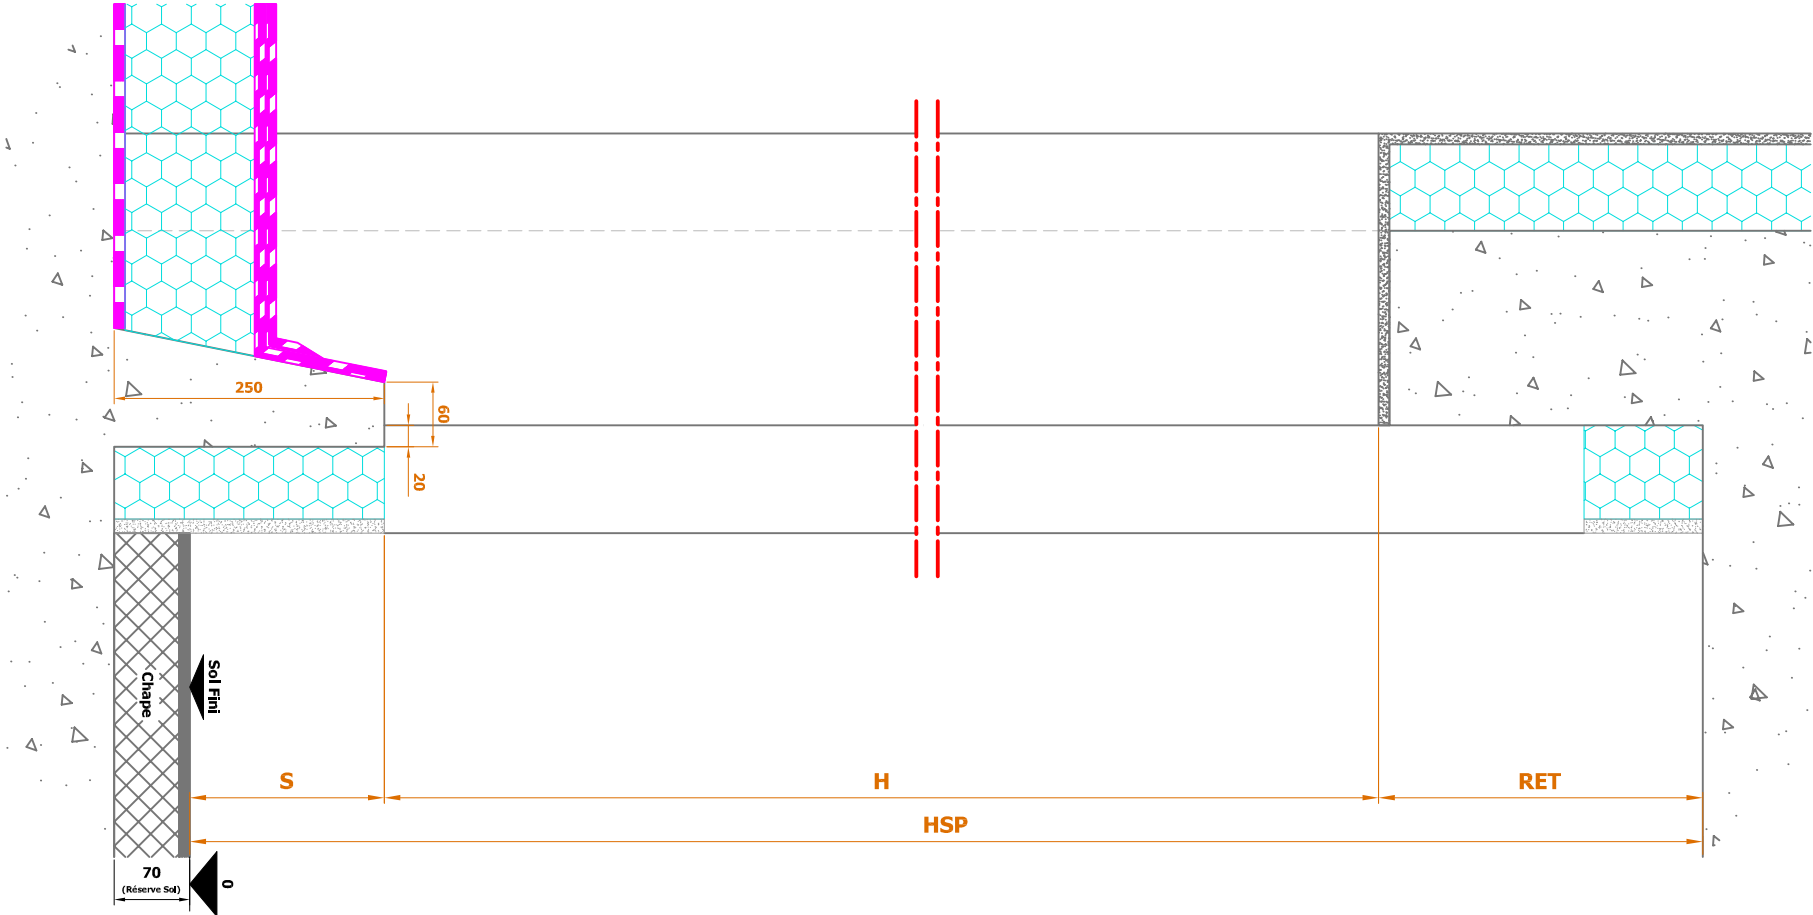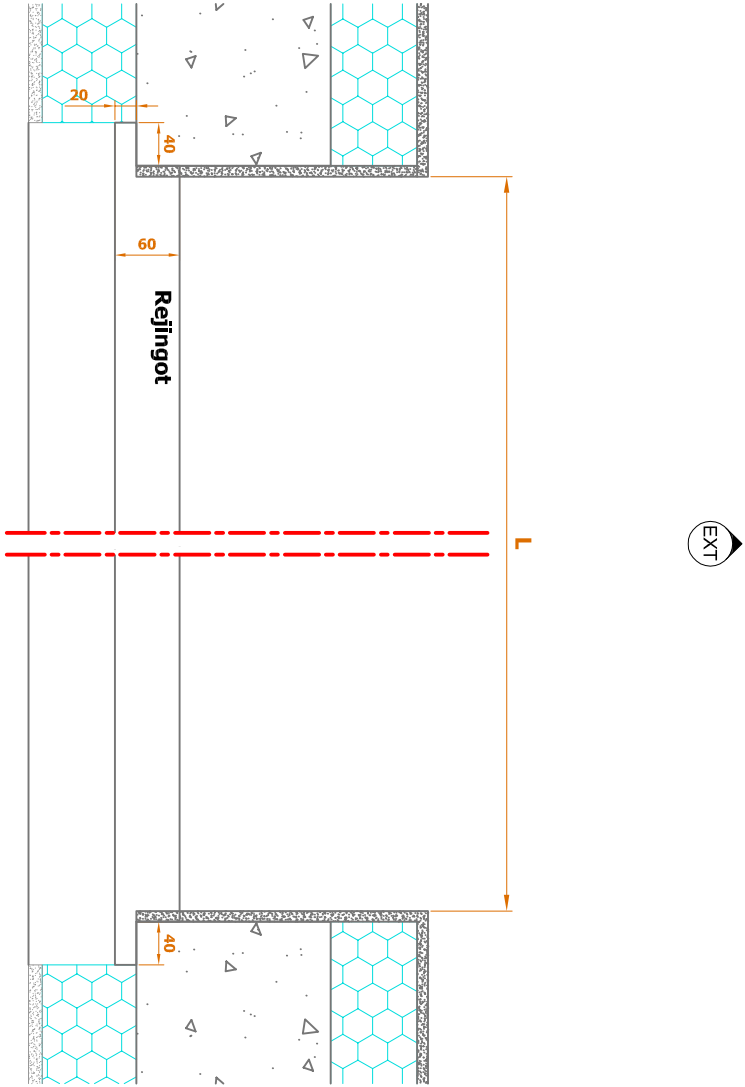

- Lexique :
- L : Largeur
 - H : Hauteur
 - S : Seuil
 - ALL : Allège
 - RET : Retombé de linteau
 - HSP : Hauteur sous Plafond
 - HSD : Hauteur Sous Dalle
 - HSL : Hauteur Sous Linteau
 - AP : Axe de Poignée
 - A : Entraxe
 - AM : Axe du Meneau
 - AT : Axe de la Traverse
 - LO : Largeur hors tout Ouvrant
 - HO : Hauteur hors tout Ouvrant
 - AB : Axe de Battement d'ouvrant
 - PL : Passage Libre
 - CA : Cote Architecte


Fenêtre sur All. vitrée avec VR

A1, A2; D1, D2; J1, J2, J3, J4; O1, O2 I1, I2; N1, N2, N3

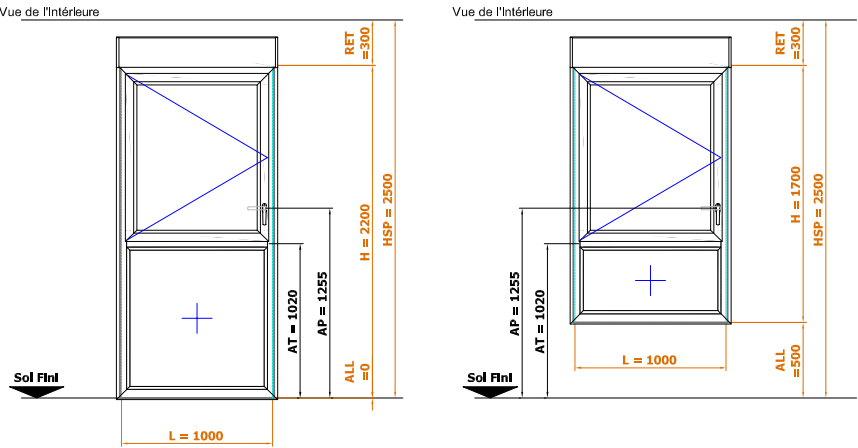


PF avec VR


A3; B1; C1; K1, K6, K7; O3, O4, O5, O6; P3 K2, K8, K9; O7; P1

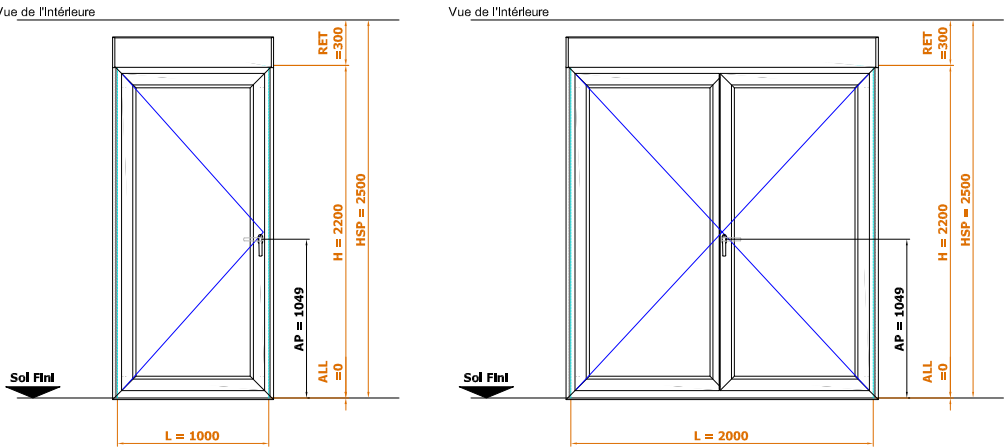


E1; K3, K4, K5, K10, K11; O8; P2

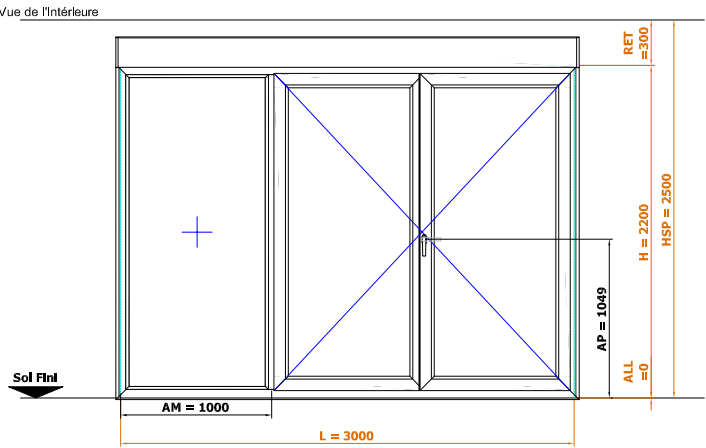


Fenêtre sur All. vitrée avec VR (hsp 2700)

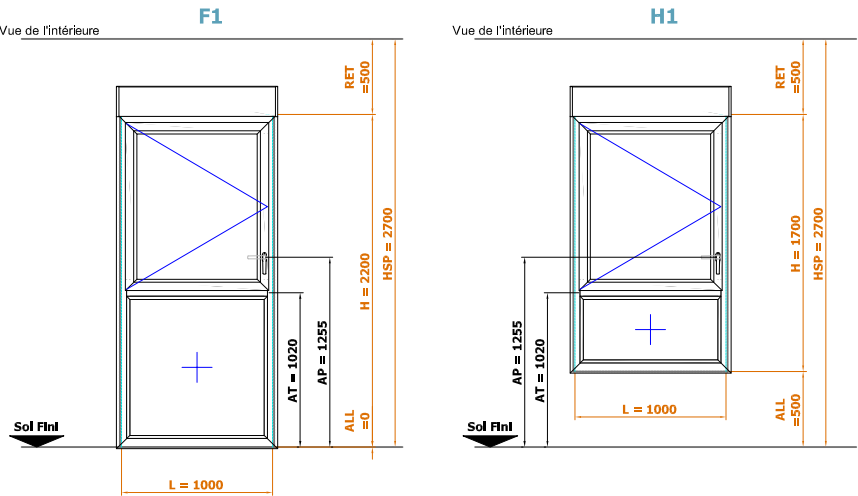


PF avec VR (hsp 2700)

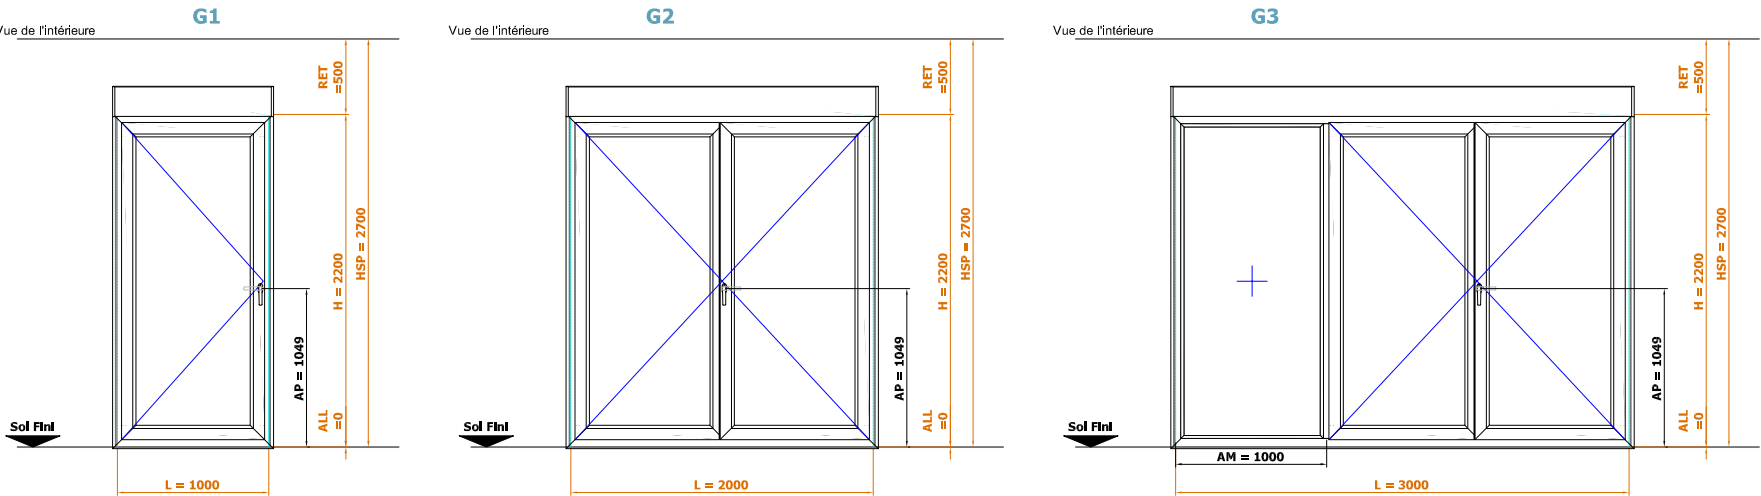


Fenêtre avec VR

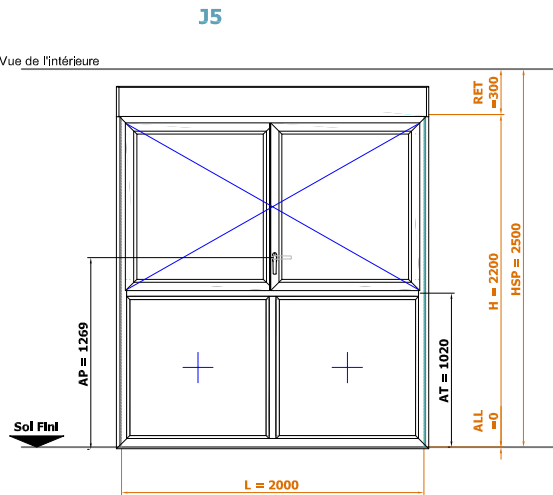

PF avec VR

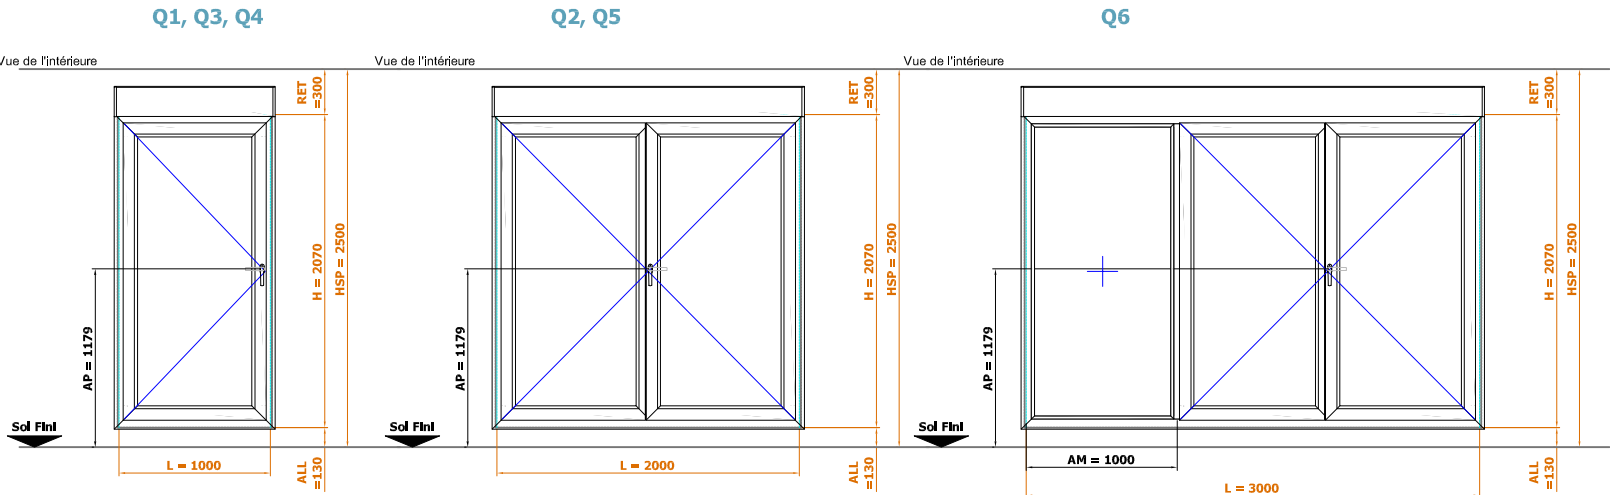

PF avec VR

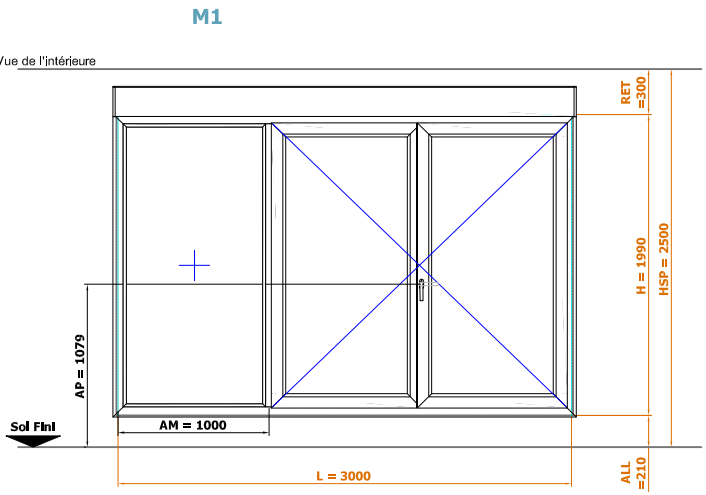

Lexique :
L : Largeur
H : Hauteur
S : Seuil
ALL : Allège
RET : Retombé de linteau
HSP : Hauteur Sous Plafond
HSD : Hauteur Sous Dalle
HSL : Hauteur Sous Linteau
AP : Axe de Palgine
A : Entraxe
AM : Axe du Meneau
AT : Axe de la Traverse
LO : Largeur hors tout Ouvrant
HO : Largeur hors tout Ouvrant
AB : Axe de Battement d'ouvrant
PL : Passage Libre
CA : Cote Architecte




LA MULATIERE (69) 15L001 - Le 180 (Bât A et B)

Elévations (1/1)

Echelle : 1:50 sur A3

Repère	Ind.	Date	Dessinateur
	A	22/06/2015	M. Branchu
	B	17/09/2015	M. Branchu
	C	25/09/2015	M. Branchu

PF avec VR

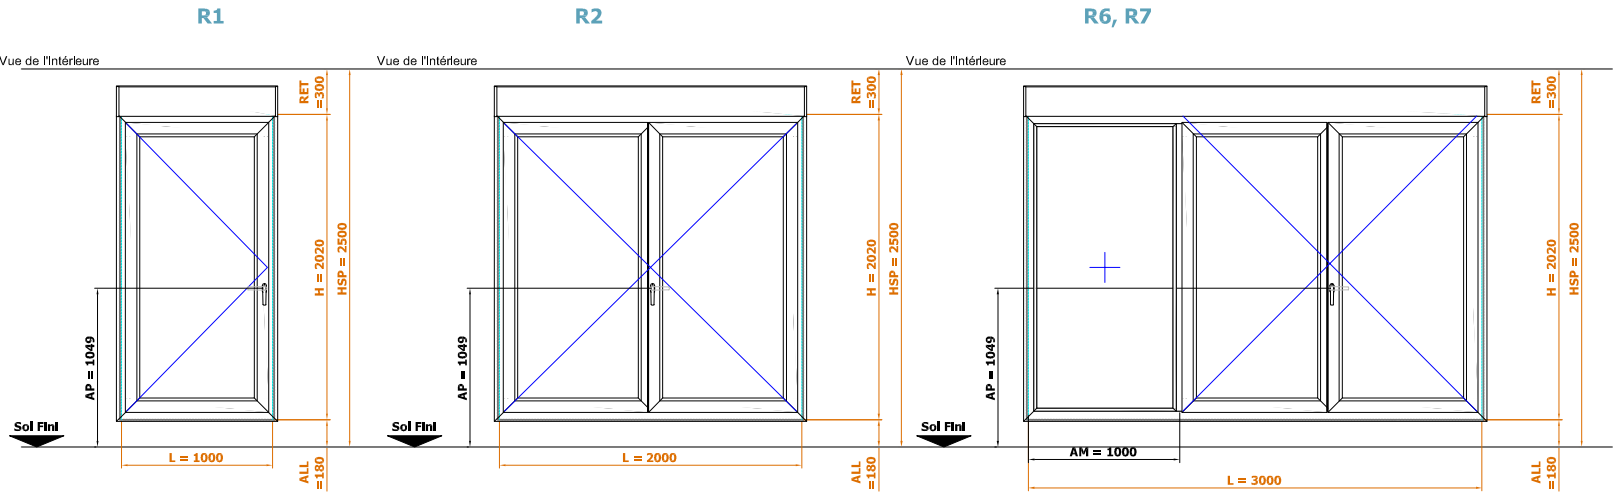

Lexique :
L : Largeur
H : Hauteur
S : Seuil
ALL : Allège
RET : Retombé de linteau
HSP : Hauteur Sous Plafond
HSD : Hauteur Sous Dalle
HSL : Hauteur Sous Linteau
AP : Axe de Pignonée
A : Entraxe
AM : Axe du Meneau
AT : Axe de la Traverse
LO : Largeur hors tout Ouvrant
HO : Largeur hors tout Ouvrant
AB : Axe de Battement d'ouvrant
PL : Passage Libre
CA : Cote Architecte





PORALU
MENUISERIES
Rue des bouleaux
01460 PORT
Tel : 04 74 76 26 66
Fax : 04 74 76 28 26

LA MULATIERE (69) 15L001 - Le 180 (Bât A et B)


Elévations (2/2)

Echelle : 1:50 sur A3

Repère	Ind.	Date	Dessinateur
	A	22/06/2015	M. Branchu
	B	17/09/2015	M. Branchu
	C	25/09/2015	M. Branchu

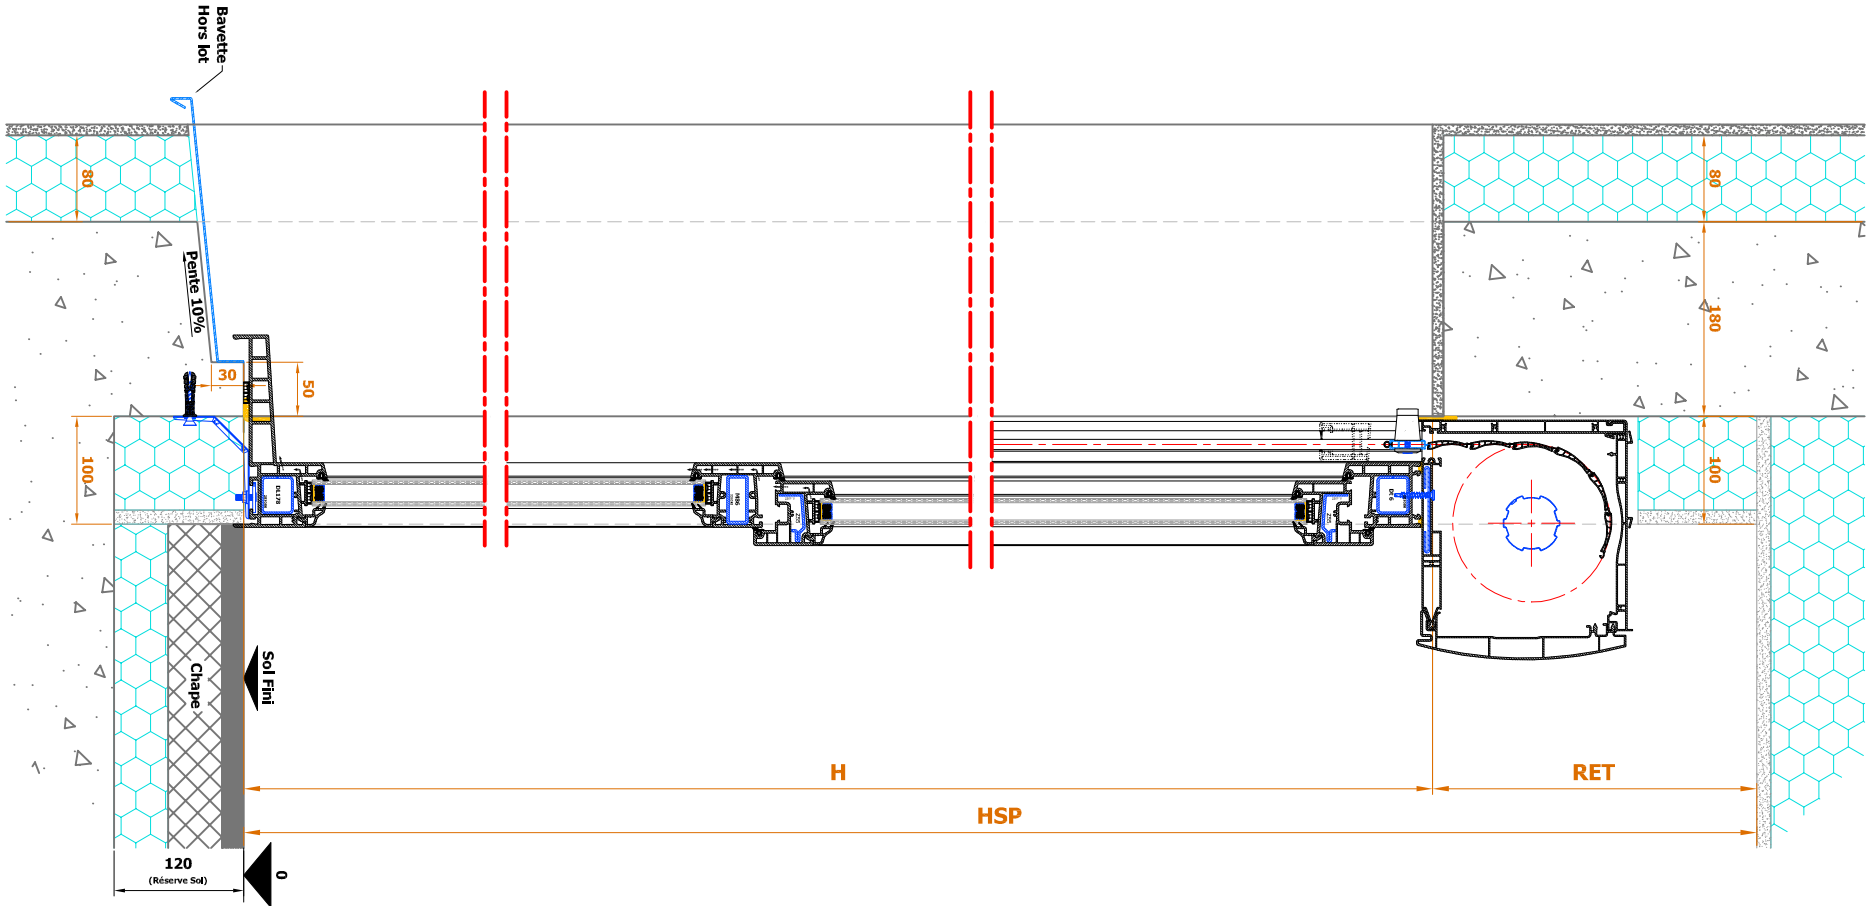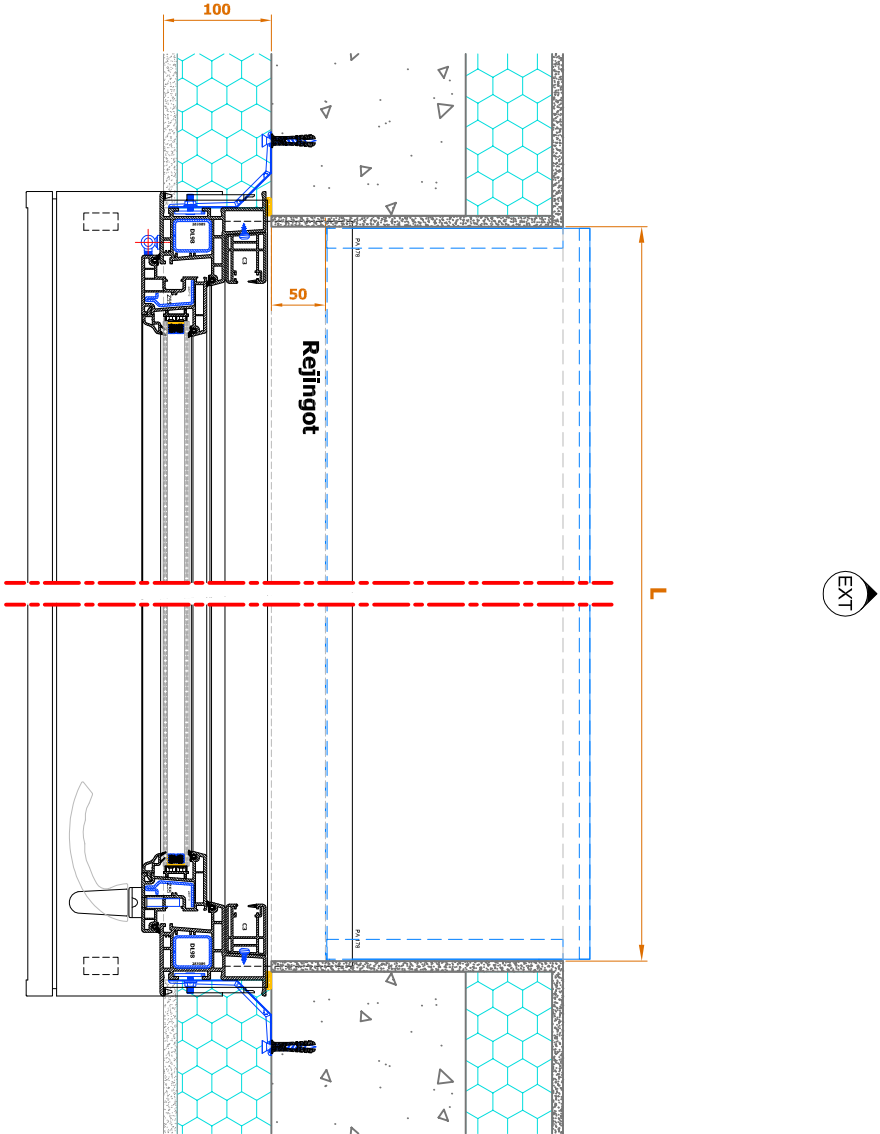


- Lexique :
- L : Largeur
 - H : Hauteur
 - S : Seuil
 - ALL : Allège
 - RET : Retombé de linteau
 - HSP : Hauteur Sous Plafond
 - HSD : Hauteur Sous Dalle
 - HSL : Hauteur Sous Linteau
 - AP : Axe de Poignée
 - A : Entraxe
 - AM : Axe du Meneau
 - AT : Axe de la Traverse
 - LO : Largeur hors tout Ouvrant
 - HO : Hauteur hors tout Ouvrant
 - AB : Axe de Battement d'ouvrant
 - PL : Passage Libre
 - CA : Cote Architecte


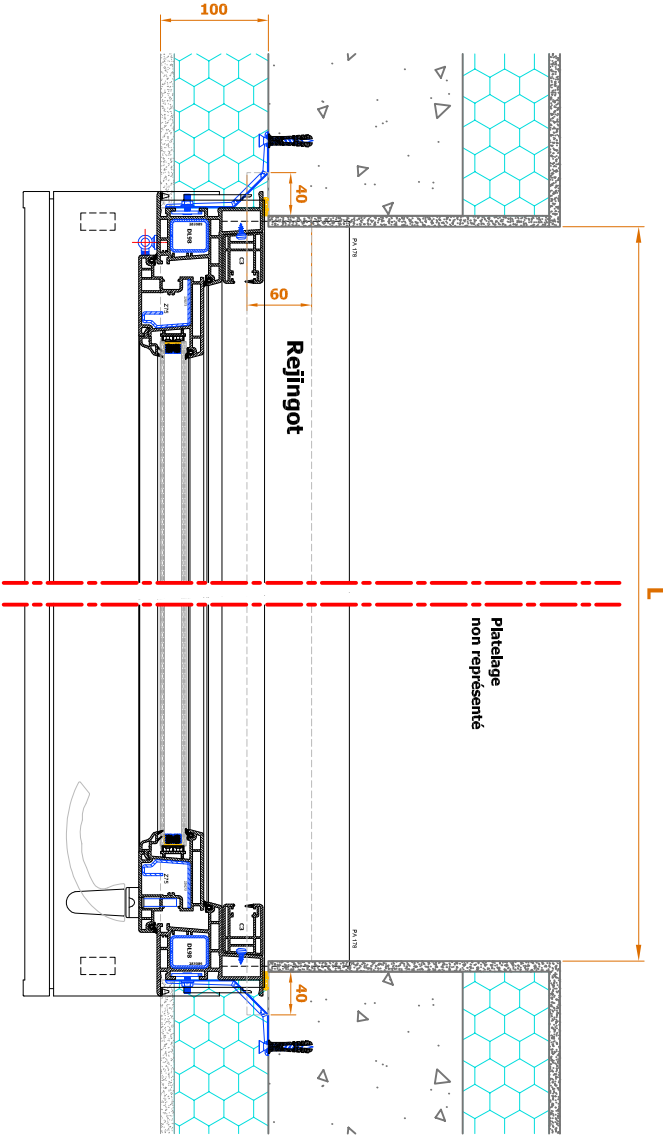


EXT

EXT

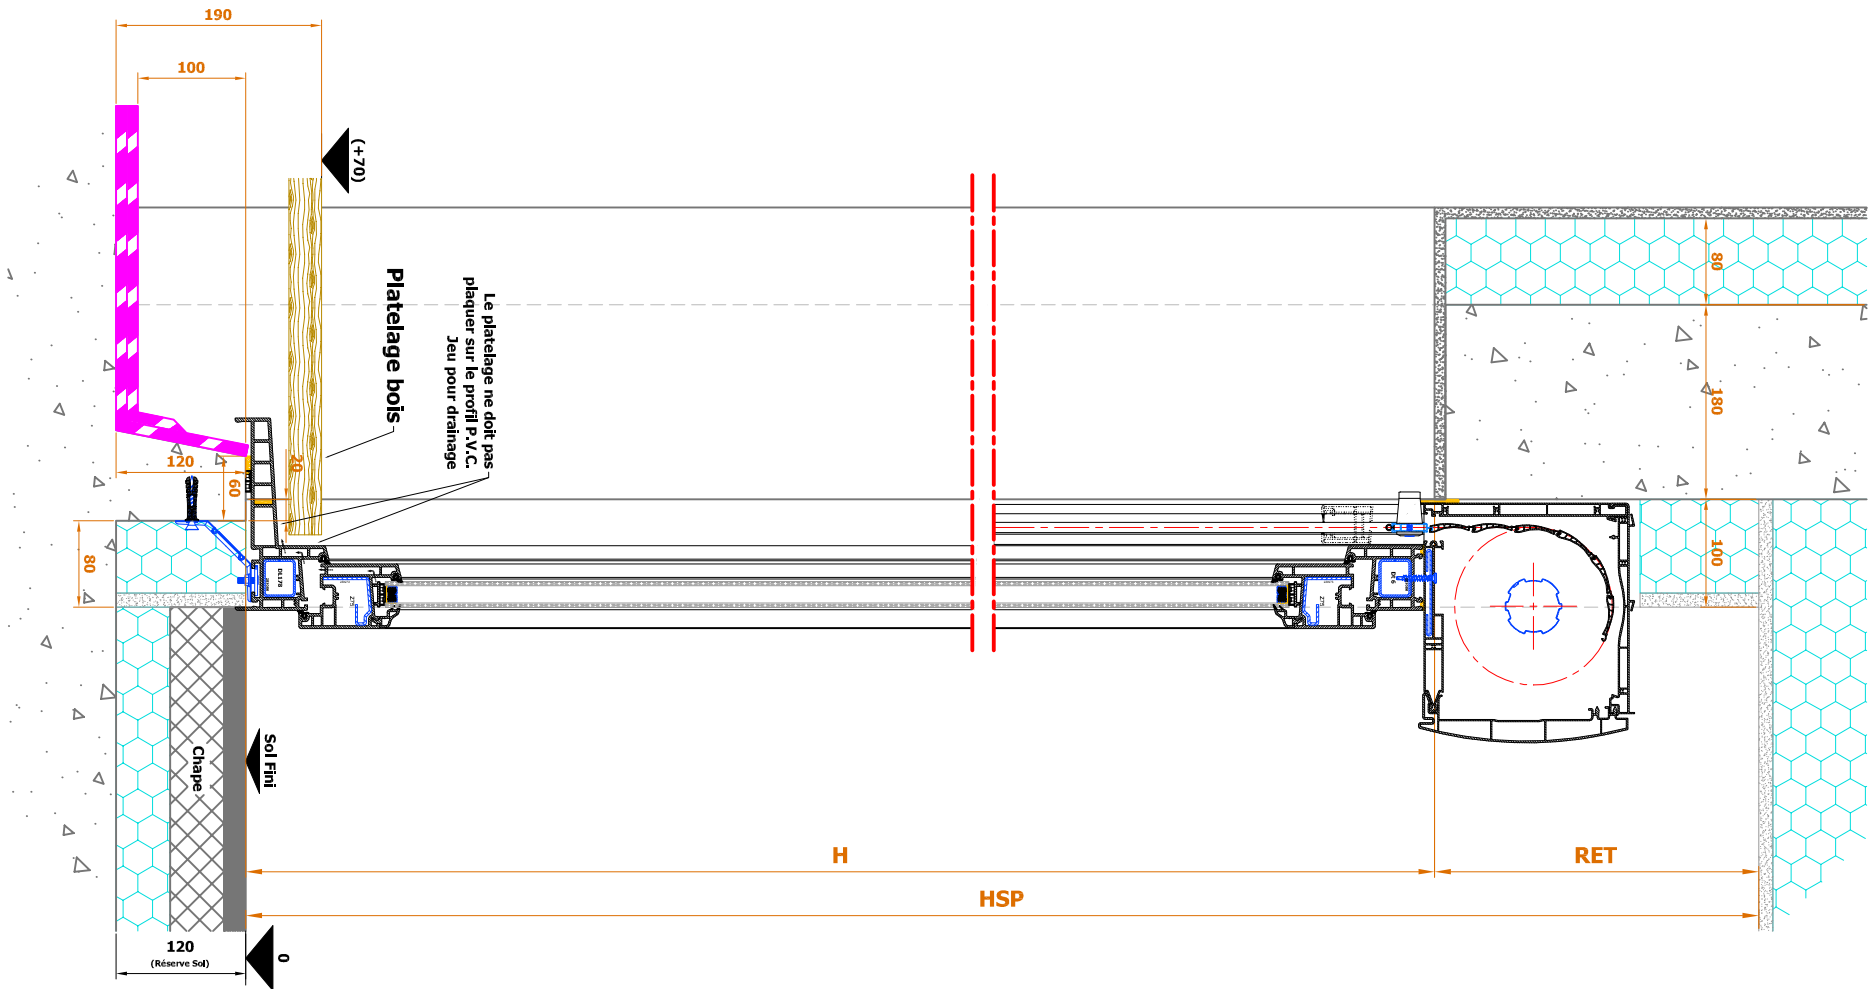

Lexique :
L : Largeur
H : Hauteur
S : Seuil
ALL : Allège
RET : Retombé de linteau
HSP : Hauteur Sous Plafond
HSD : Hauteur Sous Dalle
HSL : Hauteur Sous Linteau
AP : Axe de Poignée
A : Entraxe
AM : Axe du Meneau
AT : Axe de la Traverse
LO : Largeur hors tout Ouvrant
HO : Hauteur hors tout Ouvrant
AB : Axe de Battement d'ouvrant
PL : Passage Libre
CA : Cote Architecte

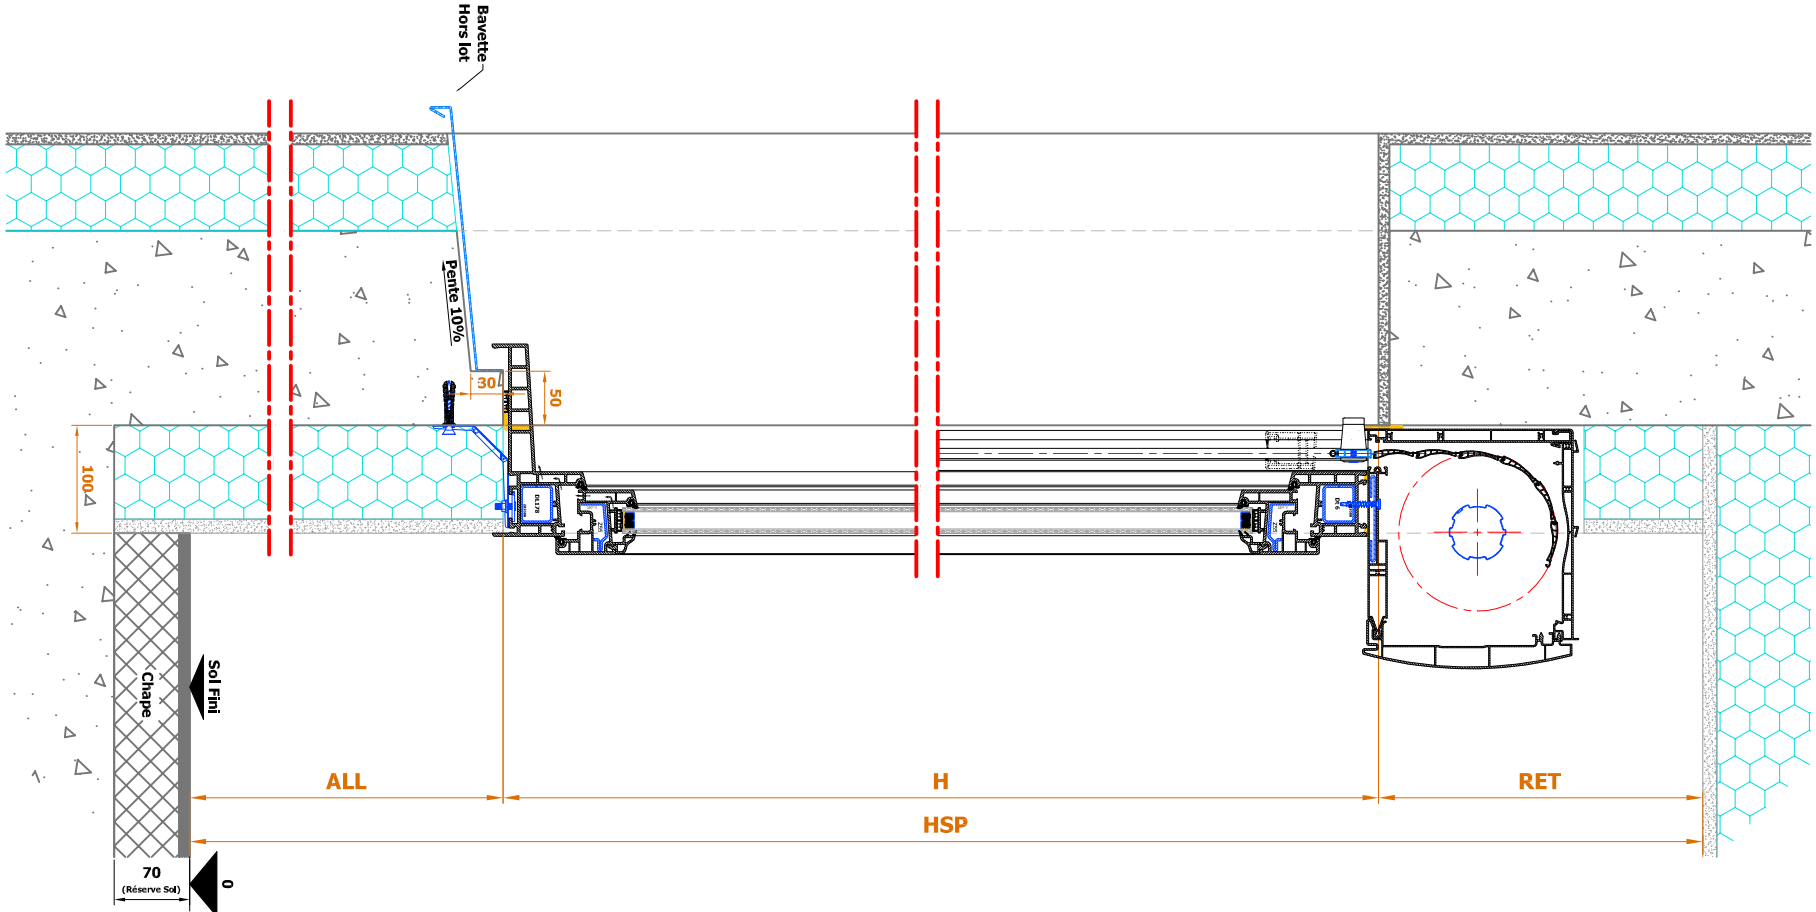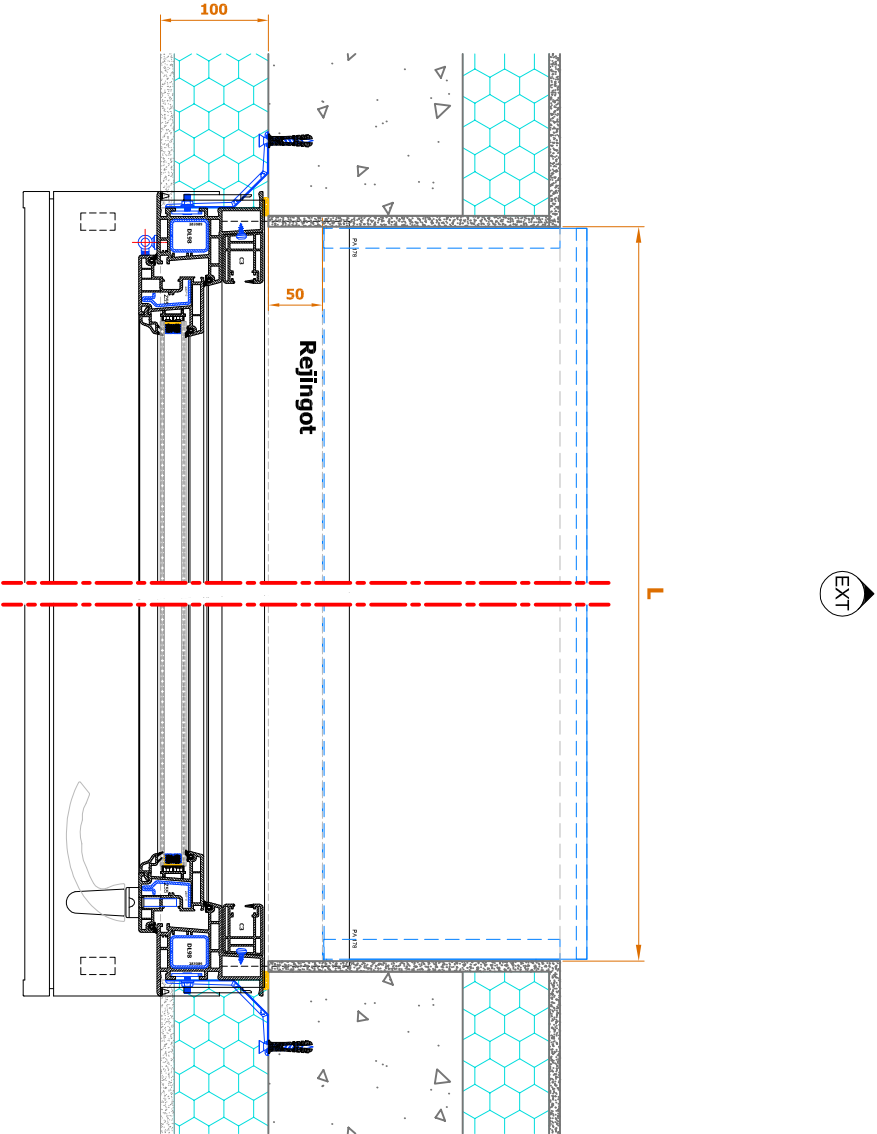

Lexique :

L : Largeur

H : Hauteur

S : Seuil

ALL : Allège

RET : Retombé de linteau

HSP : Hauteur sous Plafond

HSD : Hauteur sous Dalle

HSL : Hauteur sous Linteau

AP : Axe de Poignée

A : Entraxe

AM : Axe du Meneau

AT : Axe de la Traverse



LO : Largeur hors tout Ouvrant

HO : Hauteur hors tout Ouvrant



AB : Axe de Battement d'ouvrant

PL : Passage Libre



CA : Cote Architecte

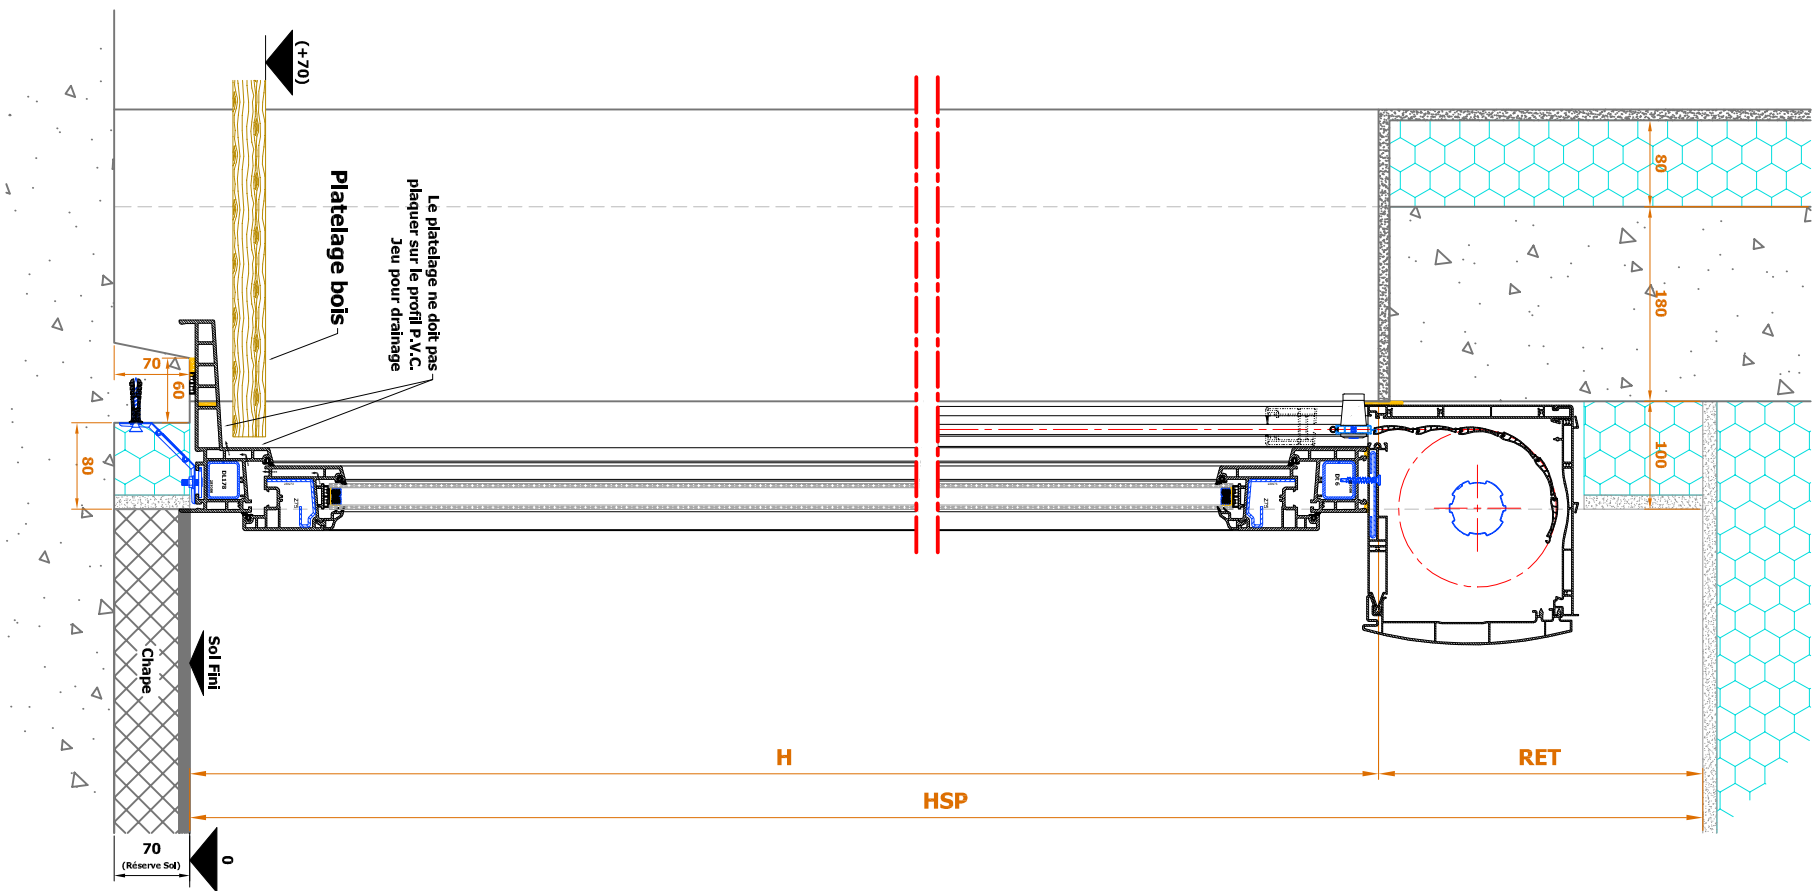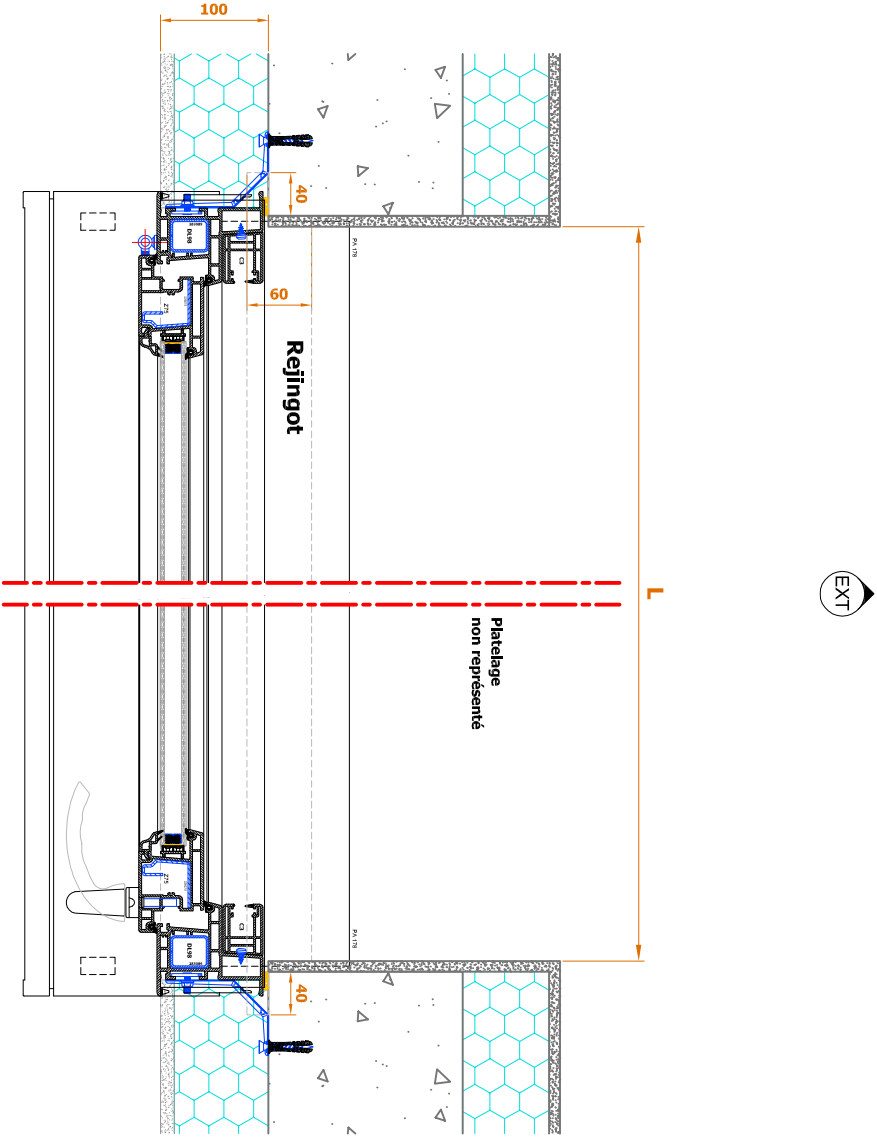

- Lexique :
- L : Largeur
 - H : Hauteur
 - S : Seuil
 - ALL : Allège
 - RET : Retombé de linteau
 - HSP : Hauteur sous Plafond
 - HSD : Hauteur Sous Dalle
 - HSL : Hauteur Sous Linteau
 - AP : Axe de Poignée
 - A : Entraxe
 - AM : Axe du Meneau
 - AT : Axe de la Traverse
 - LO : Largeur hors tout Ouvrant
 - HO : Hauteur hors tout Ouvrant
 - AB : Axe de Battement d'ouvrant
 - PL : Passage Libre
 - CA : Cote Architecte

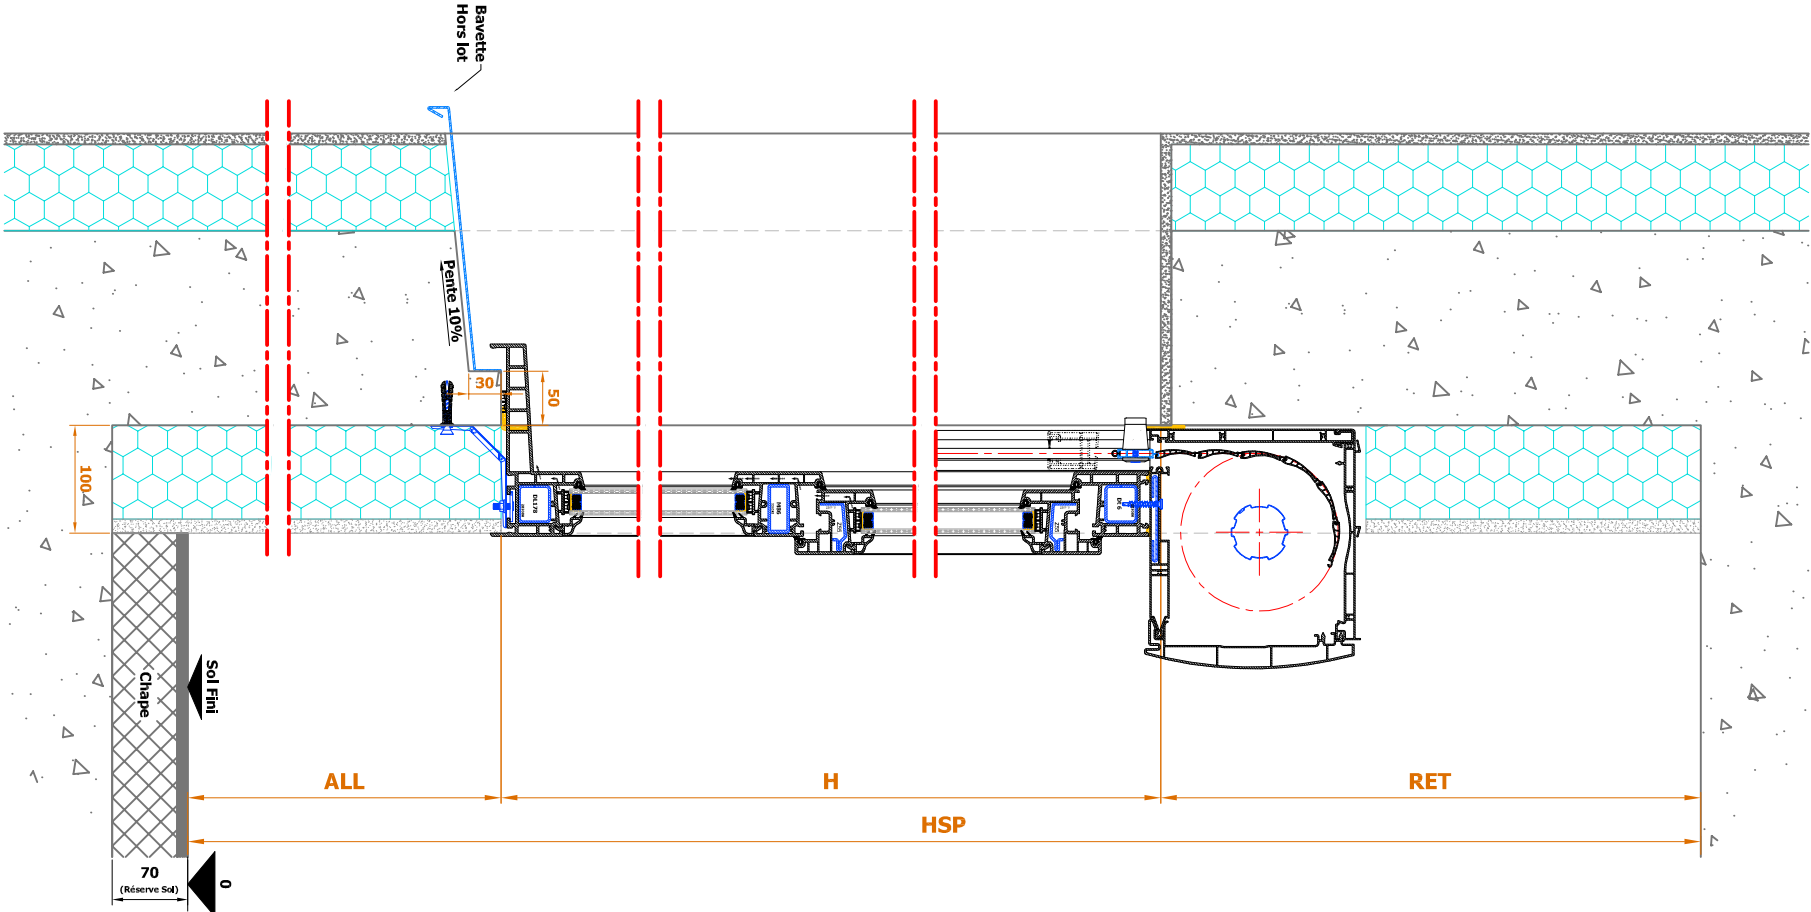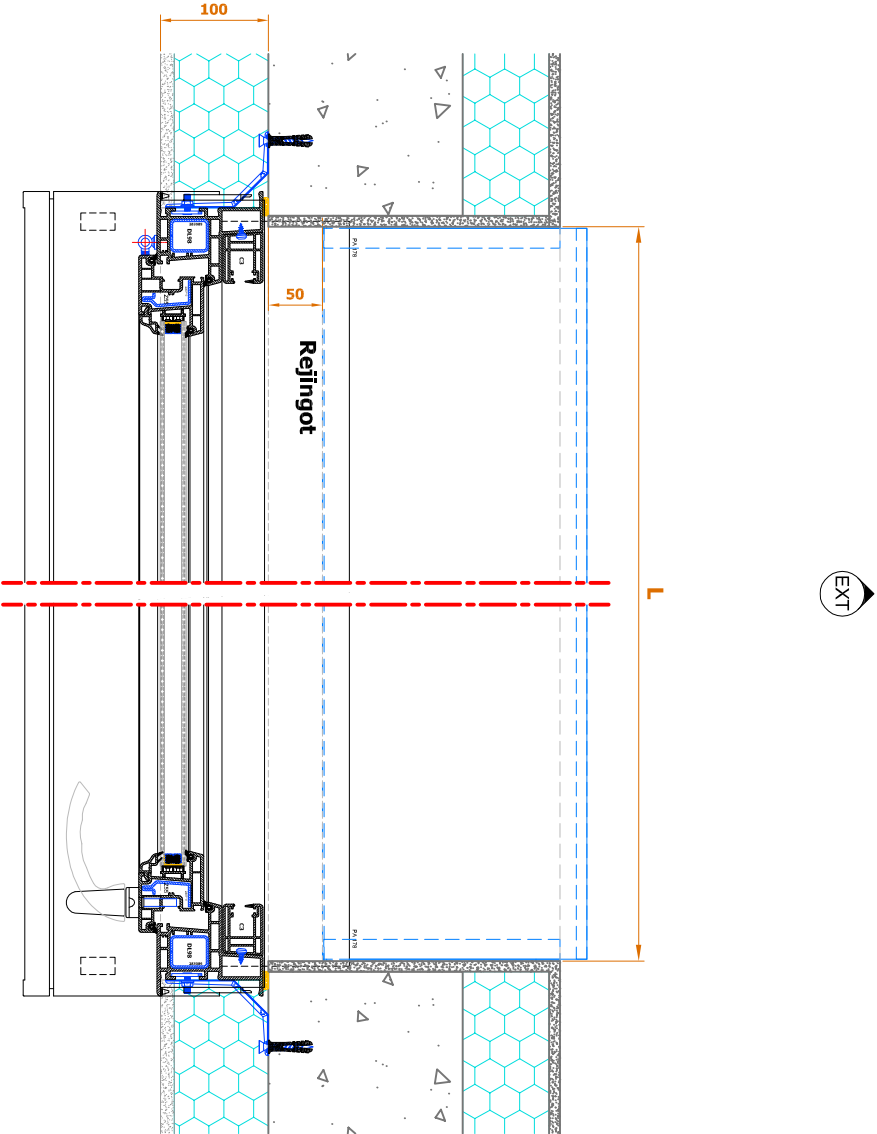

Lexique :
L : Largeur
H : Hauteur
S : Seuil
ALL : Allège
RET : Retombé de linteau
HSP : Hauteur sous Plafond
HSD : Hauteur sous Dalle
HSL : Hauteur sous Linteau
AP : Axe de Poignée
A : Entraxe
AM : Axe du Meneau
AT : Axe de la Traverse
LO : Largeur hors tout Ouvrant
HO : Hauteur hors tout Ouvrant
AB : Axe de Battement d'ouvrant
PL : Passage Libre
CA : Cote Architecte

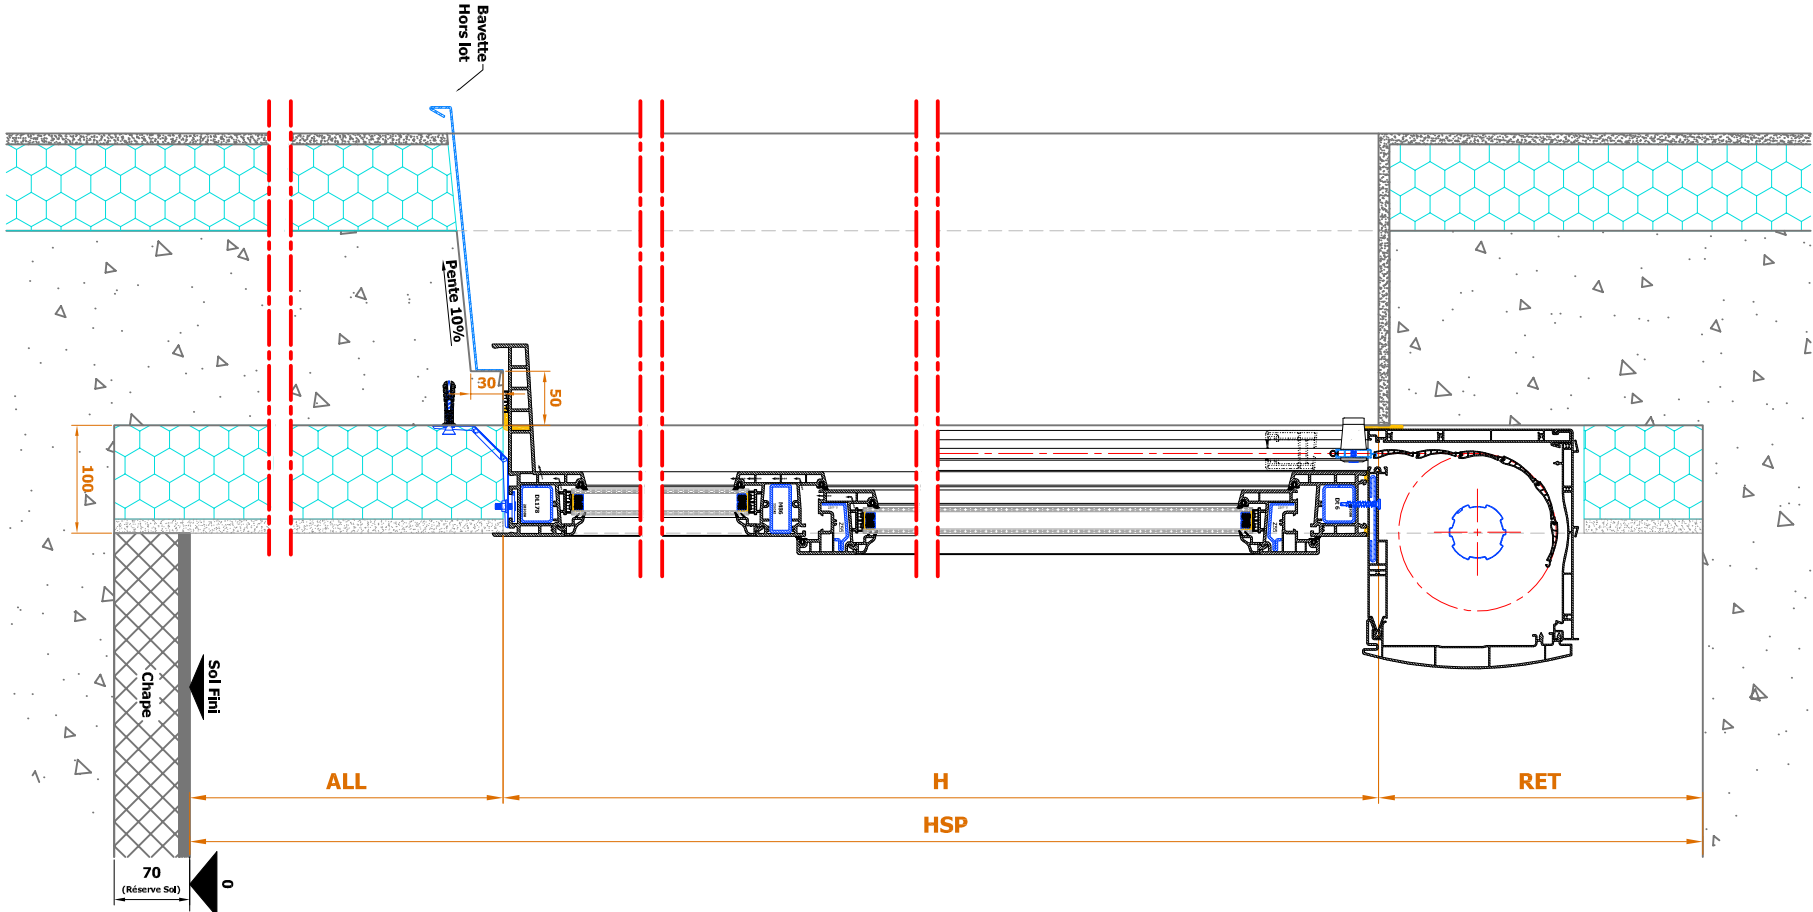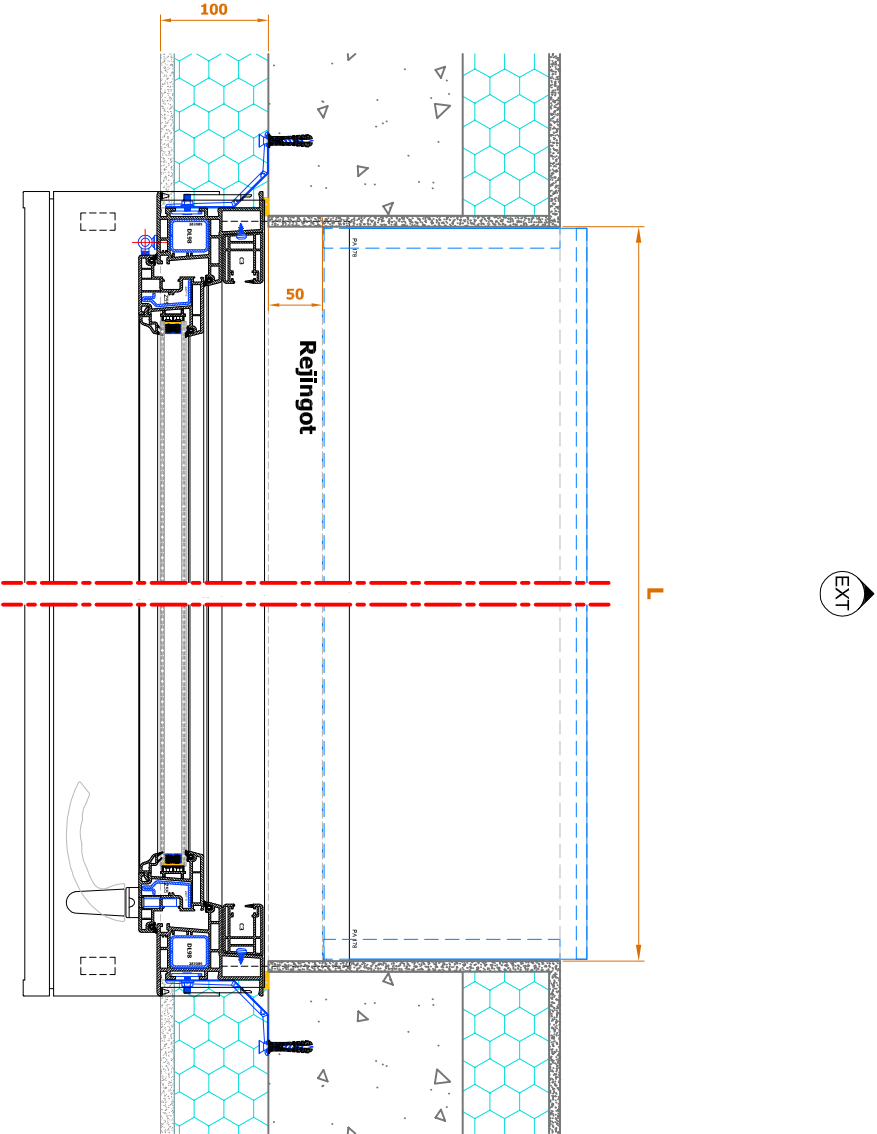

Lexique :

L : Largeur

H : Hauteur

S : Seuil

ALL : Allège

RET : Retombé de linteau

HSP : Hauteur sous Plafond

HSD : Hauteur sous Dalle

HSL : Hauteur sous Linteau

AP : Axe de Poignée

A : Entraxe

AM : Axe du Meneau

AT : Axe de la Traverse



LO : Largeur hors tout Ouvrant

HO : Hauteur hors tout Ouvrant


AB : Axe de Battement d'ouvrant


PL : Passage Libre

CA : Cote Architecte

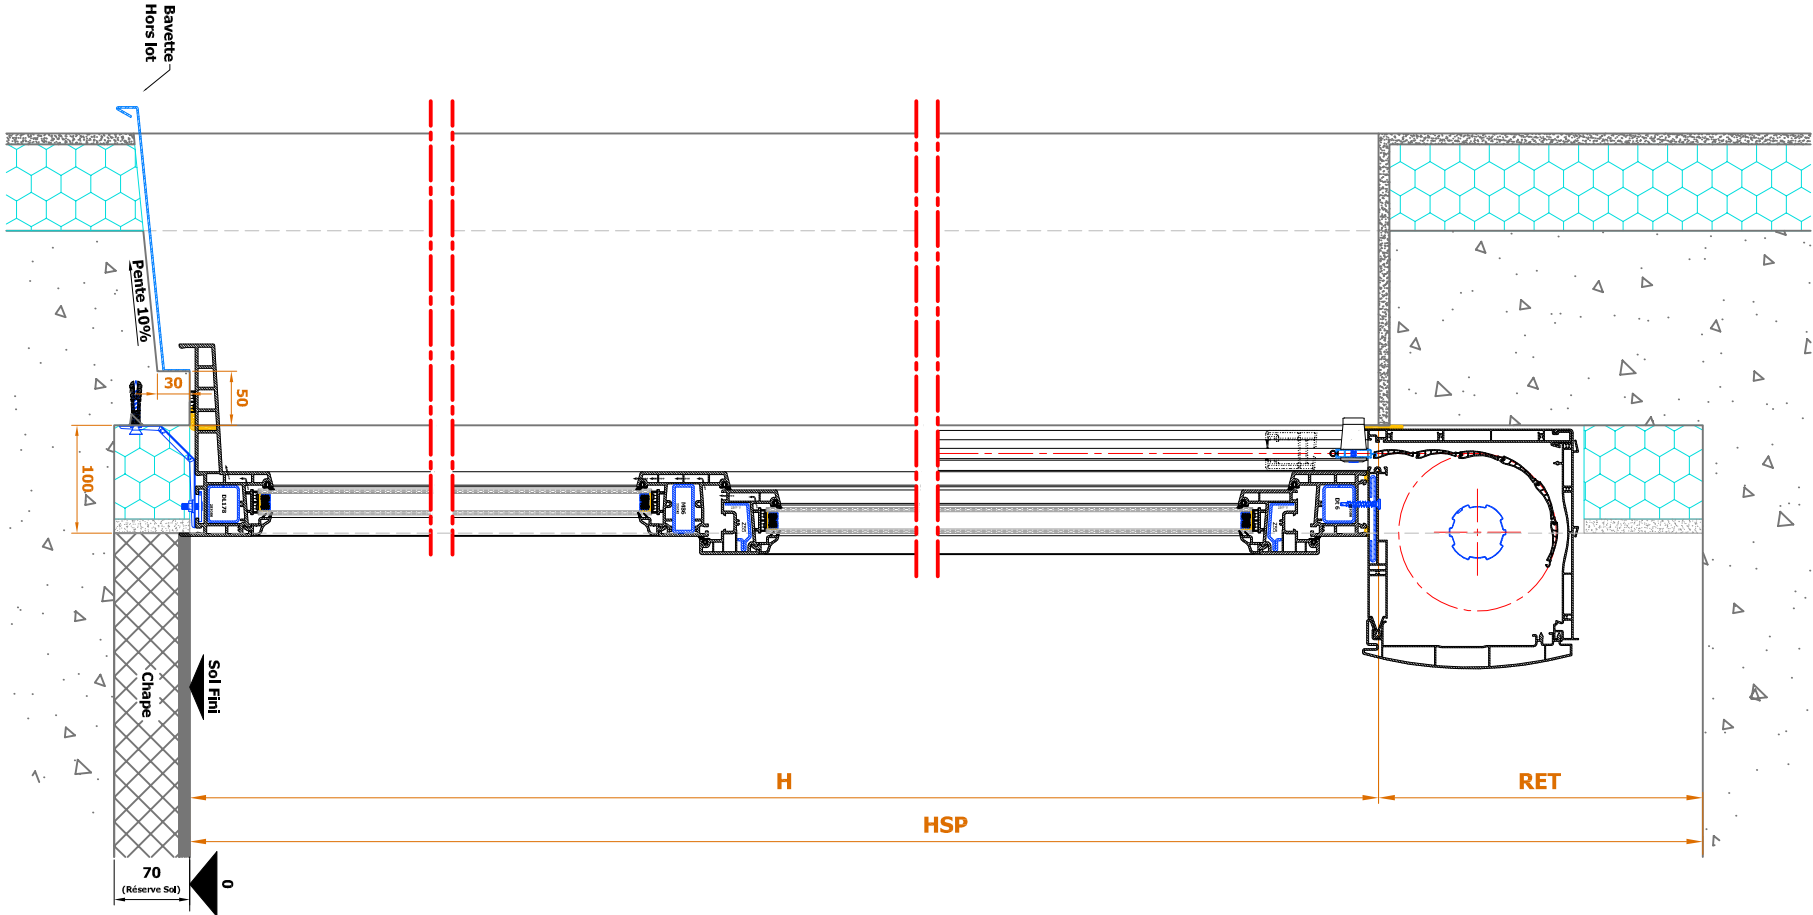
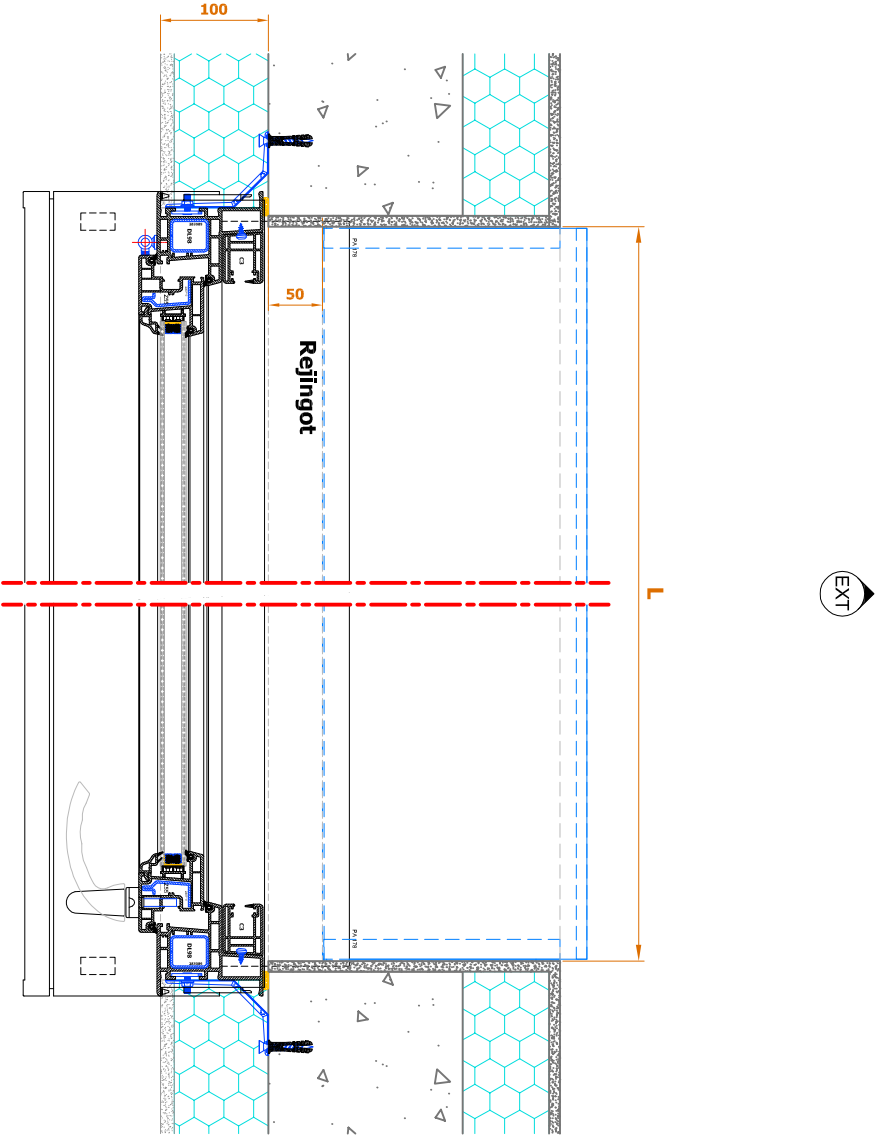


- Lexique :
- L : Largeur
 - H : Hauteur
 - S : Seuil
 - ALL : Allège
 - RET : Retombé de linteau
 - HSP : Hauteur sous Plafond
 - HSD : Hauteur Sous Dalle
 - HSL : Hauteur Sous Linteau
 - AP : Axe de Poignée
 - A : Entraxe
 - AM : Axe du Meneau
 - AT : Axe de la Traverse
 - LO : Largeur hors tout Ouvrant
 - HO : Hauteur hors tout Ouvrant
 - AB : Axe de Battement d'ouvrant
 - PL : Passage Libre
 - CA : Cote Architecte


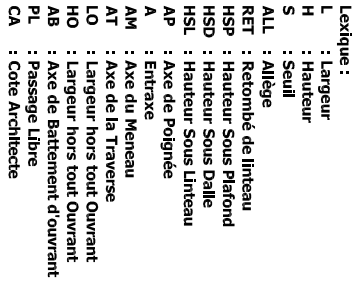


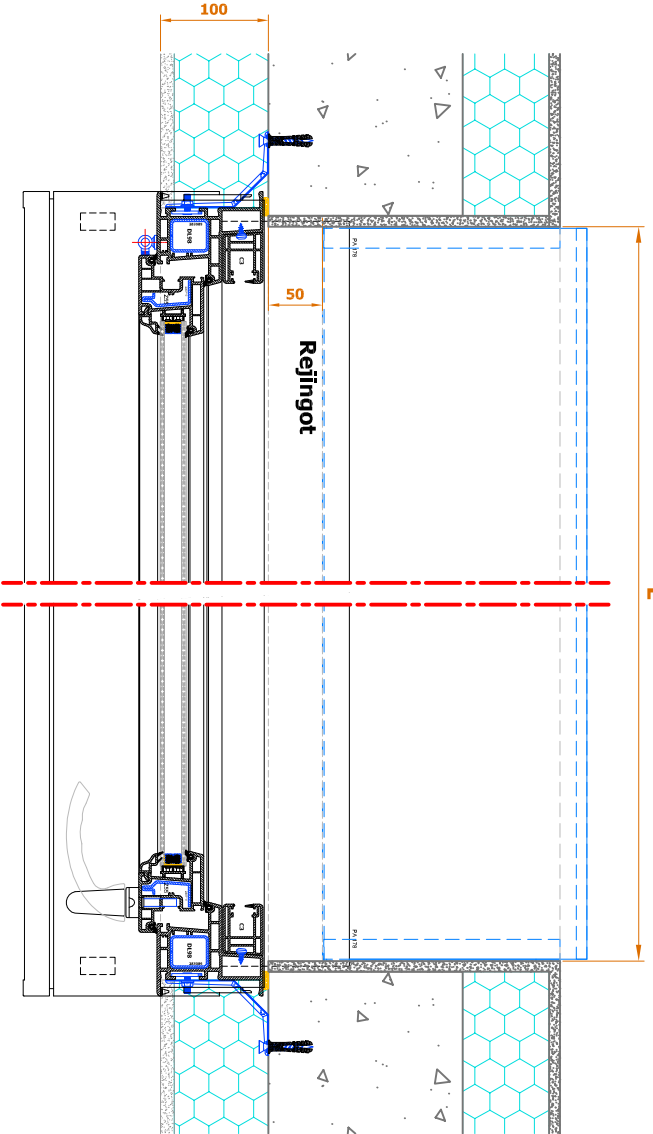


- Lexique :
- L : Largeur
 - H : Hauteur
 - S : Seuil
 - ALL : Allège
 - RET : Retombé de linteau
 - HSP : Hauteur Sous Plafond
 - HSD : Hauteur Sous Dalle
 - HSL : Hauteur Sous Linteau
 - AP : Axe de Poinçonnée
 - A : Entraxe
 - AM : Axe du Membreau
 - AT : Axe de la Traverse
 - LO : Largeur hors tout Ouvrant
 - HO : Largeur hors tout Ouvrant
 - AB : Axe de Battement d'ouvrant
 - PL : Passage Libre
 - CA : Cote Architecte

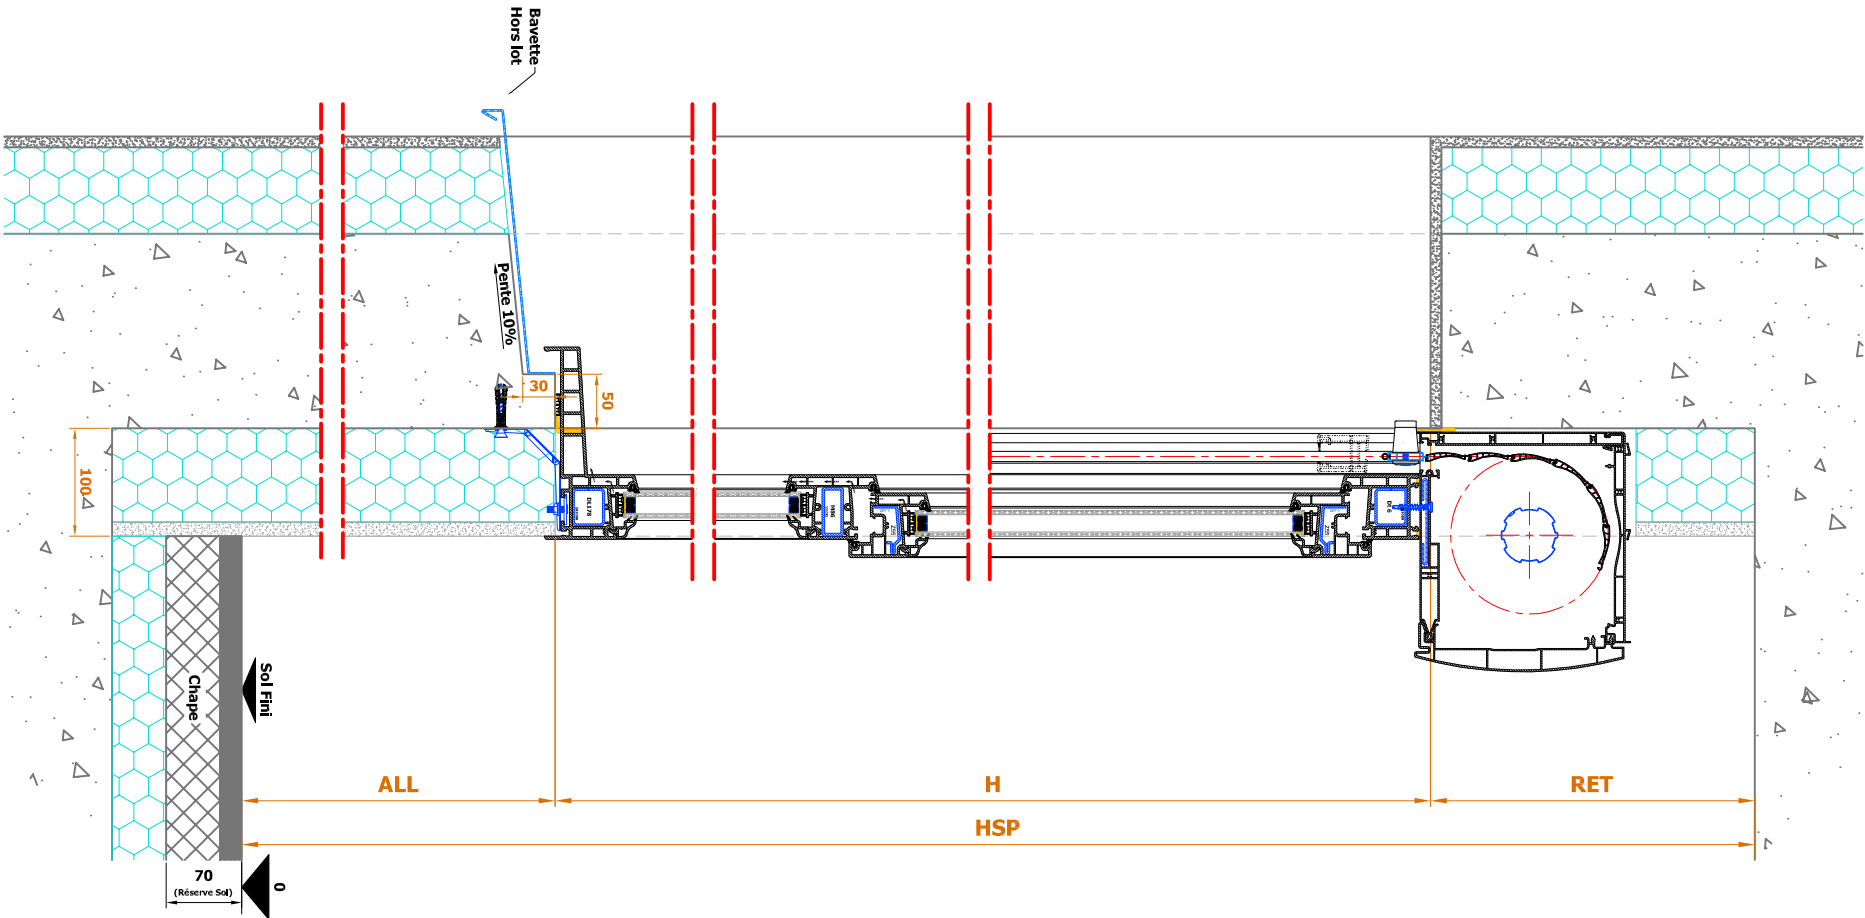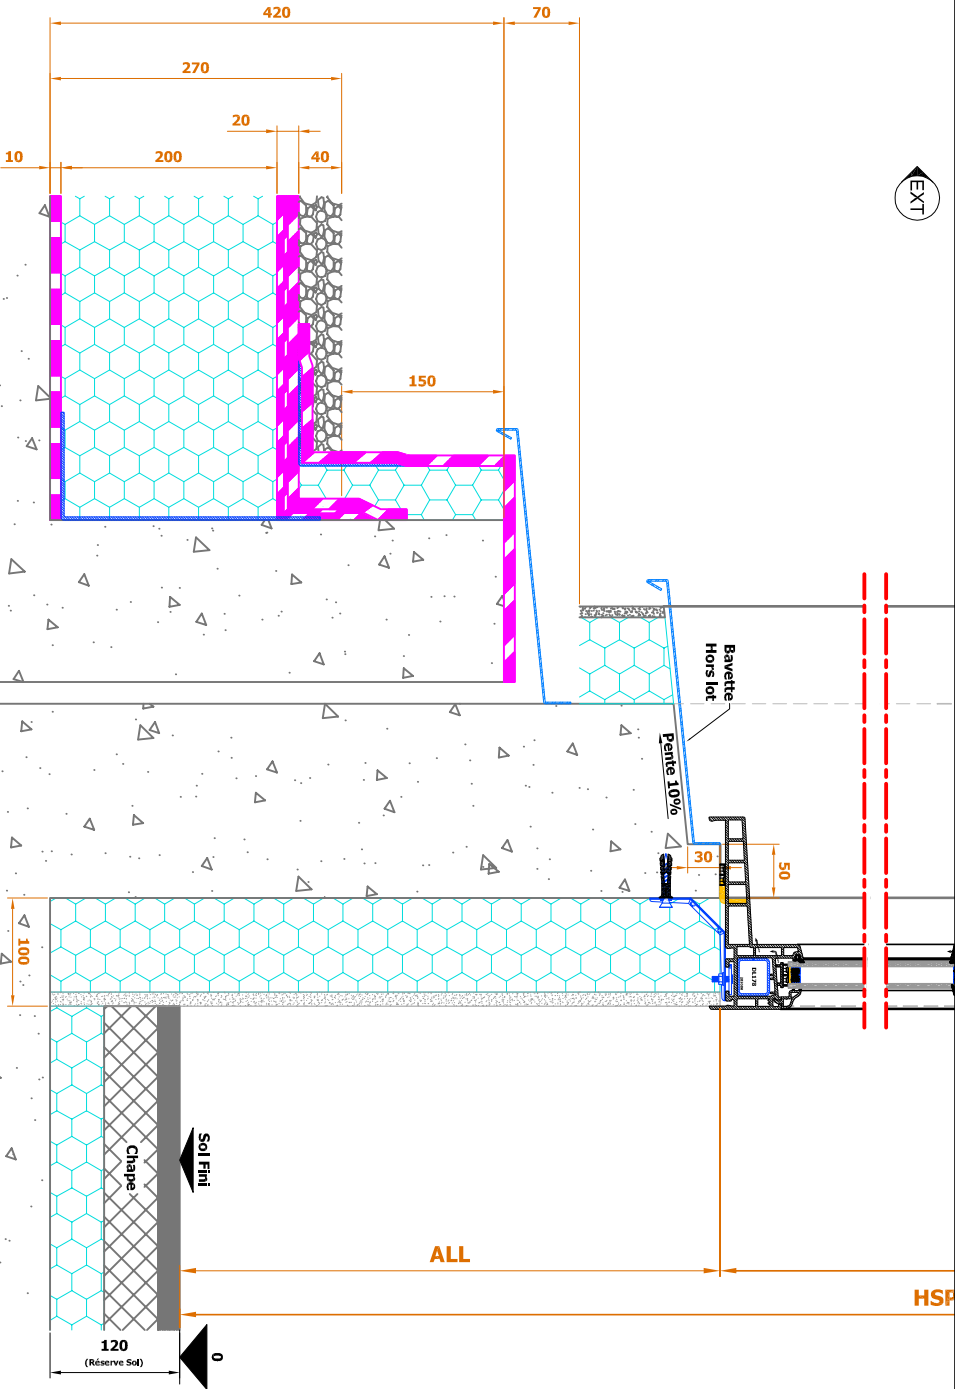

Bâtiment B / R-4 (terrasse non accessible)
(S.I.E détail 8.2)

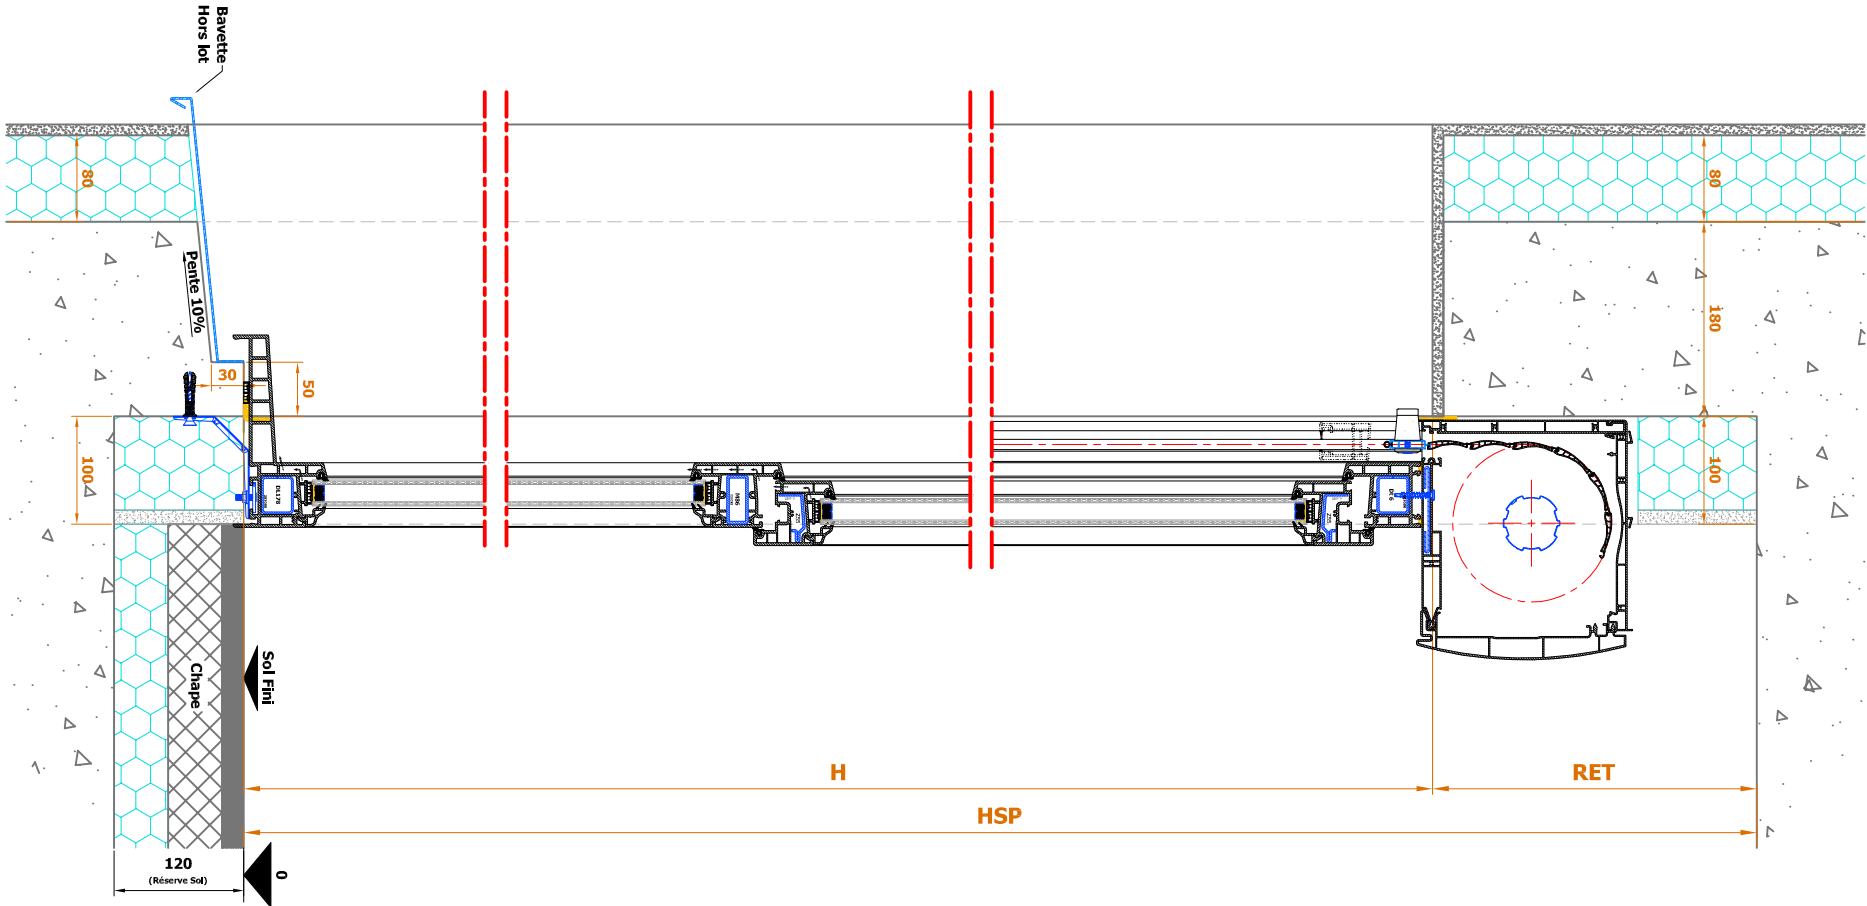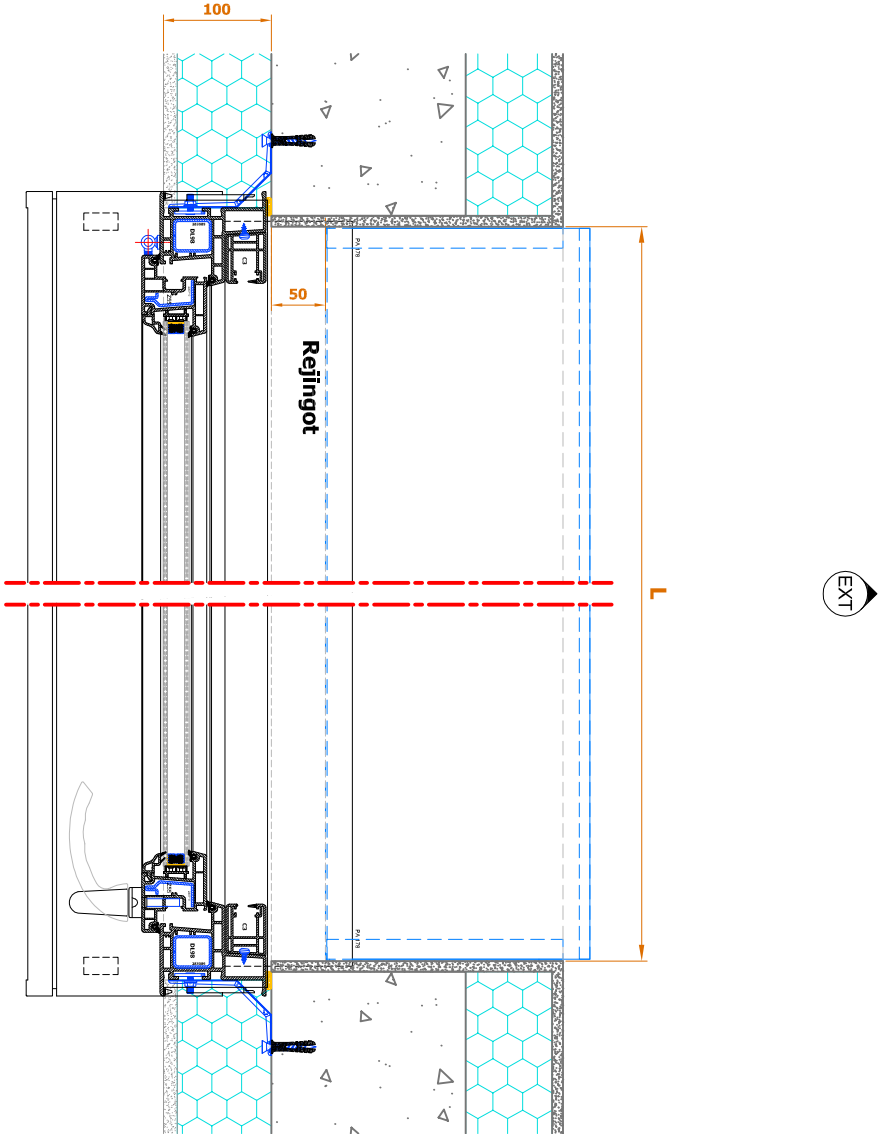


- Lexique :
- L : Largeur
 - H : Hauteur
 - S : Seuil
 - ALL : Allège
 - RET : Retombé de linteau
 - HSP : Hauteur sous Plafond
 - HSD : Hauteur Sous Dalle
 - HSL : Hauteur Sous Linteau
 - AP : Axe de Poignée
 - A : Entraxe
 - AM : Axe du Meneau
 - AT : Axe de la Traverse
 - LO : Largeur hors tout Ouvrant
 - HO : Hauteur hors tout Ouvrant
 - AB : Axe de Battement d'ouvrant
 - PL : Passage Libre
 - CA : Cote Architecte

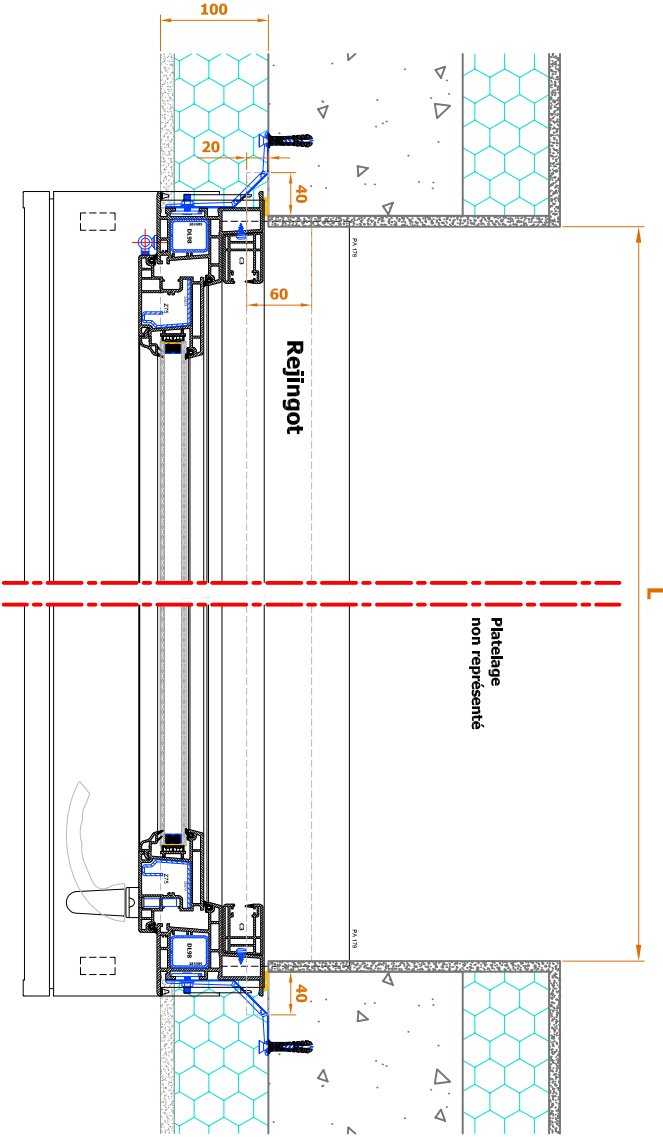


EXT

EXT

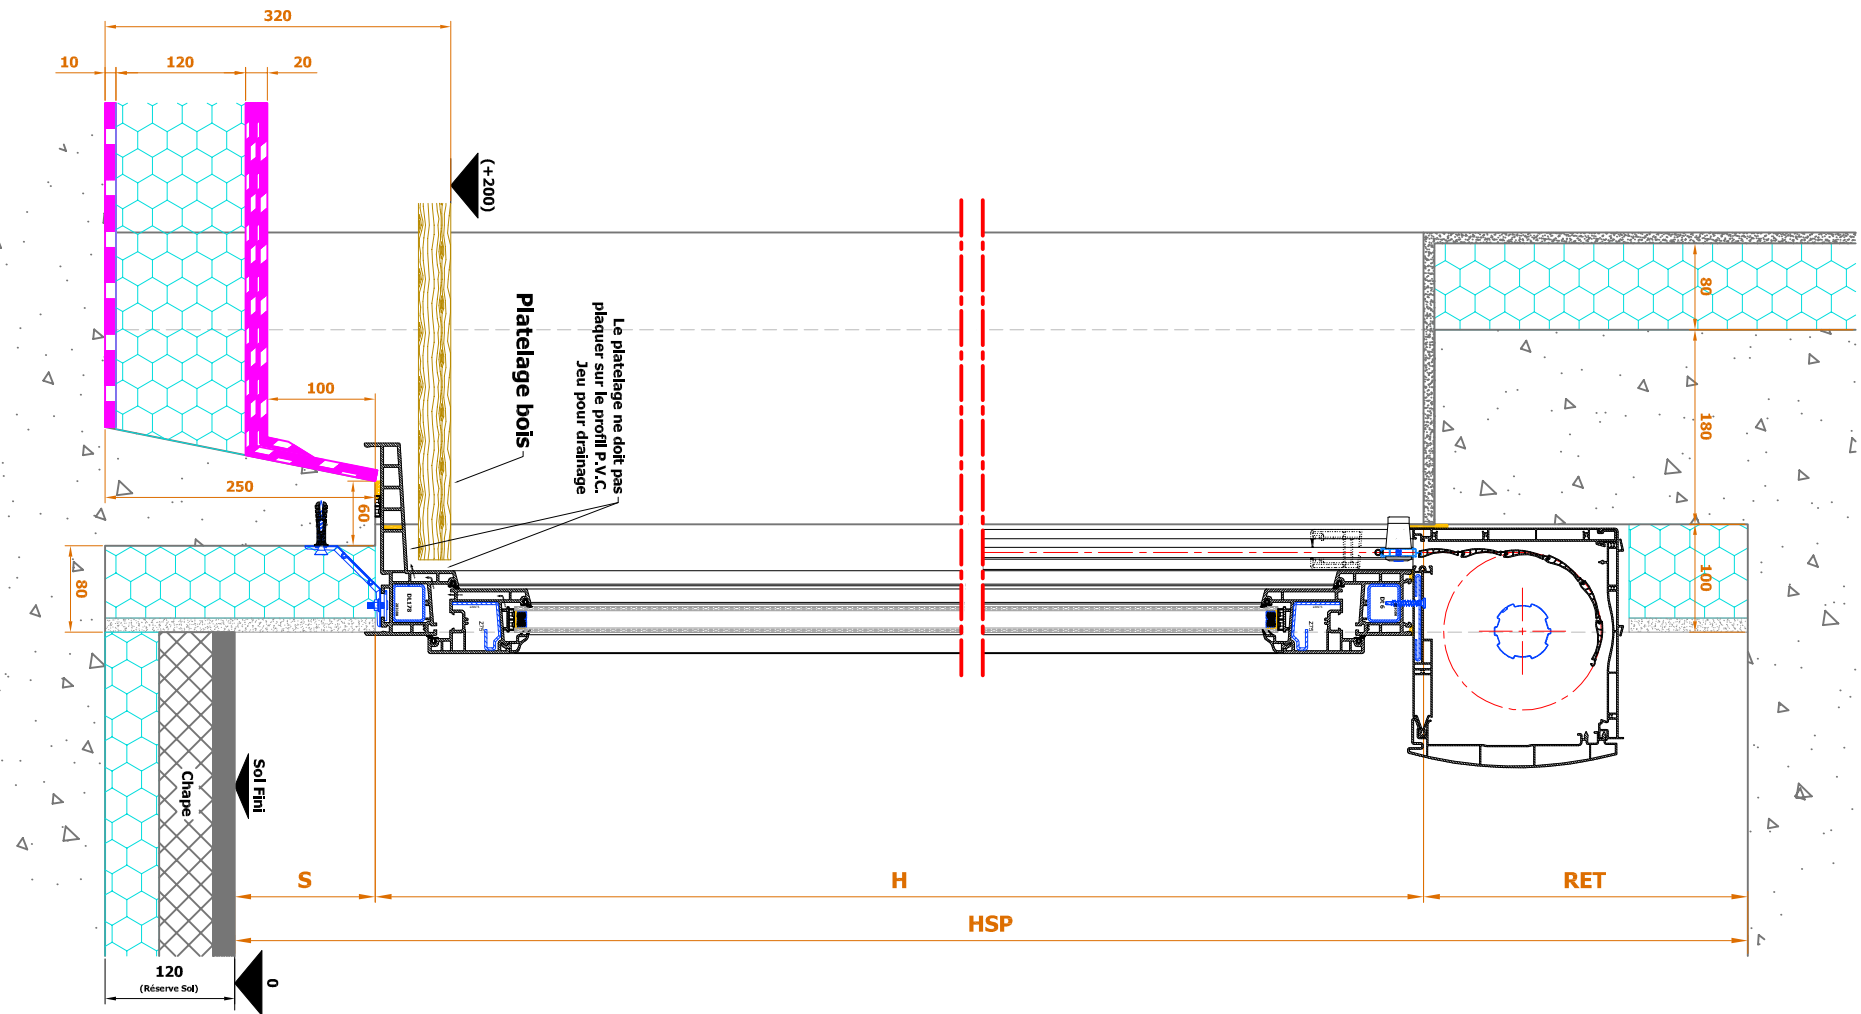


Lexique :
L : Largeur
H : Hauteur
S : Seuil
ALL : Allège
RET : Retombé de linteau
HSP : Hauteur Sous Plafond
HSD : Hauteur Sous Dalle
HSL : Hauteur Sous Linteau
AP : Axe de Poignée
A : Entraxe
AM : Axe du Meneau
AT : Axe de la Traverse
LO : Largeur hors tout Ouvrant
HO : Hauteur hors tout Ouvrant
AB : Axe de Battement d'ouvrant
PL : Passage Libre
CA : Cote Architecte

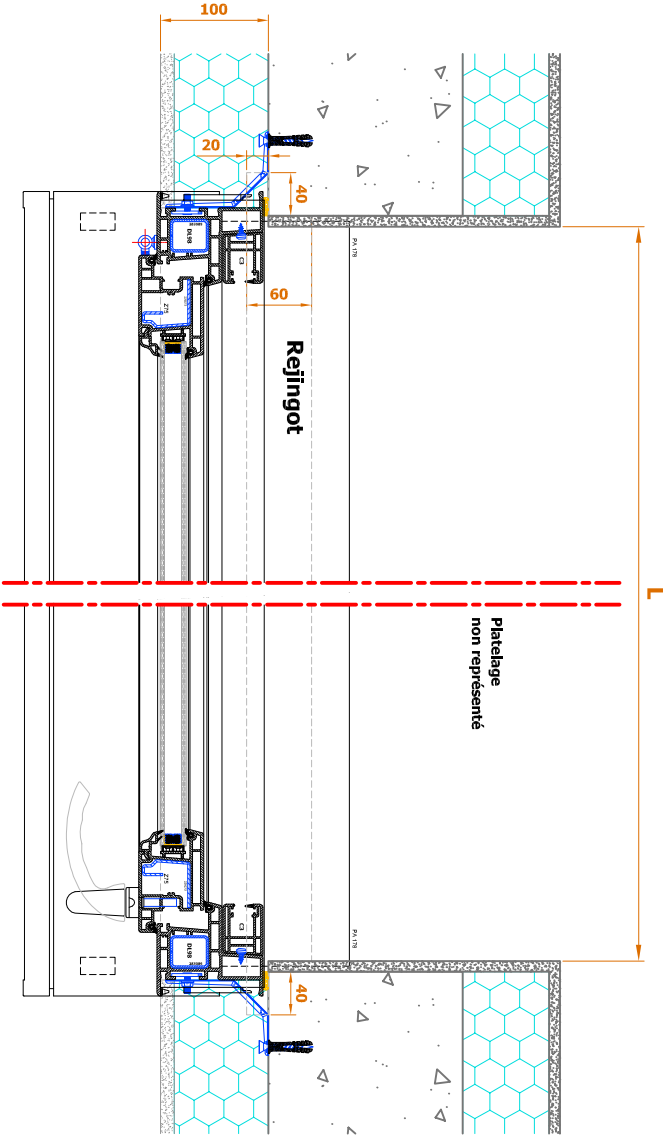

EXT

EXT

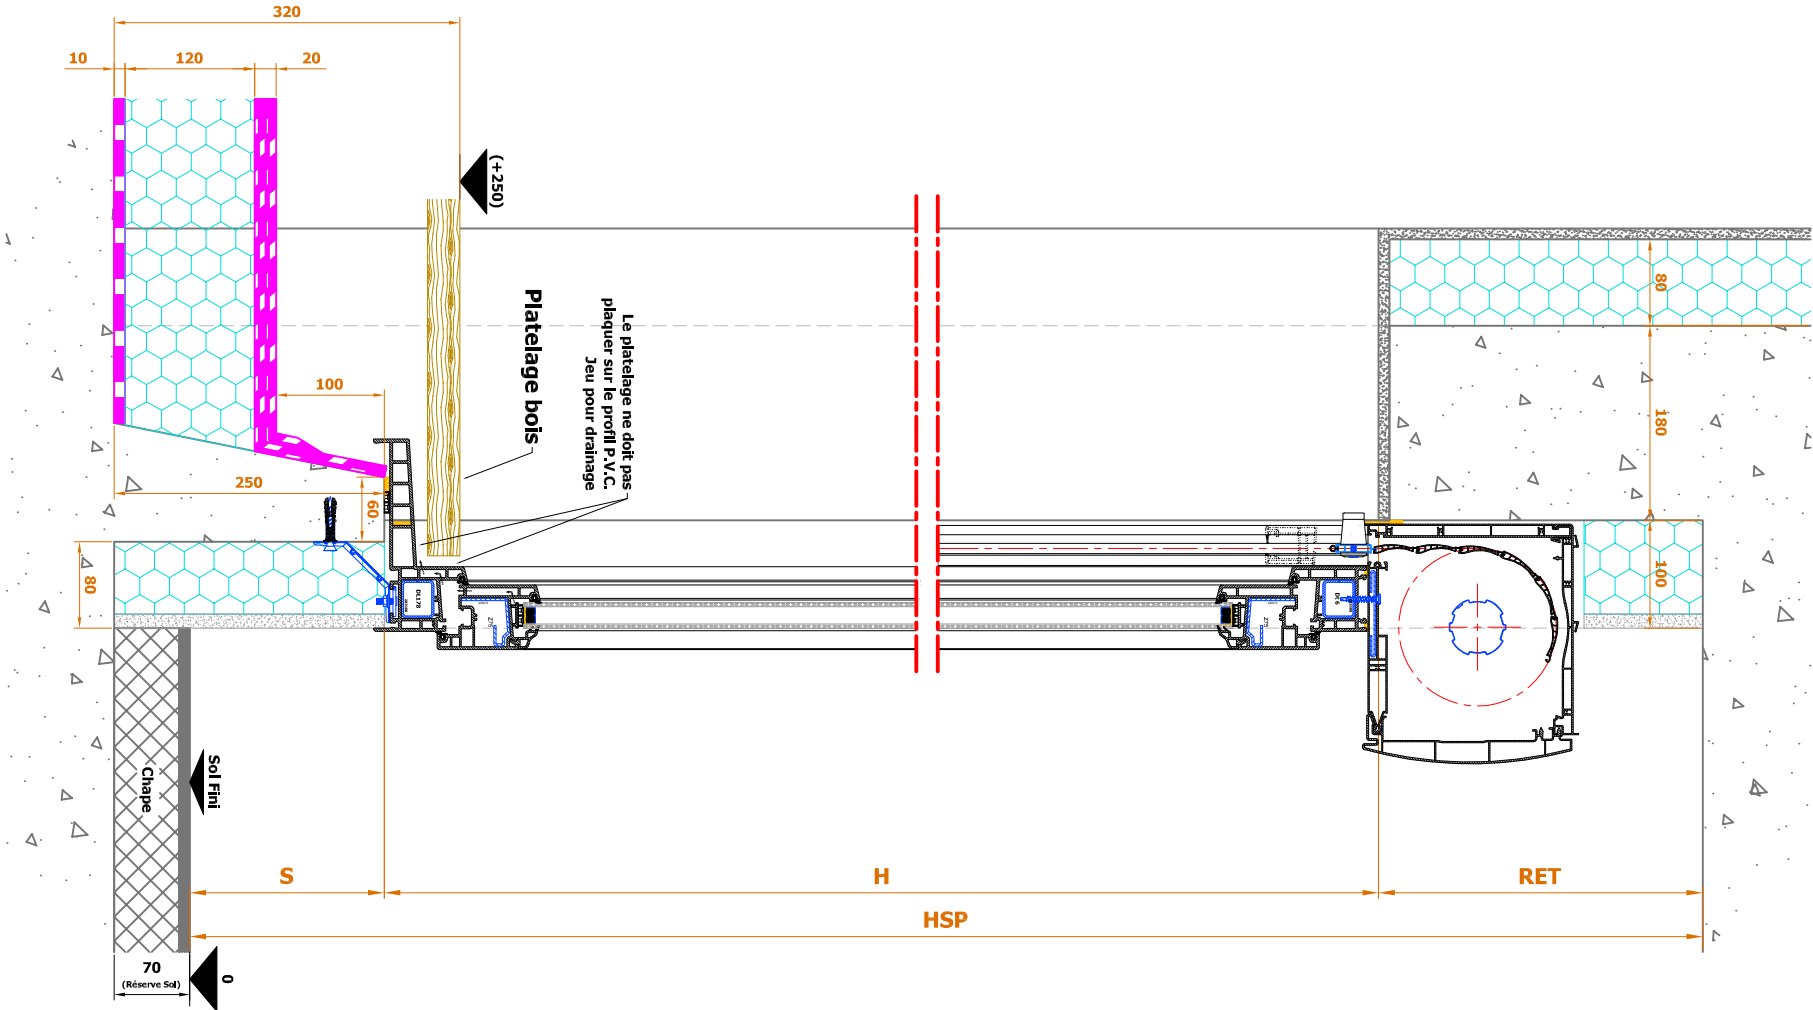

Lexique :
L : Largeur
H : Hauteur
S : Seuil
ALL : Allège
RET : Retombé de linteau
HSP : Hauteur Sous Plafond
HSD : Hauteur Sous Dalle
HSL : Hauteur Sous Linteau
AP : Axe de Poignée
A : Entraxe
AM : Axe du Meneau
AT : Axe de la Traverse
LO : Largeur hors tout Ouvrant
HO : Hauteur hors tout Ouvrant
AB : Axe de Battement d'ouvrant
PL : Passage Libre
CA : Cote Architecte