

**- LE 180 BAT A ET B-
CHEMIN DES FONTANIERES
69530 LA MULATIERE**

**MAITRE D'OUVRAGE
NOAHO**

**ARCHITECTE
ATELIER DE LA PASSERELLE**

**BUREAU DE CONTROLE
VERITAS**

**ECONOMISTE
EXECO**


LOT N° 06 : ETANCHEITE



S.I.E.
Service Industrie Etanchéité


Z.I. - Les Bords du Rhône
2, Boulevard Lucien Sampaix
BP 24 - 69191 ST-FONS

Tél : 04.72.89.12.29
Fax : 04.78.67.70.10
E-mail:
accueil@sie-etancheite.fr

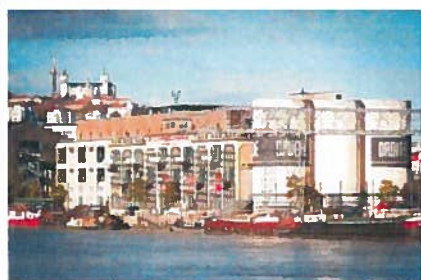

Indice	Date	Modifications	CARNET DE DETAILS		Phase
IND 0	02/09/2015	Diffusion provisoire			EXE
					N° Affaire
					2015/136
					N° Plan
					ETA
			Echelle	Date	02.06
			1/...	02/09/2015	

- Pare Vapeur soudé sur E.I.F
 - Isolant mousse PU ep:200mm R=8.70m².K/W
 - Etanchéité bicouche sur voile de verre
 - Protection par gravillons
- Equerre de renfort
 - Relevé d'étanchéité élastomère
 - Solin + joint mastic

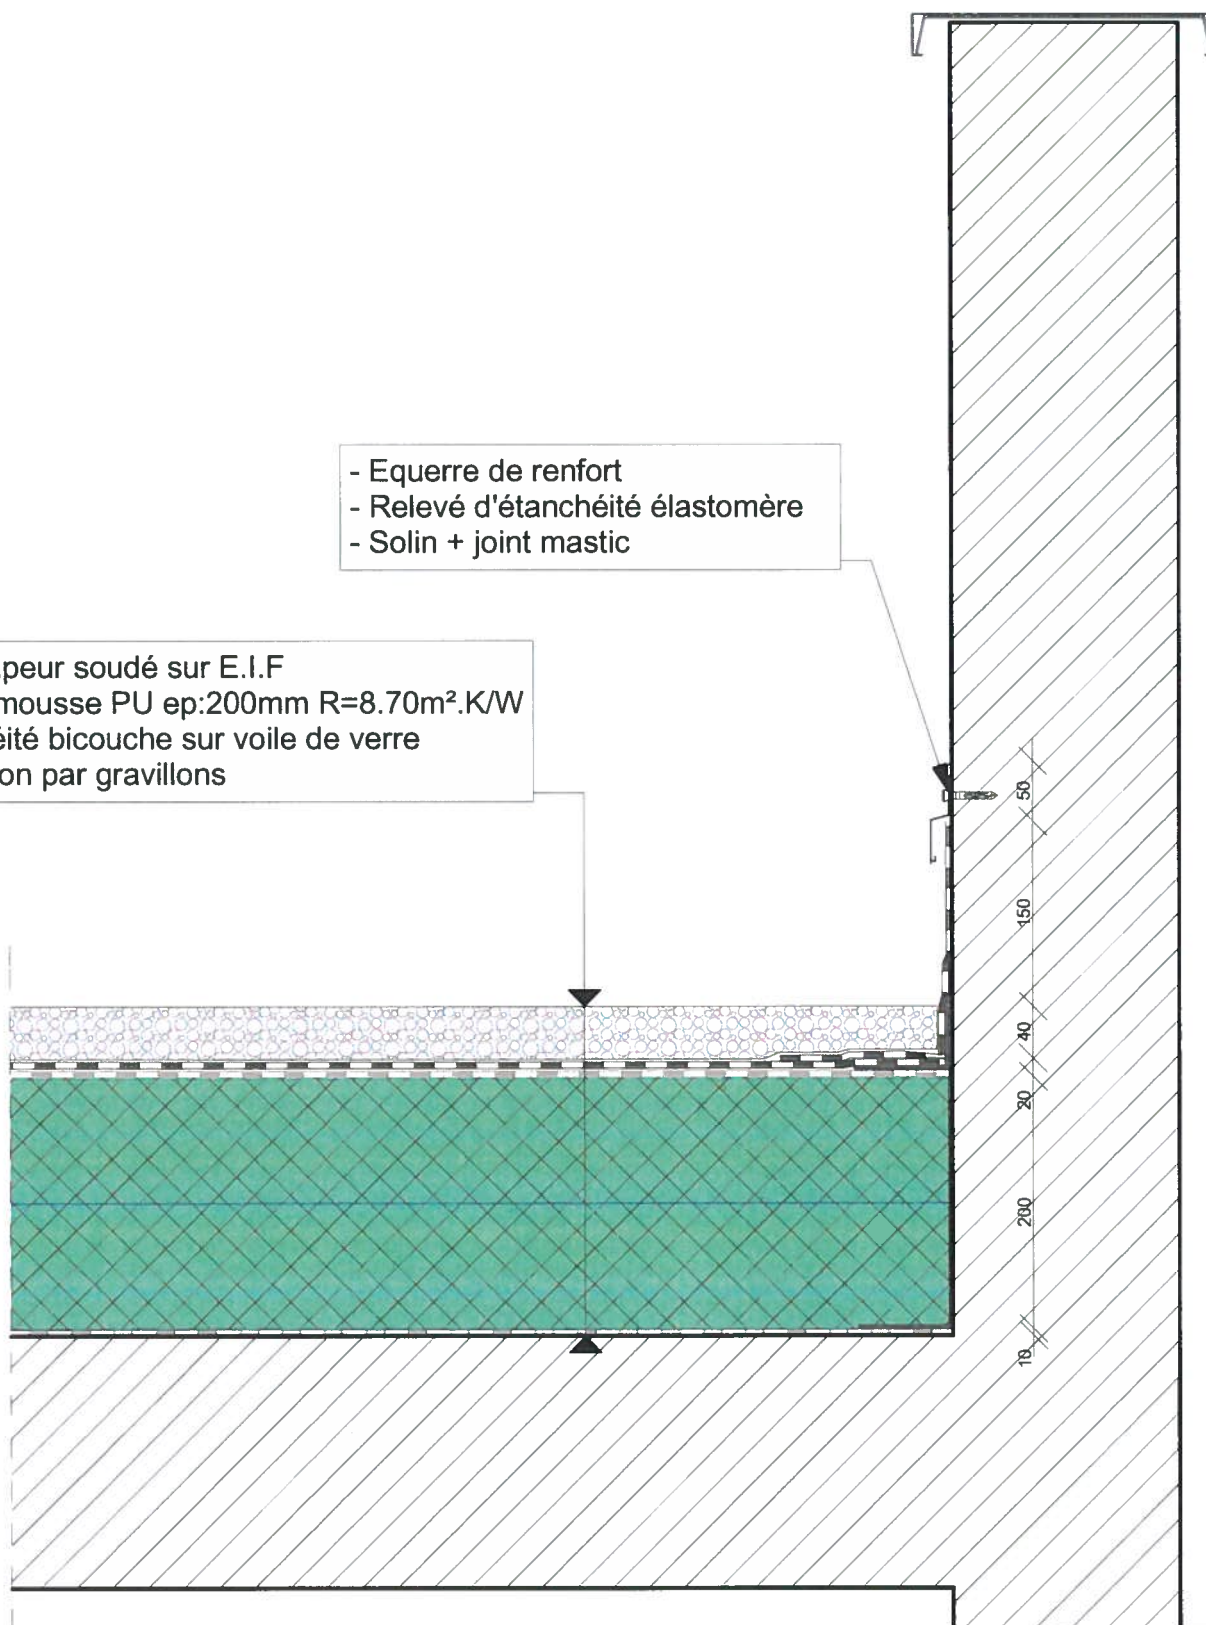

Affaire : LE 180 BAT A ET B - 69350 LA MULATIERE - NOAHO

PHASE		INTITULE		Echelle		Référence Projet: 2015/353	
EXE		RELEVÉ CONTRE ACROTERE TERRASSE INACCESSIBLE		1/5		DATE DOCUMENT: 02 Septembre 2015	
				LOT		LOCALISATION	INDICE
				06		Détail 1	1




S.I.E
Service Industrie Etanchéité

Tél : 04.72.89.12.29
Fax : 04.78.67.70.10
Z.I. - Les Bords du Rhône
2, Boulevard Lucien Sampaix
BP 24 - 69191 ST-FONS


Dessin : R.Lambert
etudes@sie-etancheite.fr
Les informations techniques contenues
dans ce document
sont la propriété exclusive de SIE

- Equerre de renfort
- Relevé d'étanchéité élastomère
- Solin + joint mastic

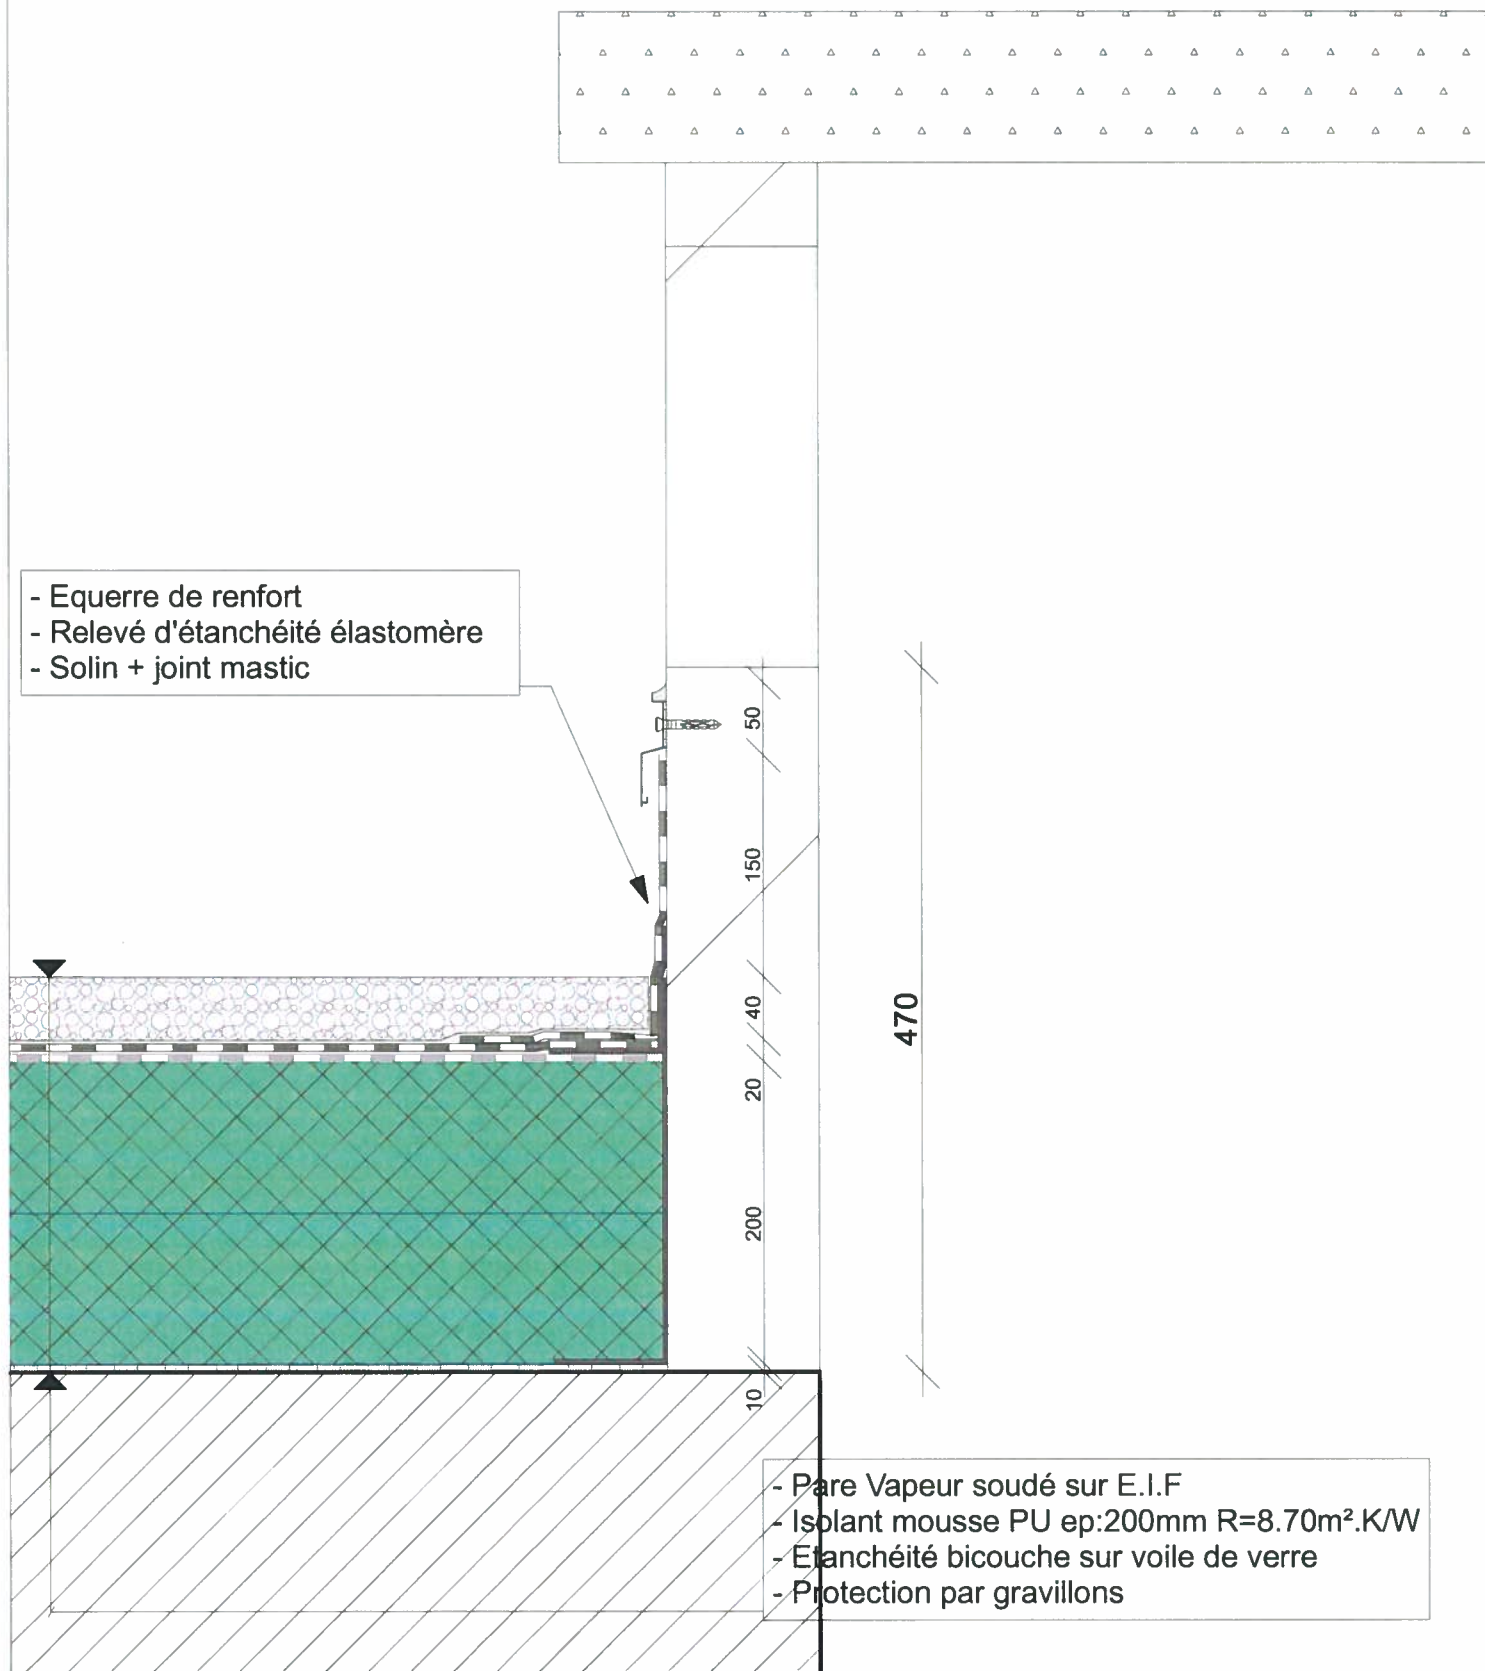


- Pare Vapeur soudé sur E.I.F
- Isolant mousse PU ep:200mm R=8.70m².K/W
- Etanchéité bicouche sur voile de verre
- Protection par gravillons

Affaire : LE 180 BAT A ET B - 69350 LA MULATIERE - NOAHO

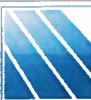		Référence Projet: 2015/353				
PHASE EXE	INTITULE RELEVÉ CONTRE SOUCHE	ECHELLE 1/5	DATE DOCUMENT: 02 Septembre 2015			
		LOT	LOCALISATION	INDICE		
 S.I.E. Service Industrie Etanchéité		Tél : 04.72.89.12.29 Fax : 04.78.67.70.10 Z.I. - Les Bords du Rhône 2, Boulevard Lucien Sampaix BP 24 - 69191 ST-FONS	Dessin : R.Lambert etudes@sie-etancheite.fr Les informations techniques contenues dans ce document sont la propriété exclusive de SIE	06	Détail 2	1

- Lanterneau de désenfumage type ECOFEU
- Lanterneau d'accès type ECOLUX

- Pare Vapeur soudé sur E.I.F
- Isolant mousse PU ep:200mm R=8.70m².K/W
- Etanchéité bicouche sur voile de verre
- Protection par gravillons

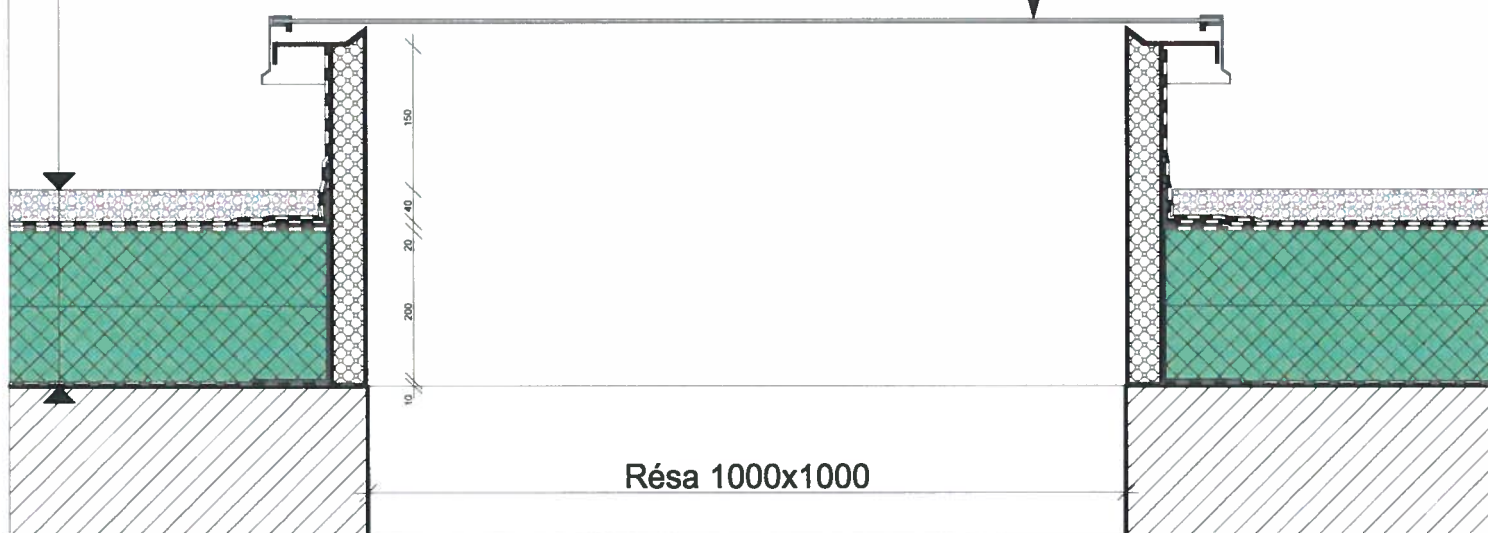


Affaire : LE 180 BAT A ET B - 69350 LA MULATIERE - NOAHO

		Référence Projet: 2015/353				
PHASE EXE	INTITULE RELEVÉ CONTRE LANTERNEAU	ECHELLE 1/5	DATE DOCUMENT: 02 Septembre 2015			
		LOT	LOCALISATION	INDICE		
 S.I.E. Service Industrie Etanchéité		Tél : 04.72.89.12.29 Fax : 04.78.67.70.10 Z.I. - Les Bords du Rhône 2, Boulevard Lucien Sampaix BP 24 - 69191 ST-FONS	Dessin : R.Lambert etudes@sie-etancheite.fr Les informations techniques contenues dans ce document sont la propriété exclusive de SIE	06	Détail 3	1

- Pare Vapeur soudé sur E.I.F
- Isolant mousse PU ep:120mm R=5.20m².K/W
- Etanchéité bicouche sur voile de verre
- Lame bois composite sur plots et lambourdes

- Costière métallique pour JD
- Protection par solin + joint mastic


- Equerre de renfort
- Relevé d'étanchéité élastomère

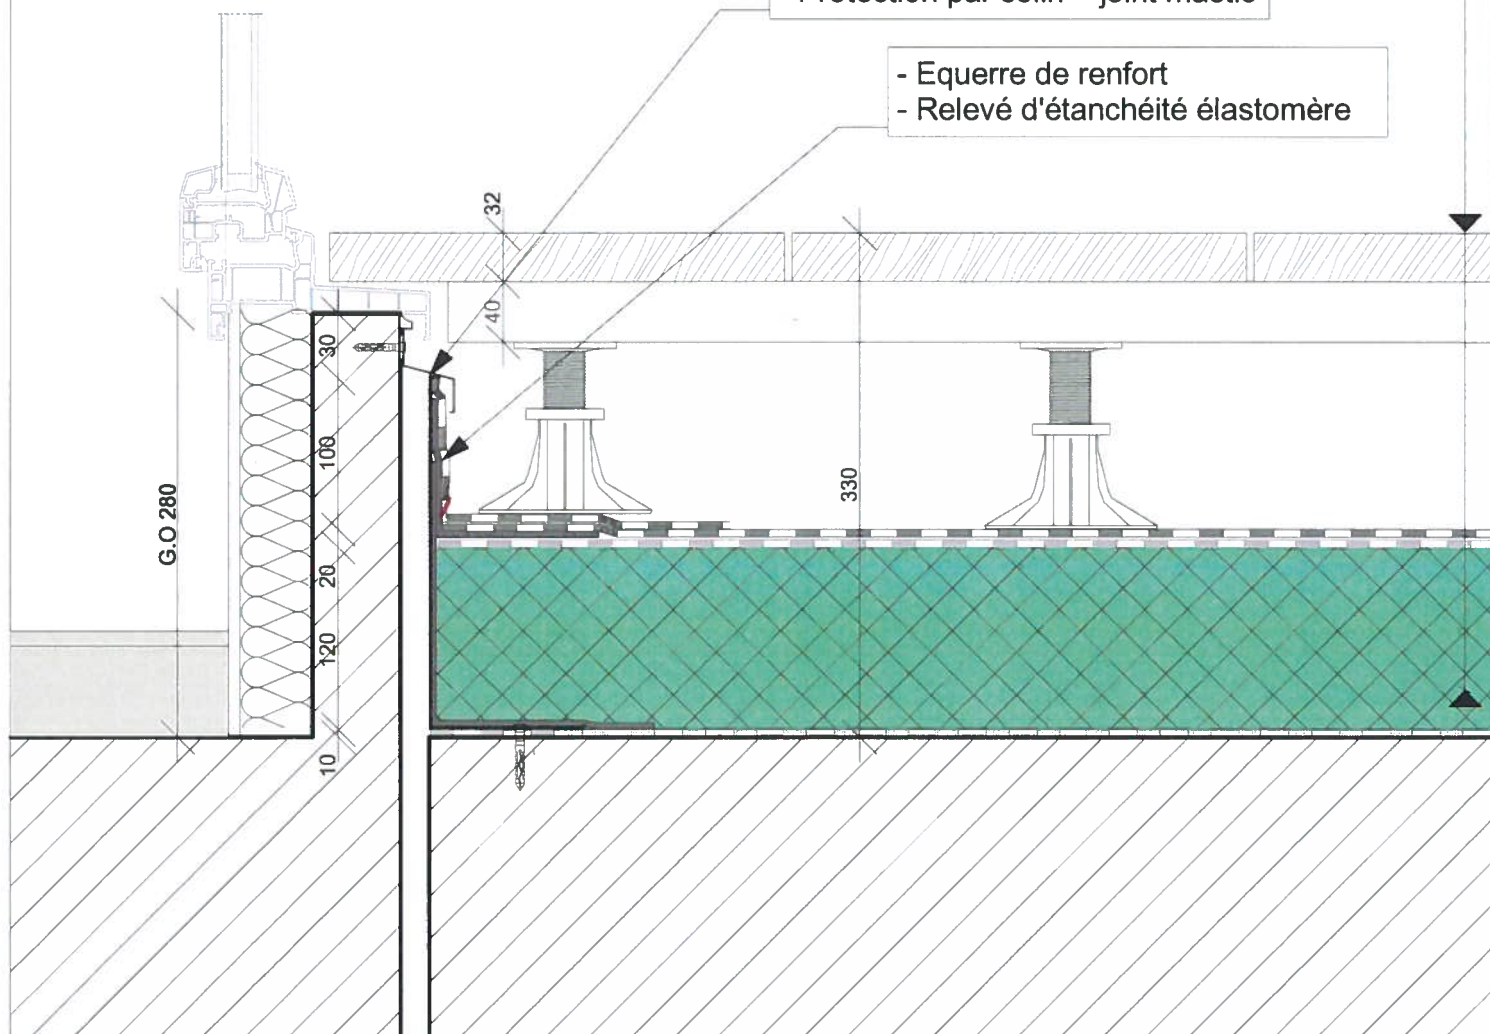

Affaire : LE 180 BAT A ET B - 69350 LA MULATIERE - NOAHO

PHASE		INTITULE		Echelle		Référence Projet: 2015/353	
EXE		RELEVÉ CONTRE SOUCHE		1/5		DATE DOCUMENT: 02 Septembre 2015	
				LOT		LOCALISATION	
				06		Détail 4.1	
						INDICE	
						1	

- Pare Vapeur soudé sur E.I.F
- Isolant mousse PU ep:120mm R=5.20m².K/W
- Etanchéité bicouche sur voile de verre
- Lame bois composite sur plots et lambourdes

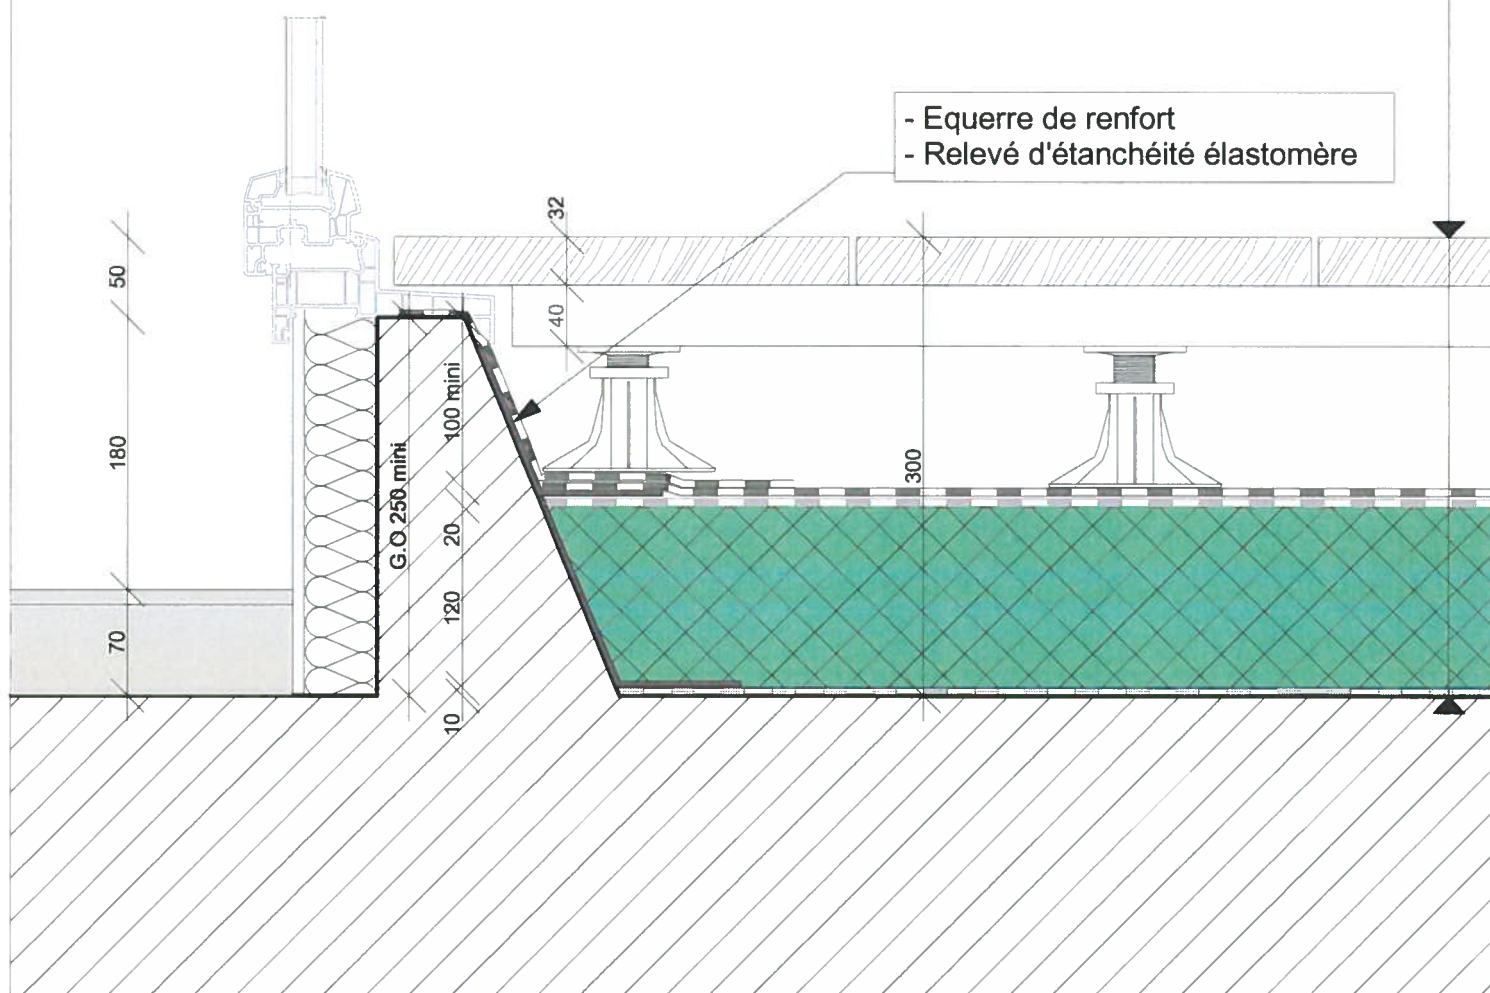


- Equerre de renfort
- Relevé d'étanchéité élastomère

Affaire : LE 180 BAT A ET B - 69350 LA MULATIERE - NOAHO


		Référence Projet: 2015/353	
PHASE	INTITULE	ECHELLE	DATE DOCUMENT:
EXE	RELEVÉ CONTRE SOUCHE	1/5	02 Septembre 2015
		LOT	LOCALISATION
		06	Détail 4.2
			1

	S.I.E. Service Industrie Etanchéité	Tél : 04.72.89.12.29 Fax : 04.78.67.70.10 Z.I. - Les Bords du Rhône 2, Boulevard Lucien Sampaix BP 24 - 69191 ST-FONS	Dessin : R.Lambert etudes@sie-etancheite.fr Les informations techniques contenues dans ce document sont la propriété exclusive de SIE
--	---	---	---

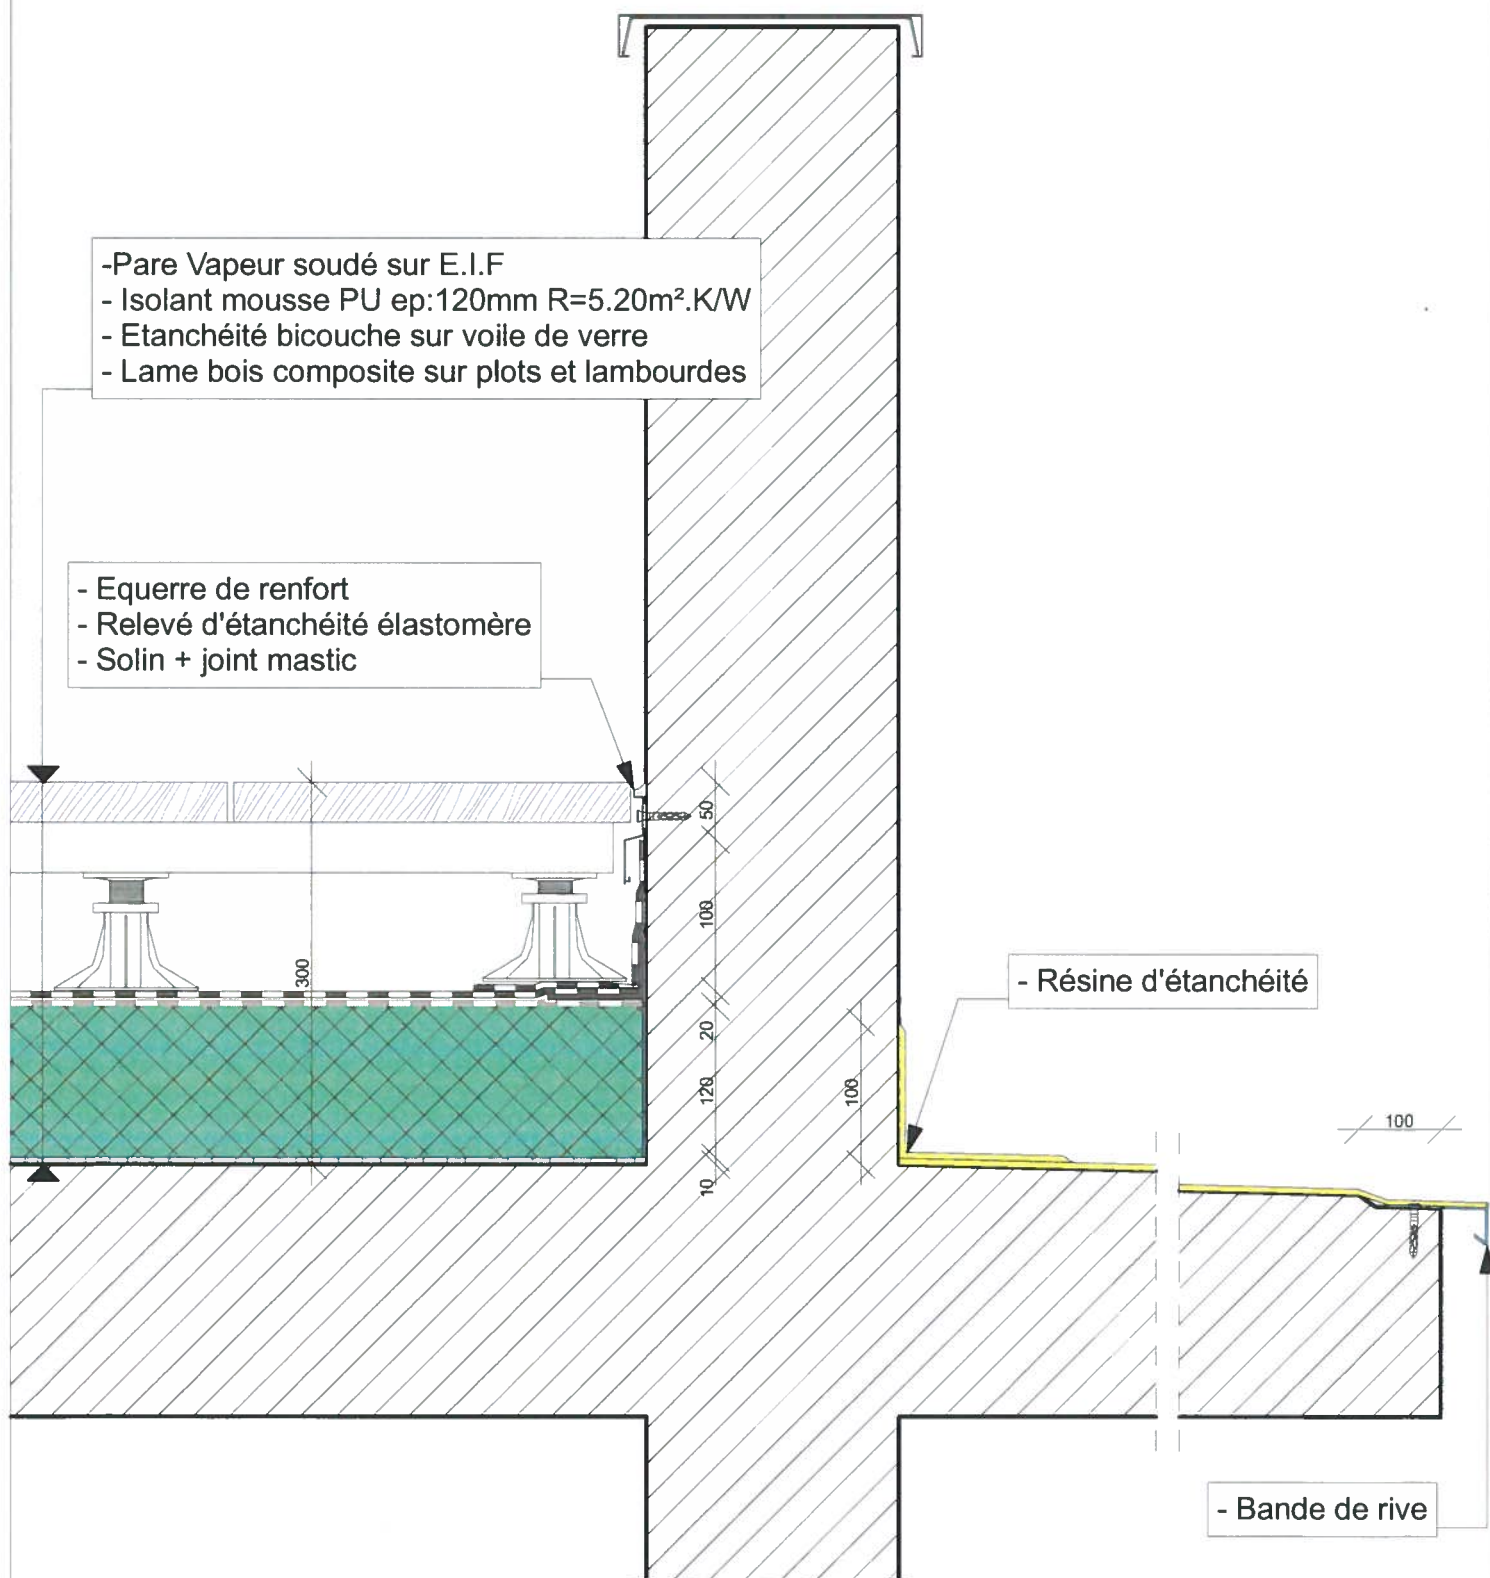

Affaire : LE 180 BAT A ET B - 69350 LA MULATIERE - NOAHO

		Référence Projet: 2015/353		
PHASE	INTITULE	ECHELLE	DATE DOCUMENT:	
EXE	RELEVÉ CONTRE ACROTERE TERRASSE ACCESSIBLE + CASQUETTE	1/5	02 Septembre 2015	
		LOT	LOCALISATION	INDICE
 S.I.E. Service Industrie Etanchéité		Tél : 04.72.89.12.29 Fax : 04.78.67.70.10 Z.I. - Les Bords du Rhône 2, Boulevard Lucien Sampaix BP 24 - 69191 ST-FONS		Dessin : R.Lambert etudes@sie-etancheite.fr Les informations techniques contenues dans ce document sont la propriété exclusive de SIE
		06	Détail 5.1	1

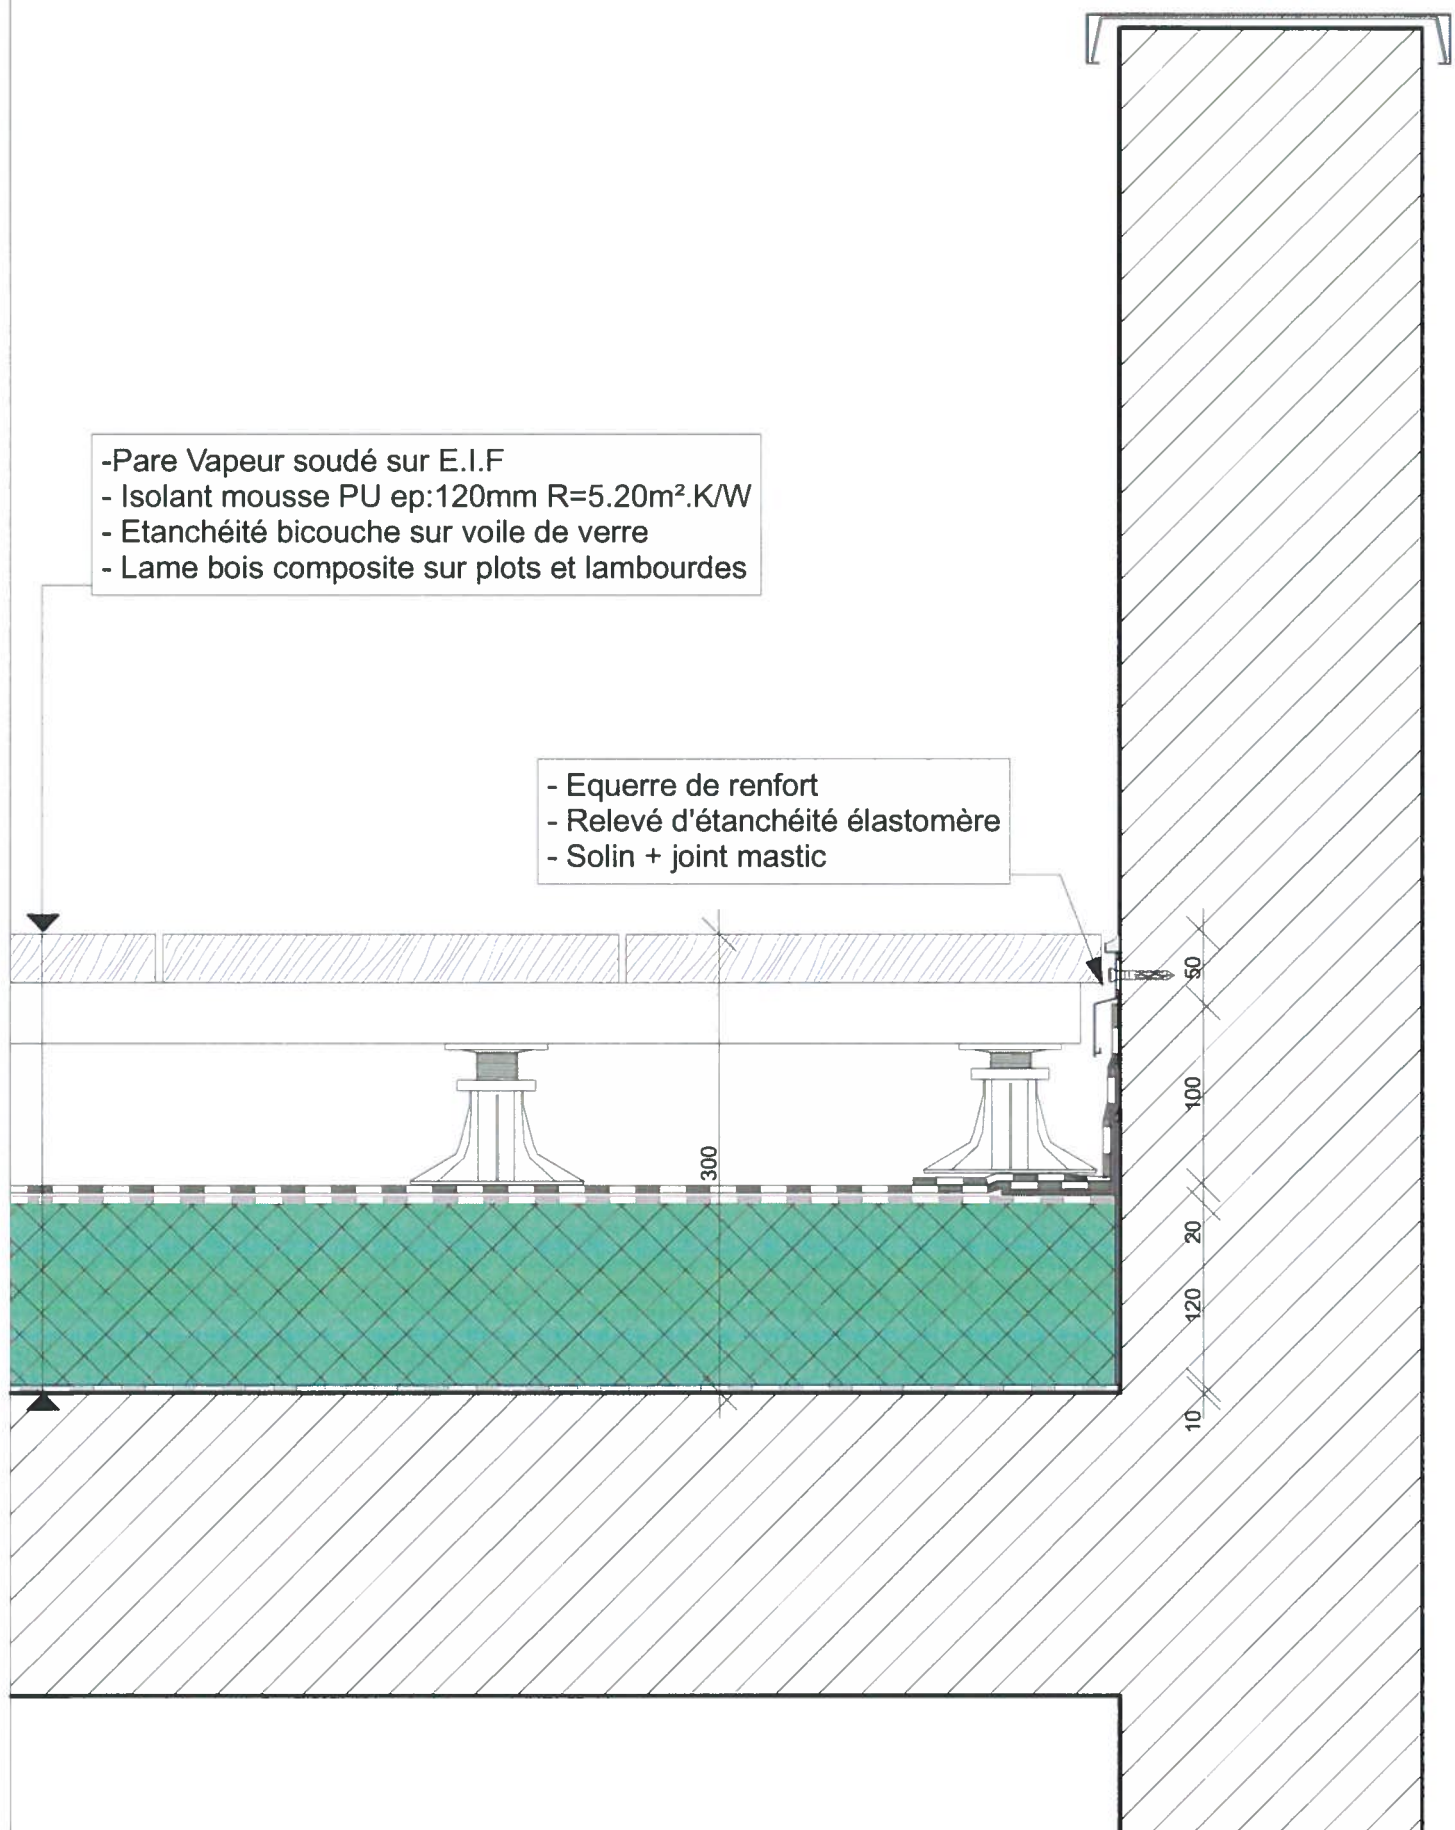

Affaire : LE 180 BAT A ET B - 69350 LA MULATIERE - NOAHO


PHASE EXE		INTITULE RELEVÉ CONTRE ACROTERE TERRASSE ACCESSIBLE	Référence Projet: 2015/353	
			ECHELLE 1/5	DATE DOCUMENT: 02 Septembre 2015
			LOT	LOCALISATION
			06	Détail 5.2
				1

- Pare Vapeur soudé sur E.I.F
- Isolant mousse PU ep:120mm R=5.20m².K/W
- Etanchéité bicouche sur voile de verre
- Lame bois composite sur plots et lambourdes

- Pare Vapeur soudé sur E.I.F
- Isolant mousse PU ep:200mm R=8.70m².K/W
- Etanchéité bicouche traité antiracine sur voile de verre
- Protection par végétalisation


- Equerre de renfort
- Relevé d'étanchéité élastomère
- Solin + joint mastic

- Equerre de renfort
- Relevé d'étanchéité ardoisé
- Solin + joint mastic

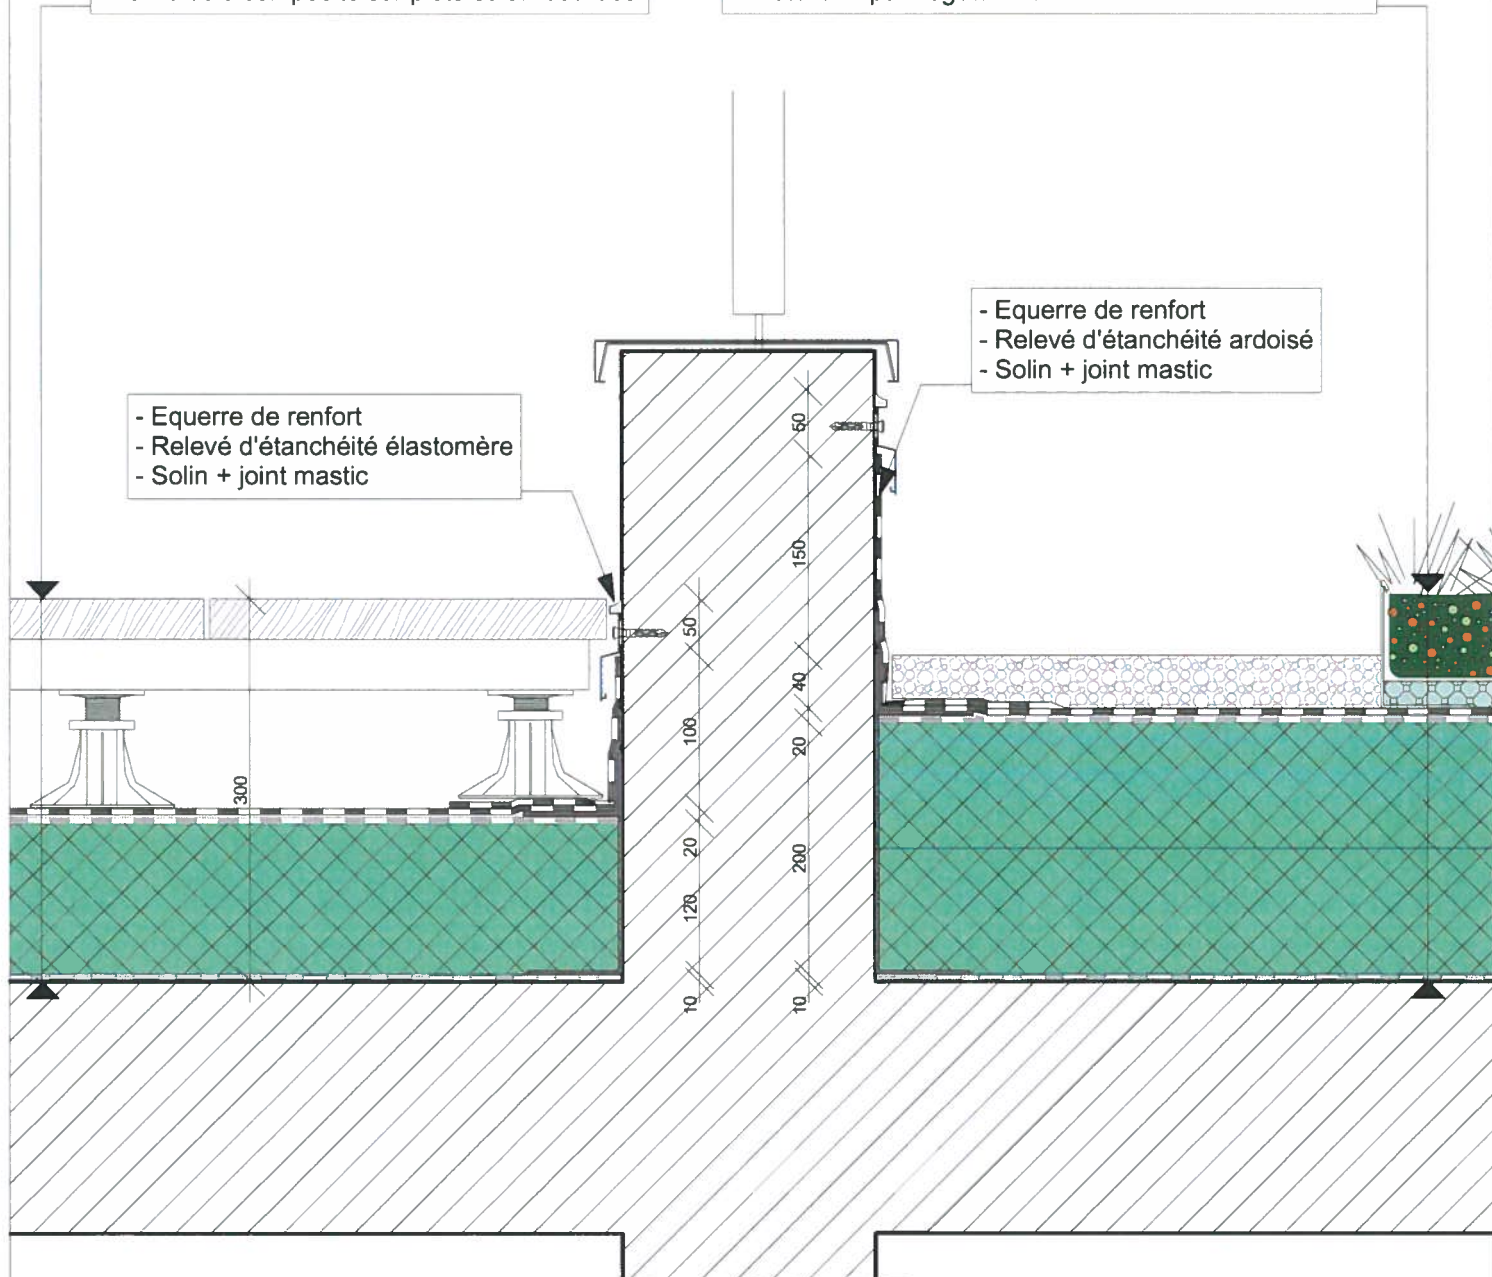

Affaire : LE 180 BAT A ET B - 69350 LA MULATIERE - NOAHO

PHASE		INTITULE		Echelle		Référence Projet: 2015/353	
EXE		RELEVÉ SUR MURET ENTRE TERRASSE ACCESSIBLE ET VÉGÉTALISÉE		1/5		DATE DOCUMENT: 02 Septembre 2015	
				LOT		LOCALISATION	INDICE
				06		Détail 6	1

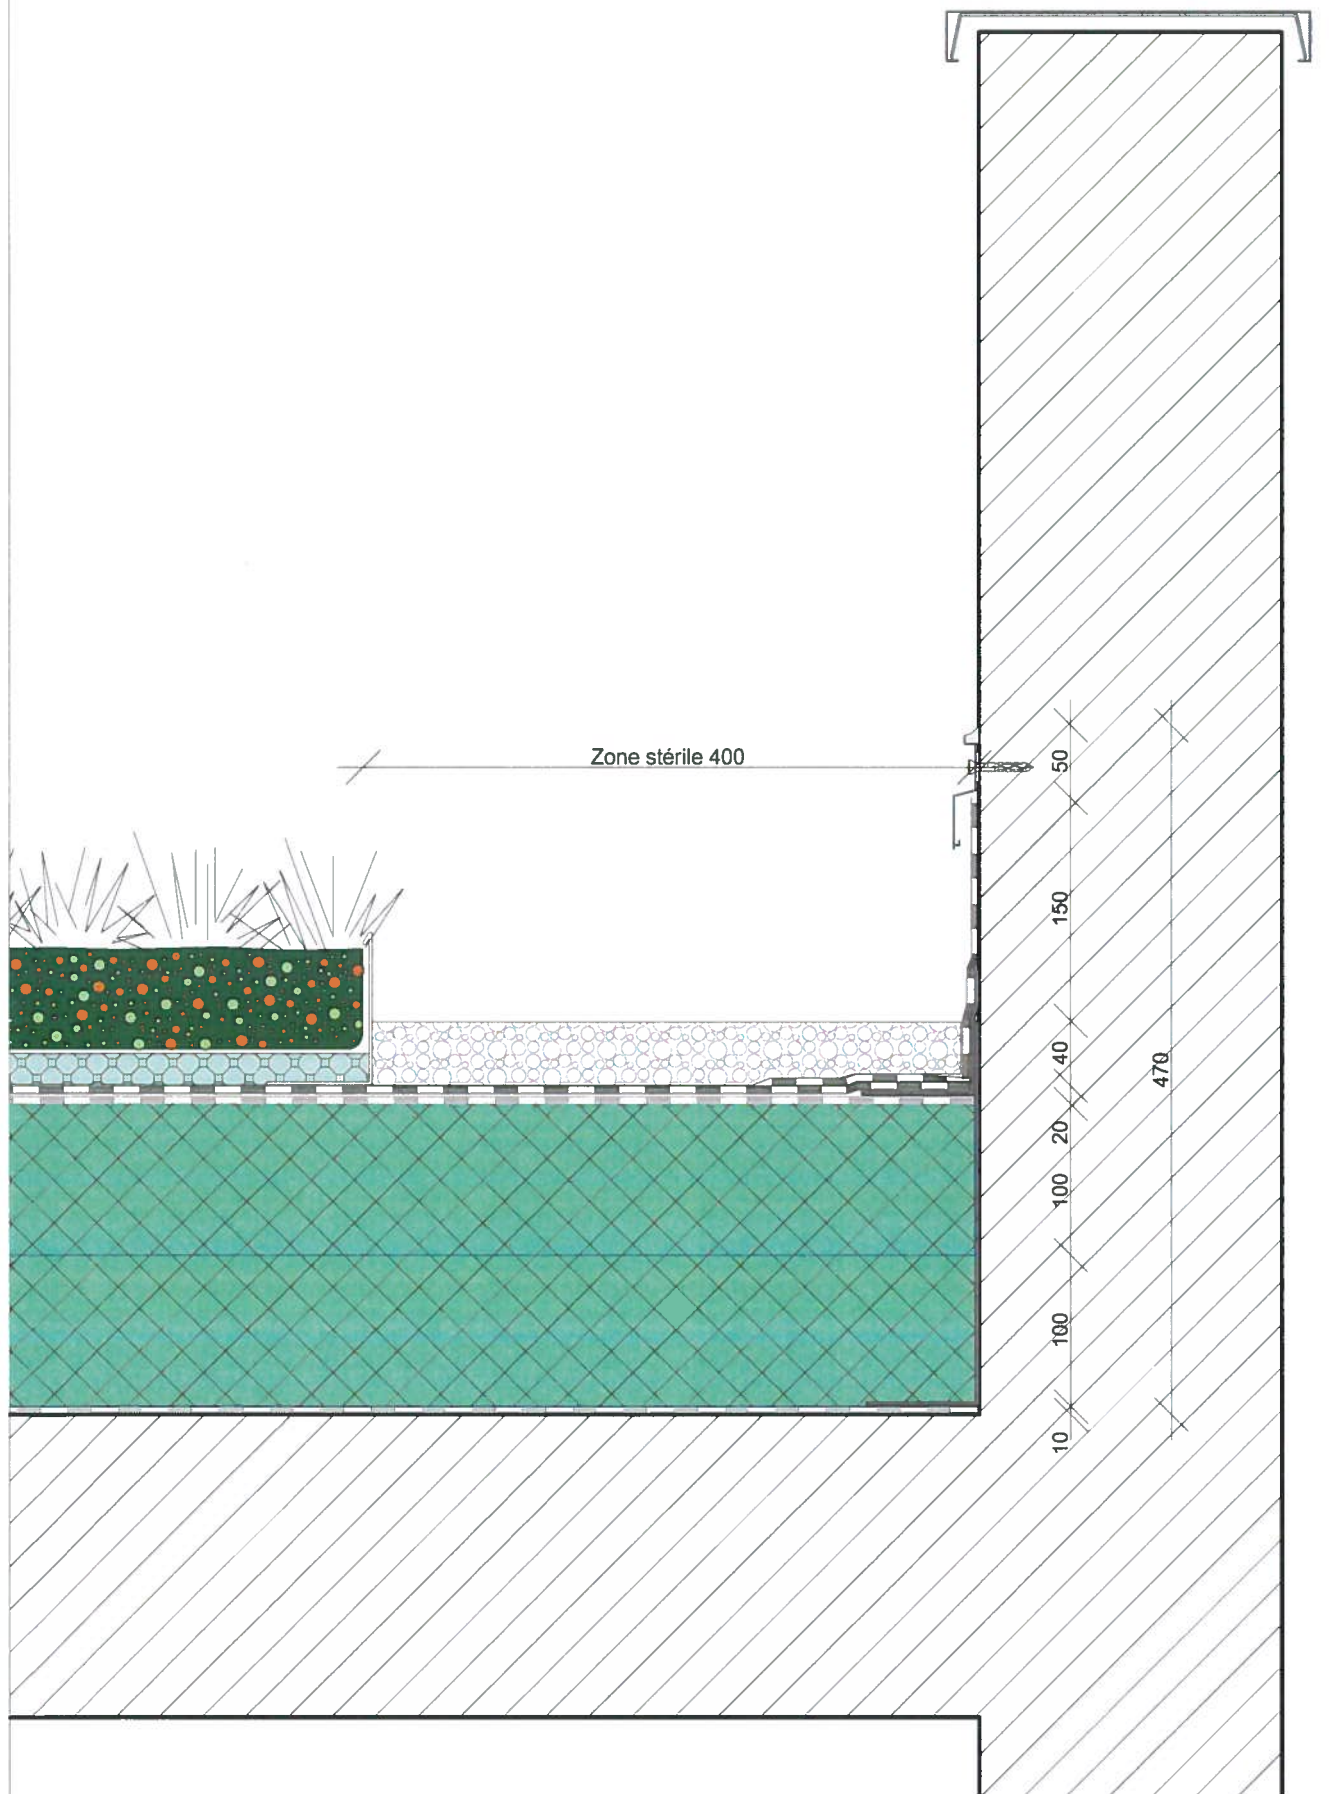

Affaire : LE 180 BAT A ET B - 69350 LA MULATIERE - NOAHO

PHASE		INTITULE		Echelle		Référence Projet: 2015/353	
EXE		RELEVÉ SUR ACROTERE TERRASSE VEGETALISEE		1/5		DATE DOCUMENT: 02 Septembre 2015	
				LOT		LOCALISATION	INDICE
				06		Détail 7	1




Tél : 04.72.89.12.29
Fax : 04.78.67.70.10
Z.I. - Les Bords du Rhône
2, Boulevard Lucien Sampaix
BP 24 - 69191 ST-FONS

Dessin : R.Lambert
etudes@sie-etanchette.fr
Les informations techniques contenues
dans ce document
sont la propriété exclusive de SIE


- Pare Vapeur soudé sur E.I.F
- Isolant mousse PU ep:200mm R=8.70m².K/W
- Etanchéité bicouche sur voile de verre
- Protection par gravillons

- Equerre de renfort
- Relevé d'étanchéité élastomère
- Solin + joint mastic

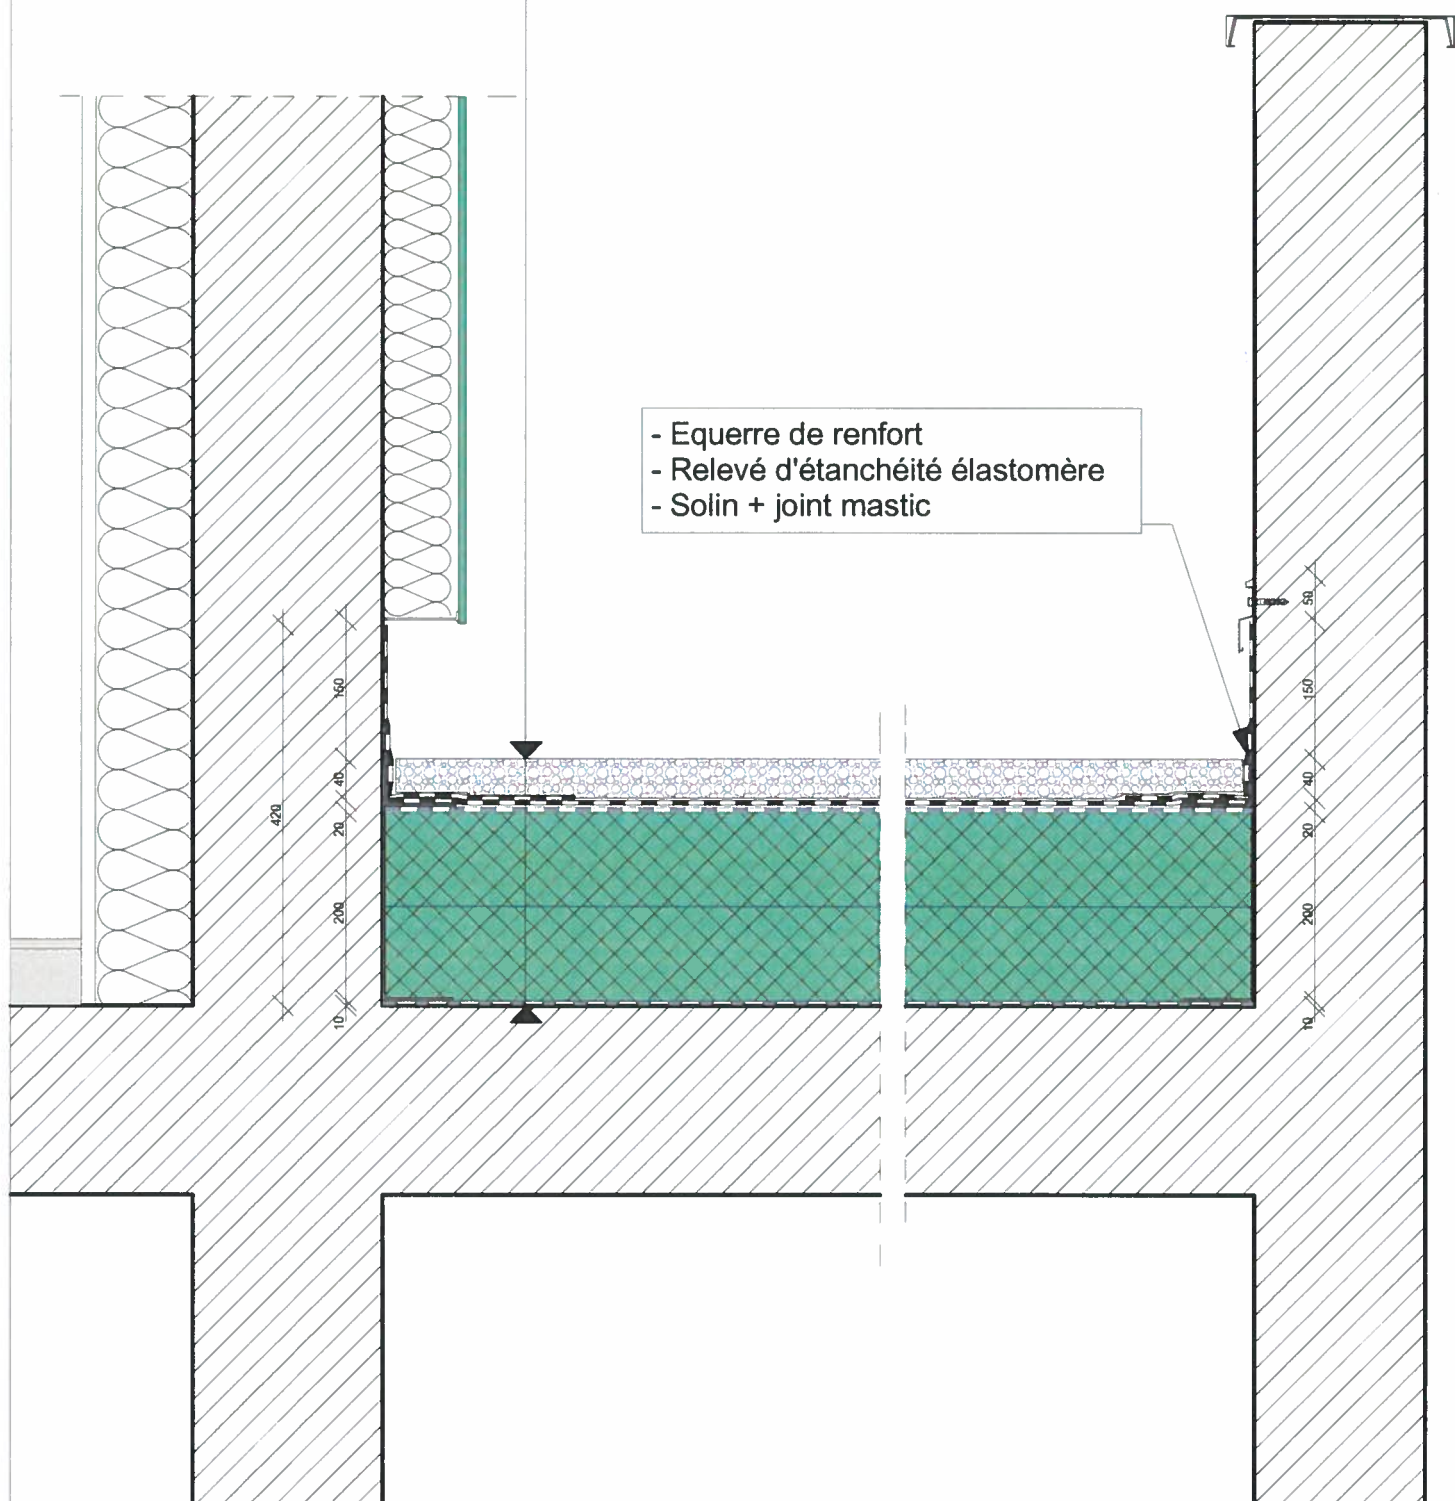

Affaire : LE 180 BAT A ET B - 69350 LA MULATIERE - NOAHO

PHASE		INTITULE		Référence Projet: 2015/353	
EXE		RELEVÉ SUR TERRASSE INACCESSIBLE R+2 ET R-4		DATE DOCUMENT: 02 Septembre 2015	
		ECHELLE		LOCALISATION	
		1/5		INDICE	
		LOT			
		06		Détail 8	
				1	

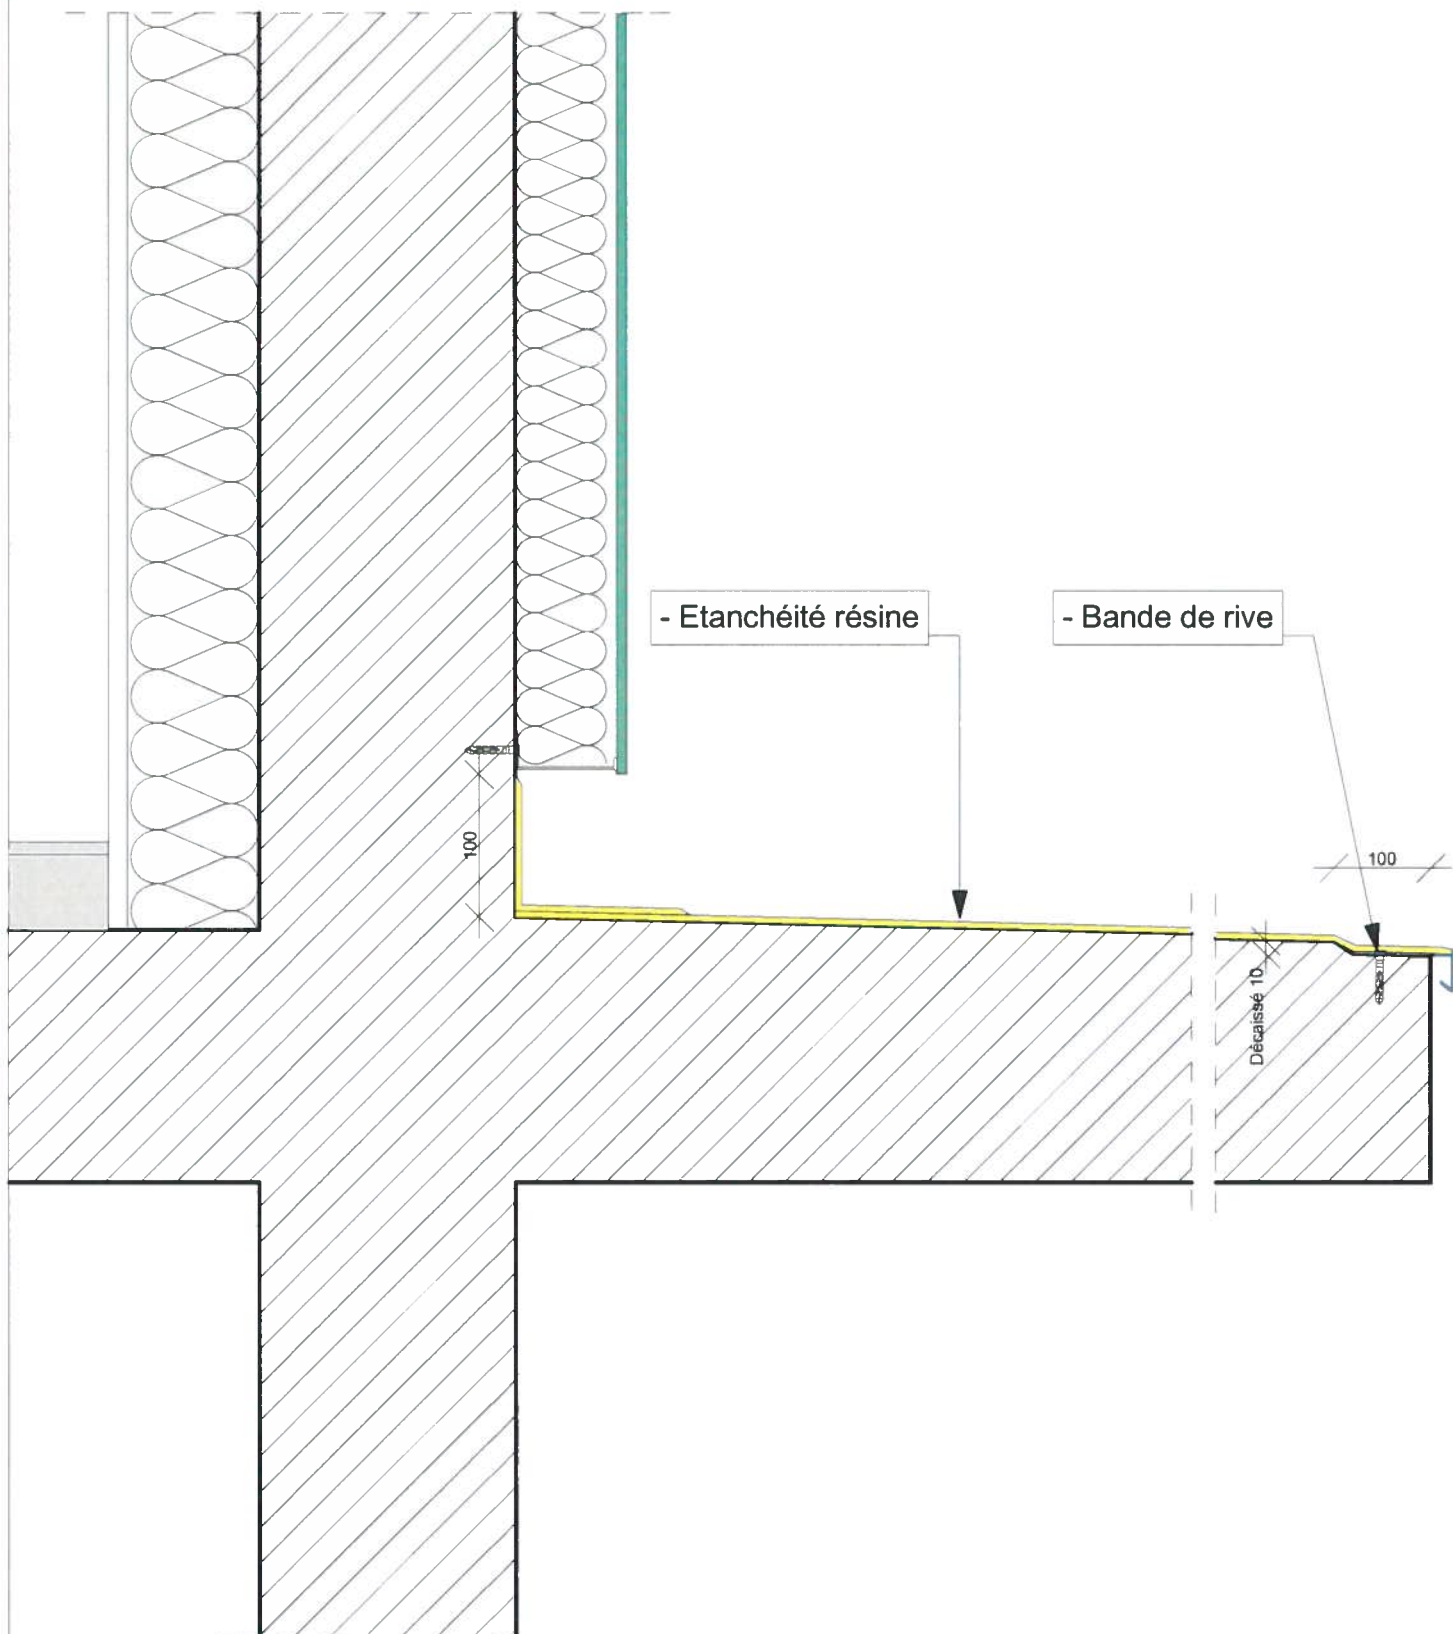


Affaire : LE 180 BAT A ET B - 69350 LA MULATIERE - NOAHO

PHASE		INTITULE		ECHELLE		Référence Projet: 2015/353	
EXE		RELEVÉ RESINE SUR FACADE		1/5		DATE DOCUMENT: 02 Septembre 2015	
				LOT		LOCALISATION	INDICE
				06		Détail 9	1



Tél : 04.72.89.12.29
Fax : 04.78.67.70.10
Z.I. - Les Bords du Rhône
2, Boulevard Lucien Sampaix
BP 24 - 69191 ST-FONS

Dessin : R. Lambert
etudes@sie-etancheite.fr
Les informations techniques contenues
dans ce document
sont la propriété exclusive de SIE

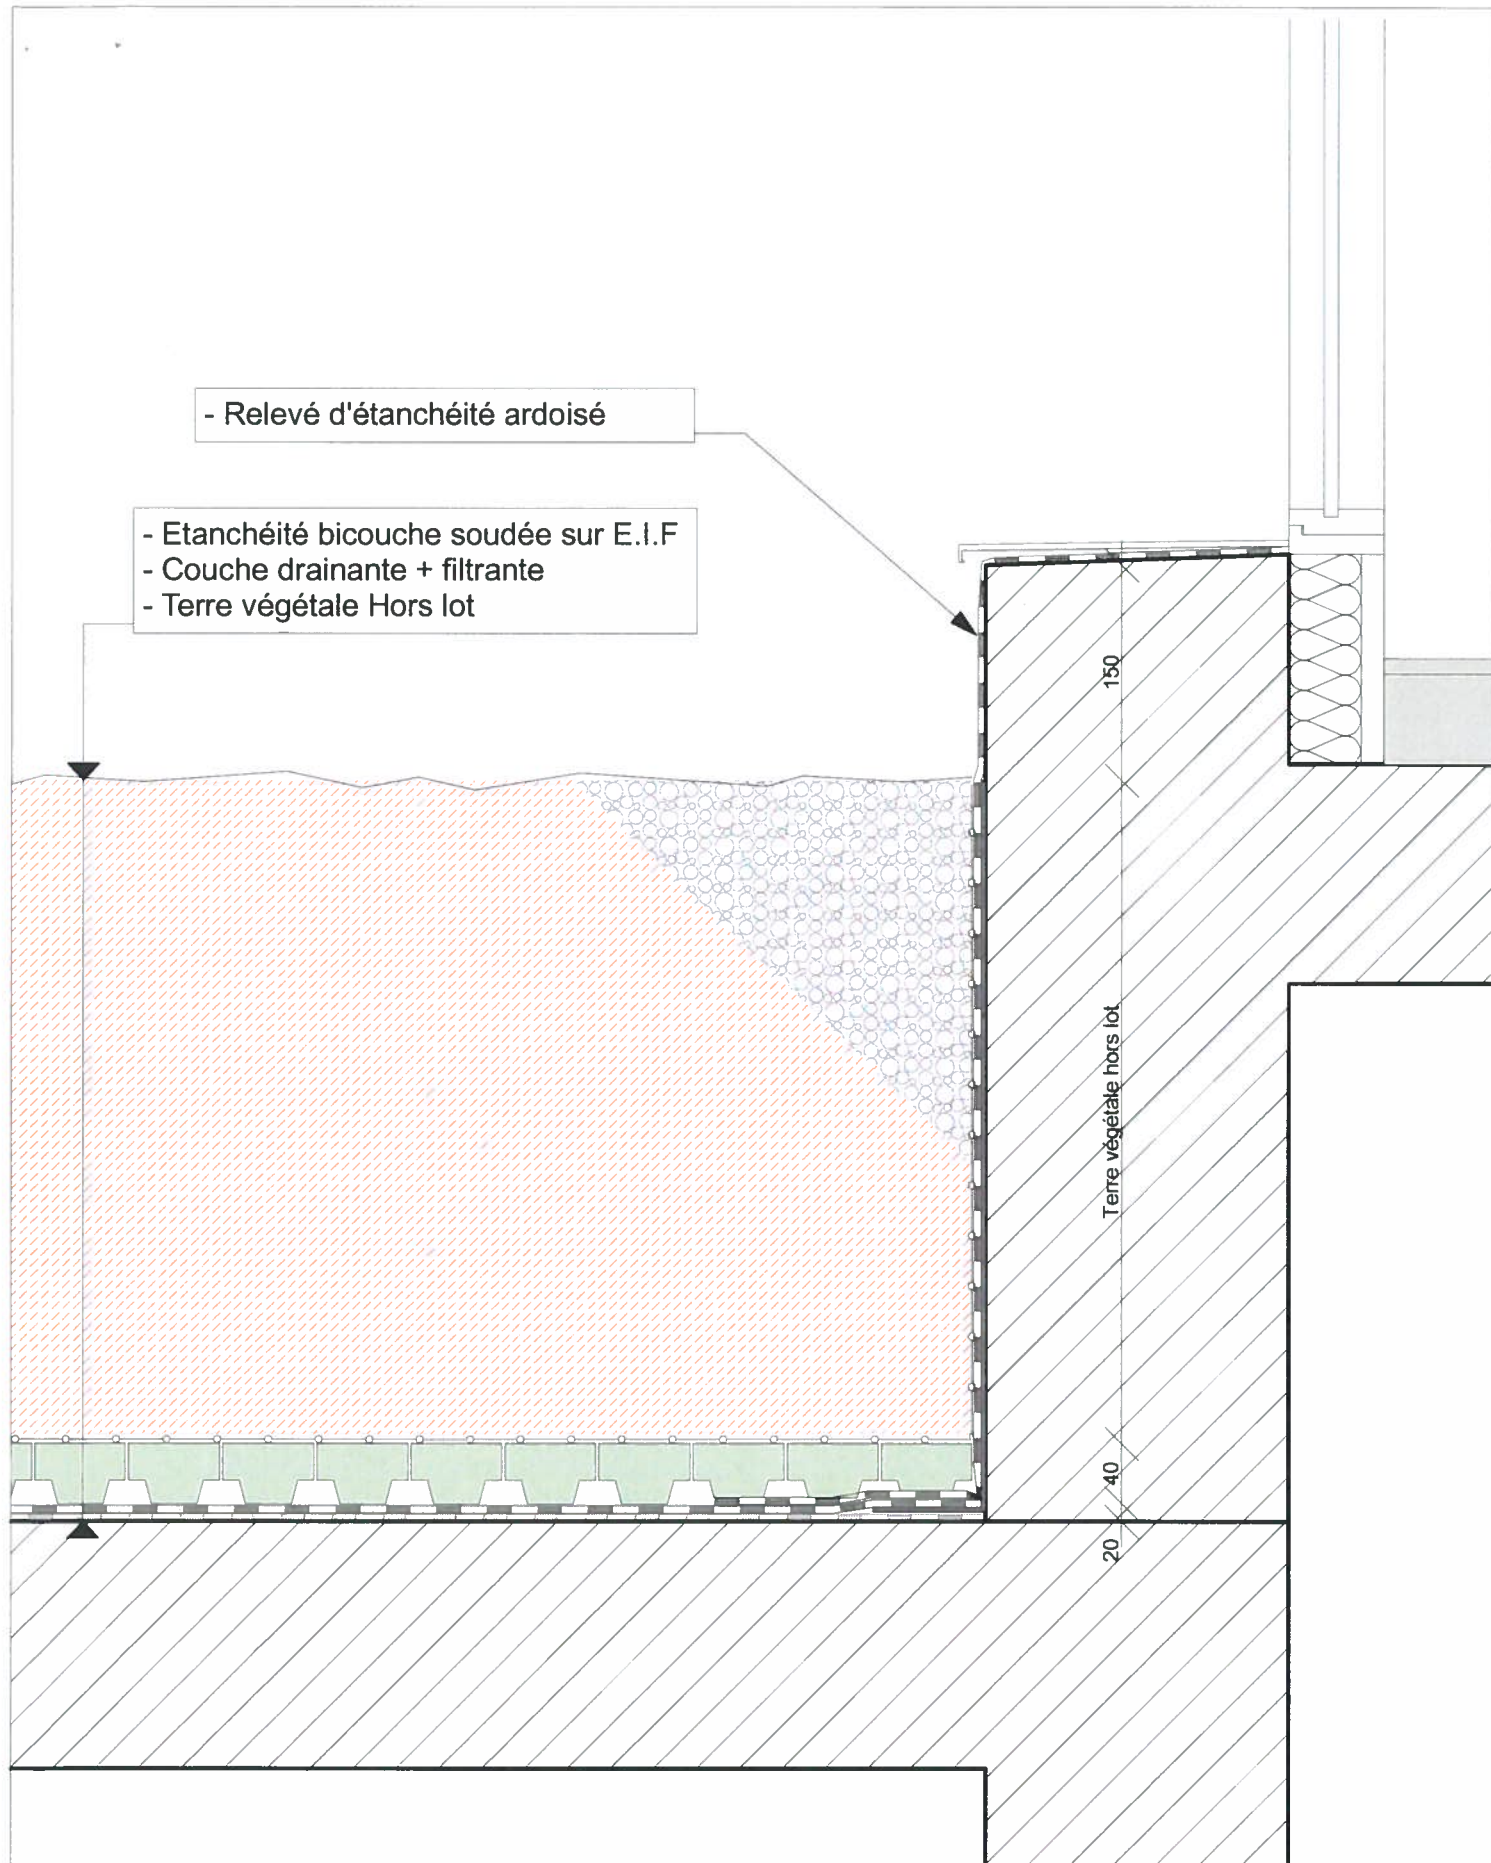

Affaire : LE 180 BAT A ET B - 69350 LA MULATIERE - NOAHO

PHASE		INTITULE		Référence Projet: 2015/353	
EXE		RELEVÉ CONTRE FACADE TERRASSE JARDIN		DATE DOCUMENT: 02 Septembre 2015	
				ECHELLE 1/5	LOCALISATION
				LOT	INDICE
				06	Détail 10
					1




S.I.E.
Service Industrie Etanchéité

Tél : 04.72.89.12.29
Fax : 04.78.67.70.10
Z.I. - Les Bords du Rhône
2, Boulevard Lucien Sampaix
BP 24 - 69191 ST-FONS

Dessin : R.Lambert
etudes@sie-etancheite.fr
Les informations techniques contenues
dans ce document
sont la propriété exclusive de SIE


- Etanchéité bicouche soudée sur E.I.F
- Couche drainante + filtrante
- Terre végétale Hors lot

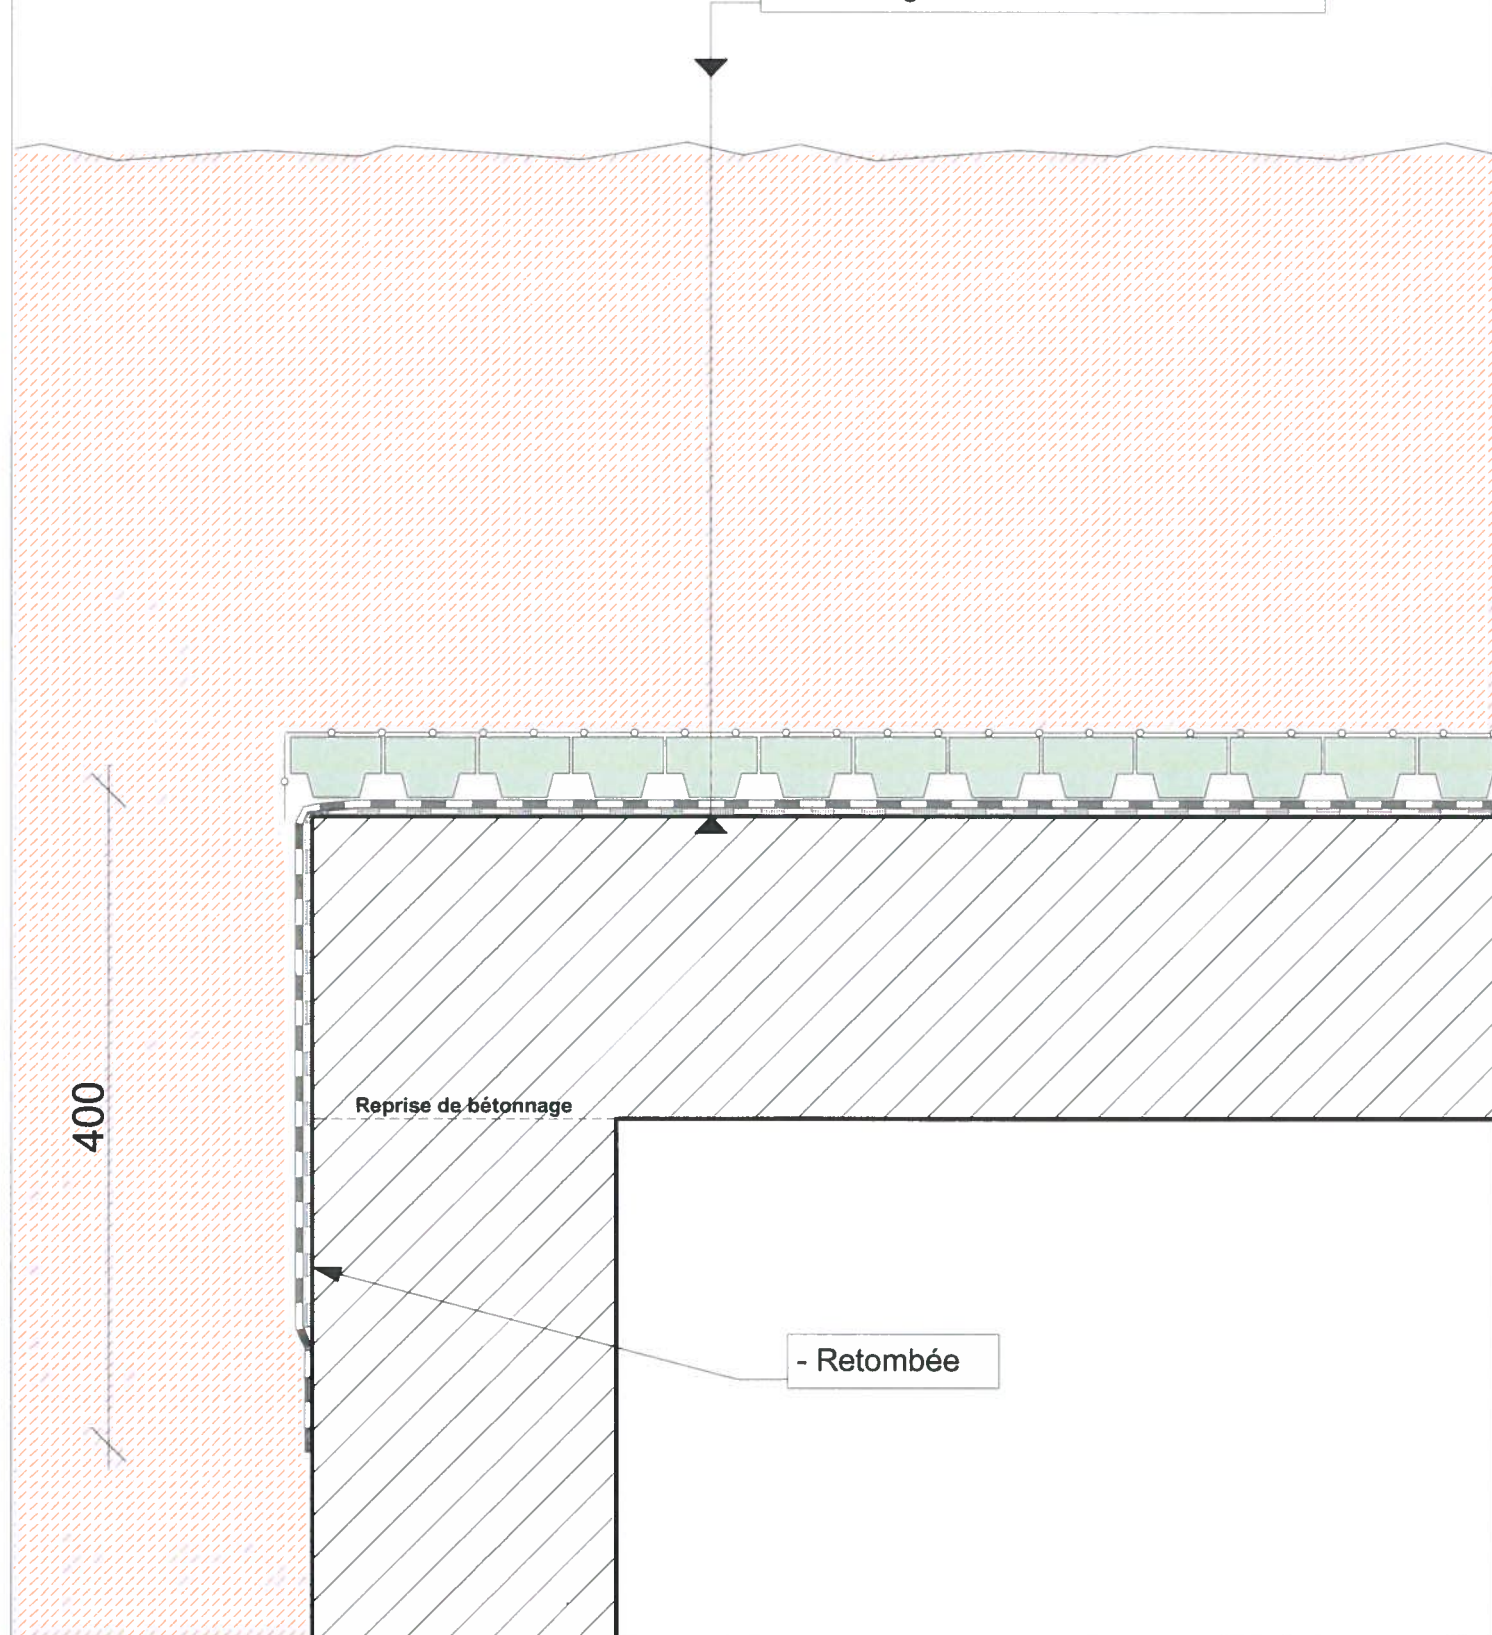

Affaire : LE 180 BAT A ET B - 69350 LA MULATIERE - NOAHO

PHASE		INTITULE		Echelle		Référence Projet: 2015/353	
EXE		RETOMBEE TERRASSE JARDIN		1/5		DATE DOCUMENT: 02 Septembre 2015	
				LOT		LOCALISATION	INDICE
				06		Détail 11	1

- Etanchéité bicouche soudée sur E.I.F
- Protection par lame bois sur lambourde et plots

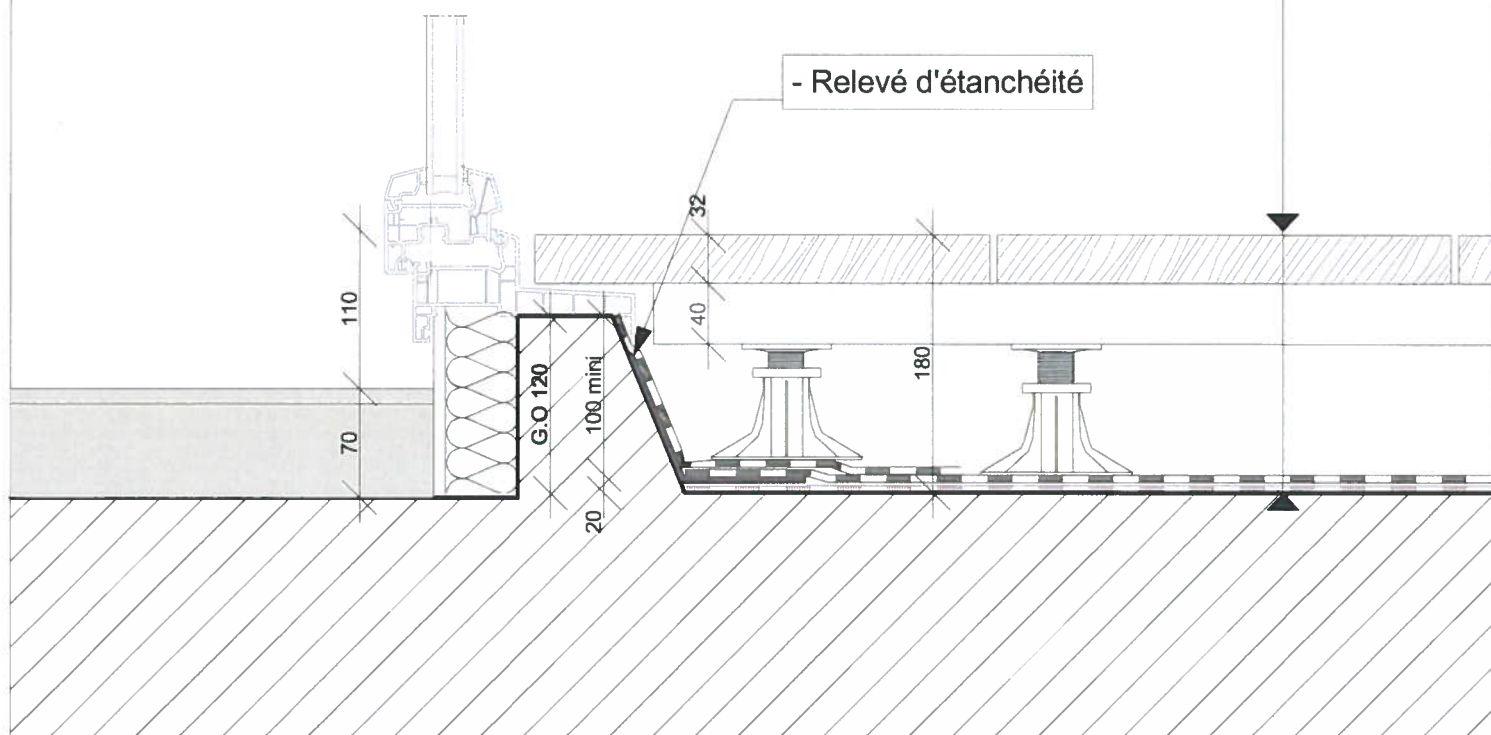

Affaire : LE 180 BAT A ET B - 69350 LA MULATIERE - NOAHO

PHASE		INTITULE		Référence Projet: 2015/353	
EXE		RELEVÉ CONTRE SEUIL TERRASSE JARDIN		DATE DOCUMENT: 02 Septembre 2015	
				ECHELLE	LOCALISATION
				1/5	
				LOT	INDICE
				06	Détail 12
					1



Tél : 04.72.89.12.29
Fax : 04.78.67.70.10
Z.I. - Les Bords du Rhône
2, Boulevard Lucien Sampaix
BP 24 - 69191 ST-FONS

Dessin : R. Lambert
etudes@sie-etancheite.fr
Les informations techniques contenues
dans ce document
sont la propriété exclusive de SIE