



FACADE OUEST AILE EST

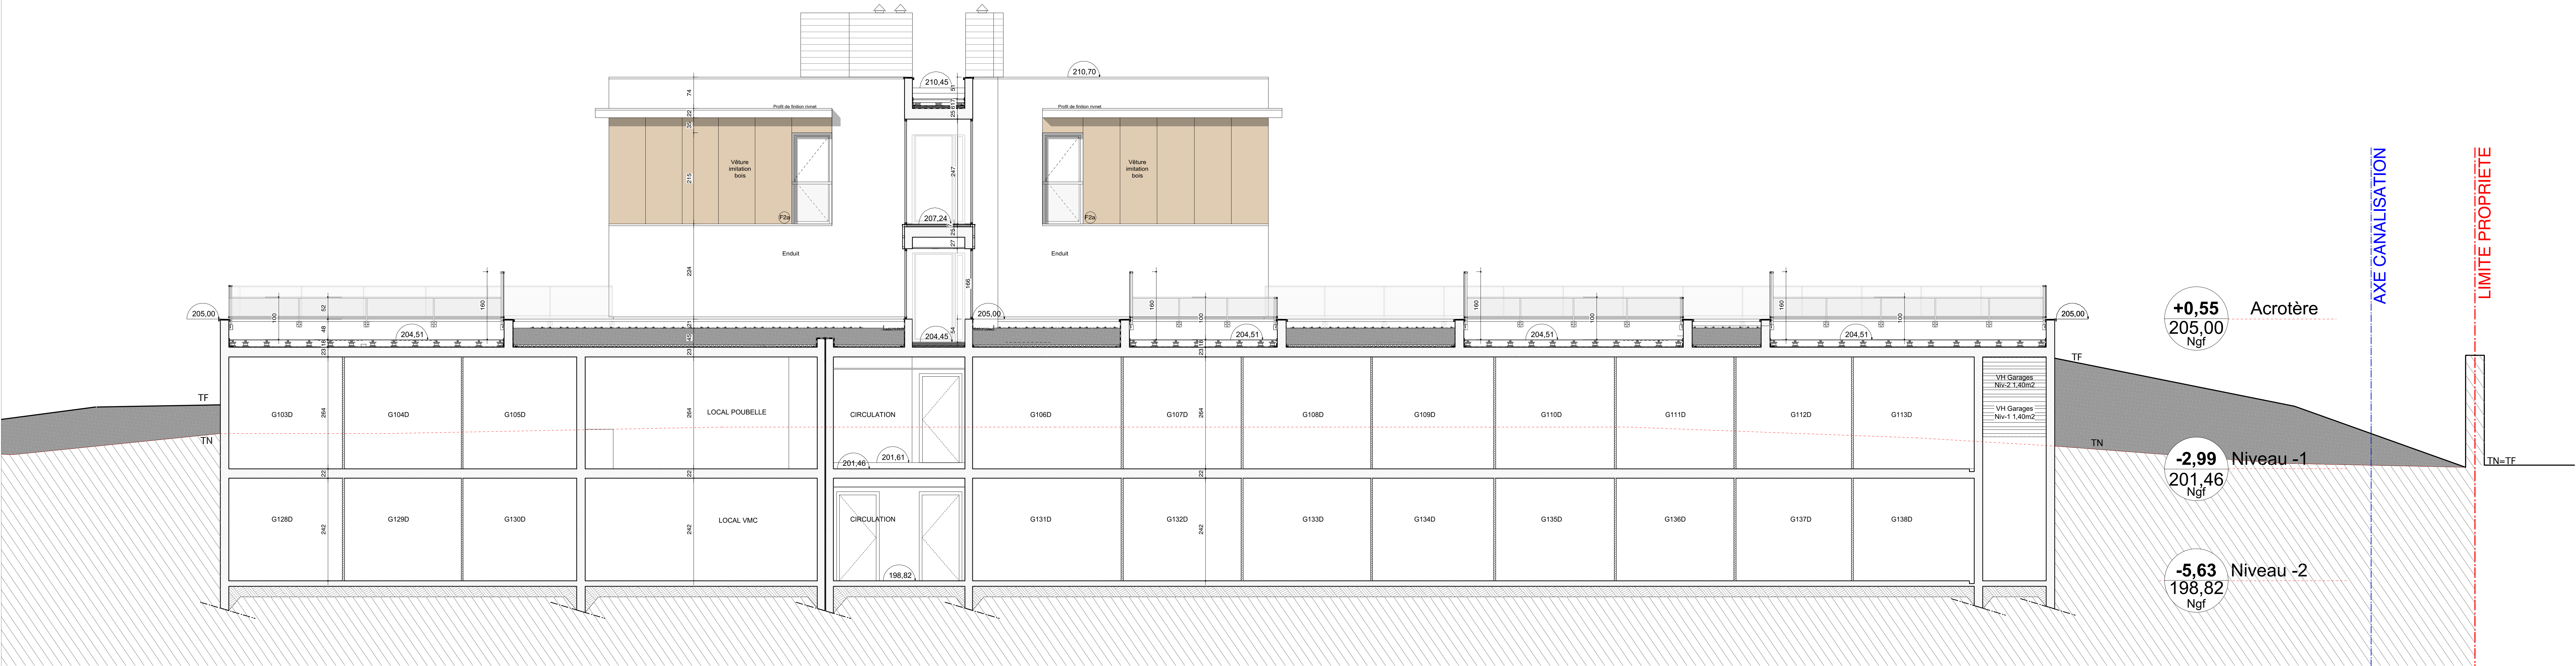

FACADE EST AILE OUEST

 

Création de logements

La Mulatière

Chemin de Fontanière - 69350 La Mulatière

Affaire n° 280

Maître d'ouvrage

NOAHO
23 Avenue de Pourmeyrol
69300 Caluire-et-Cuire
Std : 04.78.30.33.90 Fax : 04.78.30.33.91

Architecte

Atelier d'IS
51, rue Delaunay 69004 LYON
Tél : 04.78.25.20.52 Fax : 08.70.06.38.67
Mail : atelierdis@atelierdis.com

PAYSAGISTE / BET VRD SYMBIOSE Adresse : 440 rue Barthélemy Thérondier - 69530 BRIGNAIS
Std : 04.78.60.68.68 Fax : 04.78.60.12.30 Mail : symbiose@sybiose.fr

BET ECONOMIE EXECCO Adresse : 230 rue Calage 69003 - LYON
Std : 04.78.37.55.04 Fax : 04.78.37.10.18 Mail : execo@execo.fr

BET FLUIDES PRELEH Adresse : 170 Boulevard de Stalingrad - 69601 LYON
Std : 04.78.69.84.77 Fax : 04.78.85.55.01 Mail : preleh@preleh.com

BET STRUCTURE MATTE Adresse : 110 Boulevard de Stalingrad - 69500 St. LÉGERENNE
Tél : 04.72.44.02.87 Fax : 04.74.82.82.39 Mail : bet@matte.fr

BUREAU DE CONTRÔLE VERITAS Adresse : 15 Chemin du Jumeau BP 26 - 69011 SARDOLLY
Tél : 04.72.25.70.70 Fax : 04.78.35.63.10 Mail : bureau@bureauveritas.com

PLANS - COUPES - FAÇADES - PROJET
BÂTIMENT C

Phase : MARCHÉ

Bâtiment : C

Niveau :

Coups - Façades : Est & Ouest

Plan n° : 23

Indice : A

Date : AVRIL 2015

Echelle : 1/50

