

Création de logements
La Mulatière
Chemin de Fontanière - 69350 La Mulatière
Affaire n° 278


Maitre d'ouvrage
NOAHO
23 Avenue de Pomeyrol
69300 Caluire-et-Cuire
Std : 04.78.30.33.90 Fax : 04.78.30.33.91

Architecte
Atelier d'IS
51, rue Delorme 69004 LYON
Tél : 04.78.29.20.52 Fax : 09.70.06.38.67
Mail : atelierdhis@gmail.com


PAYSAGISTE / BET VRD SYMBIOSE Adresse : 440 rue Garbellery-Thomson - 69530 BRIGNAIS
Std : 04.78.60.85.47 Fax : 04.78.60.32.30 Mail : cecilegarnier@betsymbiose.fr
BET ECONOMIE EXECO Adresse : 259 rue Chézy 69003 - LYON
Std : 04.78.37.55.04 Fax : 04.78.37.10.14 Mail : cecilegarnier@betsymbiose.fr
BET FLUIDES PRELEM Adresse : 170 boulevard de Stalingrad - 69453 LYON
Std : 04.78.68.94.77 Fax : 04.78.85.55.01 Mail : seigneur@prelem.com
BET STRUCTURE MATTE Adresse : 115 boulevard de Stalingrad - 69100 VILLEURBANNE
Tél : 04.72.44.62.87 Fax : 04.74.82.62.39 Mail : bet@matte.fr
BUREAU DE CONTROLE VERITAS Adresse : 10 chemin du Jalon BP 26 - 69671 DARDILLY
Tél : 04.72.29.70.70 Fax : 04.78.78.93.10 Mail : bureau@bureauveritas.com

PLANS - COUPES - FAÇADES - PROJET
BÂTIMENT C

Phase : DCE
Bâtiment : C
Niveau : NIVEAU 2_ Aile Ouest
Coupes - Façades :
Plan n° : 10
Indice : F
Date : 16 / 04 / 15
Echelle : 1/50

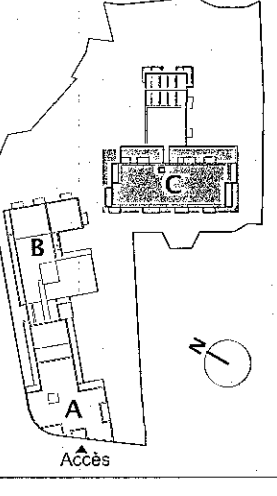

Localisation Ind. A du 13/05/2015

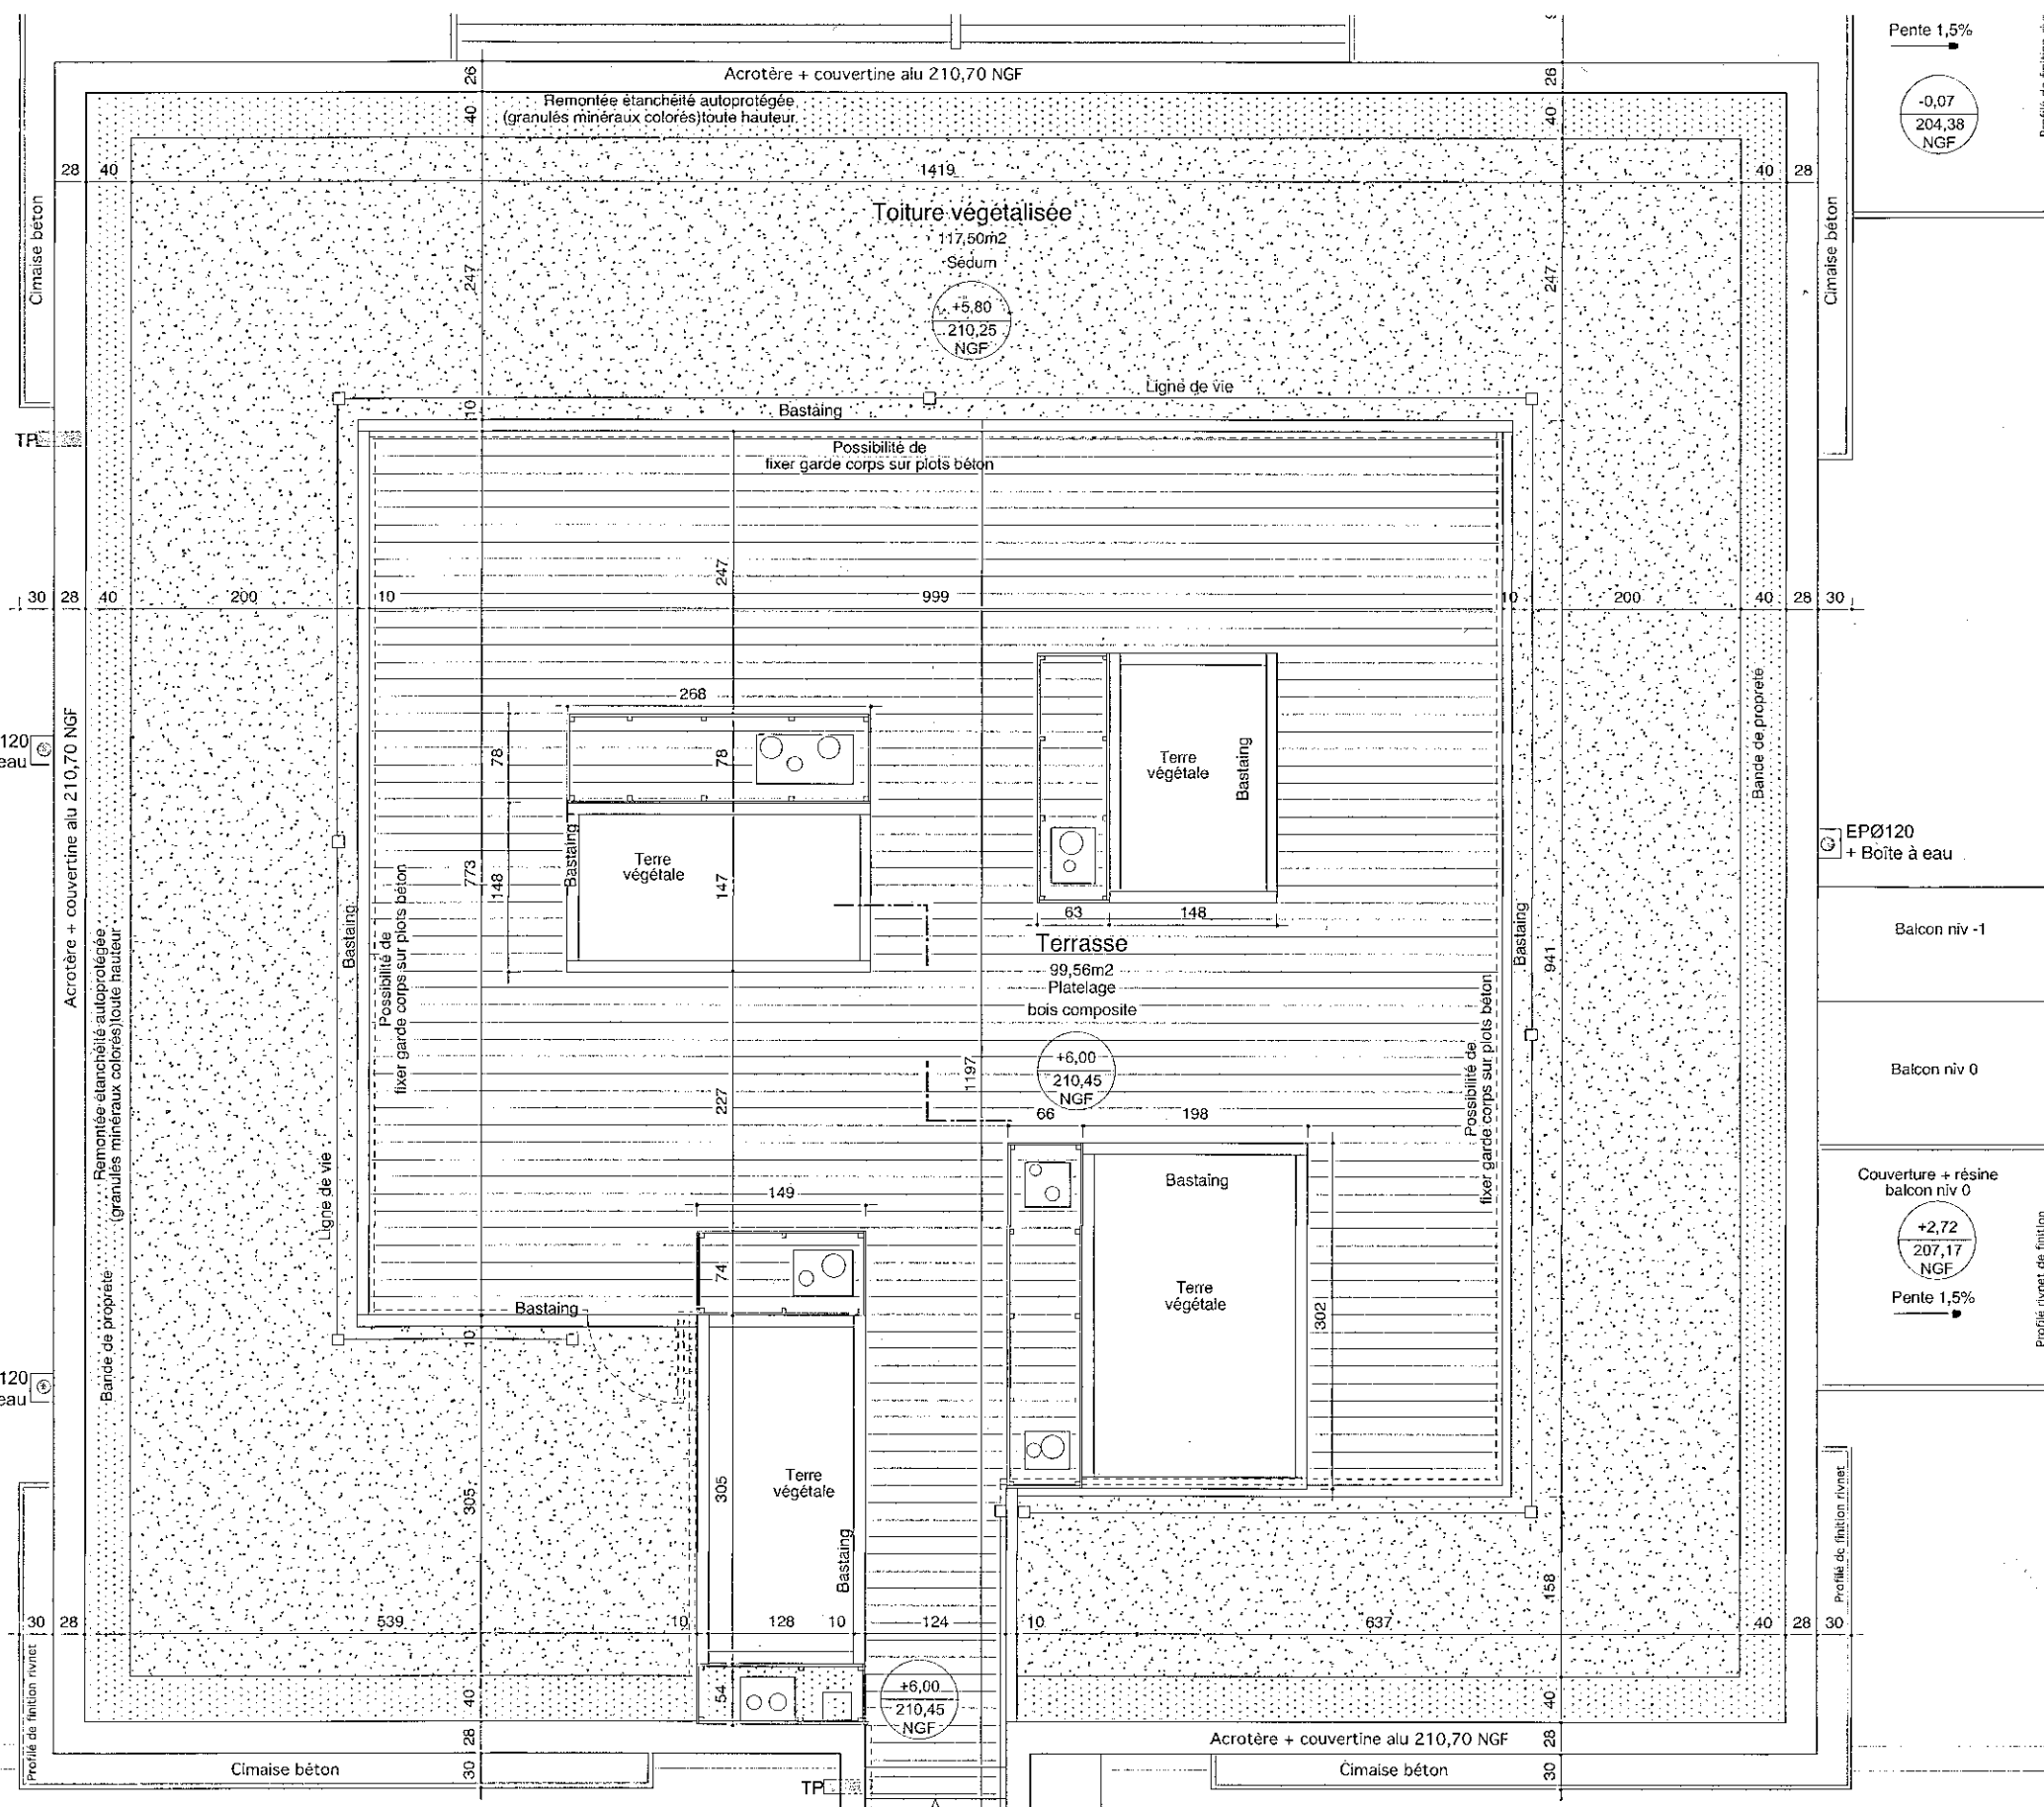

A.3

A.3



A.1

A.1