

AFFAIRE :LE 180 BATIMENT A ET B

GARDE-CORPS


Dossier d' Ouvrages Exécutés





GARDE-CORPS ACIER :

Laquage : RAL : 9007


Fournisseur : LENOIR METALLERIE

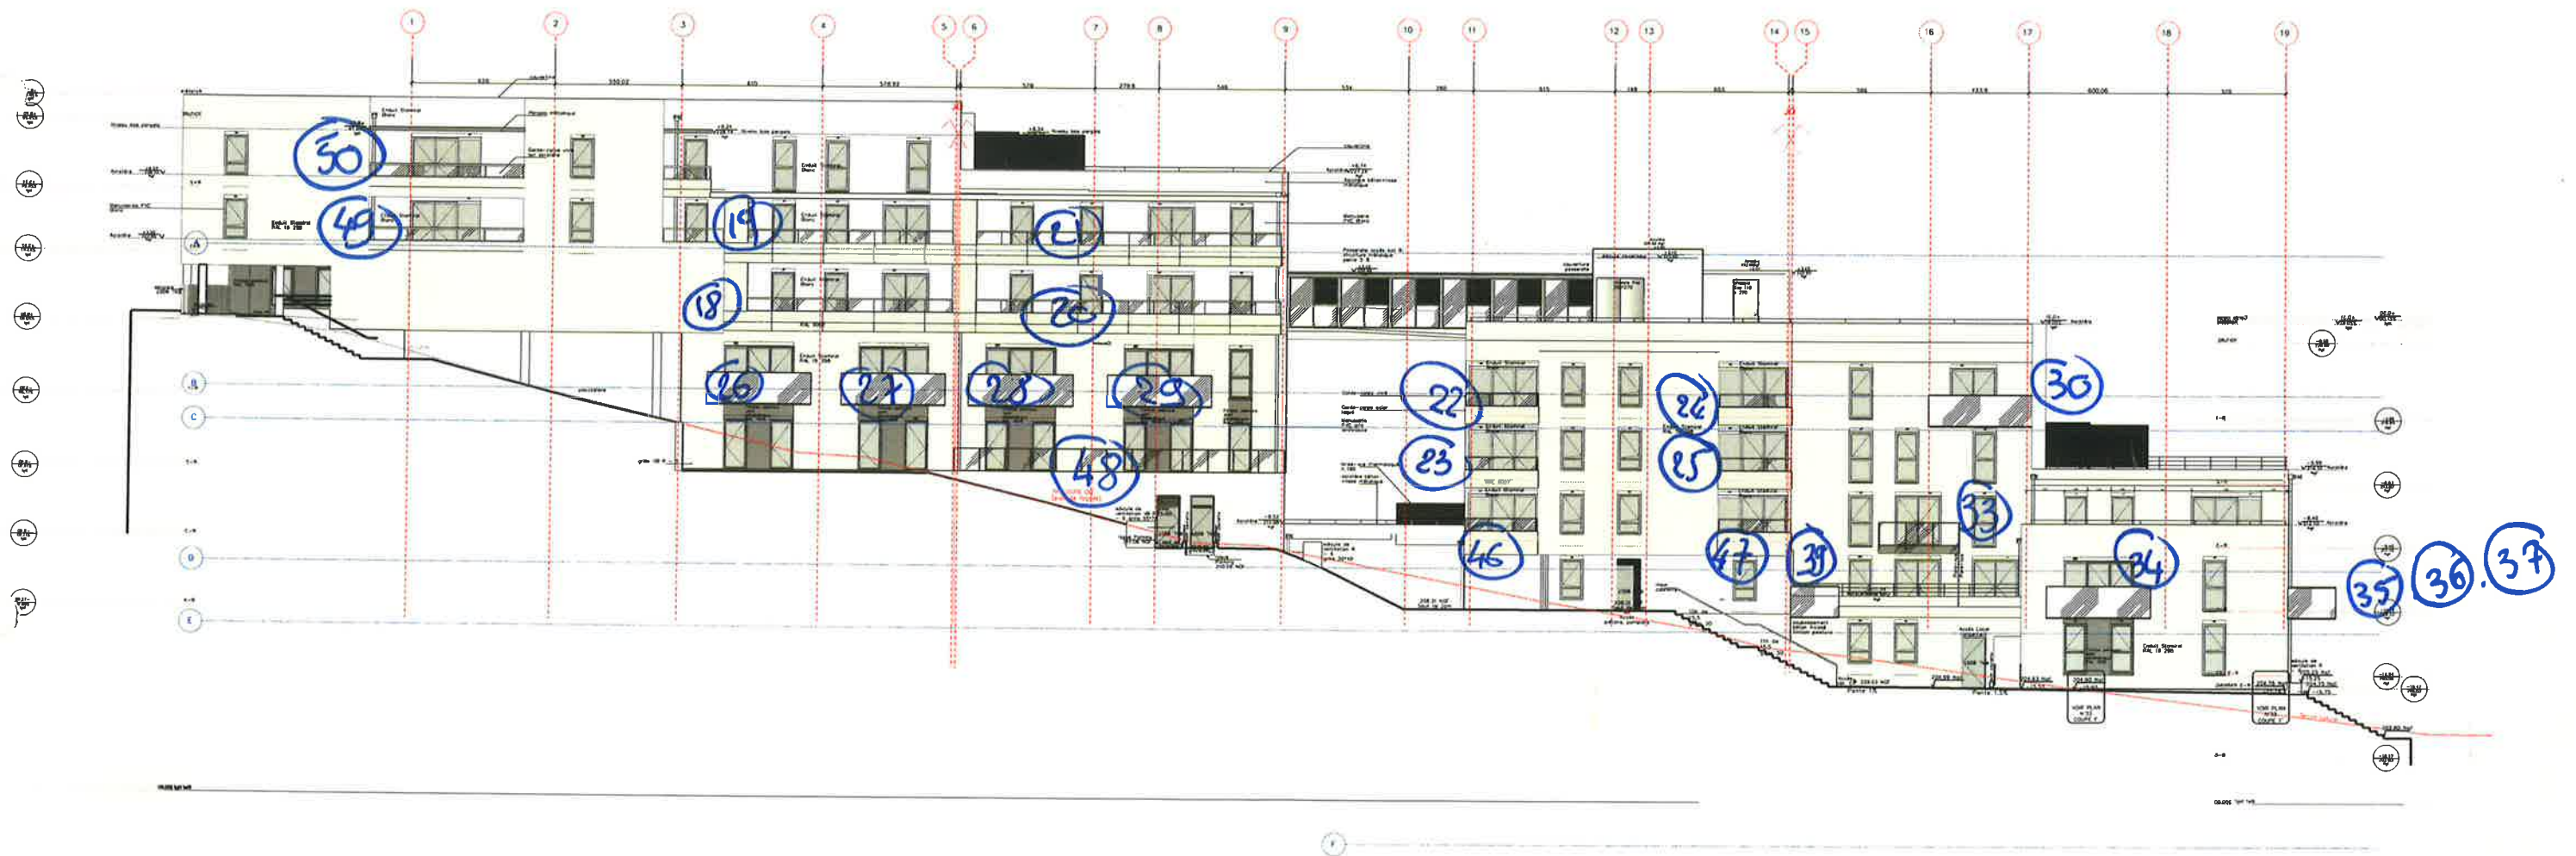




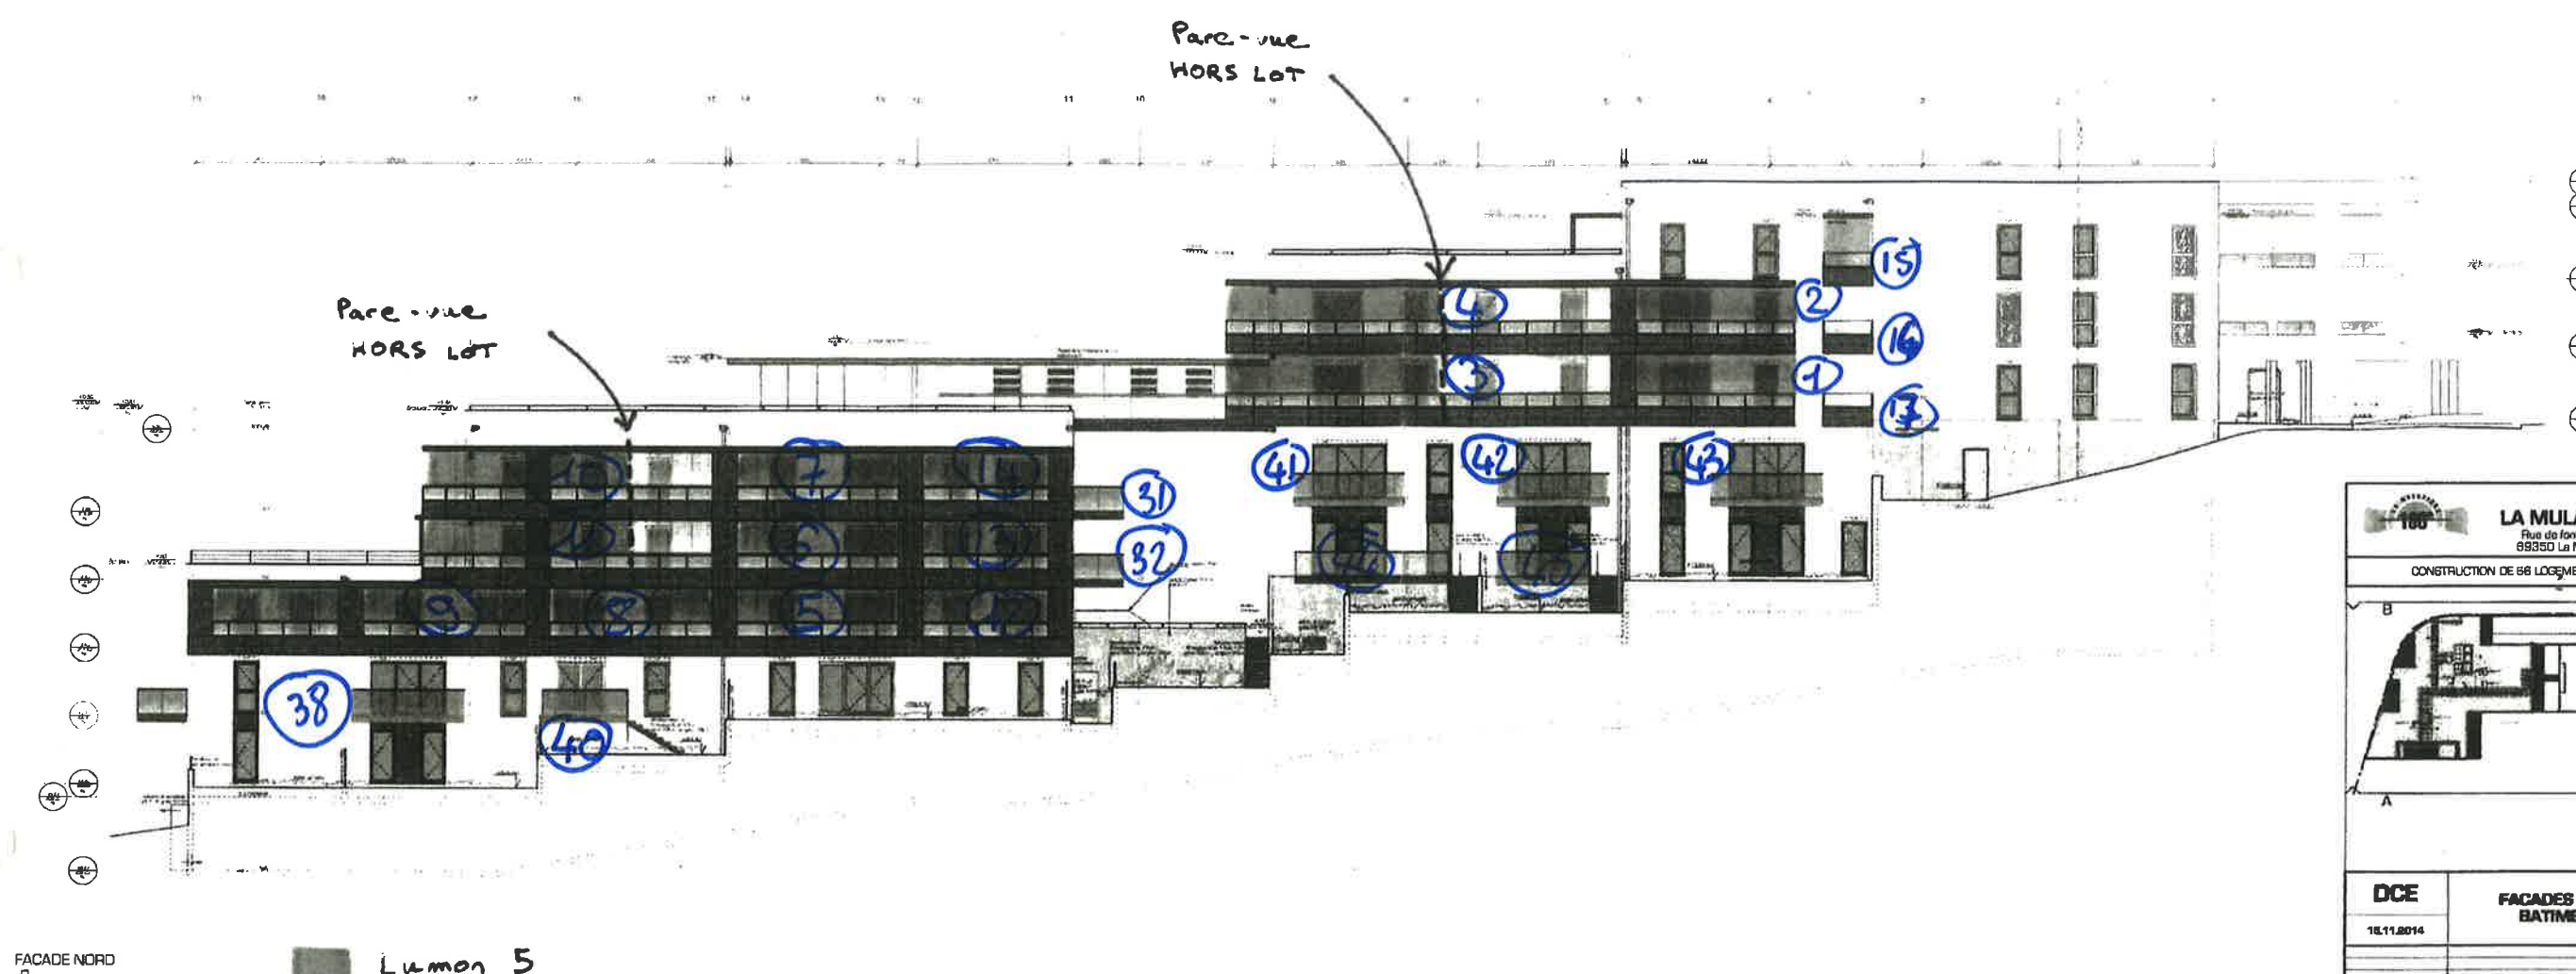


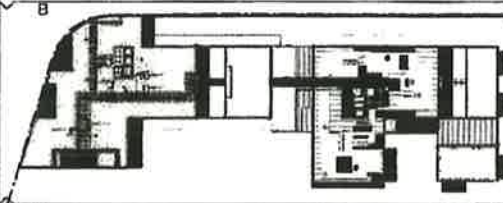 LA MULATIERE Rue de la République 89350 La Mulatière noah atelier de la passerelle 02 30 20 10 00		
CONSTRUCTION DE 66 LOGEMENTS, EN ACCESION LIBRE ET SOCIALE		
 A B		
N		
DCE	FACADES NORD ET SUD BATIMENTS A ET B	21
16.11.2014		1/100

*Pot
Garde-corps*




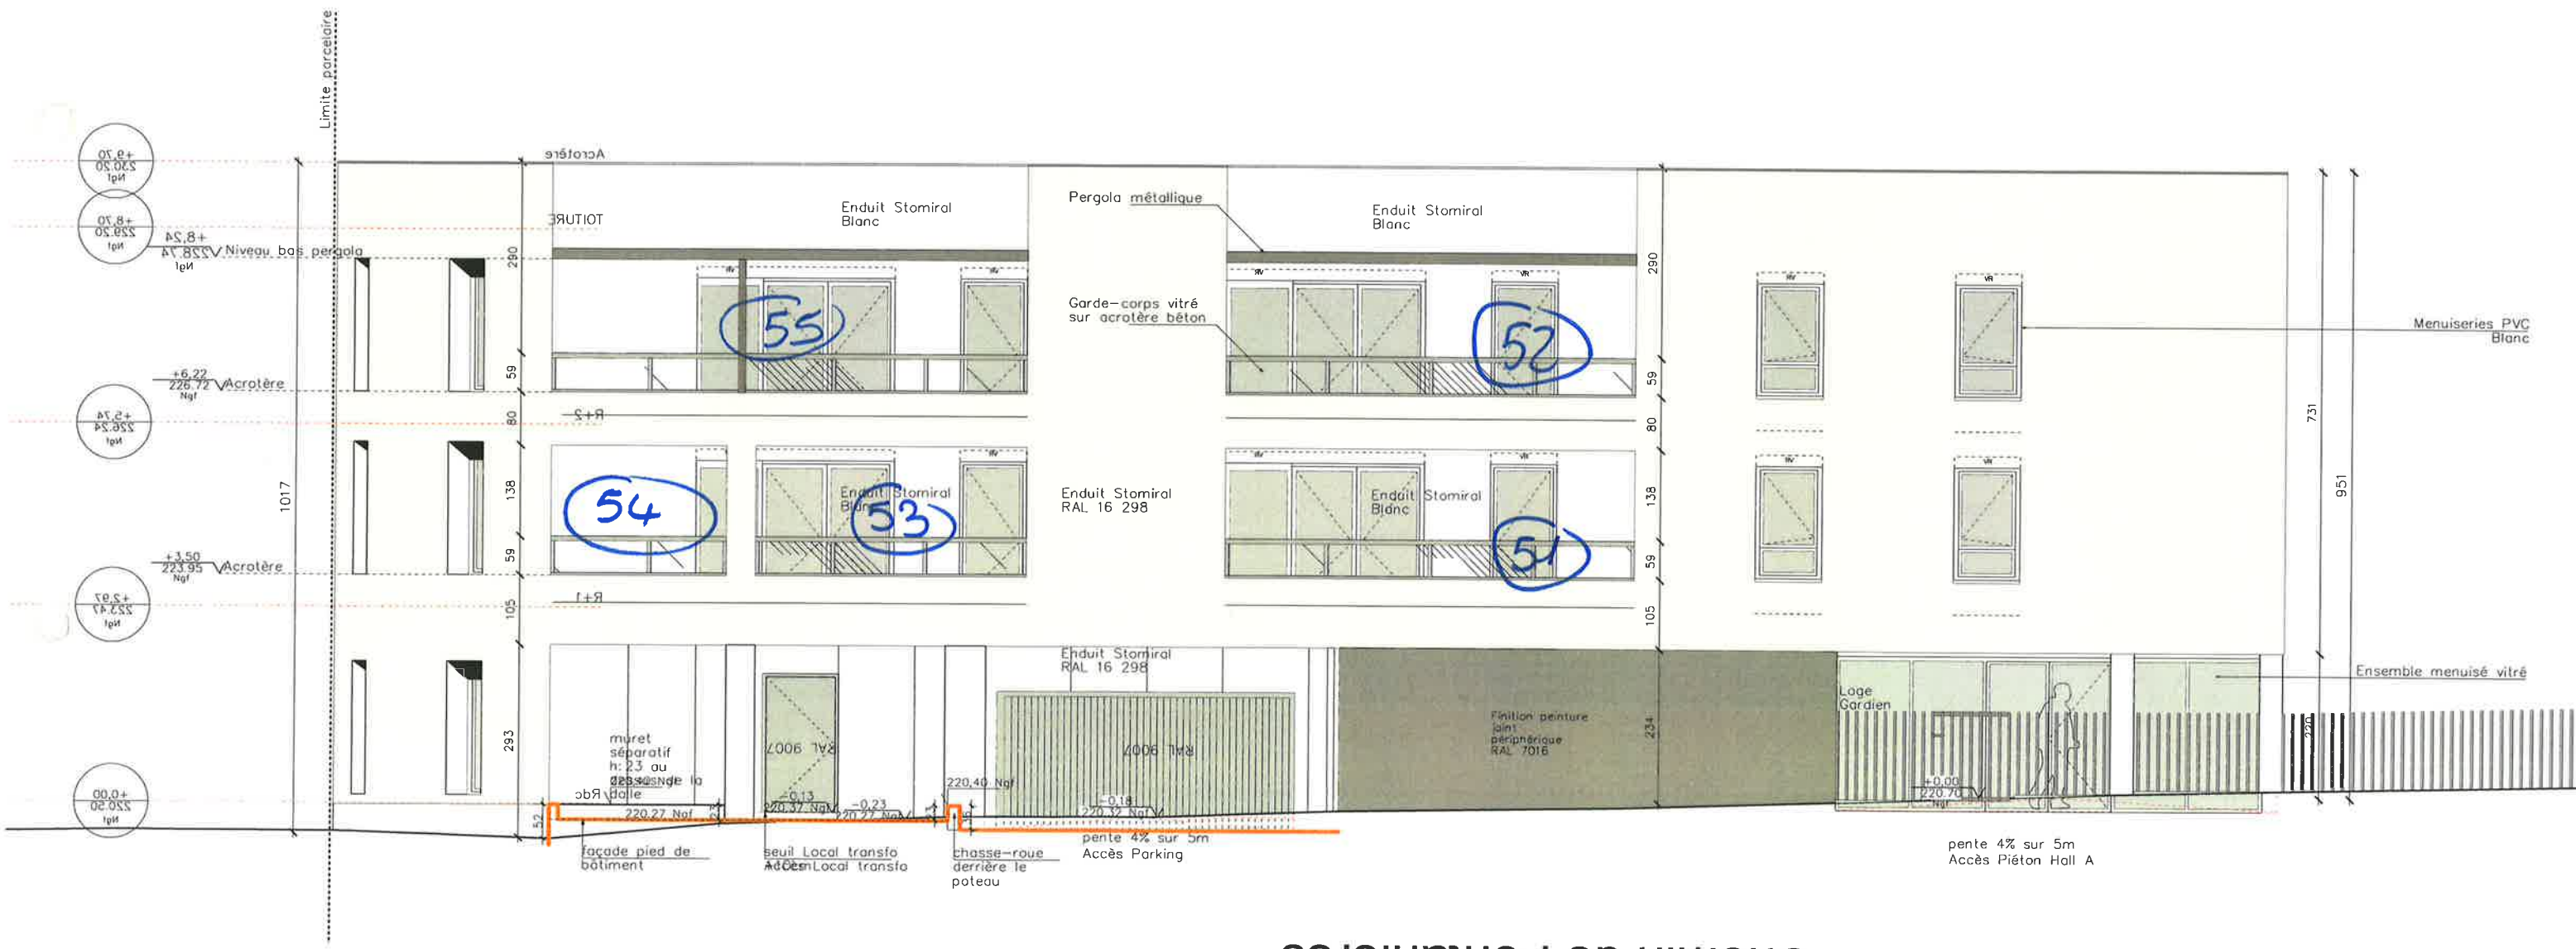



COLOMBIE LOU LUTHELO

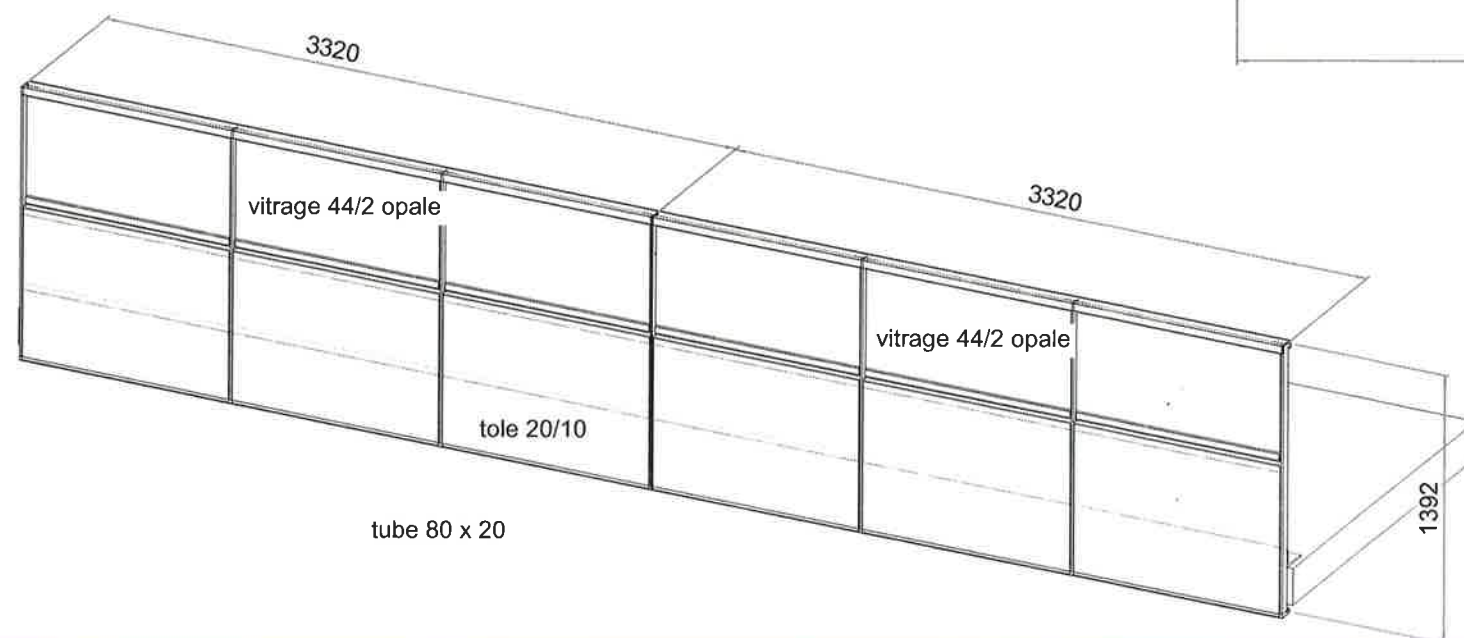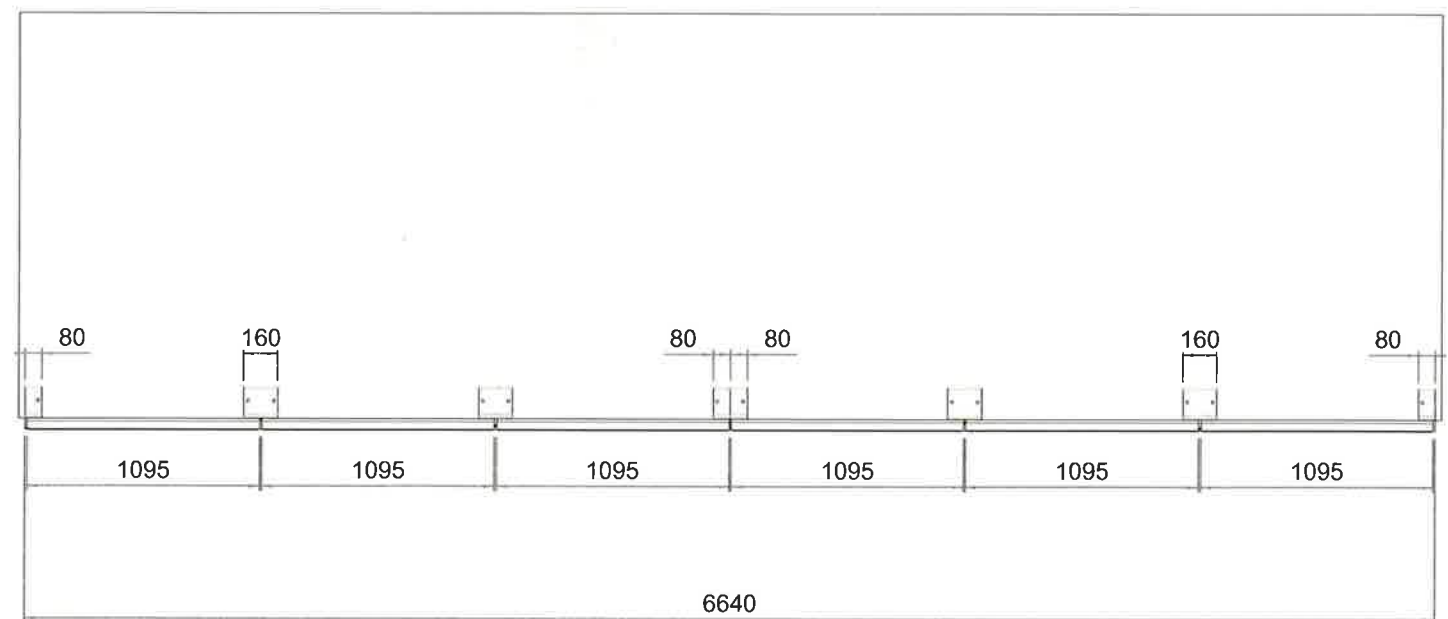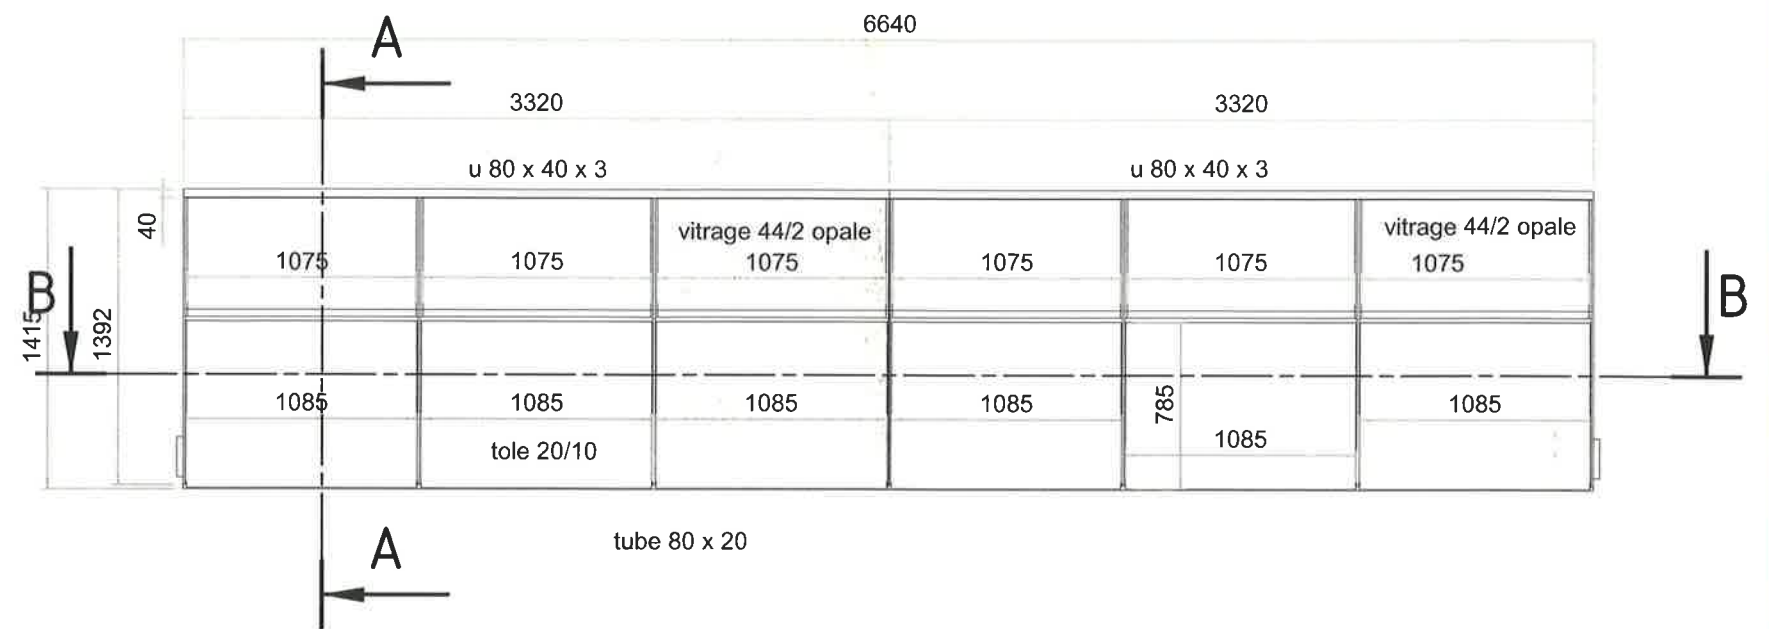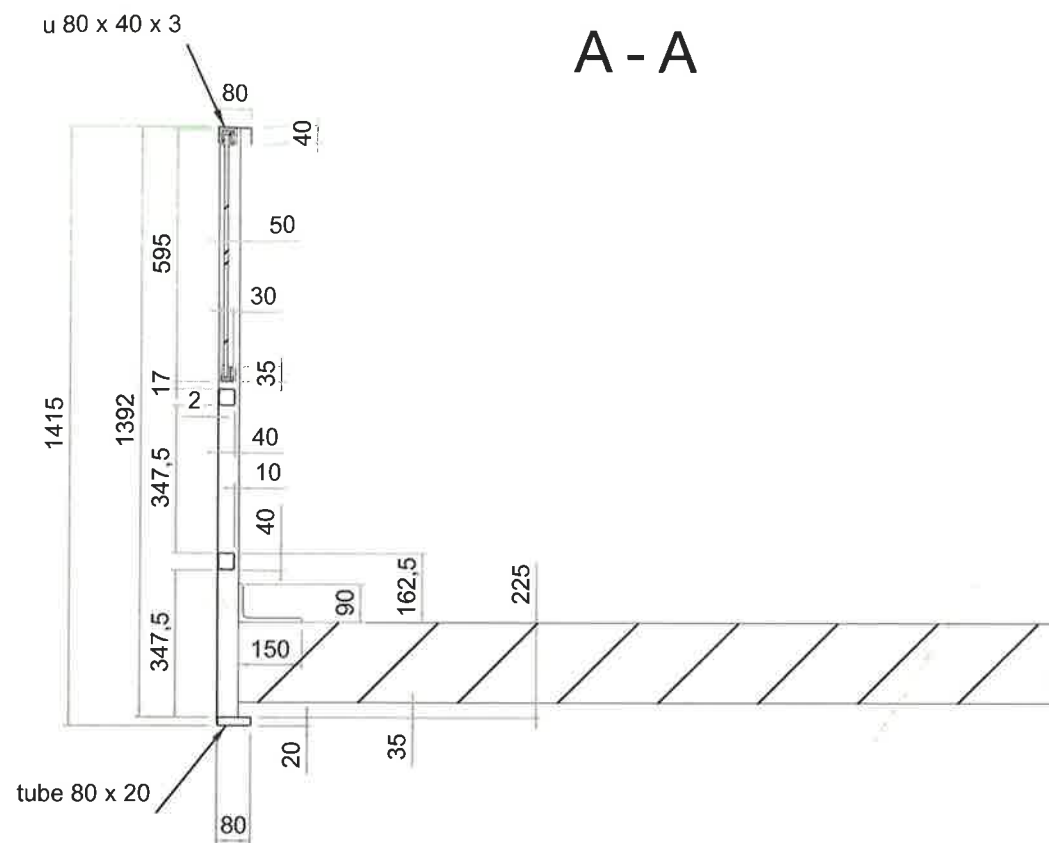


Désignation : GC-rep-1 bat A	Auteur : ETUDE 2		A3	
	Date : 23/08/2016			
Référence : CH0038		Ech. 1 : 50	Révision A	Page -
 SAS SCHONT 68 rue saint exupéry 69124 colombier saugnieu	Chantier : 180			

Désignation	Repère	Longueur	Angle de coupe 1	Angle de coupe 2	Quantité	Largeur	Largeur boîte (mise à plat)	Masse
					1			194,73,02kg
	1				1	0,00mm	0,00mm	0,00kg
	2				1	0,00mm	0,00mm	19186,66kg
	3				6	0,00mm	0,00mm	13,37kg
	4	3320,00mm	0,00°	0,00°	1	0,00mm	0,00mm	12,04kg
	5	3320,00mm	0,00°	0,00°	1	0,00mm	0,00mm	12,04kg
Cornière à ailes inégales 150 × 90 × 10, ISO 657-2	6	80,00mm	0,00°	0,00°	1			1,44kg
Cornière à ailes inégales 150 × 90 × 10, ISO 657-2	7	80,00mm	0,00°	0,00°	1			1,44kg
Cornière à ailes inégales 150 × 90 × 10, ISO 657-2	8	80,00mm	0,00°	0,00°	1			1,44kg
Cornière à ailes inégales 150 × 90 × 10, ISO 657-2	9	80,00mm	0,00°	0,00°	1			1,44kg
Cornière à ailes inégales 150 × 90 × 10, ISO 657-2	10	160,00mm	0,00°	0,00°	4			2,88kg
patte vitrage 60	11				24			
plat-50x5	12	1392,00mm	0,00°	0,00°	1	0,00mm	0,00mm	2,73kg
plat-50x5	13	1392,00mm	0,00°	0,00°	1	0,00mm	0,00mm	2,73kg
plat-50x10	14	1392,00mm	0,00°	0,00°	1	0,00mm	0,00mm	5,46kg
plat-50x10	15	1392,00mm	0,00°	0,00°	1	0,00mm	0,00mm	5,46kg
plat-50x10	16	1392,00mm	0,00°	0,00°	4	0,00mm	0,00mm	5,46kg
profil alu+joint	17	1075,00mm	0,00°	0,00°	6			
profil alu+joint	18	1075,00mm	0,00°	0,00°	6			
Profilé carré creux 40 × 2, ISO 4019	19	1095,00mm	0,00°	0,00°	12			2,52kg
tube 80x20	20	3320,00mm	0,00°	0,00°	1	0,00mm	0,00mm	7,58kg
tube 80x20	21	3320,00mm	0,00°	0,00°	1	0,00mm	0,00mm	7,58kg
vitrage	22				6	1075,00mm	571,00mm	13,50kg

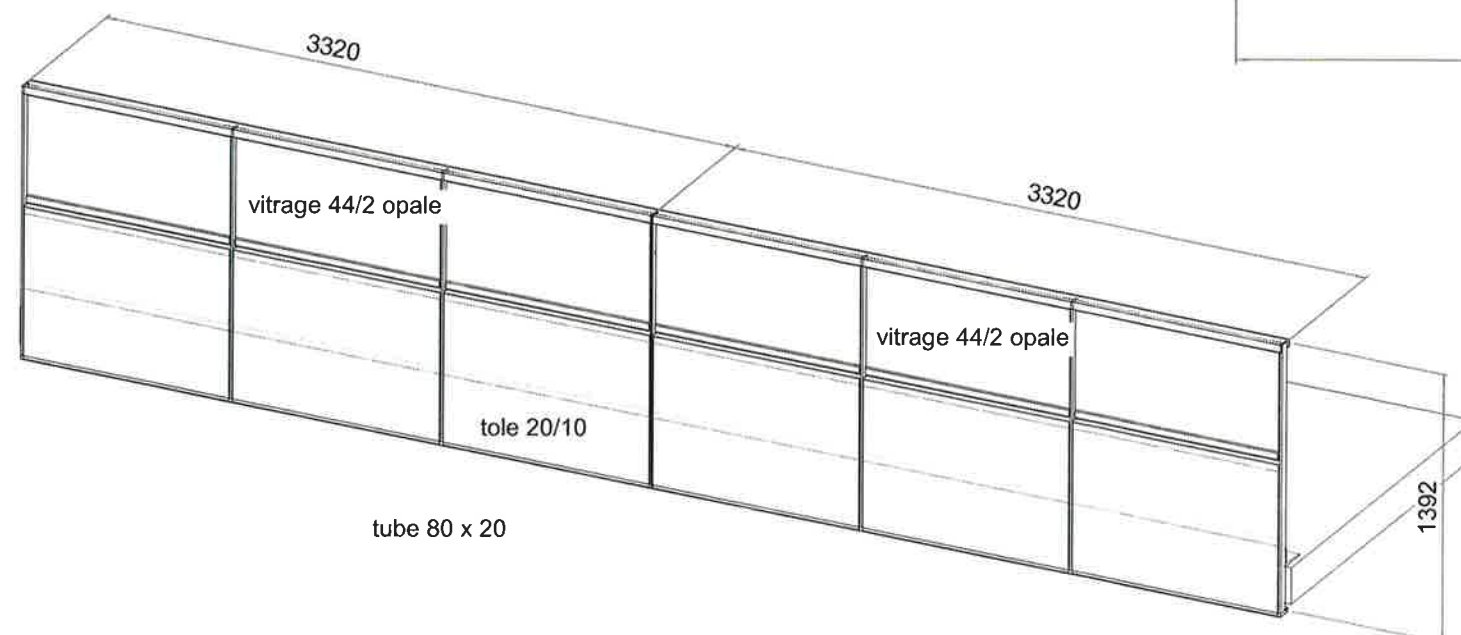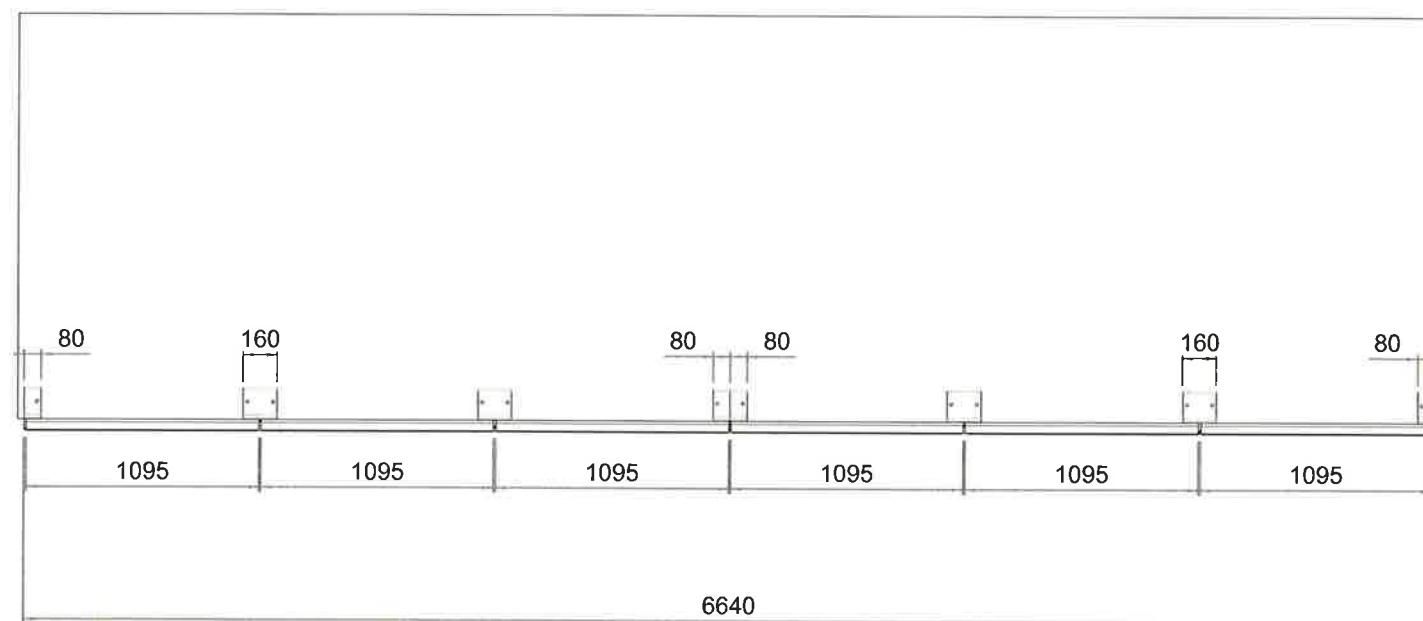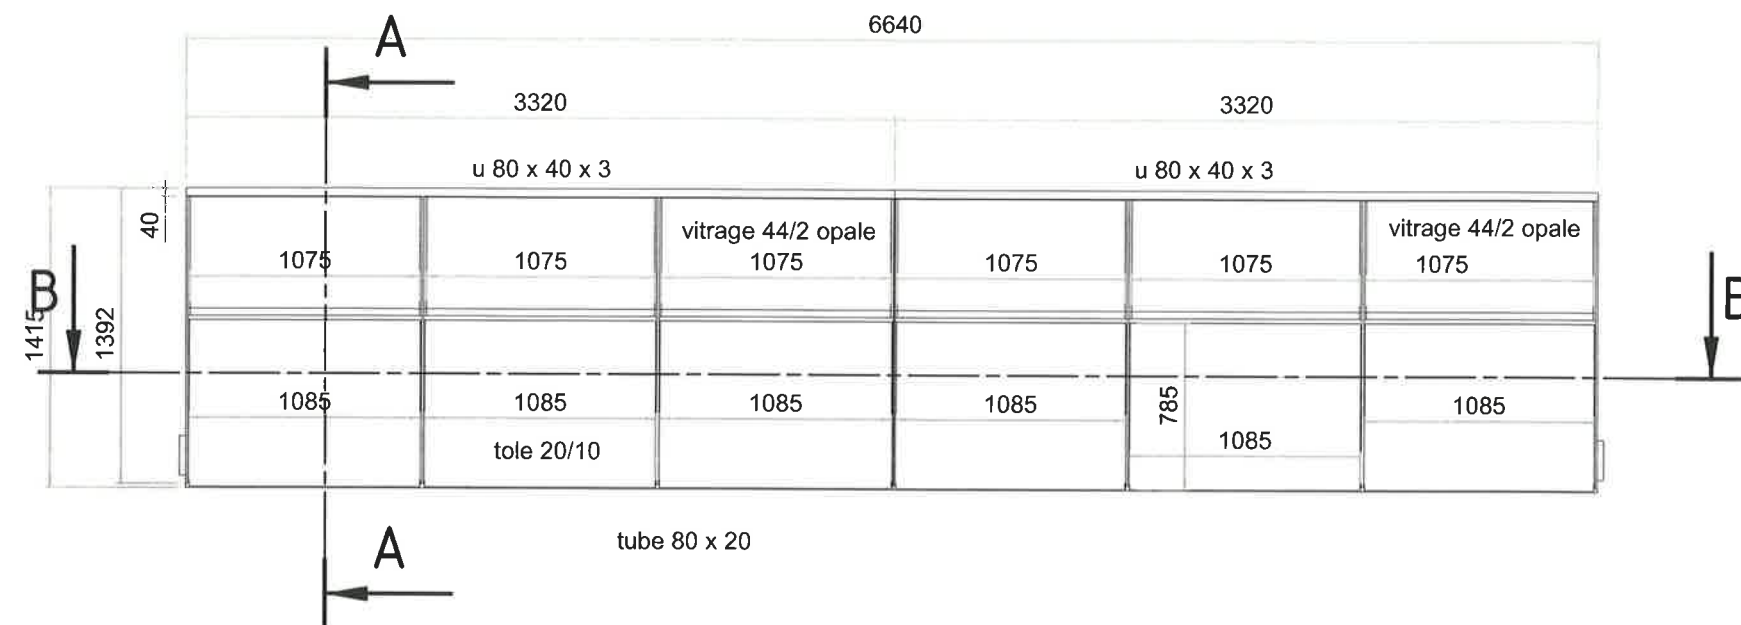
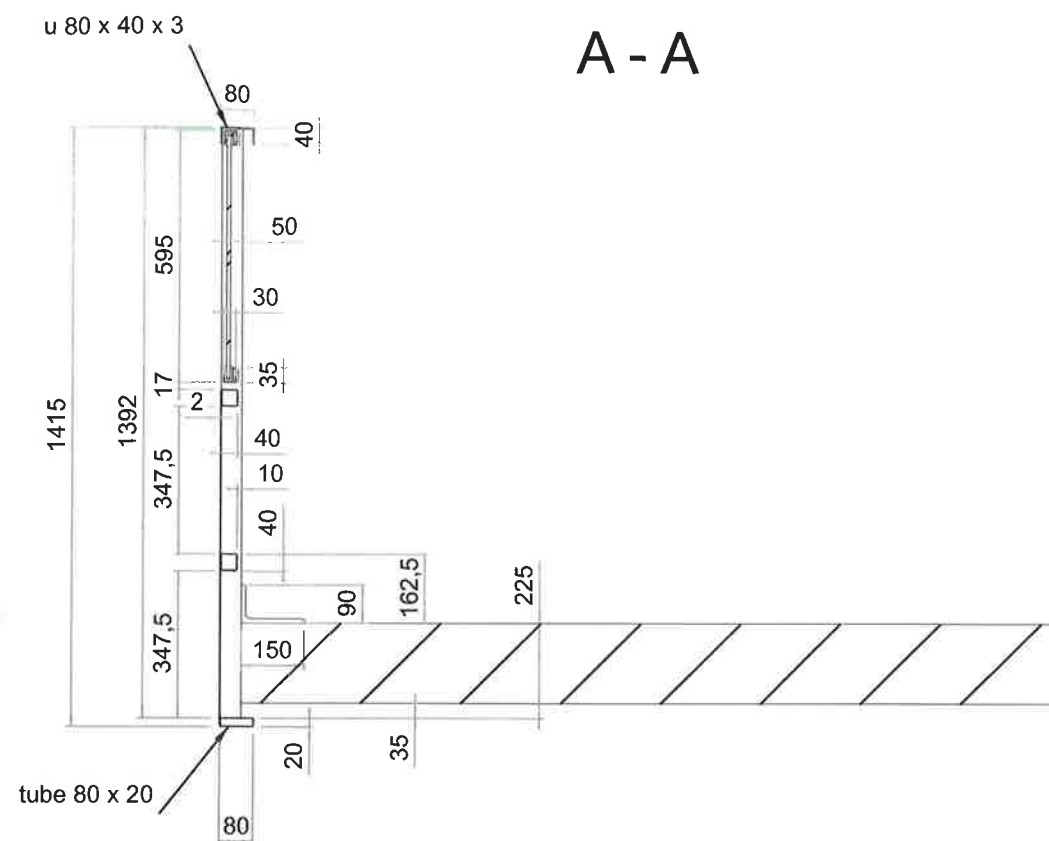


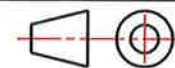Désignation : GC-rep-2 bat A Référence : CH0038	Auteur : ETUDE 2		A3	
	Date : 23/08/2016			
	 SAS SCHONT 68 rue saint exupéry 69124 colombier saugnieu		Ech. 1 : 50	Révision A
Chantier : 180				

Désignation	Repère	Longueur	Angle de coupe 1	Angle de coupe 2	Quantité	Largeur	Largeur boîte (mise à plat)	Masse
					1			19,73,02kg
	1				1	0,00mm	0,00mm	0,00kg
	2				1	0,00mm	0,00mm	19186,66kg
	3				6	0,00mm	0,00mm	13,37kg
	4	3320,00mm	0,00°	0,00°	1	0,00mm	0,00mm	12,04kg
	5	3320,00mm	0,00°	0,00°	1	0,00mm	0,00mm	12,04kg
	6	80,00mm	0,00°	0,00°	1			1,44kg
Cornière à ailes inégales 150 × 90 × 10, ISO 657-2	7	80,00mm	0,00°	0,00°	1			1,44kg
Cornière à ailes inégales 150 × 90 × 10, ISO 657-2	8	80,00mm	0,00°	0,00°	1			1,44kg
Cornière à ailes inégales 150 × 90 × 10, ISO 657-2	9	80,00mm	0,00°	0,00°	1			1,44kg
Cornière à ailes inégales 150 × 90 × 10, ISO 657-2	10	160,00mm	0,00°	0,00°	4			2,88kg
patte vitrage 60	11				24			
plat-50x5	12	1392,00mm	0,00°	0,00°	1	0,00mm	0,00mm	2,73kg
plat-50x5	13	1392,00mm	0,00°	0,00°	1	0,00mm	0,00mm	2,73kg
plat-50x10	14	1392,00mm	0,00°	0,00°	1	0,00mm	0,00mm	5,46kg
plat-50x10	15	1392,00mm	0,00°	0,00°	1	0,00mm	0,00mm	5,46kg
plat-50x10	16	1392,00mm	0,00°	0,00°	4	0,00mm	0,00mm	5,46kg
profil alu+joint	17	1075,00mm	0,00°	0,00°	6			
profil alu+joint	18	1075,00mm	0,00°	0,00°	6			
Profilé carré creux 40 × 2, ISO 4019	19	1095,00mm	0,00°	0,00°	12			2,52kg
tube 80x20	20	3320,00mm	0,00°	0,00°	1	0,00mm	0,00mm	7,58kg
tube 80x20	21	3320,00mm	0,00°	0,00°	1	0,00mm	0,00mm	7,58kg
vitrage	22				6	1075,00mm	571,00mm	13,50kg

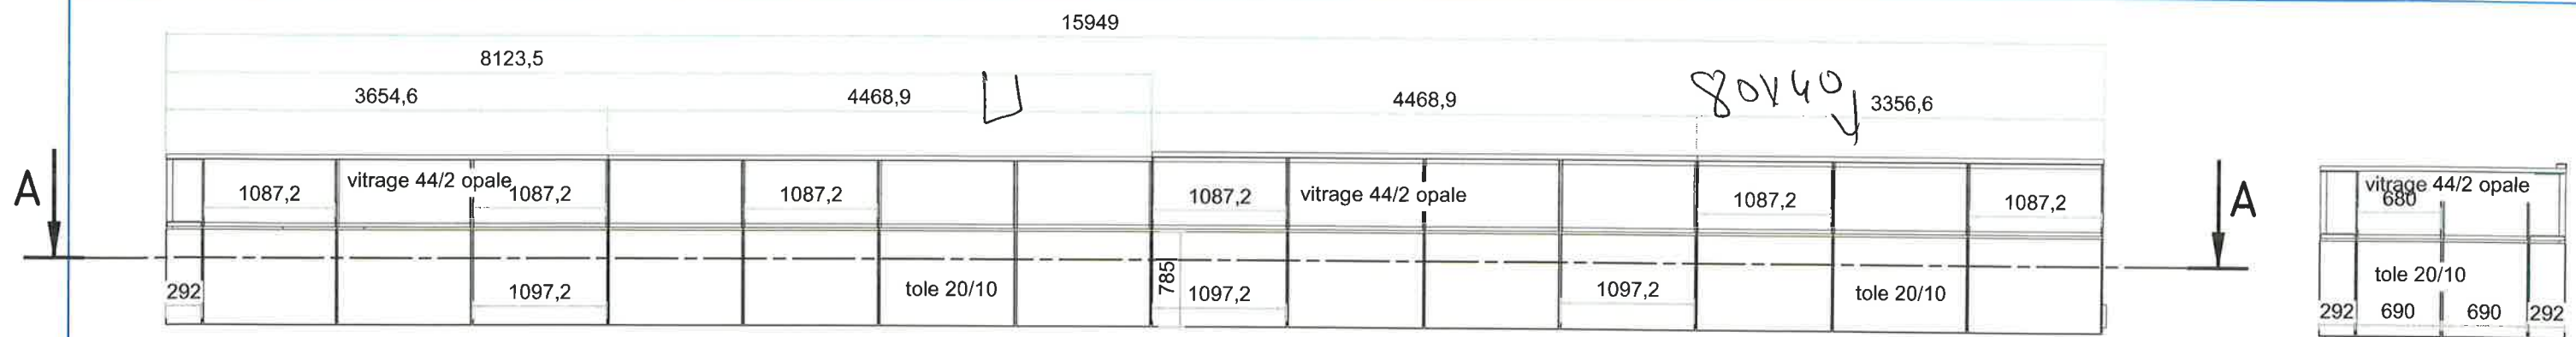


A - A

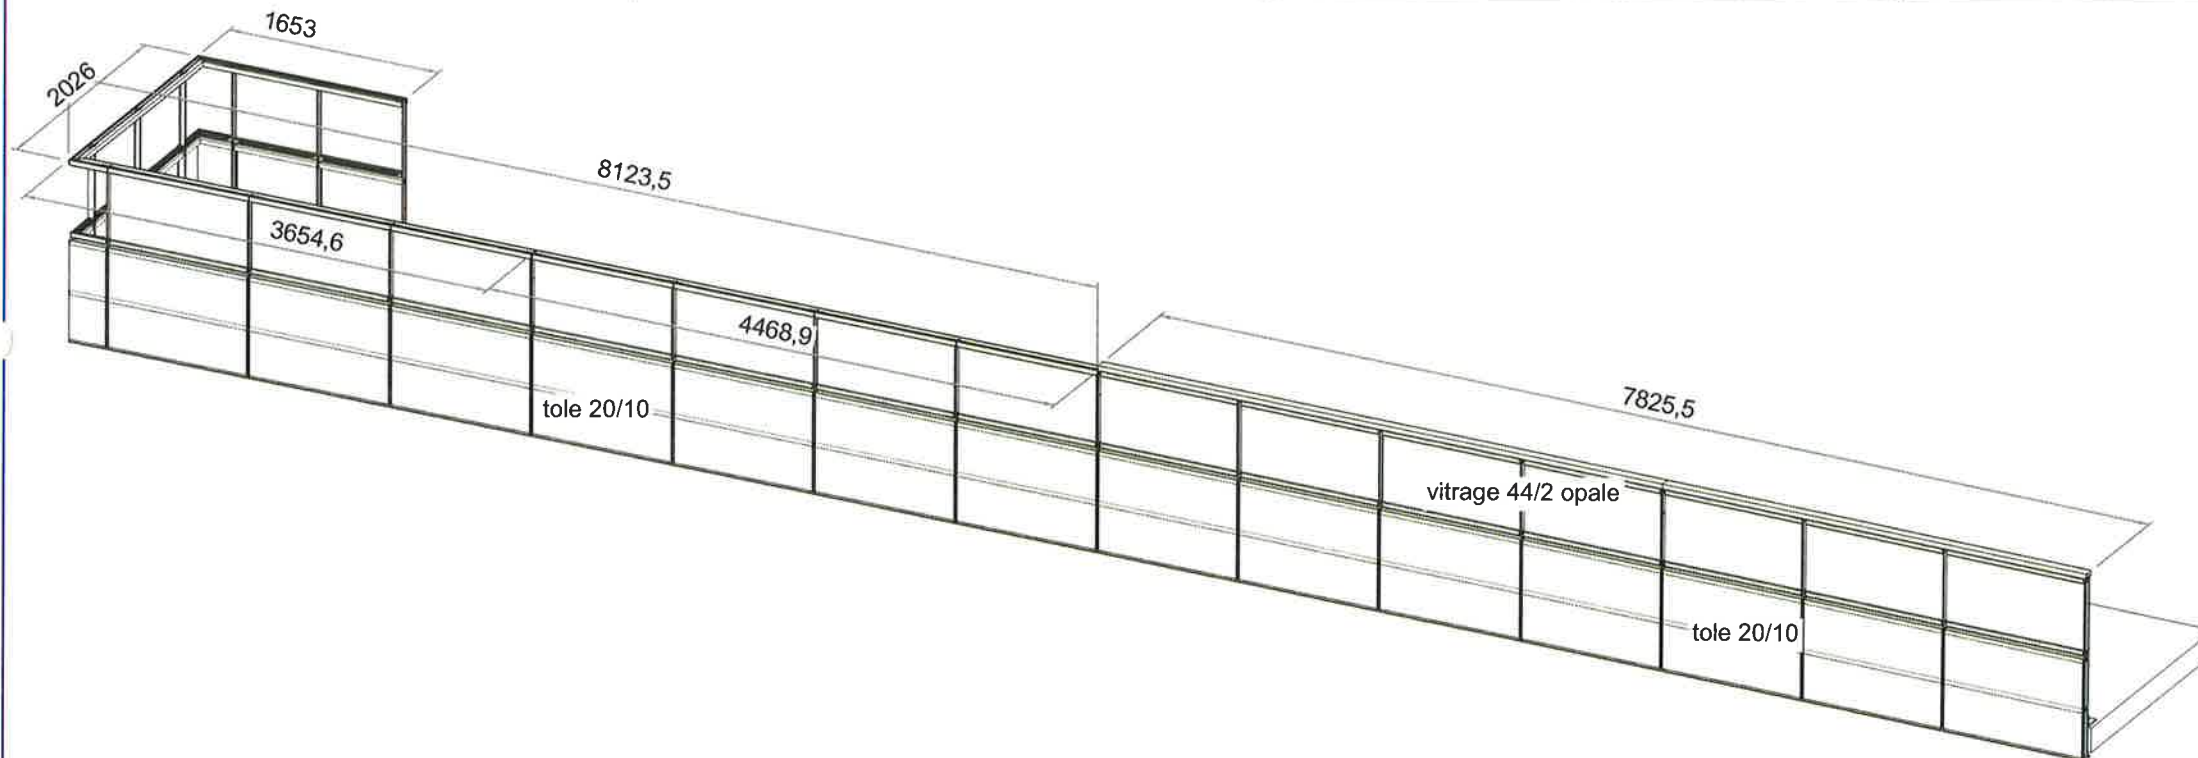
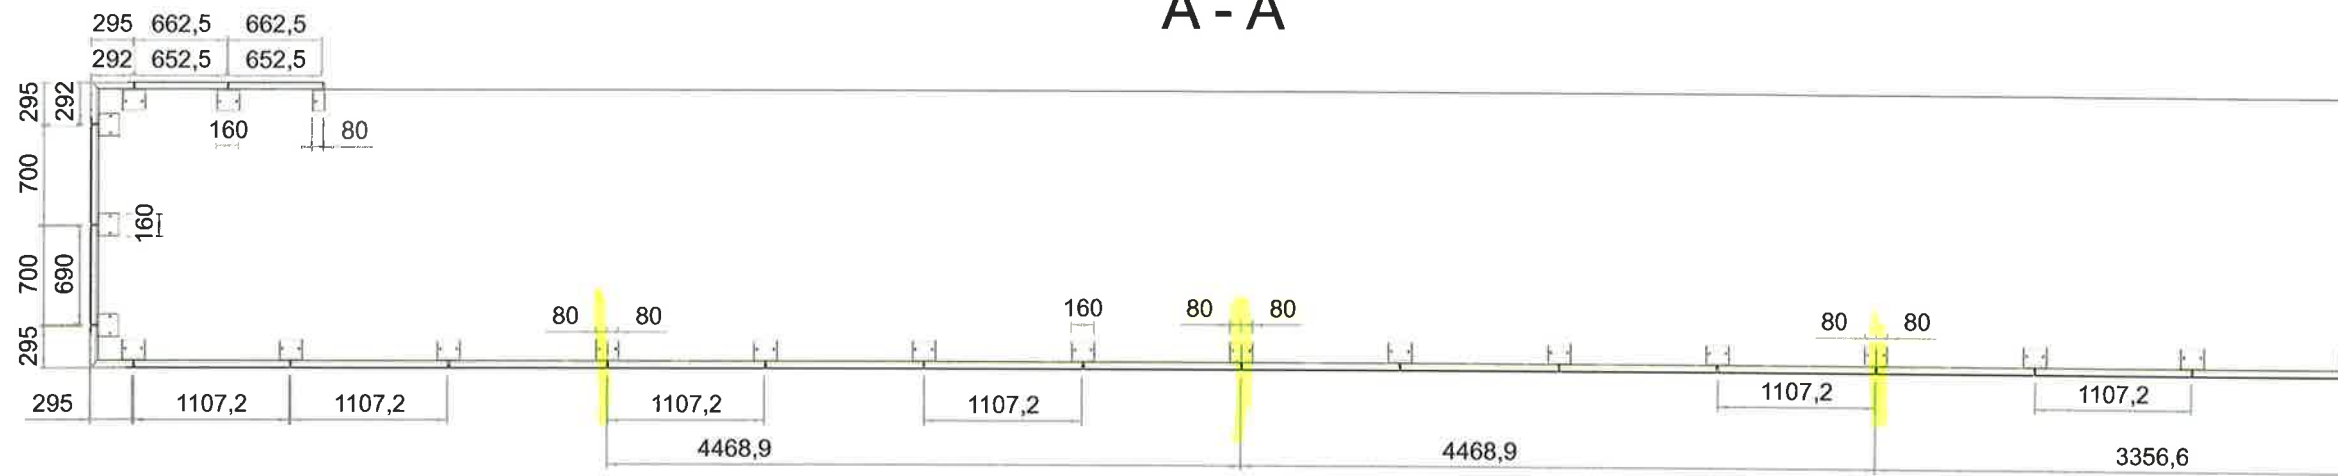



Désignation : GC-rep-3 bat A	Auteur : ETUDE 2		A3	
	Date : 23/08/2016			
Référence : CH0038		Ech. 1 : 100	Révision A	Page -
 SAS SCHONT 68 rue saint exupéry 69124 colombier saugnieu	Chantier : 180			

Désignation	Repère	Longueur	Angle de coupe 1	Angle de coupe 2	Quantité	Largeur boîte (mise à plat)	Largeur boîte (mise à plat)
	1				1		
	2				1	0,00mm	0,00mm
	3				1	0,00mm	0,00mm
	4				1	0,00mm	0,00mm
	5				1	0,00mm	0,00mm
	6				1	0,00mm	0,00mm
	7				1	0,00mm	0,00mm
	8				1	0,00mm	0,00mm
	9				14	0,00mm	0,00mm
	10	1653,00mm	0,00°	45,00°	1	0,00mm	0,00mm
	11	2026,00mm	45,00°	45,00°	1	0,00mm	0,00mm
	12	3654,64mm	45,00°	0,00°	1	0,00mm	0,00mm
	13	4468,86mm	0,00°	0,00°	1	0,00mm	0,00mm
Cornière à ailes inégales 150 x 90 x 10, ISO 657-2	14	80,00mm	0,00°	0,00°	1		
Cornière à ailes inégales 150 x 90 x 10, ISO 657-2	15	80,00mm	0,00°	0,00°	1		
Cornière à ailes inégales 150 x 90 x 10, ISO 657-2	16	80,00mm	0,00°	0,00°	3		
Cornière à ailes inégales 150 x 90 x 10, ISO 657-2	17	80,00mm	0,00°	0,00°	3		
Cornière à ailes inégales 150 x 90 x 10, ISO 657-2	18	160,00mm	0,00°	0,00°	16		
patte vitrage 60	19				80		
plat-50x5	20	1392,00mm	0,00°	0,00°	3	0,00mm	0,00mm
plat-50x5	21	1392,00mm	0,00°	0,00°	3	0,00mm	0,00mm
plat-50x10	22	1392,00mm	0,00°	0,00°	1	0,00mm	0,00mm
plat-50x10	23	1392,00mm	0,00°	0,00°	1	0,00mm	0,00mm
plat-50x10	24	1392,00mm	0,00°	0,00°	16	0,00mm	0,00mm
profil alu+joint	25	280,00mm	0,00°	45,00°	1		
profil alu+joint	26	280,00mm	0,00°	45,00°	1		
profil alu+joint	27	280,00mm	0,00°	45,00°	1		
profil alu+joint	28	280,00mm	0,00°	45,00°	1		
profil alu+joint	29	280,00mm	45,00°	0,00°	1		
profil alu+joint	30	280,00mm	45,00°	0,00°	1		
profil alu+joint	31	280,00mm	45,00°	0,00°	1		
profil alu+joint	32	280,00mm	45,00°	0,00°	1		
profil alu+joint	33	642,00mm	0,00°	0,00°	2		
profil alu+joint	34	642,00mm	0,00°	0,00°	2		
profil alu+joint	35	680,00mm	0,00°	0,00°	2		
profil alu+joint	36	680,00mm	0,00°	0,00°	2		
profil alu+joint	37	1087,21mm	0,00°	0,00°	14		
profil alu+joint	38	1087,21mm	0,00°	0,00°	14		
Profilé carré creux 40 x 2, ISO 4019	39	295,00mm	45,00°	0,00°	1		
Profilé carré creux 40 x 2, ISO 4019	40	295,00mm	45,00°	0,00°	1		
Profilé carré creux 40 x 2, ISO 4019	41	295,00mm	45,00°	0,00°	1		
Profilé carré creux 40 x 2, ISO 4019	42	295,00mm	45,00°	0,00°	1		
Profilé carré creux 40 x 2, ISO 4019	43	295,00mm	45,00°	0,00°	1		
Profilé carré creux 40 x 2, ISO 4019	44	295,00mm	45,00°	0,00°	1		
Profilé carré creux 40 x 2, ISO 4019	45	295,00mm	45,00°	0,00°	1		
Profilé carré creux 40 x 2, ISO 4019	46	295,00mm	45,00°	0,00°	1		
Profilé carré creux 40 x 2, ISO 4019	47	662,50mm	0,00°	0,00°	4		
Profilé carré creux 40 x 2, ISO 4019	48	700,00mm	0,00°	0,00°	4		
Profilé carré creux 40 x 2, ISO 4019	49	1107,21mm	0,00°	0,00°	28		
tube 80x20	50	1650,00mm	0,00°	45,00°	1	0,00mm	0,00mm
tube 80x20	51	2020,00mm	45,00°	45,00°	1	0,00mm	0,00mm
tube 80x20	52	3651,64mm	45,00°	0,00°	1	0,00mm	0,00mm
tube 80x20	53	12294,36mm	0,00°	0,00°	1	0,00mm	0,00mm
tube 80x40	54	3356,64mm	0,00°	0,00°	1	0,00mm	0,00mm
tube 80x40	55	4468,86mm	0,00°	0,00°	1	0,00mm	0,00mm
vitrage	56				2	642,00mm	571,00mm
vitrage	57				2	680,00mm	571,00mm
vitrage	58				14	1087,21mm	571,00mm

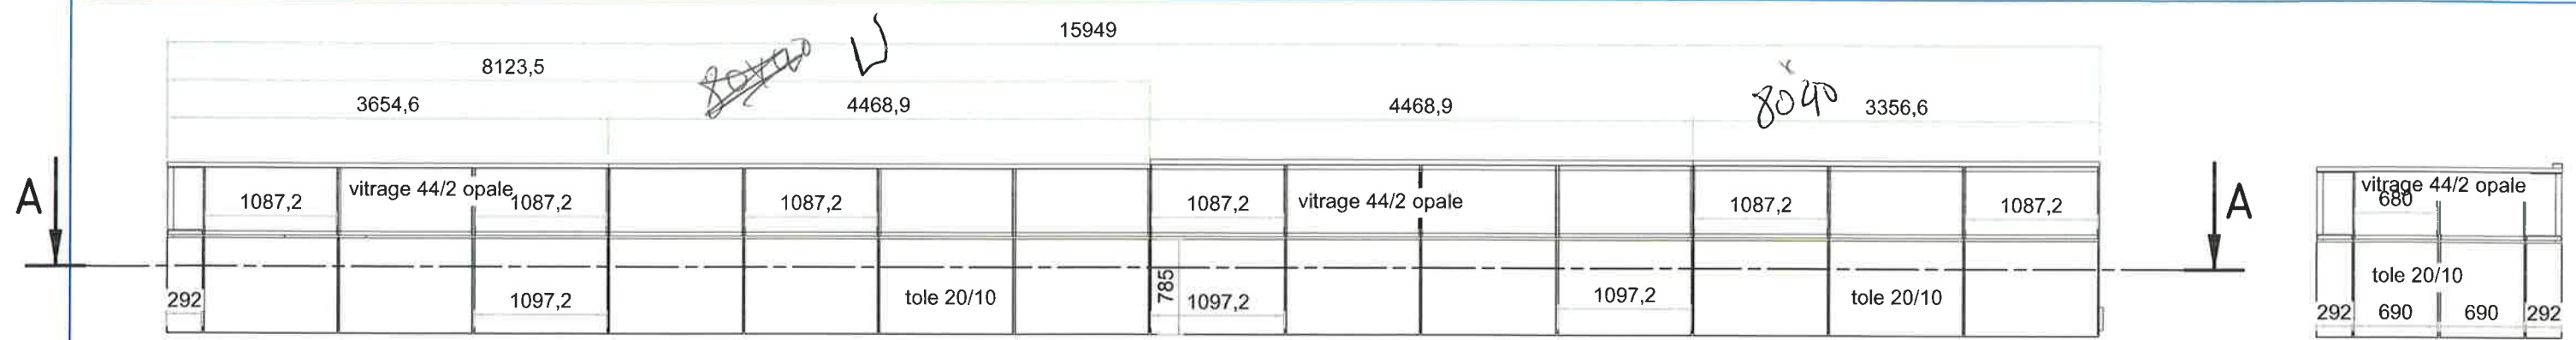

A - A

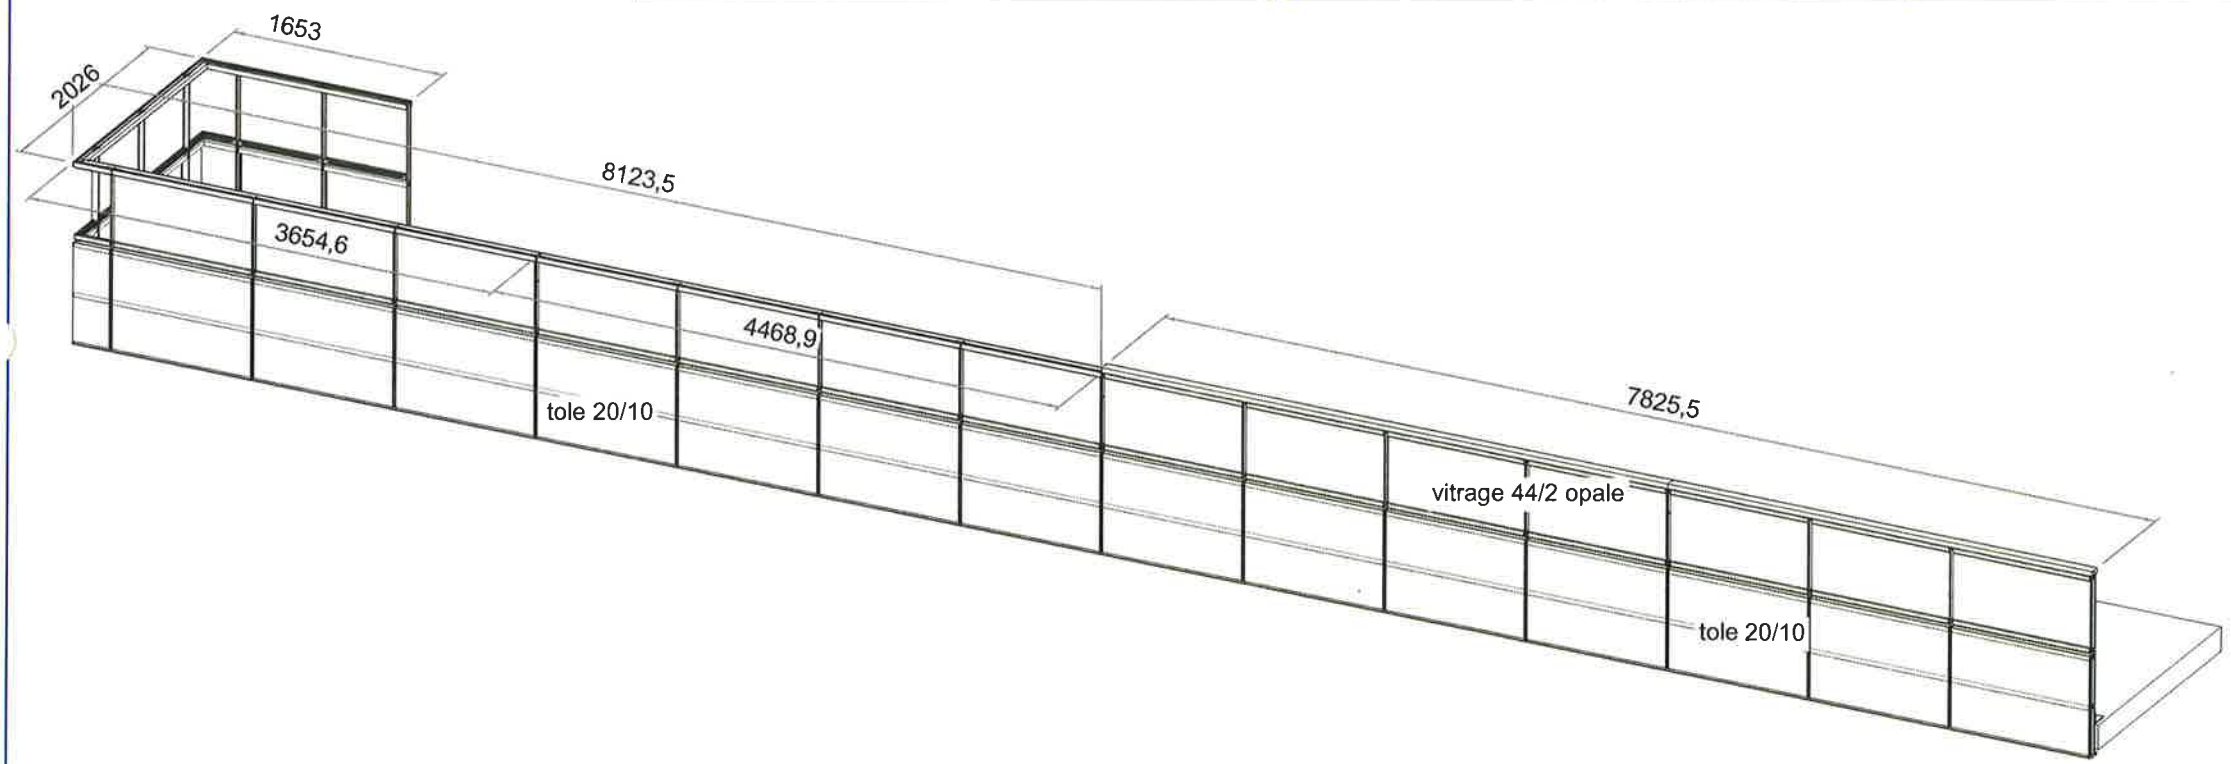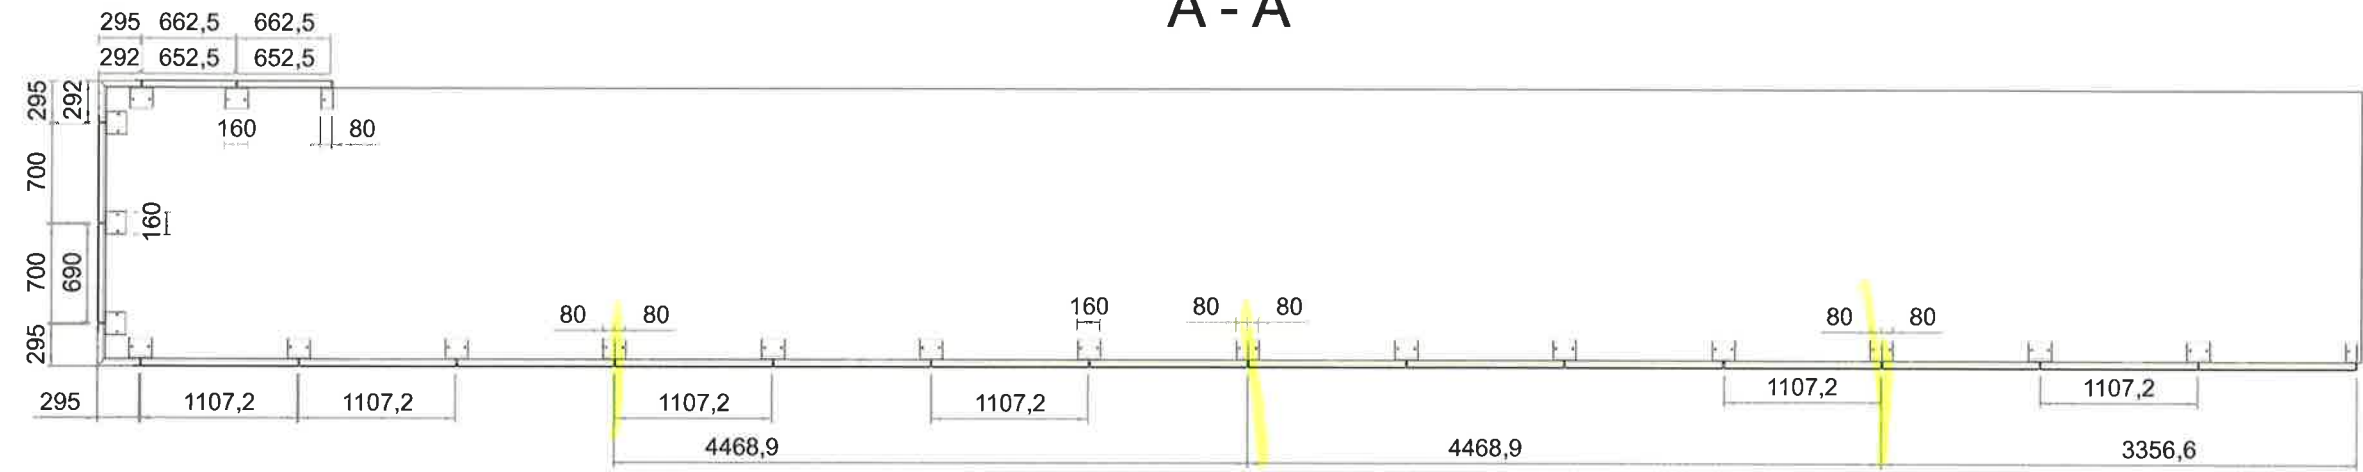

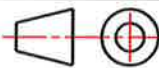Désignation : GC-rep-4 bat A	Auteur : ETUDE 2		A3	
Référence : CH0038	Date : 23/08/2016			
		Ech. 1 : 100	Révision A	Page -
		Chantier : 180		
		SAS SCHONT 68 rue saint exupéry 69124 colombier saugnieu		

Désignation	Repère	Longueur	Angle de coupe 1	Angle de coupe 2	Quantité	Largeur boîte (mise à plat)	Largeur boîte (mise à plat)
					1		
1					1	0,00mm	0,00mm
2					1	0,00mm	0,00mm
3					1	0,00mm	0,00mm
4					1	0,00mm	0,00mm
5					1	0,00mm	0,00mm
6					1	0,00mm	0,00mm
7					1	0,00mm	0,00mm
8					1	0,00mm	0,00mm
9					14	0,00mm	0,00mm
10		1653,00mm	0,00°	45,00°	1	0,00mm	0,00mm
11		2026,00mm	45,00°	45,00°	1	0,00mm	0,00mm
12		3654,64mm	45,00°	0,00°	1	0,00mm	0,00mm
13		4468,86mm	0,00°	0,00°	1	0,00mm	0,00mm
14	Cornière à ailes inégales 150 x 90 x 10, ISO 657-2	80,00mm	0,00°	0,00°	1		
15	Cornière à ailes inégales 150 x 90 x 10, ISO 657-2	80,00mm	0,00°	0,00°	1		
16	Cornière à ailes inégales 150 x 90 x 10, ISO 657-2	80,00mm	0,00°	0,00°	3		
17	Cornière à ailes inégales 150 x 90 x 10, ISO 657-2	80,00mm	0,00°	0,00°	3		
18	Cornière à ailes inégales 150 x 90 x 10, ISO 657-2	160,00mm	0,00°	0,00°	16		
19	patte vitrage 60				80		
20	plat-50x5	1392,00mm	0,00°	0,00°	3	0,00mm	0,00mm
21	plat-50x5	1392,00mm	0,00°	0,00°	3	0,00mm	0,00mm
22	plat-50x10	1392,00mm	0,00°	0,00°	1	0,00mm	0,00mm
23	plat-50x10	1392,00mm	0,00°	0,00°	1	0,00mm	0,00mm
24	plat-50x10	1392,00mm	0,00°	0,00°	16	0,00mm	0,00mm
25	profil alu+joint	280,00mm	0,00°	45,00°	1		
26	profil alu+joint	280,00mm	0,00°	45,00°	1		
27	profil alu+joint	280,00mm	0,00°	45,00°	1		
28	profil alu+joint	280,00mm	0,00°	45,00°	1		
29	profil alu+joint	280,00mm	45,00°	0,00°	1		
30	profil alu+joint	280,00mm	45,00°	0,00°	1		
31	profil alu+joint	280,00mm	45,00°	0,00°	1		
32	profil alu+joint	280,00mm	45,00°	0,00°	1		
33	profil alu+joint	642,00mm	0,00°	0,00°	2		
34	profil alu+joint	642,00mm	0,00°	0,00°	2		
35	profil alu+joint	680,00mm	0,00°	0,00°	2		
36	profil alu+joint	680,00mm	0,00°	0,00°	2		
37	profil alu+joint	1087,21mm	0,00°	0,00°	14		
38	profil alu+joint	1087,21mm	0,00°	0,00°	14		
39	Profilé carré creux 40 x 2, ISO 4019	295,00mm	45,00°	0,00°	1		
40	Profilé carré creux 40 x 2, ISO 4019	295,00mm	45,00°	0,00°	1		
41	Profilé carré creux 40 x 2, ISO 4019	295,00mm	45,00°	0,00°	1		
42	Profilé carré creux 40 x 2, ISO 4019	295,00mm	45,00°	0,00°	1		
43	Profilé carré creux 40 x 2, ISO 4019	295,00mm	45,00°	0,00°	1		
44	Profilé carré creux 40 x 2, ISO 4019	295,00mm	45,00°	0,00°	1		
45	Profilé carré creux 40 x 2, ISO 4019	295,00mm	45,00°	0,00°	1		
46	Profilé carré creux 40 x 2, ISO 4019	295,00mm	45,00°	0,00°	1		
47	Profilé carré creux 40 x 2, ISO 4019	662,50mm	0,00°	0,00°	4		
48	Profilé carré creux 40 x 2, ISO 4019	700,00mm	0,00°	0,00°	4		
49	Profilé carré creux 40 x 2, ISO 4019	1107,21mm	0,00°	0,00°	28		
50	tube 80x20	1650,00mm	0,00°	45,00°	1	0,00mm	0,00mm
51	tube 80x20	2020,00mm	45,00°	45,00°	1	0,00mm	0,00mm
52	tube 80x20	3651,64mm	45,00°	0,00°	1	0,00mm	0,00mm
53	tube 80x20	12294,36mm	0,00°	0,00°	1	0,00mm	0,00mm
54	tube 80x40	3356,64mm	0,00°	0,00°	1	0,00mm	0,00mm
55	tube 80x40	4468,86mm	0,00°	0,00°	1	0,00mm	0,00mm
56	vitrage				2	642,00mm	571,00mm
57	vitrage				2	680,00mm	571,00mm
58	vitrage				14	1087,21mm	571,00mm

u 80 x 40 x 3

80

40

50

30

35

2

17

595

1392

1415

347,5

40

10

40

162,5

225

90

150

35


20

80

tube 80 x 20

A - A

Technical drawing of a roof plan. The drawing shows a rectangular layout with dimensions and structural elements. The overall dimensions are 7337 (width) and 7277 (height). The plan is divided into sections with dimensions: 80, 160, 80, 80, 160, and 80. The horizontal segments are labeled 1028,1, 1028,1, 1028,1, 1028,1, 1028,1, and 2066,3. The vertical segments are labeled 80, 160, 80, 80, 160, and 80. The drawing includes a grid of lines and a central rectangular area.

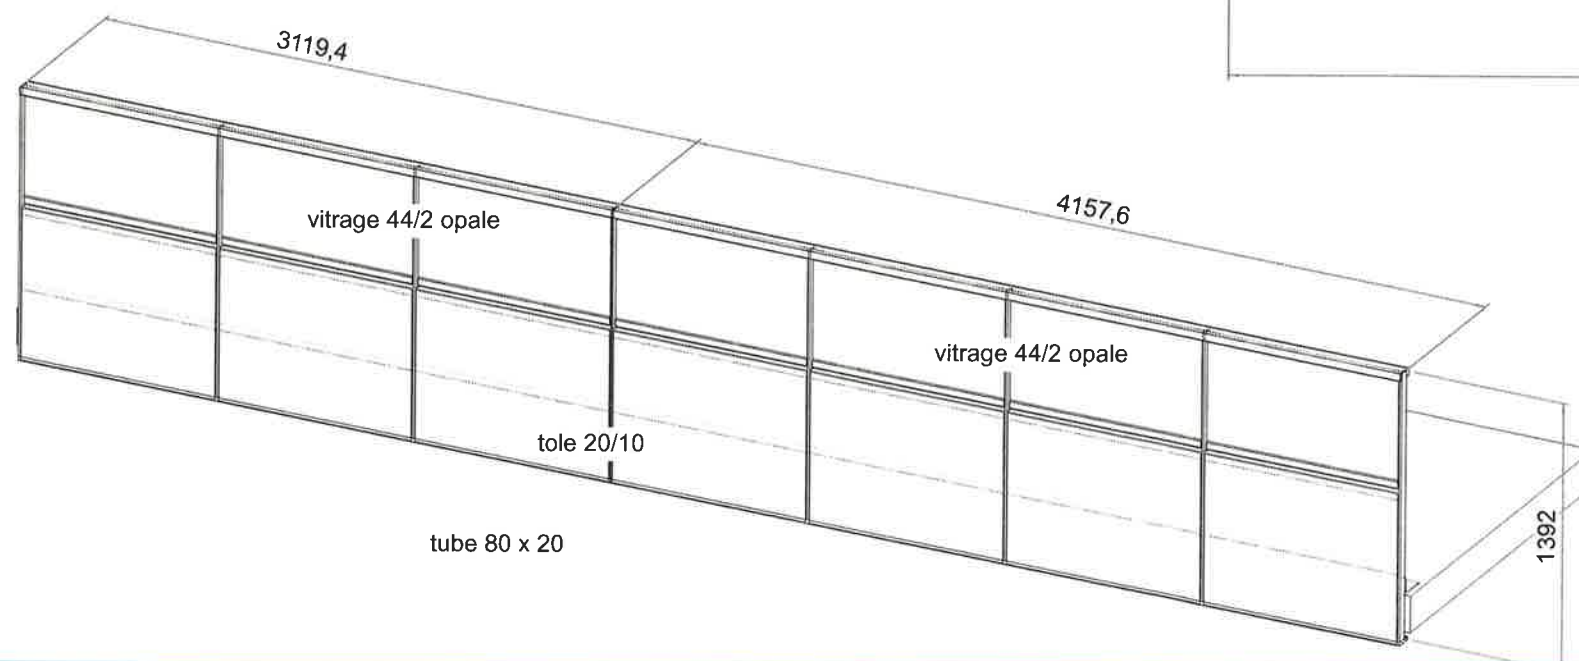

Désignation : GC-rep-5 bat b	Auteur : ETUDE 2		A3	
	Date : 24/08/2016			
Référence : CH0038		Ech. 1 : 50	Révision	Page
			A	-
 SAS SCHONT 68 rue saint exupéry 69124 colombier saugnieu		Chantier : 180		

Désignation	Repère	Longueur	Angle de coupe 1	Angle de coupe 2	Quantité	Largeur	Largeur boîte (mise à plat)	Masse
					1			21327,39kg
	1				1	0,00mm	0,00mm	0,00kg
	2				1	0,00mm	0,00mm	21010,82kg
	3				7	0,00mm	0,00mm	12,55kg
	4	4157,57mm	0,00°	0,00°	1	0,00mm	0,00mm	15,08kg
	5	3119,43mm	0,00°	0,00°	1	0,00mm	0,00mm	11,31kg
	6	80,00mm	0,00°	0,00°	1			1,44kg
Cornière à ailes inégales 150 × 90 × 10, ISO 657-2	7	80,00mm	0,00°	0,00°	1			1,44kg
Cornière à ailes inégales 150 × 90 × 10, ISO 657-2	8	80,00mm	0,00°	0,00°	1			1,44kg
Cornière à ailes inégales 150 × 90 × 10, ISO 657-2	9	80,00mm	0,00°	0,00°	1			1,44kg
Cornière à ailes inégales 150 × 90 × 10, ISO 657-2	10	160,00mm	0,00°	0,00°	5			2,88kg
patte vitrage 60	11				28			
plat-50x5	12	1392,00mm	0,00°	0,00°	1	0,00mm	0,00mm	2,73kg
plat-50x5	13	1392,00mm	0,00°	0,00°	1	0,00mm	0,00mm	2,73kg
plat-50x10	14	1392,00mm	0,00°	0,00°	1	0,00mm	0,00mm	5,46kg
plat-50x10	15	1392,00mm	0,00°	0,00°	1	0,00mm	0,00mm	5,46kg
plat-50x10	16	1392,00mm	0,00°	0,00°	5	0,00mm	0,00mm	5,46kg
profil alu+joint	17	1008,14mm	0,00°	0,00°	7			
profil alu+joint	18	1008,14mm	0,00°	0,00°	7			
Profilé carré creux 40 × 2, ISO 4019	19	1028,14mm	0,00°	0,00°	14			
tube 80x20	20	4157,57mm	0,00°	0,00°	1	0,00mm	0,00mm	2,37kg
tube 80x20	21	3119,43mm	0,00°	0,00°	1	0,00mm	0,00mm	9,50kg
vitrage	22				7	1008,14mm	571,00mm	7,13kg
								12,66kg

u 80 x 40 x 3

80

40

50

30

35

2

17

595

1392

1415

347,5

40

10

40

90

150

20

35

162,5

225

80

tube 80 x 20

A - A

Technical drawing of a building facade section, showing structural details, dimensions, and material specifications.

Dimensions and Measurements:

- Overall width: 7277
- Overall height: 1415
- Section cut A-A: 3119,4 (width of cut), 4157,6 (width of remaining section)
- Section cut B-B: 1392 (width of cut), 785 (width of remaining section)
- Height of upper section: 40
- Height of lower section: 1018,1
- Height of middle section: 1018,1
- Height of bottom section: 1018,1

Structural Details and Materials:

- Top horizontal member: u 80 x 40 x 3
- Bottom horizontal member: tube 80 x 20
- Vertical members: u 80 x 40 x 3
- Wall/Partition: vitrage 44/2 opale
- Internal Partition: toile 20/10


Dimensions and Measurements:

- Overall width: 7277
- Overall height: 1415
- Section cut A-A: 3119,4 (width of cut), 4157,6 (width of remaining section)
- Section cut B-B: 1392 (width of cut), 785 (width of remaining section)
- Height of upper section: 40
- Height of lower section: 1018,1
- Height of middle section: 1018,1
- Height of bottom section: 1018,1

Structural Details and Materials:

- Top horizontal member: u 80 x 40 x 3
- Bottom horizontal member: tube 80 x 20
- Vertical members: u 80 x 40 x 3
- Wall/Partition: vitrage 44/2 opale
- Internal Partition: toile 20/10




Technical drawing of a roof plan showing a rectangular layout with dimensions and structural elements. The drawing includes a central horizontal section with a width of 7337 and a total length of 7277. The section is divided into segments with widths of 1028,1, 1028,1, 1028,1, 1028,1, 1028,1, and 2066,3. Structural elements are indicated by small squares and rectangles, with dimensions 80, 160, 80, 80, 160, and 80. Two yellow highlights are present on the drawing.

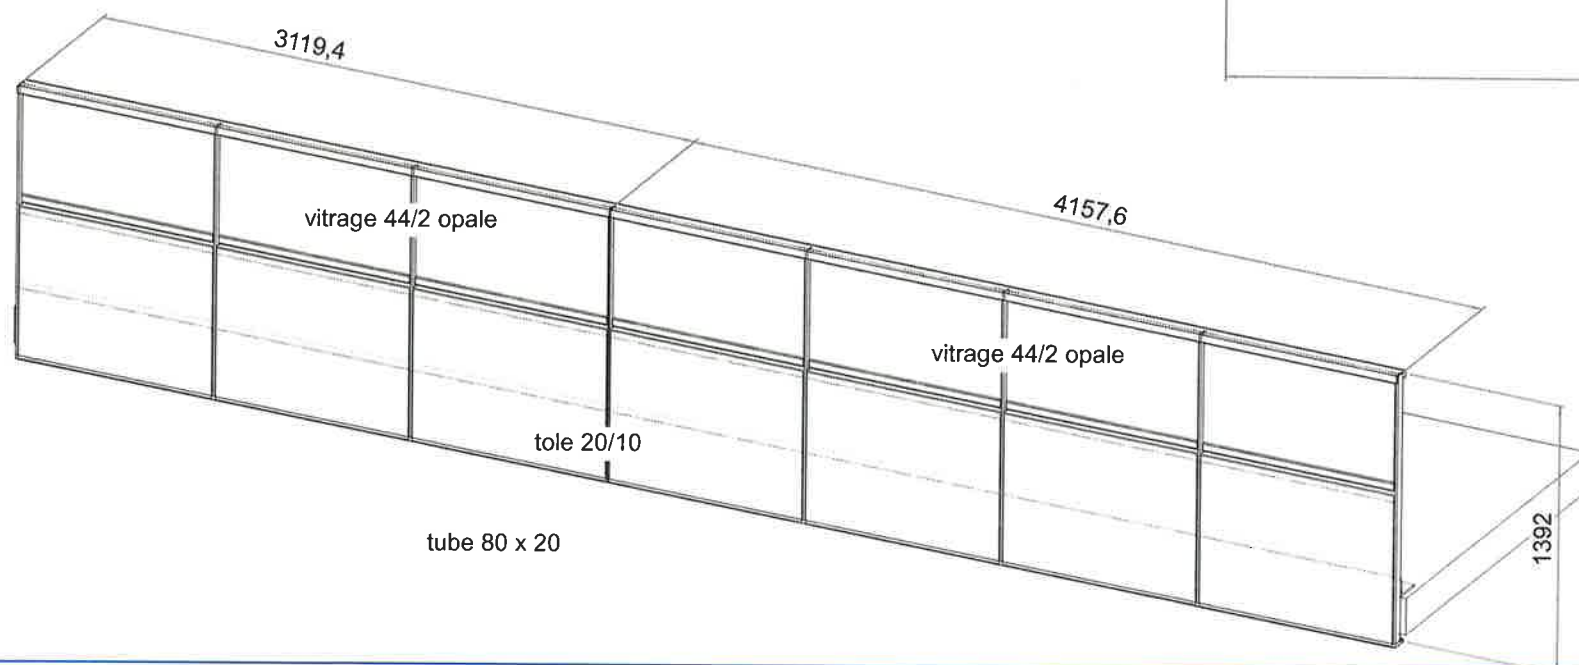

Désignation : GC-rep-6 bat b	Auteur : ETUDE 2		A3		
	Date : 24/08/2016				
Référence : CH0038			Ech. 1 : 50	Révision A	Page -
			Chantier : 180		

Désignation	Repère	Longueur	Angle de coupe 1	Angle de coupe 2	Quantité	Longueur sur boîte (mise à plat)	Largeur boîte (mise à plat)	Masse
					1			21327,39kg
	1				1	0,00mm	0,00mm	0,00kg
	2				1	0,00mm	0,00mm	21010,82kg
	3				7	0,00mm	0,00mm	12,55kg
	4	4157,57mm	0,00°	0,00°	1	0,00mm	0,00mm	15,08kg
	5	3119,43mm	0,00°	0,00°	1	0,00mm	0,00mm	11,31kg
	6	80,00mm	0,00°	0,00°	1			1,44kg
	7	80,00mm	0,00°	0,00°	1			1,44kg
	8	80,00mm	0,00°	0,00°	1			1,44kg
	9	80,00mm	0,00°	0,00°	1			1,44kg
	10	160,00mm	0,00°	0,00°	5			2,88kg
	11				28			
	12	1392,00mm	0,00°	0,00°	1	0,00mm	0,00mm	2,73kg
	13	1392,00mm	0,00°	0,00°	1	0,00mm	0,00mm	2,73kg
	14	1392,00mm	0,00°	0,00°	1	0,00mm	0,00mm	5,46kg
	15	1392,00mm	0,00°	0,00°	1	0,00mm	0,00mm	5,46kg
	16	1392,00mm	0,00°	0,00°	5	0,00mm	0,00mm	5,46kg
	17	1008,14mm	0,00°	0,00°	7			
	18	1008,14mm	0,00°	0,00°	7			
	19	1028,14mm	0,00°	0,00°	14			2,37kg
	20	4157,57mm	0,00°	0,00°	1	0,00mm	0,00mm	9,50kg
	21	3119,43mm	0,00°	0,00°	1	0,00mm	0,00mm	7,13kg
	22				7	1008,14mm	571,00mm	12,66kg


Rep = 8

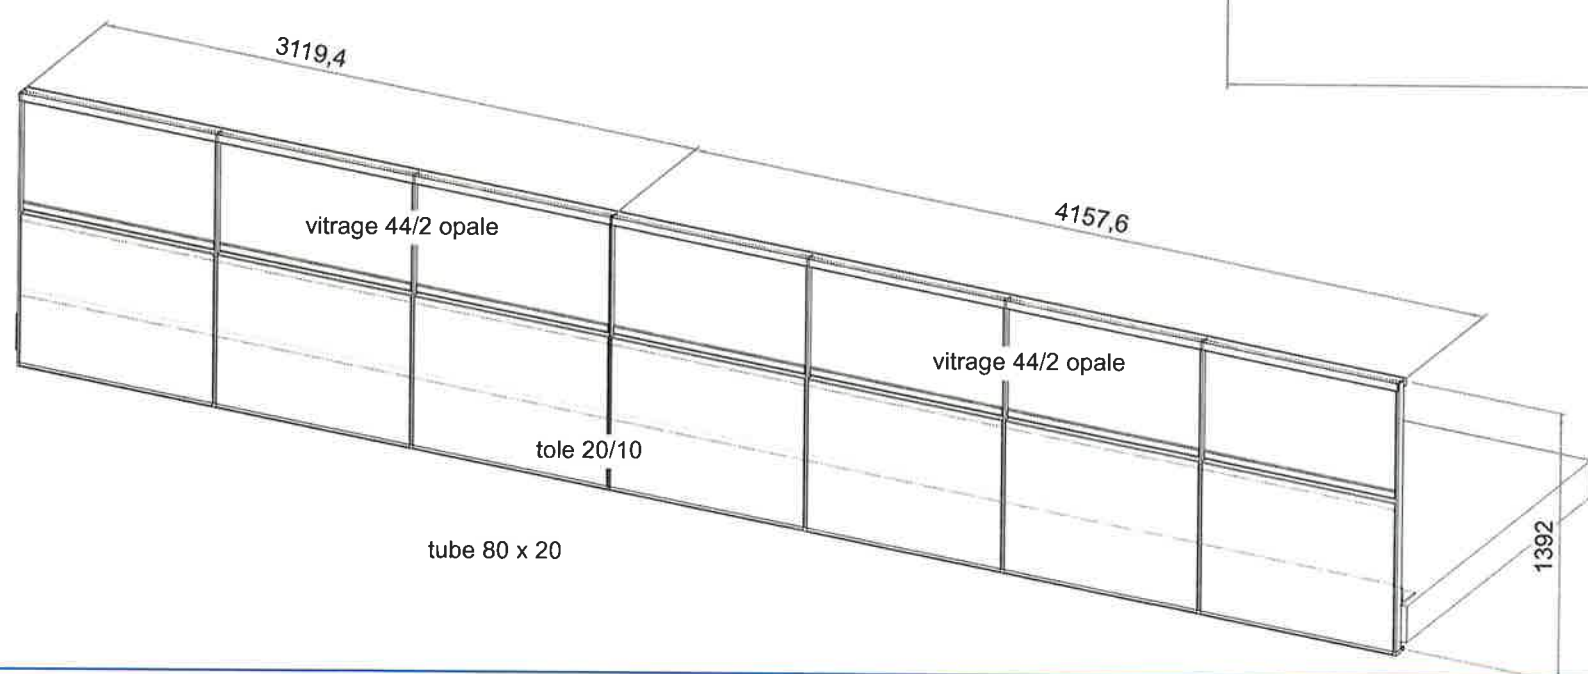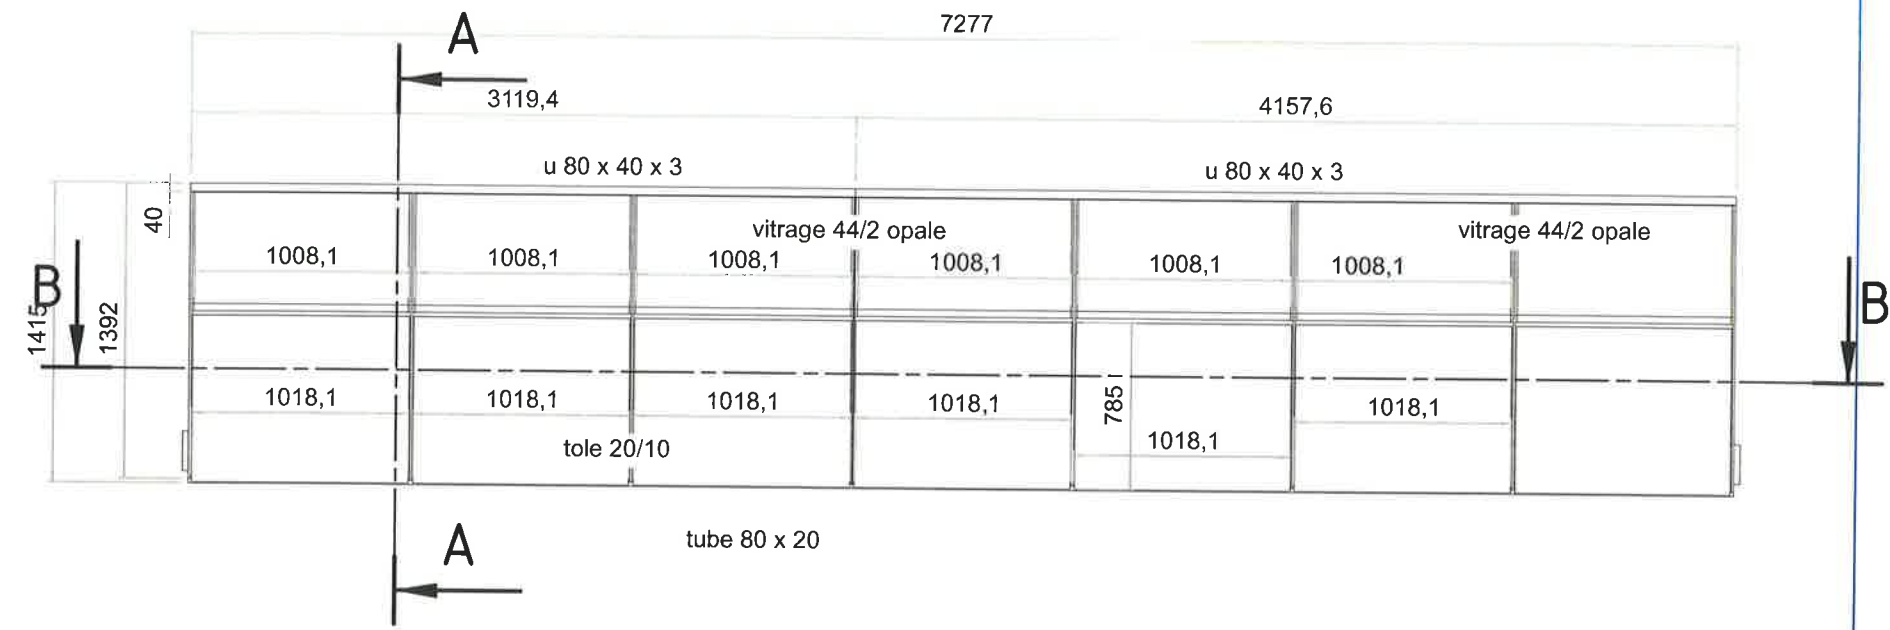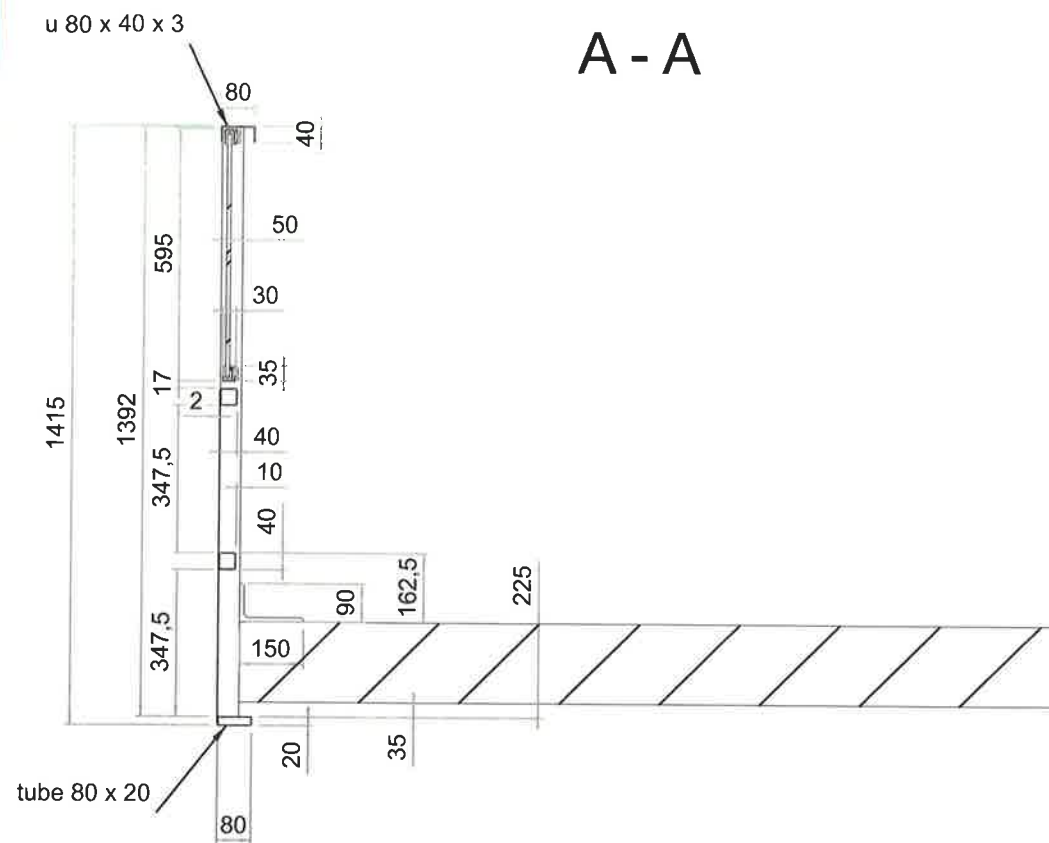

Désignation : GC-rep-7 bat b	Auteur : ETUDE 2		A3	
	Date : 24/08/2016			
Référence : CH0038		Ech. 1 : 50	Révision A	Page -
		Chantier : 180		
 SAS SCHONT 68 rue saint exupéry 69124 colombier saugnieu				

Désignation	Repère	Longueur	Angle de coupe 1	Angle de coupe 2	Quantité	Largeur	Largeur boîte (mise à plat)	Masse
					1			21327,39kg
	1				1	0,00mm	0,00mm	0,00kg
	2				1	0,00mm	0,00mm	21010,82kg
	3				7	0,00mm	0,00mm	12,55kg
	4	4157,57mm	0,00°	0,00°	1	0,00mm	0,00mm	15,08kg
	5	3119,43mm	0,00°	0,00°	1	0,00mm	0,00mm	11,31kg
	6	80,00mm	0,00°	0,00°	1			1,44kg
Cornière à ailes inégales 150 × 90 × 10, ISO 657-2	7	80,00mm	0,00°	0,00°	1			1,44kg
Cornière à ailes inégales 150 × 90 × 10, ISO 657-2	8	80,00mm	0,00°	0,00°	1			1,44kg
Cornière à ailes inégales 150 × 90 × 10, ISO 657-2	9	80,00mm	0,00°	0,00°	1			1,44kg
Cornière à ailes inégales 150 × 90 × 10, ISO 657-2	10	160,00mm	0,00°	0,00°	5			2,88kg
patte vitrage 60	11				28			
plat-50x5	12	1392,00mm	0,00°	0,00°	1	0,00mm	0,00mm	2,73kg
plat-50x5	13	1392,00mm	0,00°	0,00°	1	0,00mm	0,00mm	2,73kg
plat-50x10	14	1392,00mm	0,00°	0,00°	1	0,00mm	0,00mm	5,46kg
plat-50x10	15	1392,00mm	0,00°	0,00°	1	0,00mm	0,00mm	5,46kg
plat-50x10	16	1392,00mm	0,00°	0,00°	5	0,00mm	0,00mm	5,46kg
profil alu+joint	17	1008,14mm	0,00°	0,00°	7			
profil alu+joint	18	1008,14mm	0,00°	0,00°	7			
Profilé carré creux 40 × 2, ISO 4019	19	1028,14mm	0,00°	0,00°	14			2,37kg
tube 80x20	20	4157,57mm	0,00°	0,00°	1	0,00mm	0,00mm	9,50kg
tube 80x20	21	3119,43mm	0,00°	0,00°	1	0,00mm	0,00mm	7,13kg
vitrage	22				7	1008,14mm	571,00mm	12,66kg

Désignation	Repère	Longueur	Angle de coupe 1	Angle de coupe 2	Quantité	Largeur sur boîte (mise à plat)	Largeur boîte (mise à plat)	Masse
					1			21405,58kg
	1				1	0,00mm	0,00mm	0,00kg
	2				1	0,00mm	0,00mm	21088,14kg
	3				7	0,00mm	0,00mm	12,60kg
	4	4173,00mm	0,00°	0,00°	1	0,00mm	0,00mm	15,13kg
	5	3131,00mm	0,00°	0,00°	1	0,00mm	0,00mm	11,36kg
	6	80,00mm	0,00°	0,00°	1			1,44kg
Cornière à ailes inégales 150 × 90 × 10, ISO 657-2								
Cornière à ailes inégales 150 × 90 × 10, ISO 657-2	7	80,00mm	0,00°	0,00°	1			1,44kg
Cornière à ailes inégales 150 × 90 × 10, ISO 657-2	8	80,00mm	0,00°	0,00°	1			1,44kg
Cornière à ailes inégales 150 × 90 × 10, ISO 657-2	9	80,00mm	0,00°	0,00°	1			1,44kg
Cornière à ailes inégales 150 × 90 × 10, ISO 657-2	10	160,00mm	0,00°	0,00°	5			2,88kg
patte vitrage 60	11				28			
plat-50x5	12	1392,00mm	0,00°	0,00°	1	0,00mm	0,00mm	2,73kg
plat-50x5	13	1392,00mm	0,00°	0,00°	1	0,00mm	0,00mm	2,73kg
plat-50x10	14	1392,00mm	0,00°	0,00°	1	0,00mm	0,00mm	5,46kg
plat-50x10	15	1392,00mm	0,00°	0,00°	1	0,00mm	0,00mm	5,46kg
plat-50x10	16	1392,00mm	0,00°	0,00°	5	0,00mm	0,00mm	5,46kg
profil alu+joint	17	1012,00mm	0,00°	0,00°	7			
profil alu+joint	18	1012,00mm	0,00°	0,00°	7			
Profilé carré creux 40 × 2, ISO 4019	19	1032,00mm	0,00°	0,00°	14			2,38kg
tube 80x20	20	4173,00mm	0,00°	0,00°	1	0,00mm	0,00mm	9,53kg
tube 80x20	21	3131,00mm	0,00°	0,00°	1	0,00mm	0,00mm	7,15kg
vitrage	22				7	1012,00mm	571,00mm	12,71kg

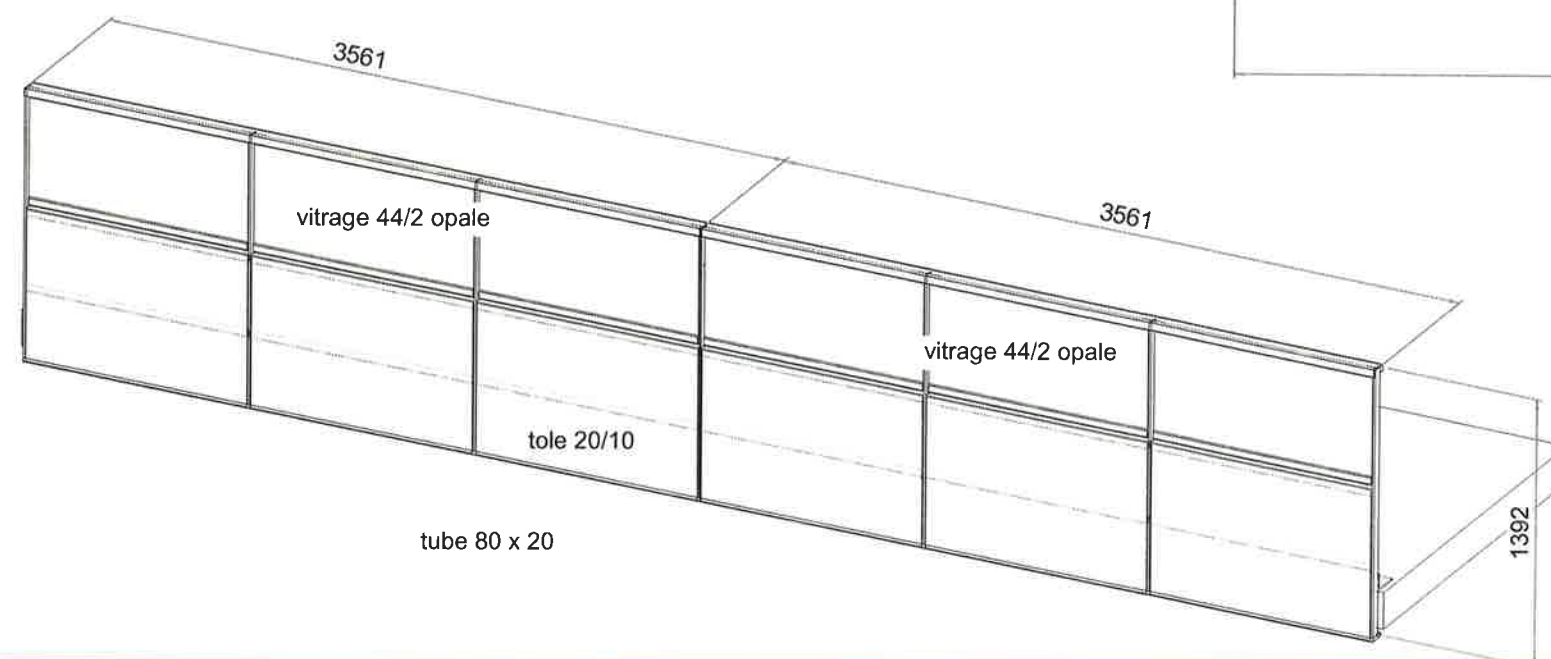

Désignation : GC-rep-9 bat b	Auteur : ETUDE 2		A3		
Référence : CH0038	Date : 24/08/2016				
 SAS SCHONT 68 rue saint exupéry 69124 colombier saugnieu			Ech. 1 : 50	Révision A	Page -
	Chantier : 180				

Désignation	Repère	Longueur	Angle de coupe 1	Angle de coupe 2	Quantité	largeur sur boîte (mise à plat)	Largeur boîte (mise à plat)	Masse
					1			20873,88kg
	1				1	0,00mm	0,00mm	0,00kg
	2				1	0,00mm	0,00mm	20566,95kg
	3				6	0,00mm	0,00mm	14,36kg
	4	3561,00mm	0,00°	0,00°	1	0,00mm	0,00mm	12,91kg
	5	3561,00mm	0,00°	0,00°	1	0,00mm	0,00mm	12,91kg
	6	80,00mm	0,00°	0,00°	1			1,44kg
Cornière à ailes inégales 150 x 90 x 10, ISO 657-2	7	80,00mm	0,00°	0,00°	1			1,44kg
Cornière à ailes inégales 150 x 90 x 10, ISO 657-2	8	80,00mm	0,00°	0,00°	1			1,44kg
Cornière à ailes inégales 150 x 90 x 10, ISO 657-2	9	80,00mm	0,00°	0,00°	1			1,44kg
Cornière à ailes inégales 150 x 90 x 10, ISO 657-2	10	160,00mm	0,00°	0,00°	4			2,88kg
patte vitrage 60	11				24			
plat-50x5	12	1392,00mm	0,00°	0,00°	1	0,00mm	0,00mm	2,73kg
plat-50x5	13	1392,00mm	0,00°	0,00°	1	0,00mm	0,00mm	2,73kg
plat-50x10	14	1392,00mm	0,00°	0,00°	1	0,00mm	0,00mm	5,46kg
plat-50x10	15	1392,00mm	0,00°	0,00°	1	0,00mm	0,00mm	5,46kg
plat-50x10	16	1392,00mm	0,00°	0,00°	4	0,00mm	0,00mm	5,46kg
profil alu+joint	17	1155,33mm	0,00°	0,00°	6			
profil alu+joint	18	1155,33mm	0,00°	0,00°	6			
Profilé carré creux 40 x 2, ISO 4019	19	1175,33mm	0,00°	0,00°	12			
tube 80x20	20	3561,00mm	0,00°	0,00°	1	0,00mm	0,00mm	2,71kg
tube 80x20	21	3561,00mm	0,00°	0,00°	1	0,00mm	0,00mm	8,13kg
vitrage	22				6	1155,33mm	571,00mm	8,13kg
								14,51kg

Rep = 9 .