


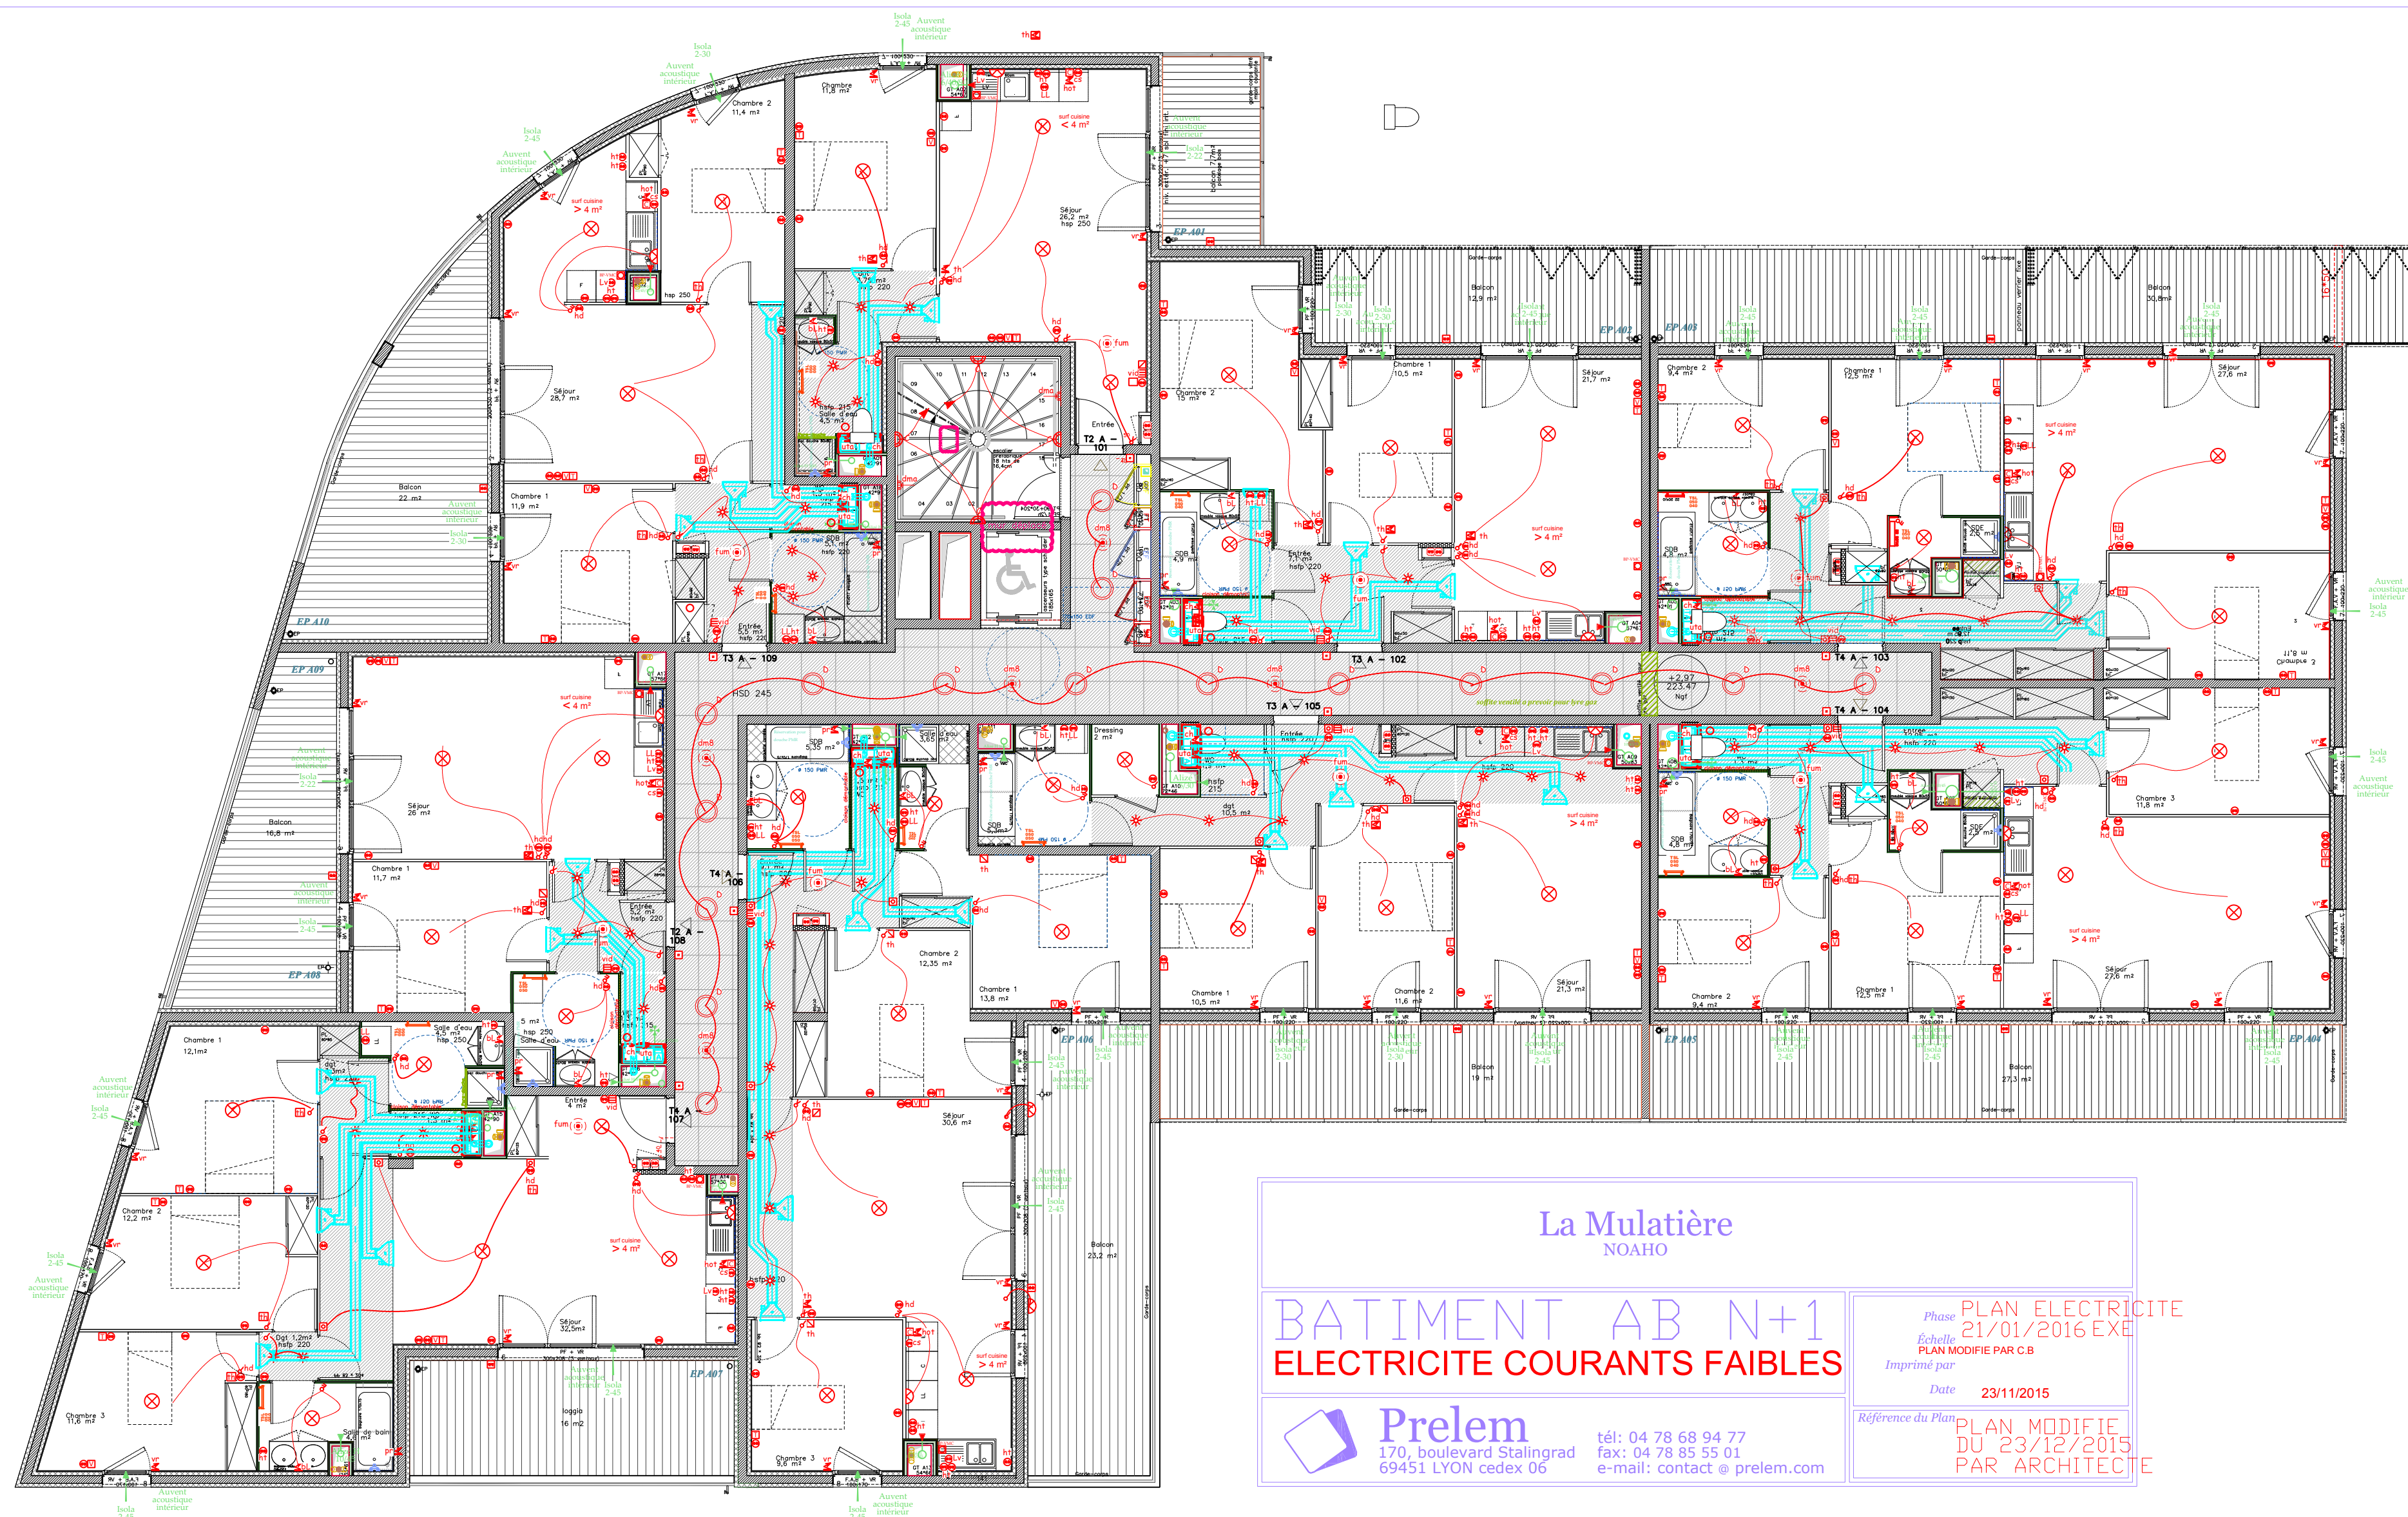

La Mulatière
NOAHO

BATIMENT AB N+1

ELECTRICITE COURANTS FAIBLES



Prelam

170, boulevard Stalingrad
69451 LYON cedex 06

tél: 04 78 68 94 77
fax: 04 78 85 55 01
e-mail: contact @ prelam.com

Phase **PLAN ELECTRICITE**
21/01/2016 EXE

Imprimé par
PLAN MODIFIE PAR C.B

Date 23/11/2015

Référence du Plan
DU 23/12/2015
PAR ARCHITECTE