


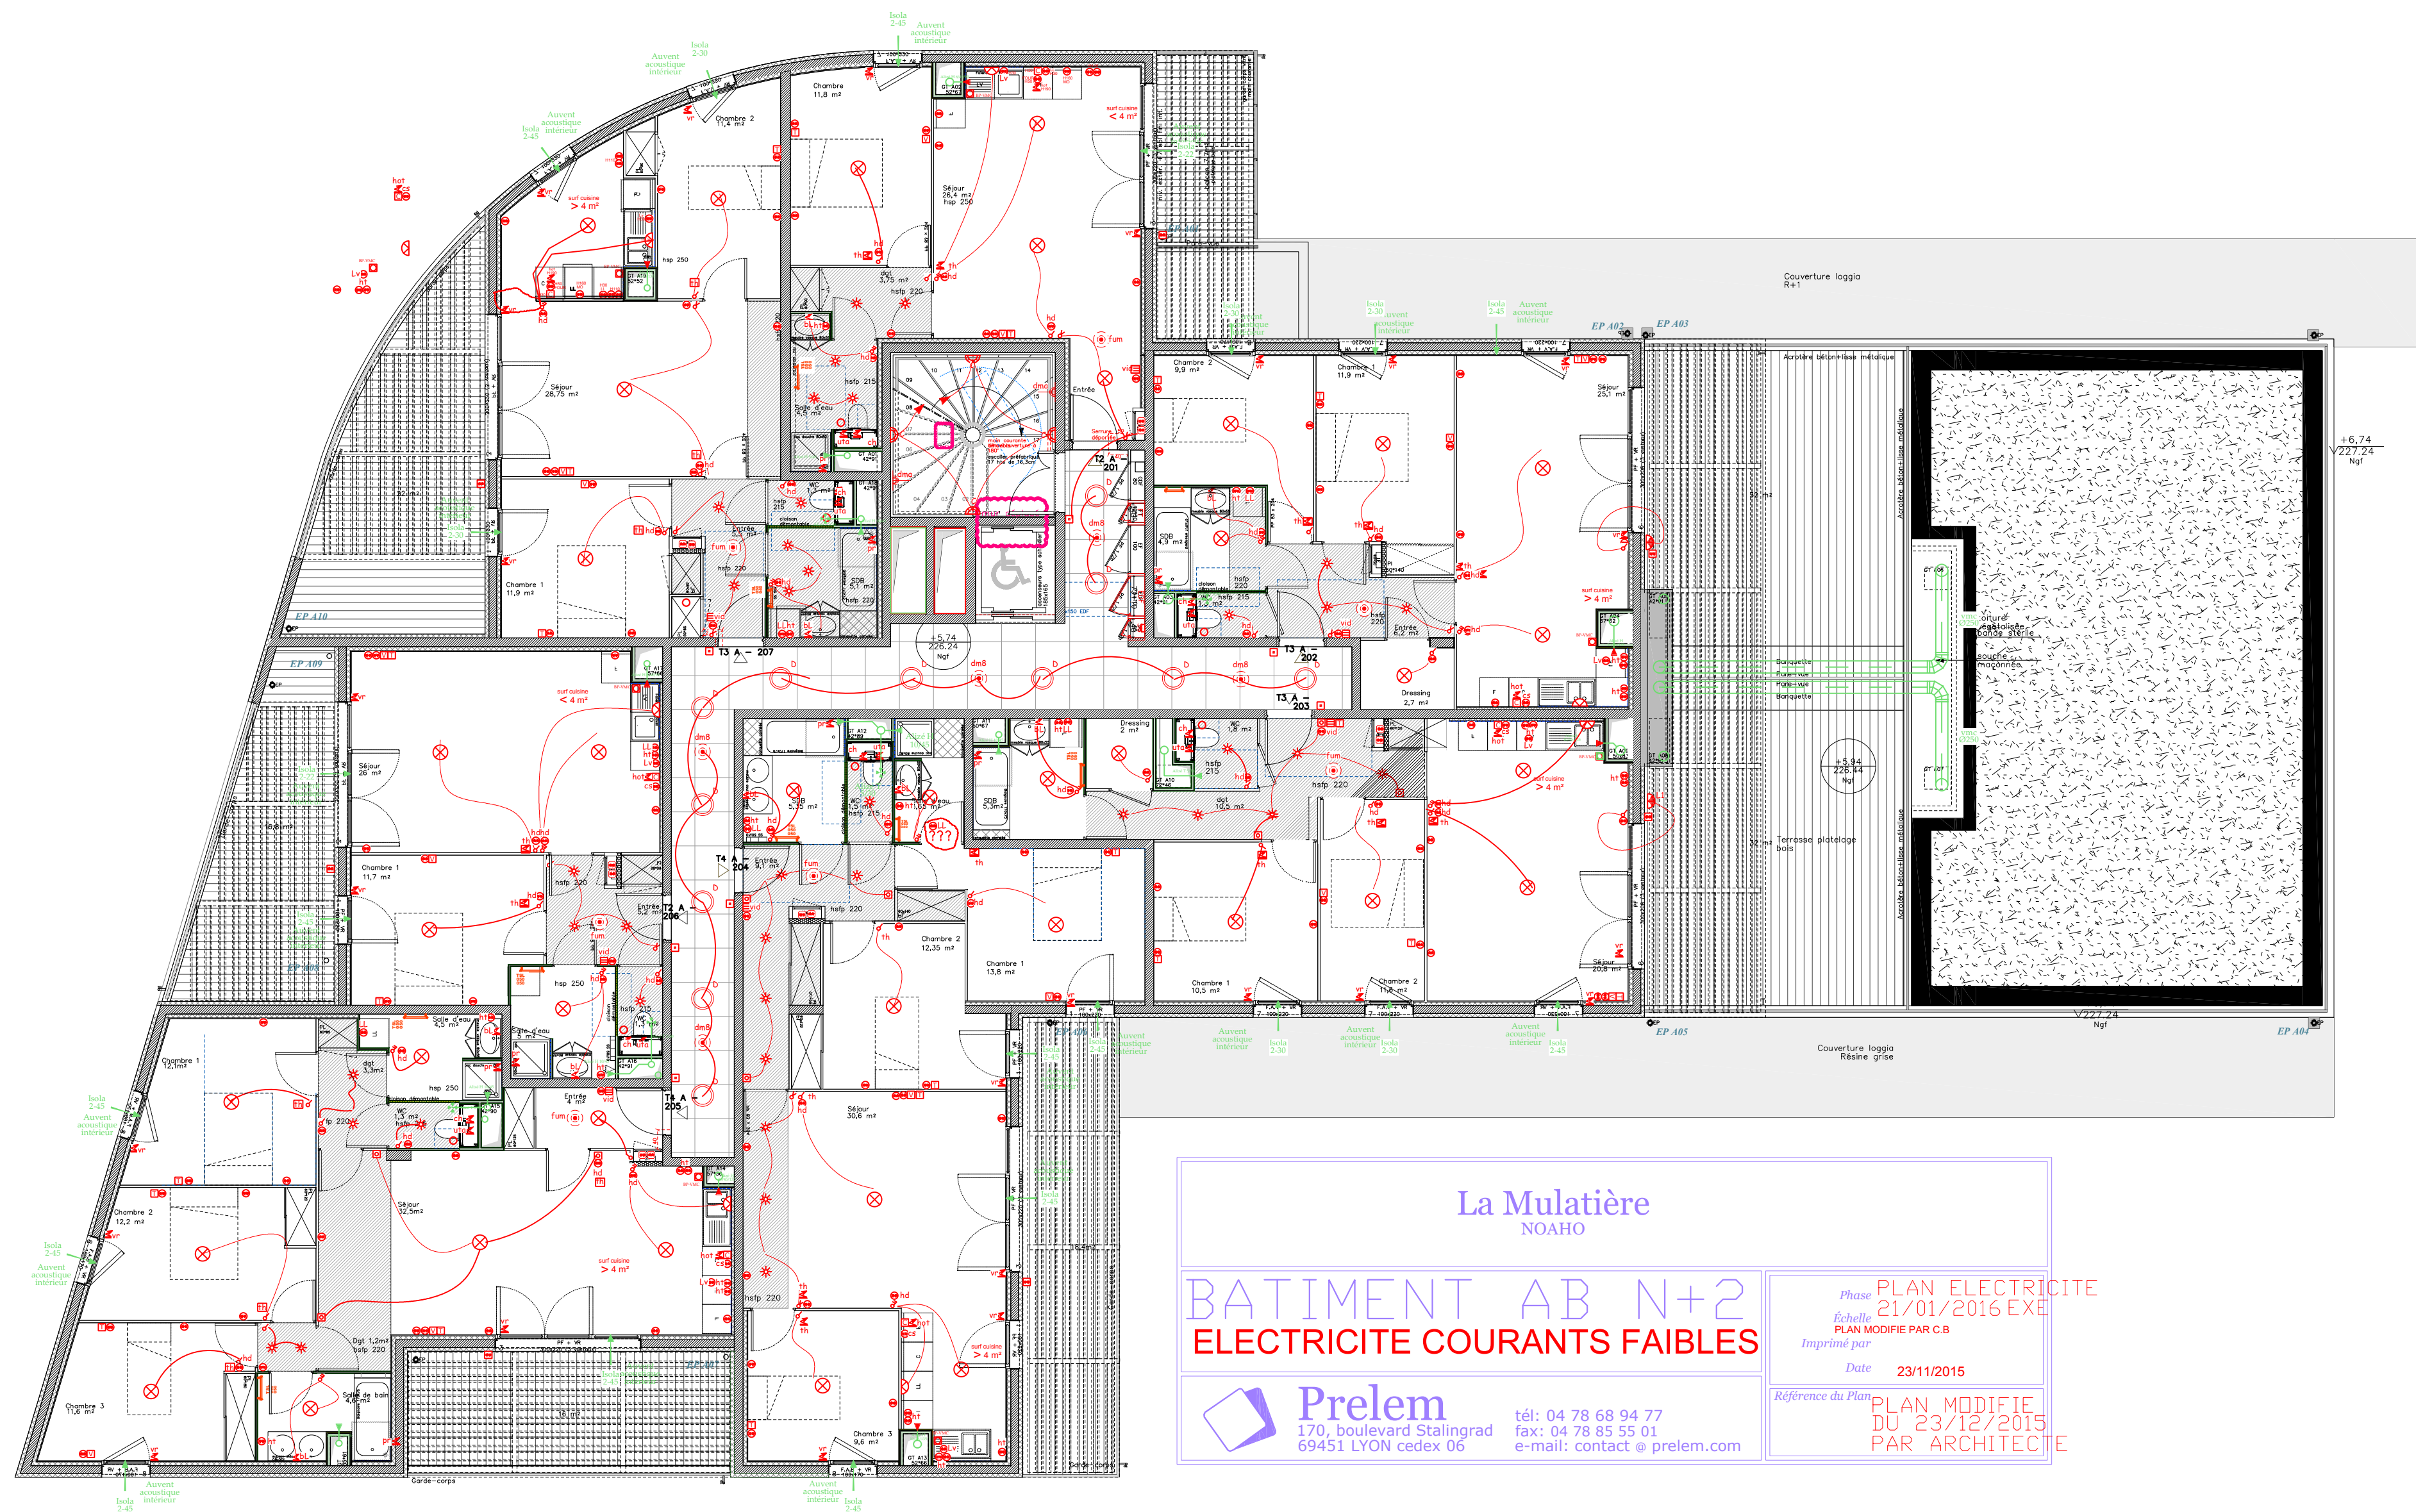

La Mulatière
NOAHO

BATIMENT AB N+2

ELECTRICITE COURANTS FAIBLES



Prelem
170, boulevard Stalingrad
69451 LYON cedex 06

tél: 04 78 68 94 77
fax: 04 78 85 55 01
e-mail: contact @ prelem.com

Phase **PLAN ELECTRICITE**
Échelle **21/01/2016 EXE**
Imprimé par **PLAN MODIFIE PAR C.B**
Date **23/11/2015**
Référence du Plan **PLAN MODIFIE DU 23/12/2015 PAR ARCHITECTE**