



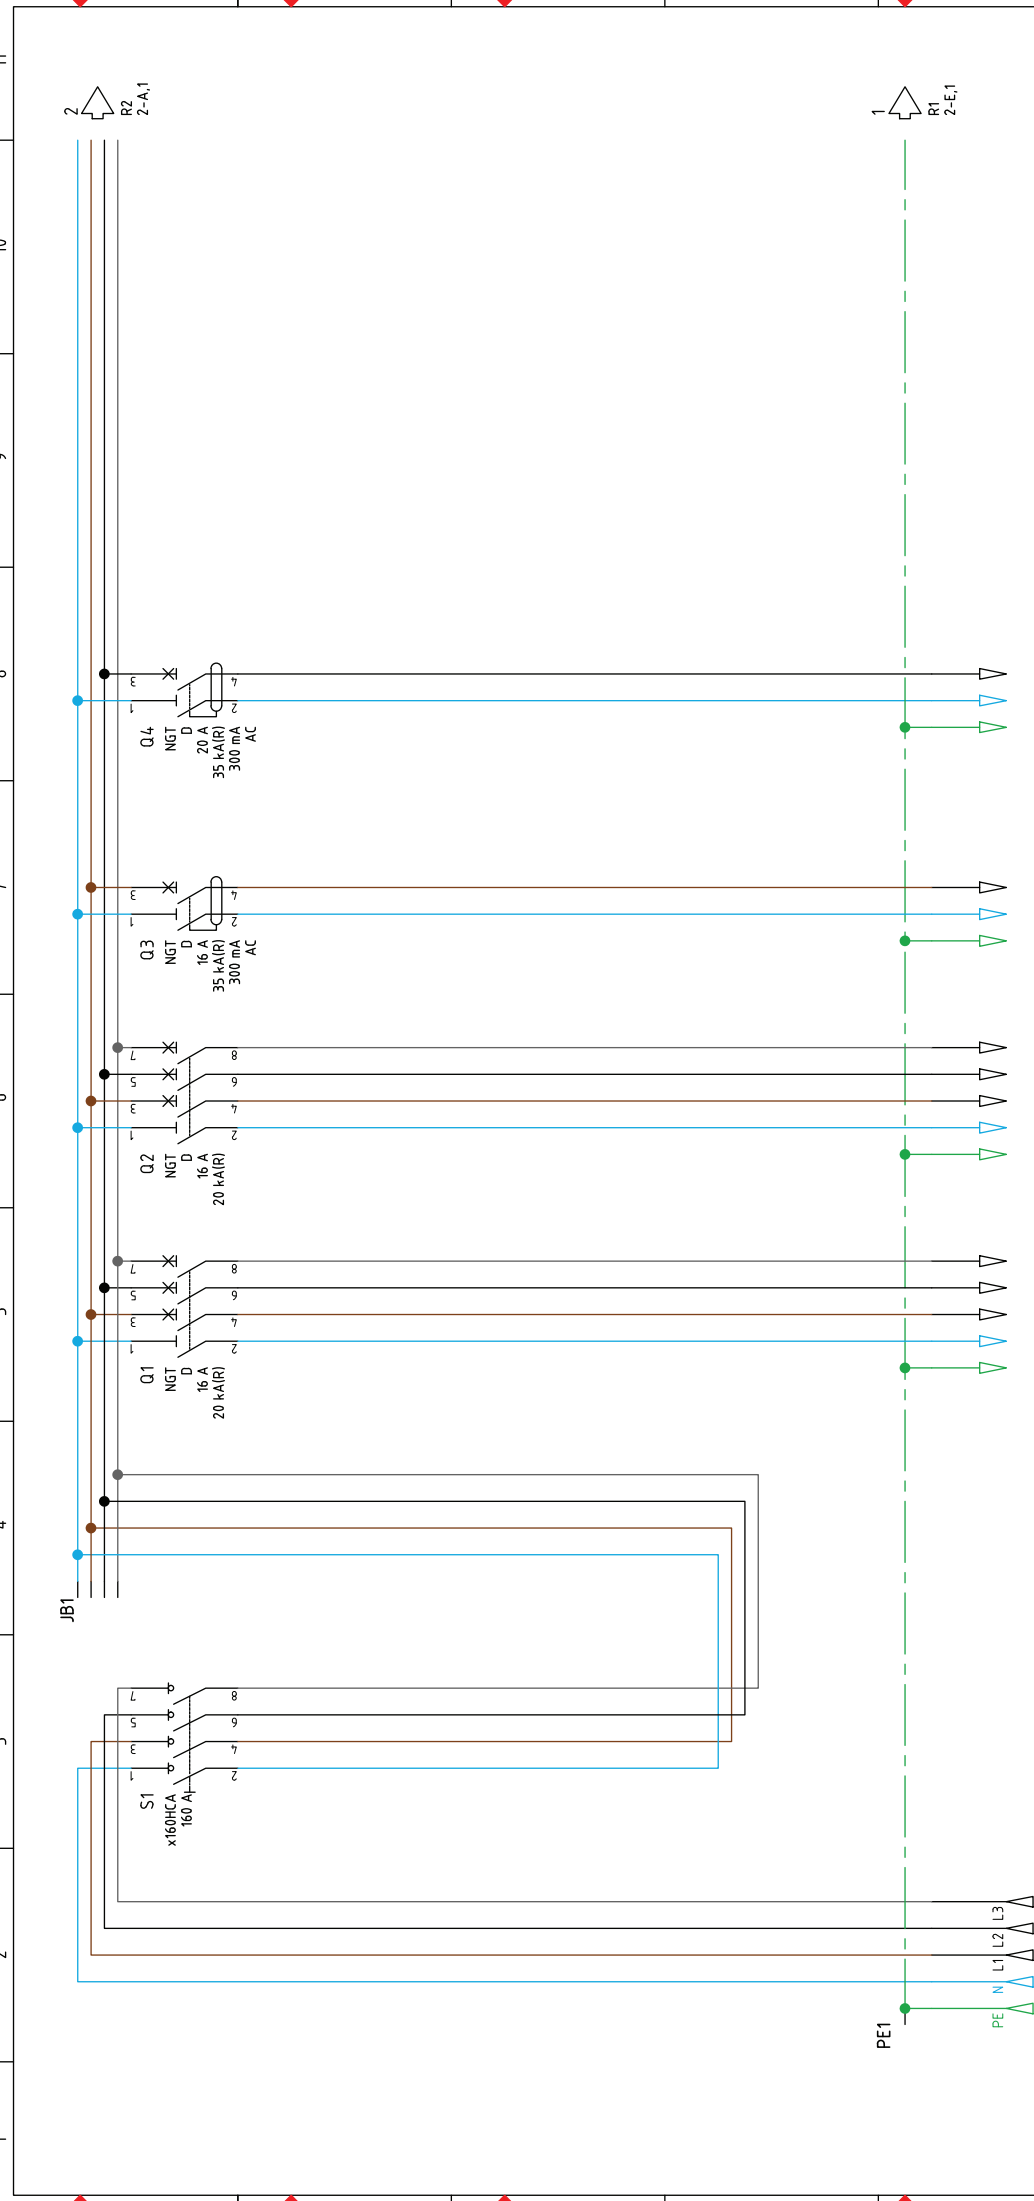

Application des départs Localisation	Alim. tableau TGBT										SS-1 Désenfumage	SS-2 Désenfumage	Parking Pompe relevage	EP Pompe relevage		indice : b	
	3								Nom du projet : 310073460								
	2								N° d'affaire :								
	1								Schéma de puissance								
	Modification																
	Echelle : 1																
								</									

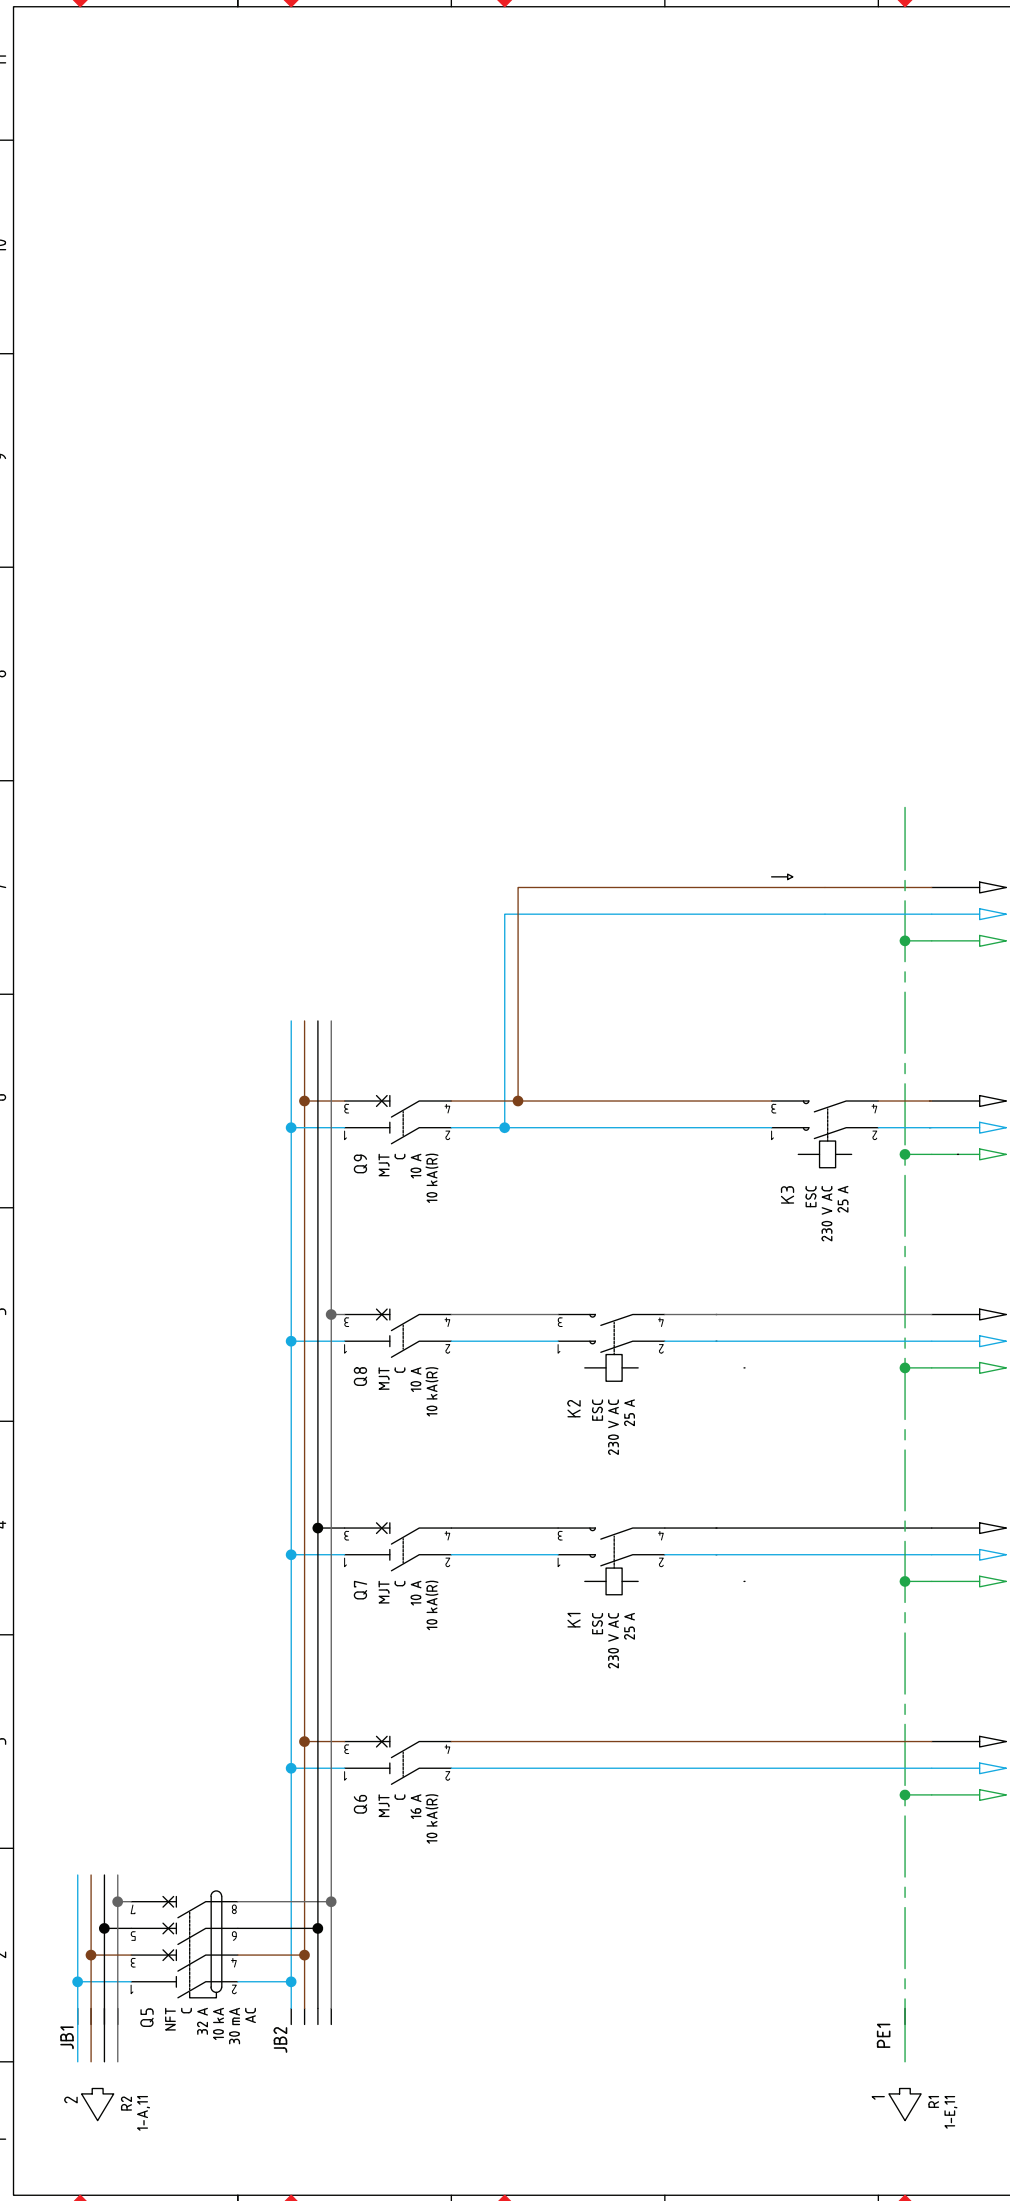

Repère câble	W5		W6		W7		W8		W9	
Type de câble										
Section (mm²)										
Repère départ	E5		E6		E7		E8		E9	
Pictogramme										
Application Localisation des départs	Prises de courant		Eclairage		Eclairage		Eclairage		Eclairage	
	Sous sol		SS-1		SS-2		Rampe d'accès SSol		Local fibre	
	local fibre		SS-1		SS-2		Eclairage		Eclairage	
			N° plan		Date		Nom du projet : 310073460			
			Date		18/11/2016		N° d'affaire :			
3									indire : b	
2									TD SG	
1									Folio : 2 / 2	
Modification	Date modification		Modifié par		Validé par		Schéma de puissance			
Echelle : 1	lk1 :		lk1 :		Régime de neutre : TT					