



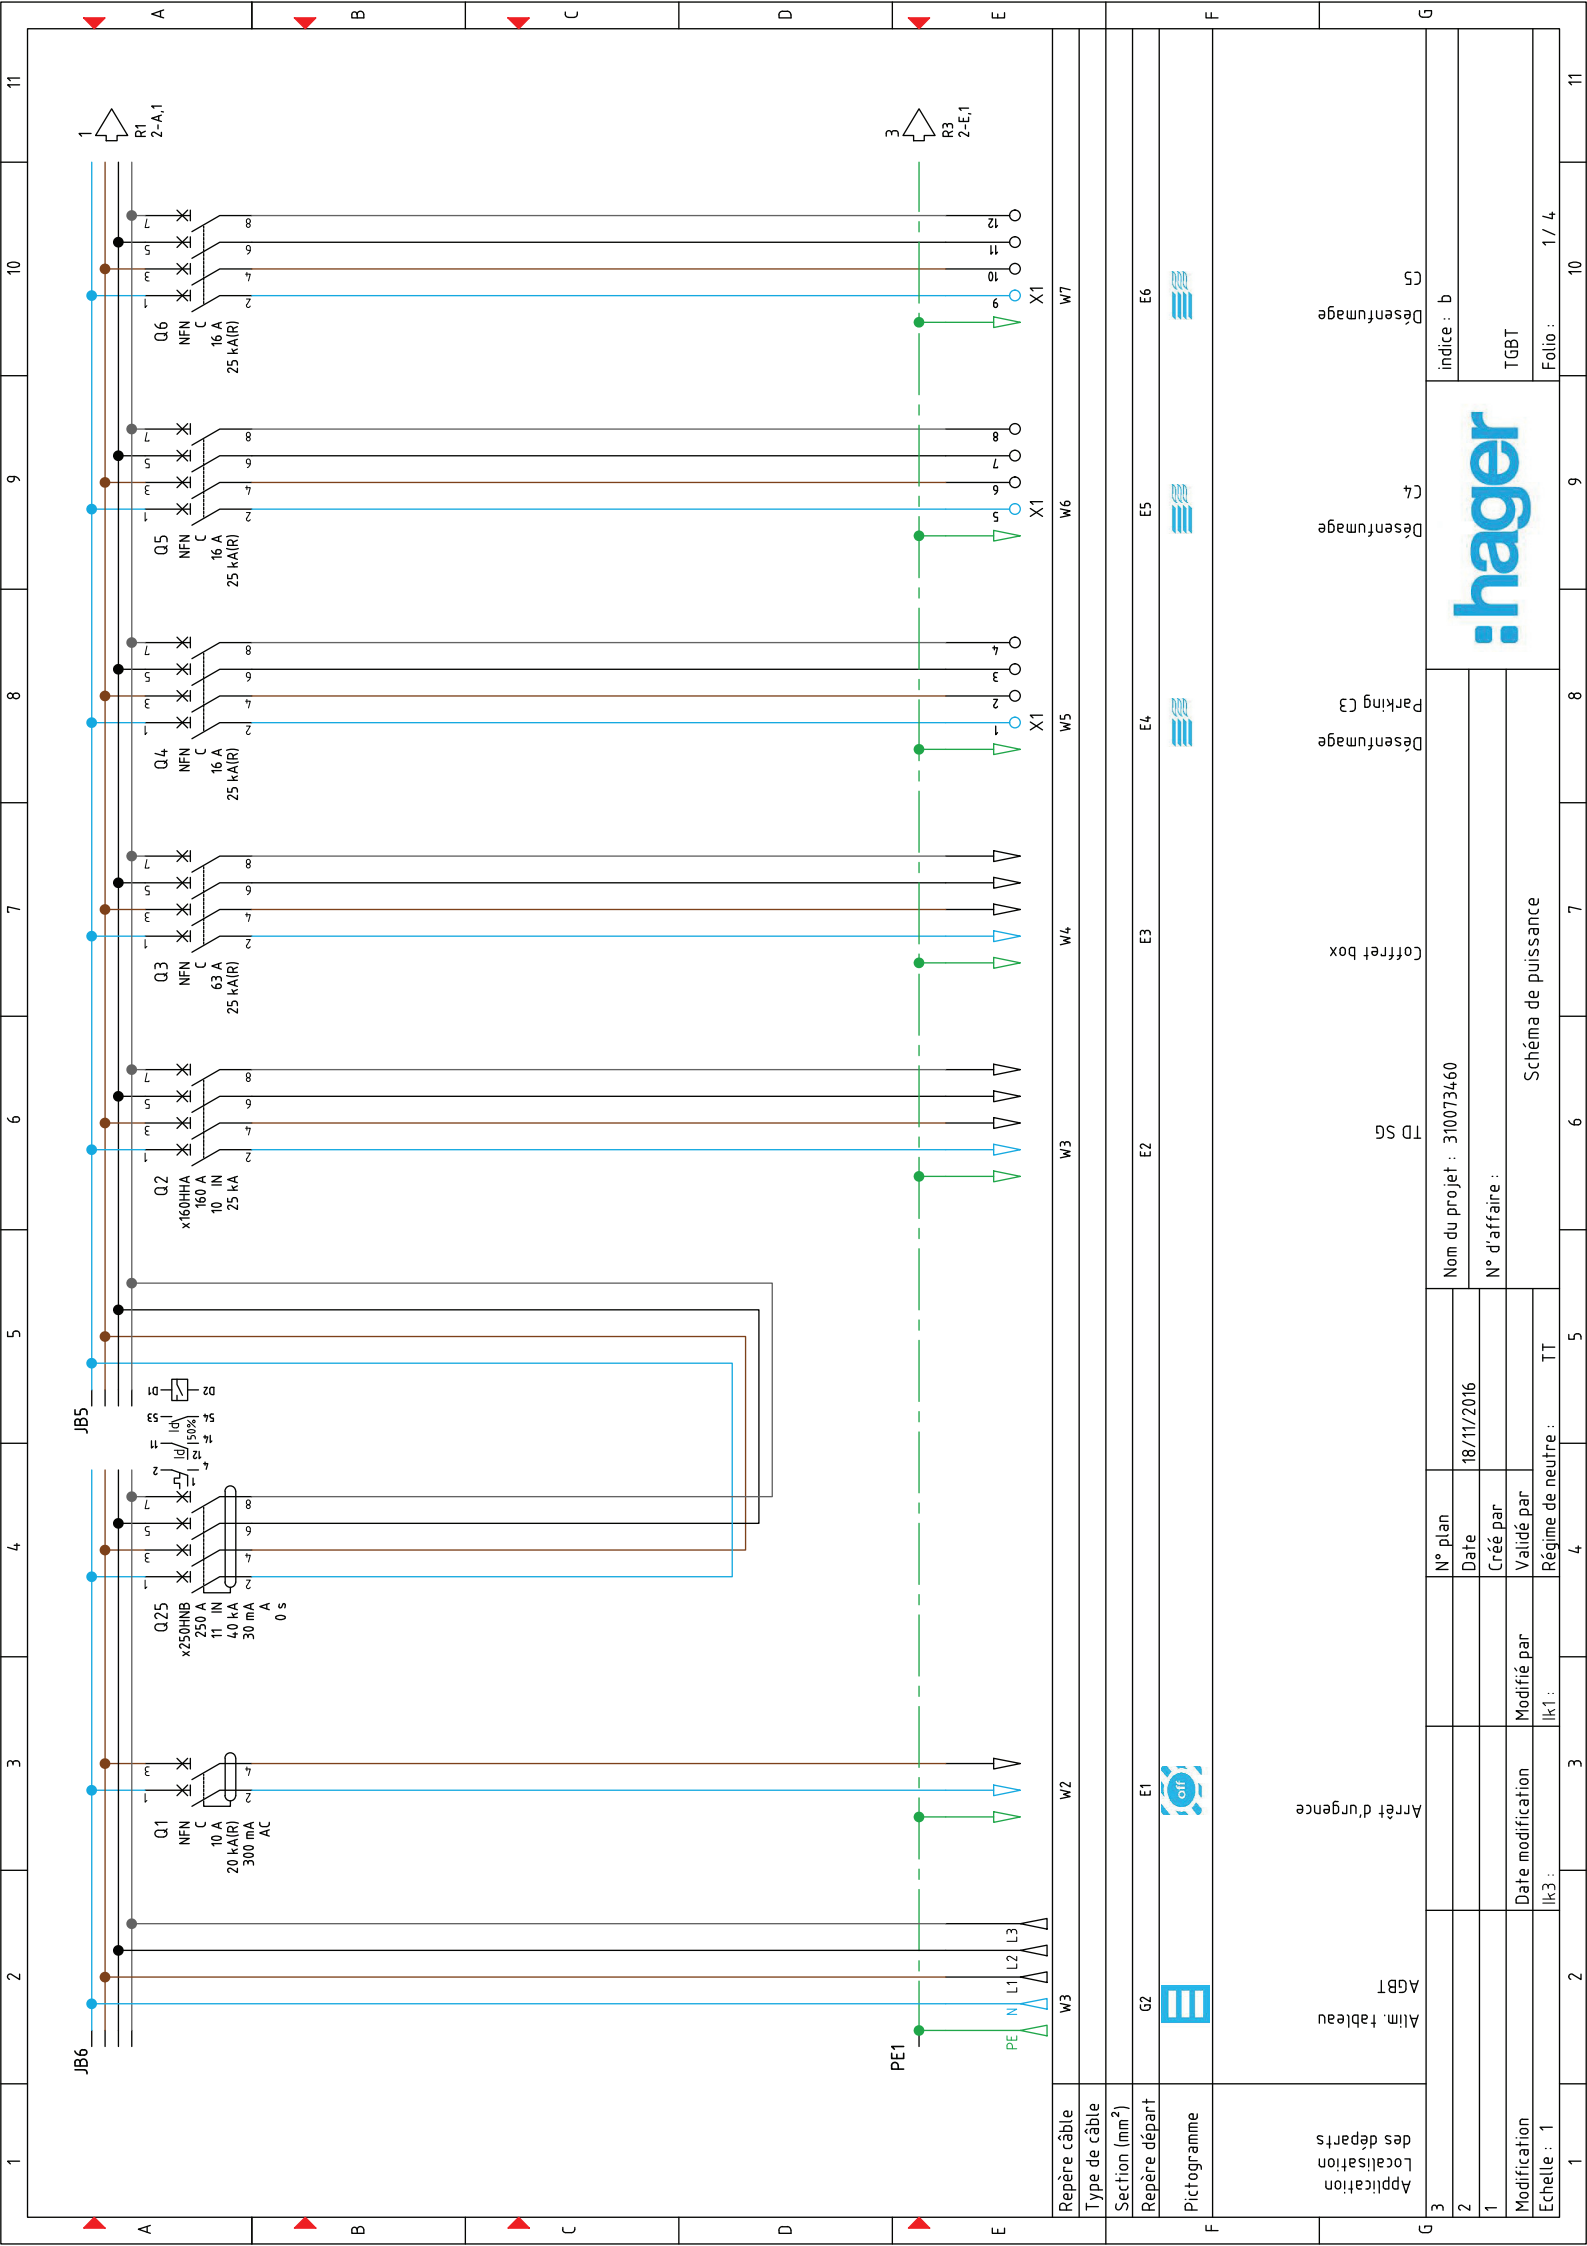

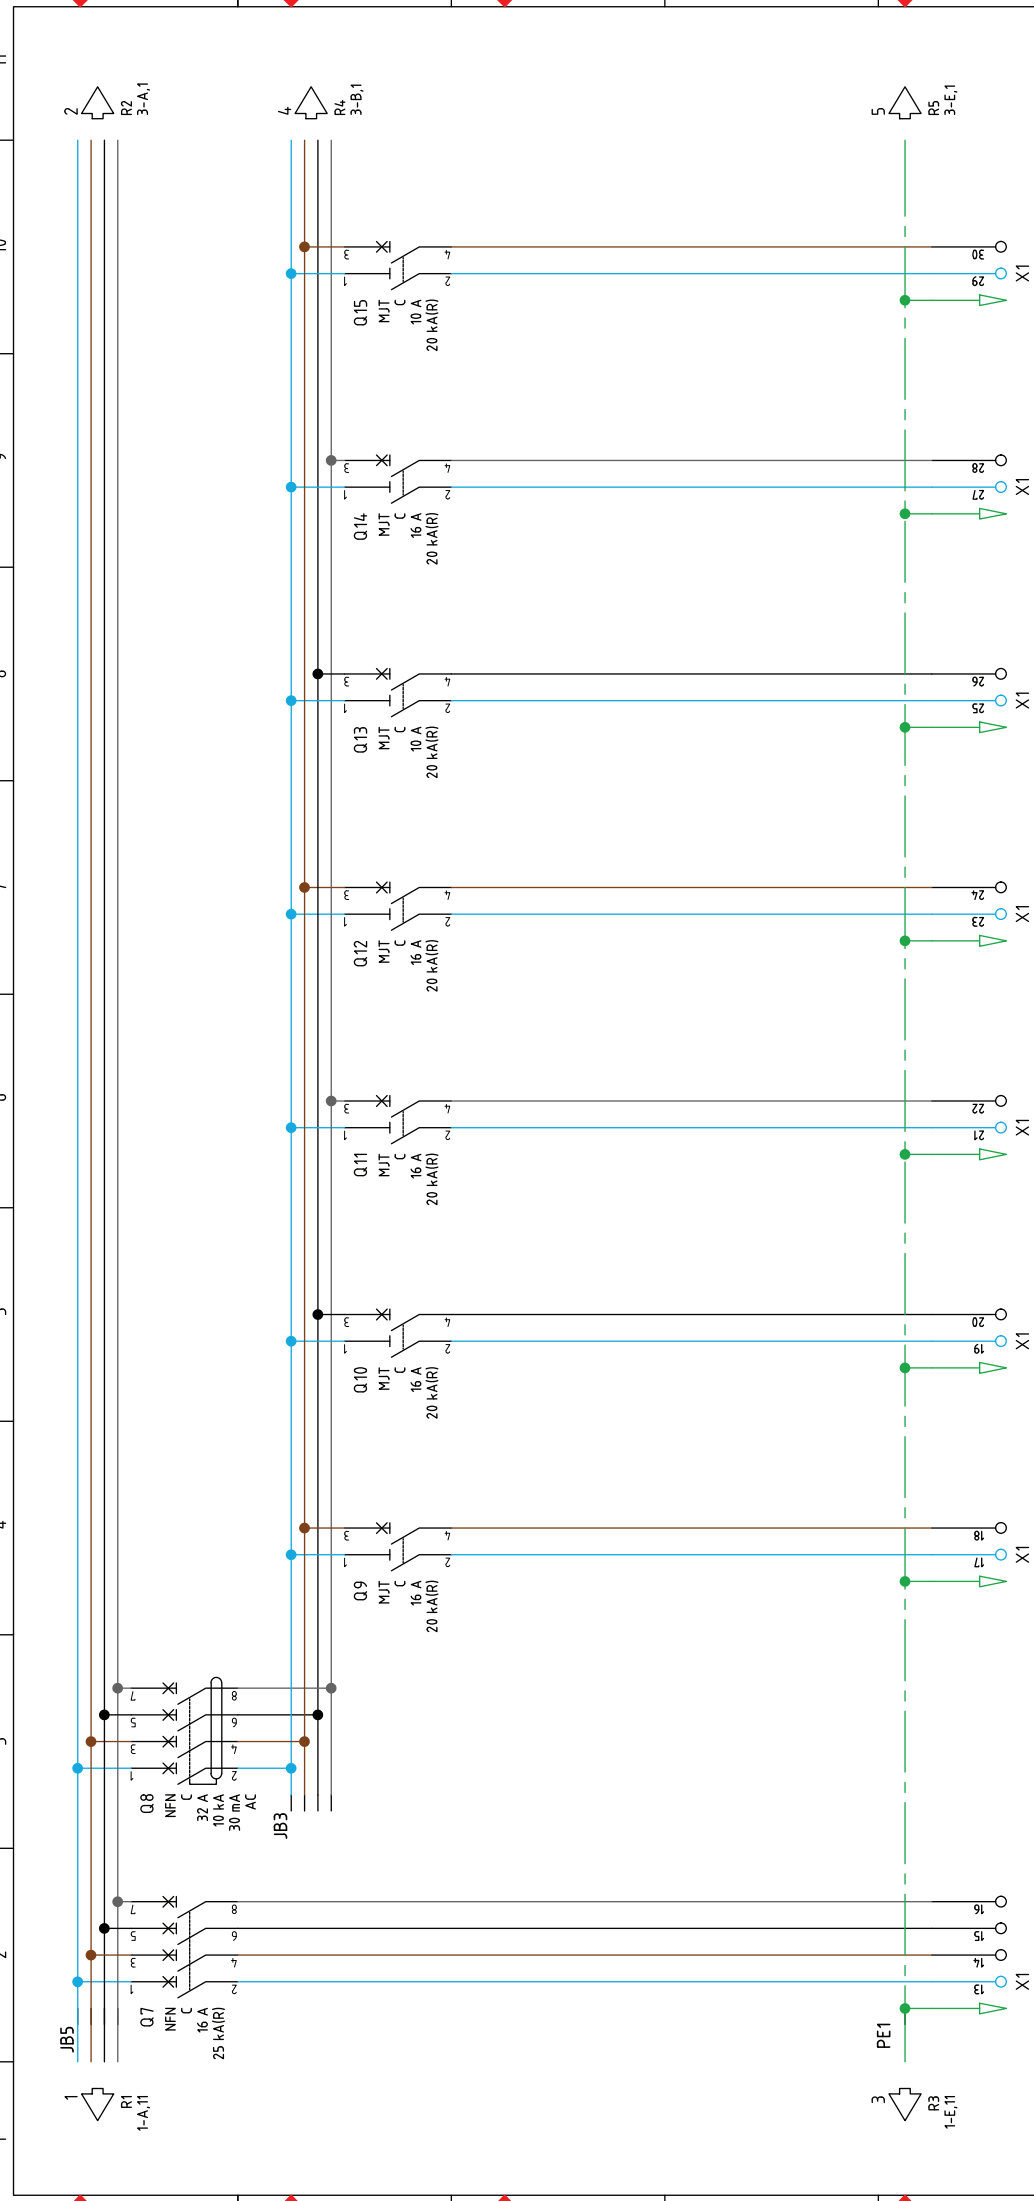

Repère câble	W8										
Type de câble	W16										
Section (mm ²)	W15										
Repère départ	W14										
Pictogramme	W13										

Application des départs	Désenfumage										
	Prises de courant										
	Local technique										
	Accès sous sol										
	Gardiennage										
Localisation	Centrale incendie										
	Prises de courant										
	Local gardien										
	Interphone										
	Indice : b										
3	Nom du projet : 310073460										
2	N° d'affaire :										
1	Schéma de puissance										
Modification	Date modification										
Echelle : 1	Ik1 : Ik2 : Ik3 :										
1	2	3	4	5	6	7	8	9	10	11	

