


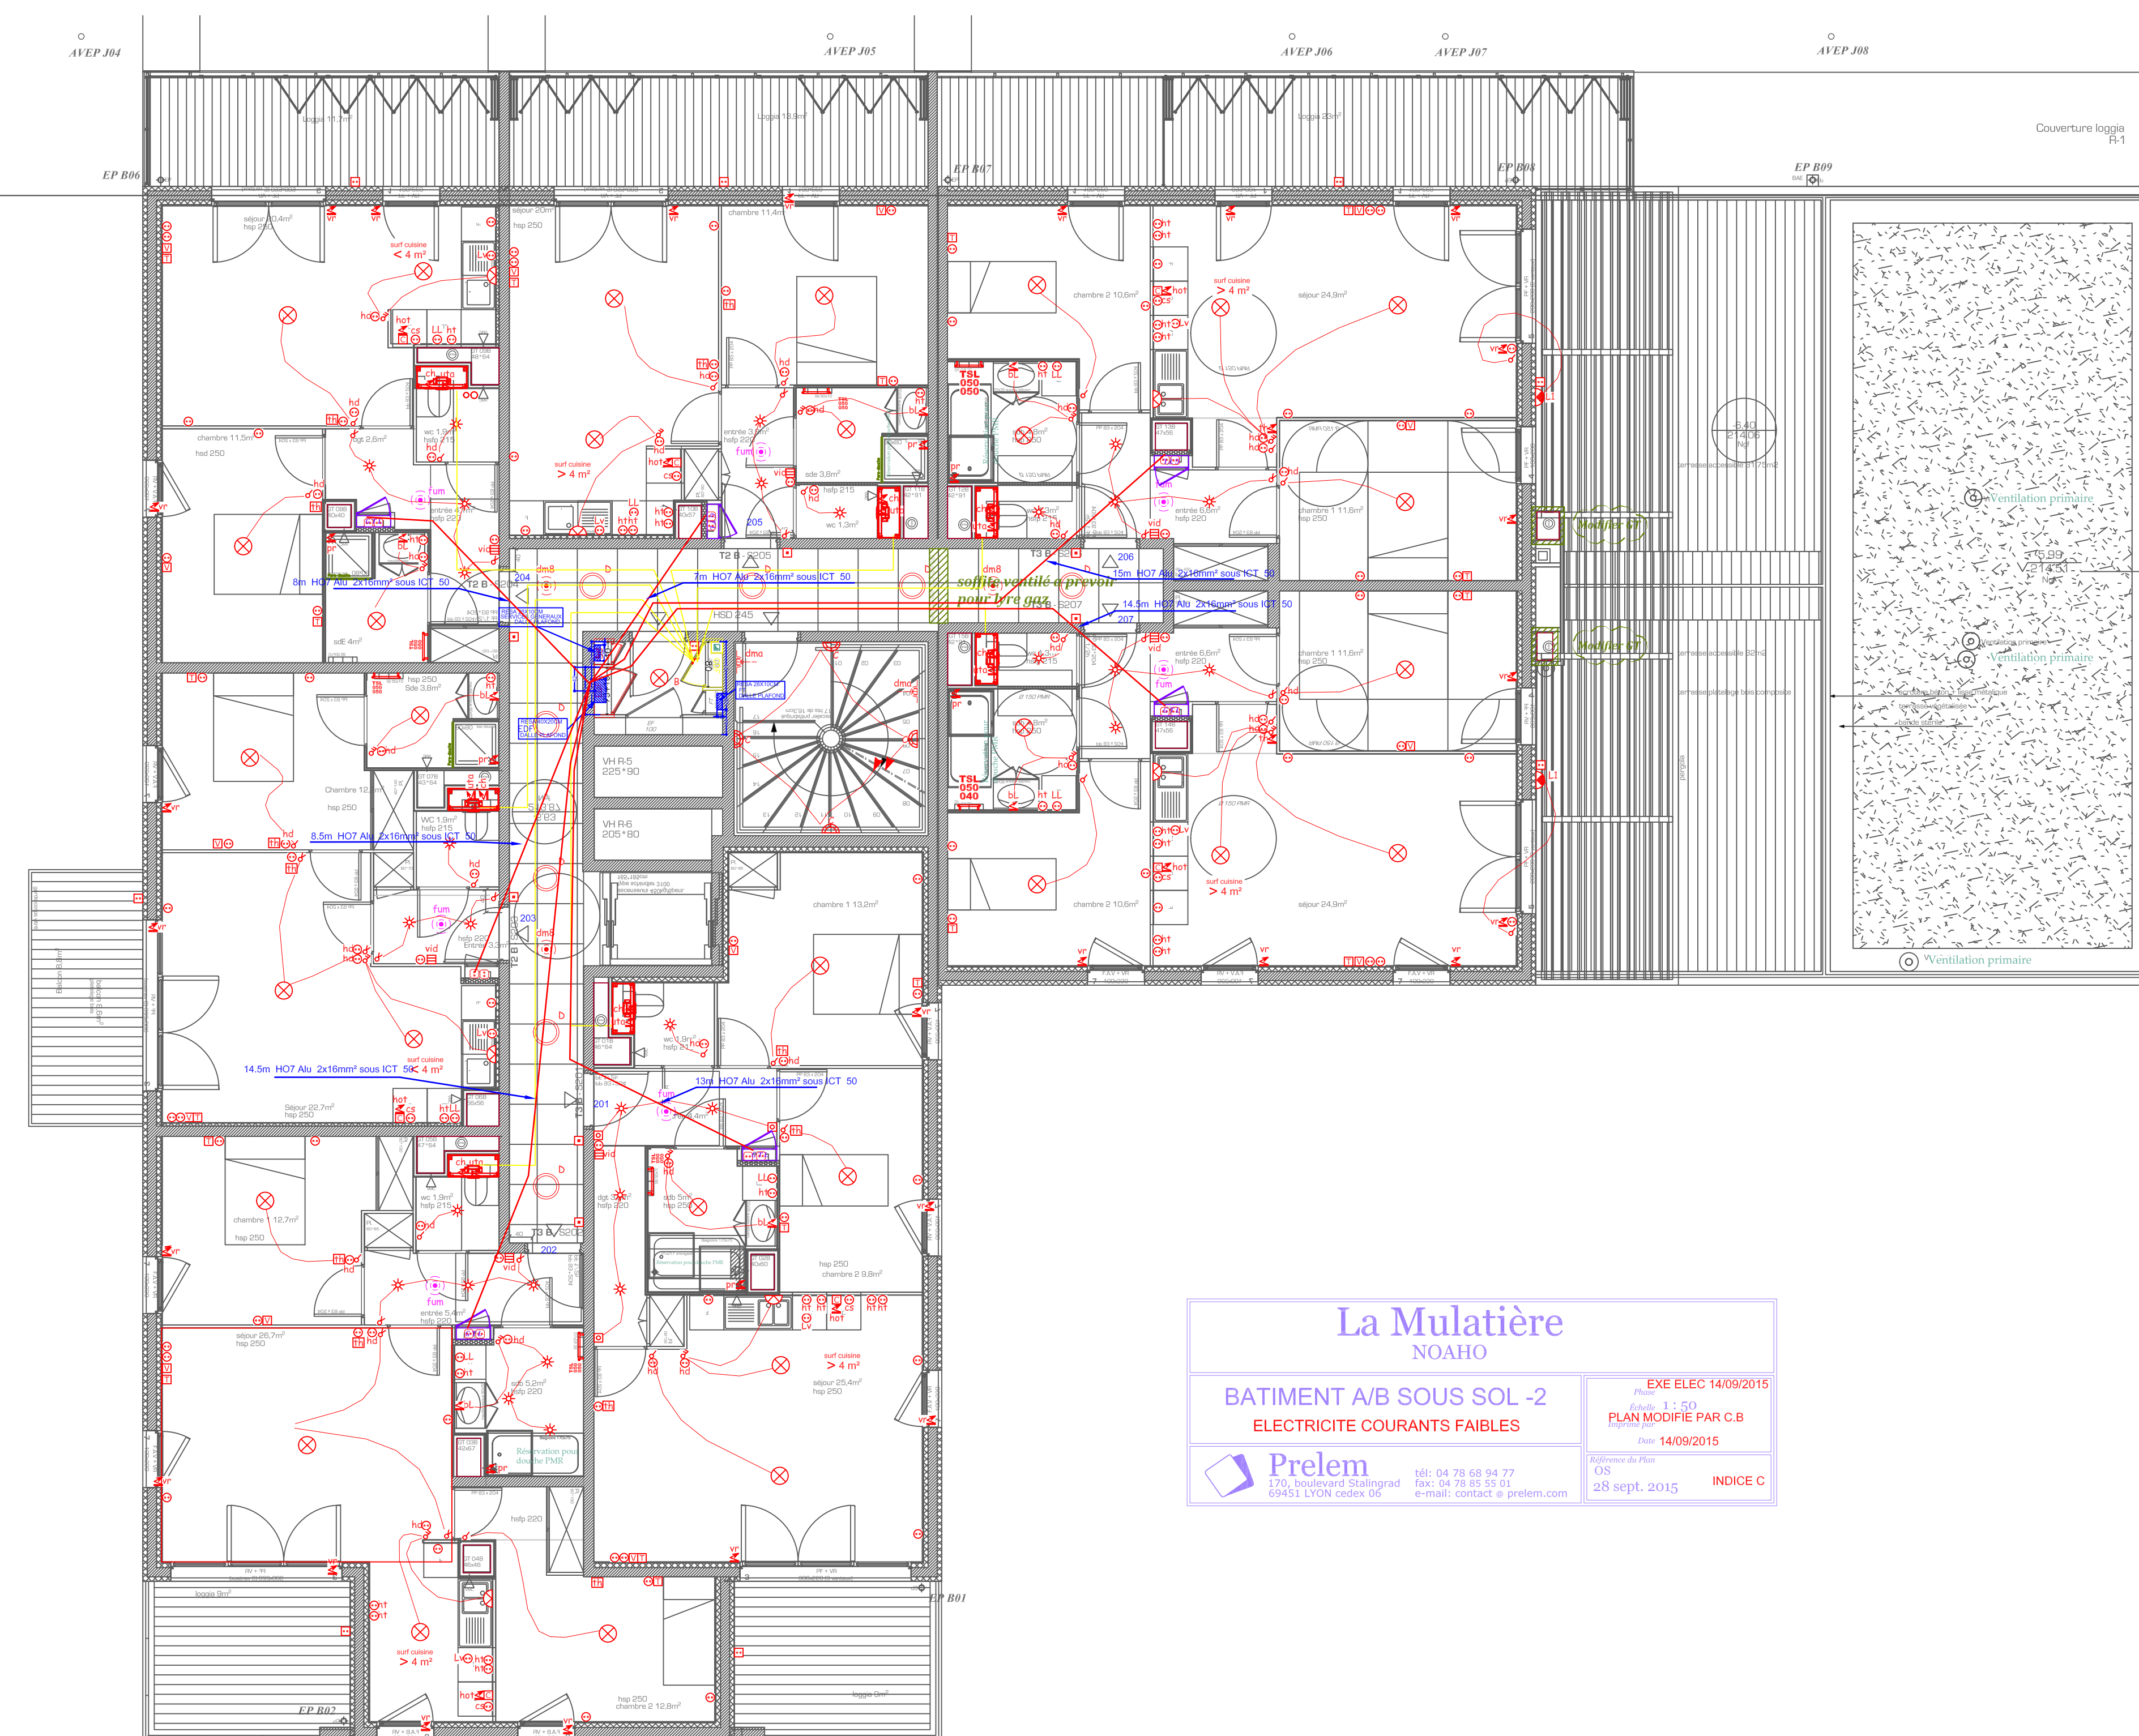

La Mulatière NOAHO		EXE ELABORÉ 14/09/2015	
BATIMENT A/B SOUS SOL -2 ELECTRICITE COURANTS FAIBLES		<i>Plan</i> : 1 : 50 PLAN MODIFIÉ PAR C.B <i>date</i> : 14/09/2015	
 Prellem 170, boulevard Stalagard 69453 LYON cedex 04		28 sept. 2015 INDICE C	
tél: 04 78 68 94 94 fax: 04 78 85 50 04 e-mail: contact@prellem.com			