


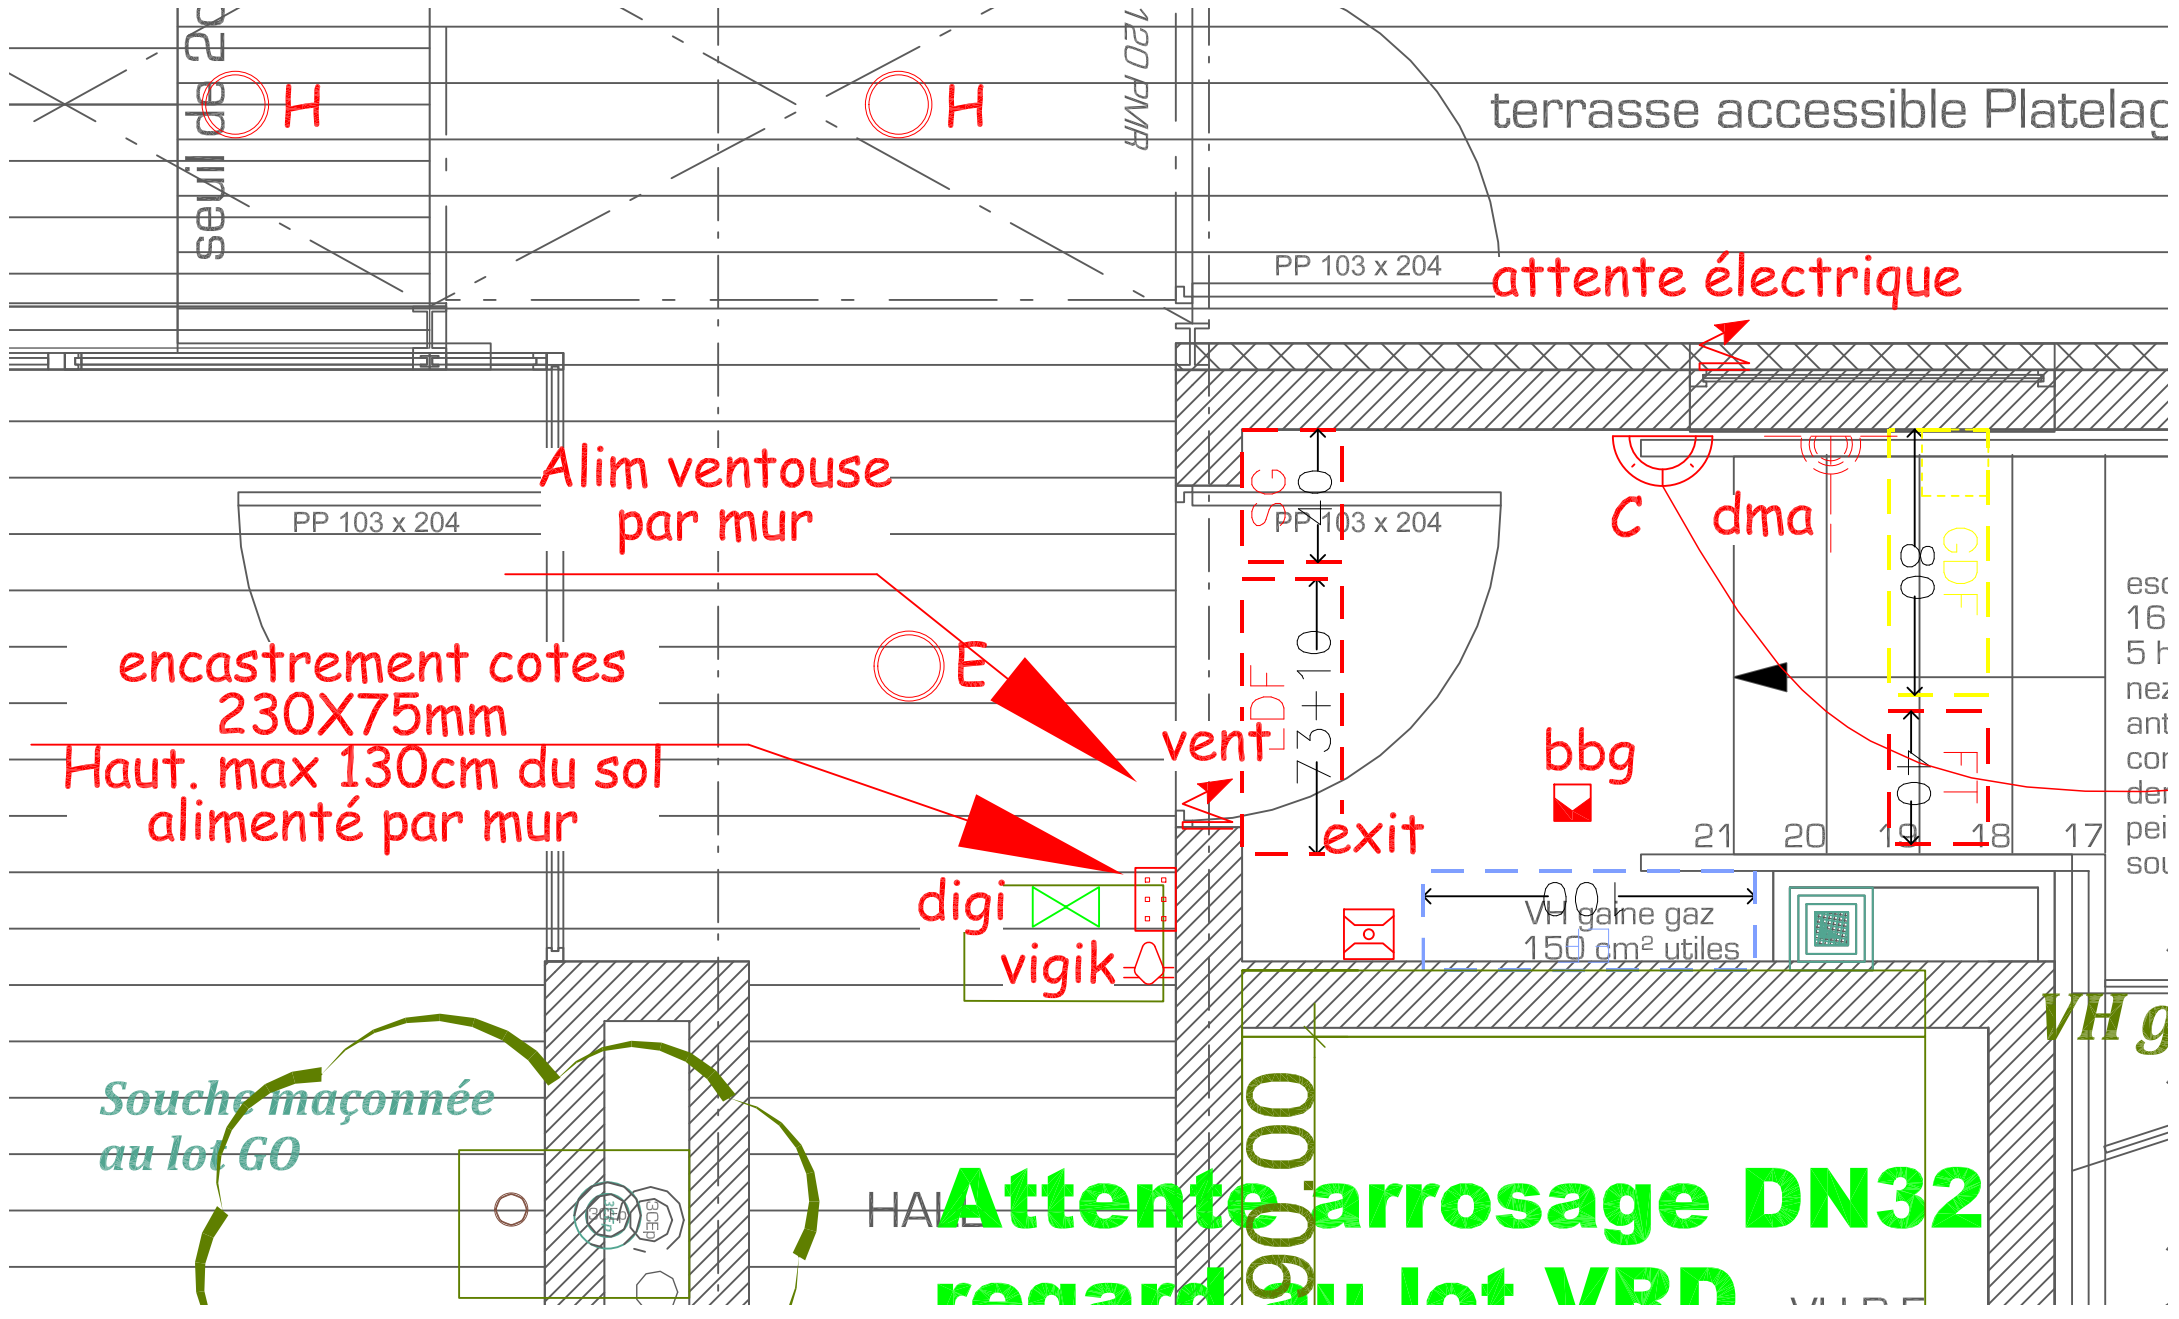

seuil de 2c

H

H

120 PMH

terrasse accessible Platelac

PP 103 x 204

attente électrique

PP 103 x 204

Alim ventouse
par mur

encastrement cotes
230X75mm

Haut. max 130cm du sol
alimenté par mur

E

vent

exit

digi

vigik

C

dma

GDF

bbg

21

20

19

18

17

VH gaine gaz
150 cm² utiles

Souche maçonnée
au lot G0

Attente arrosage DN32
regard au lot VRN

esc
16
5 h
nez
ant
cor
der
pei
sol

VH g