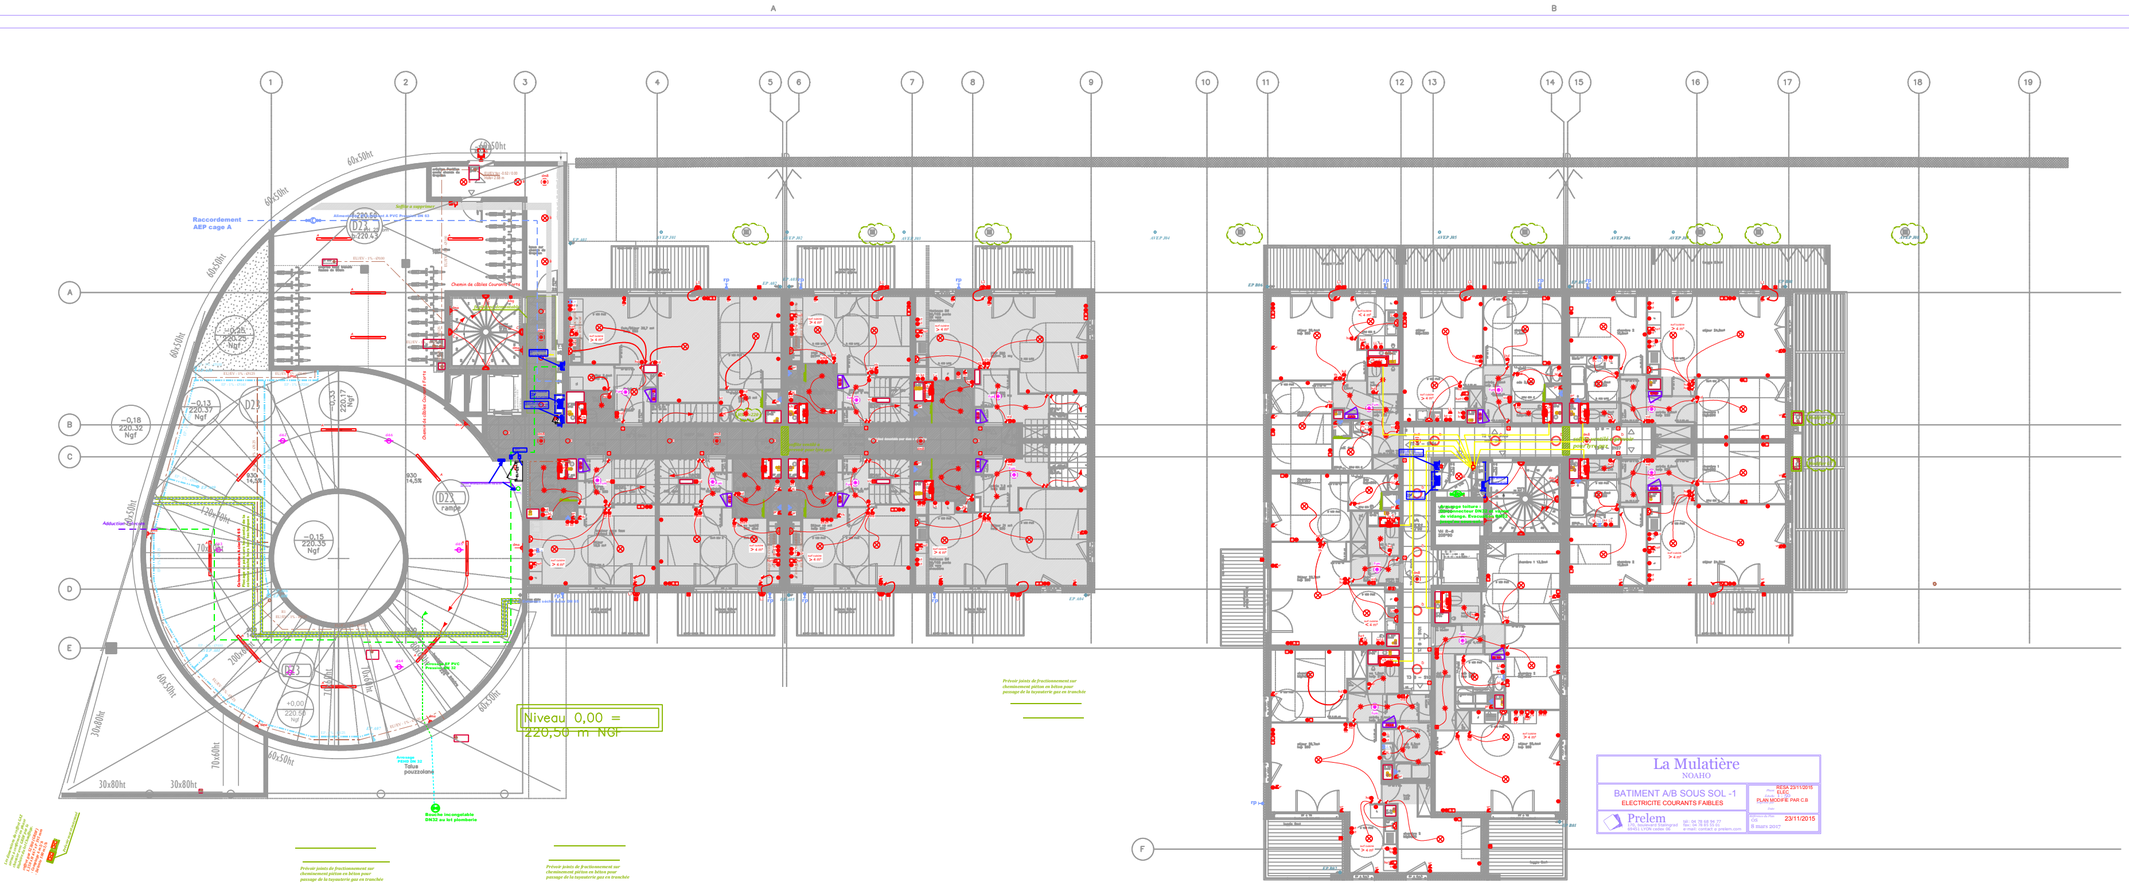

Raccordement AEP cage A
Niveau 0,00 = 220,50 m NGI
La Mulatière
NOAHO
BATIMENT A/B SOUS SOL -1
ELECTRICITE COURANTS FAIBLES
Prelem
23/11/2015