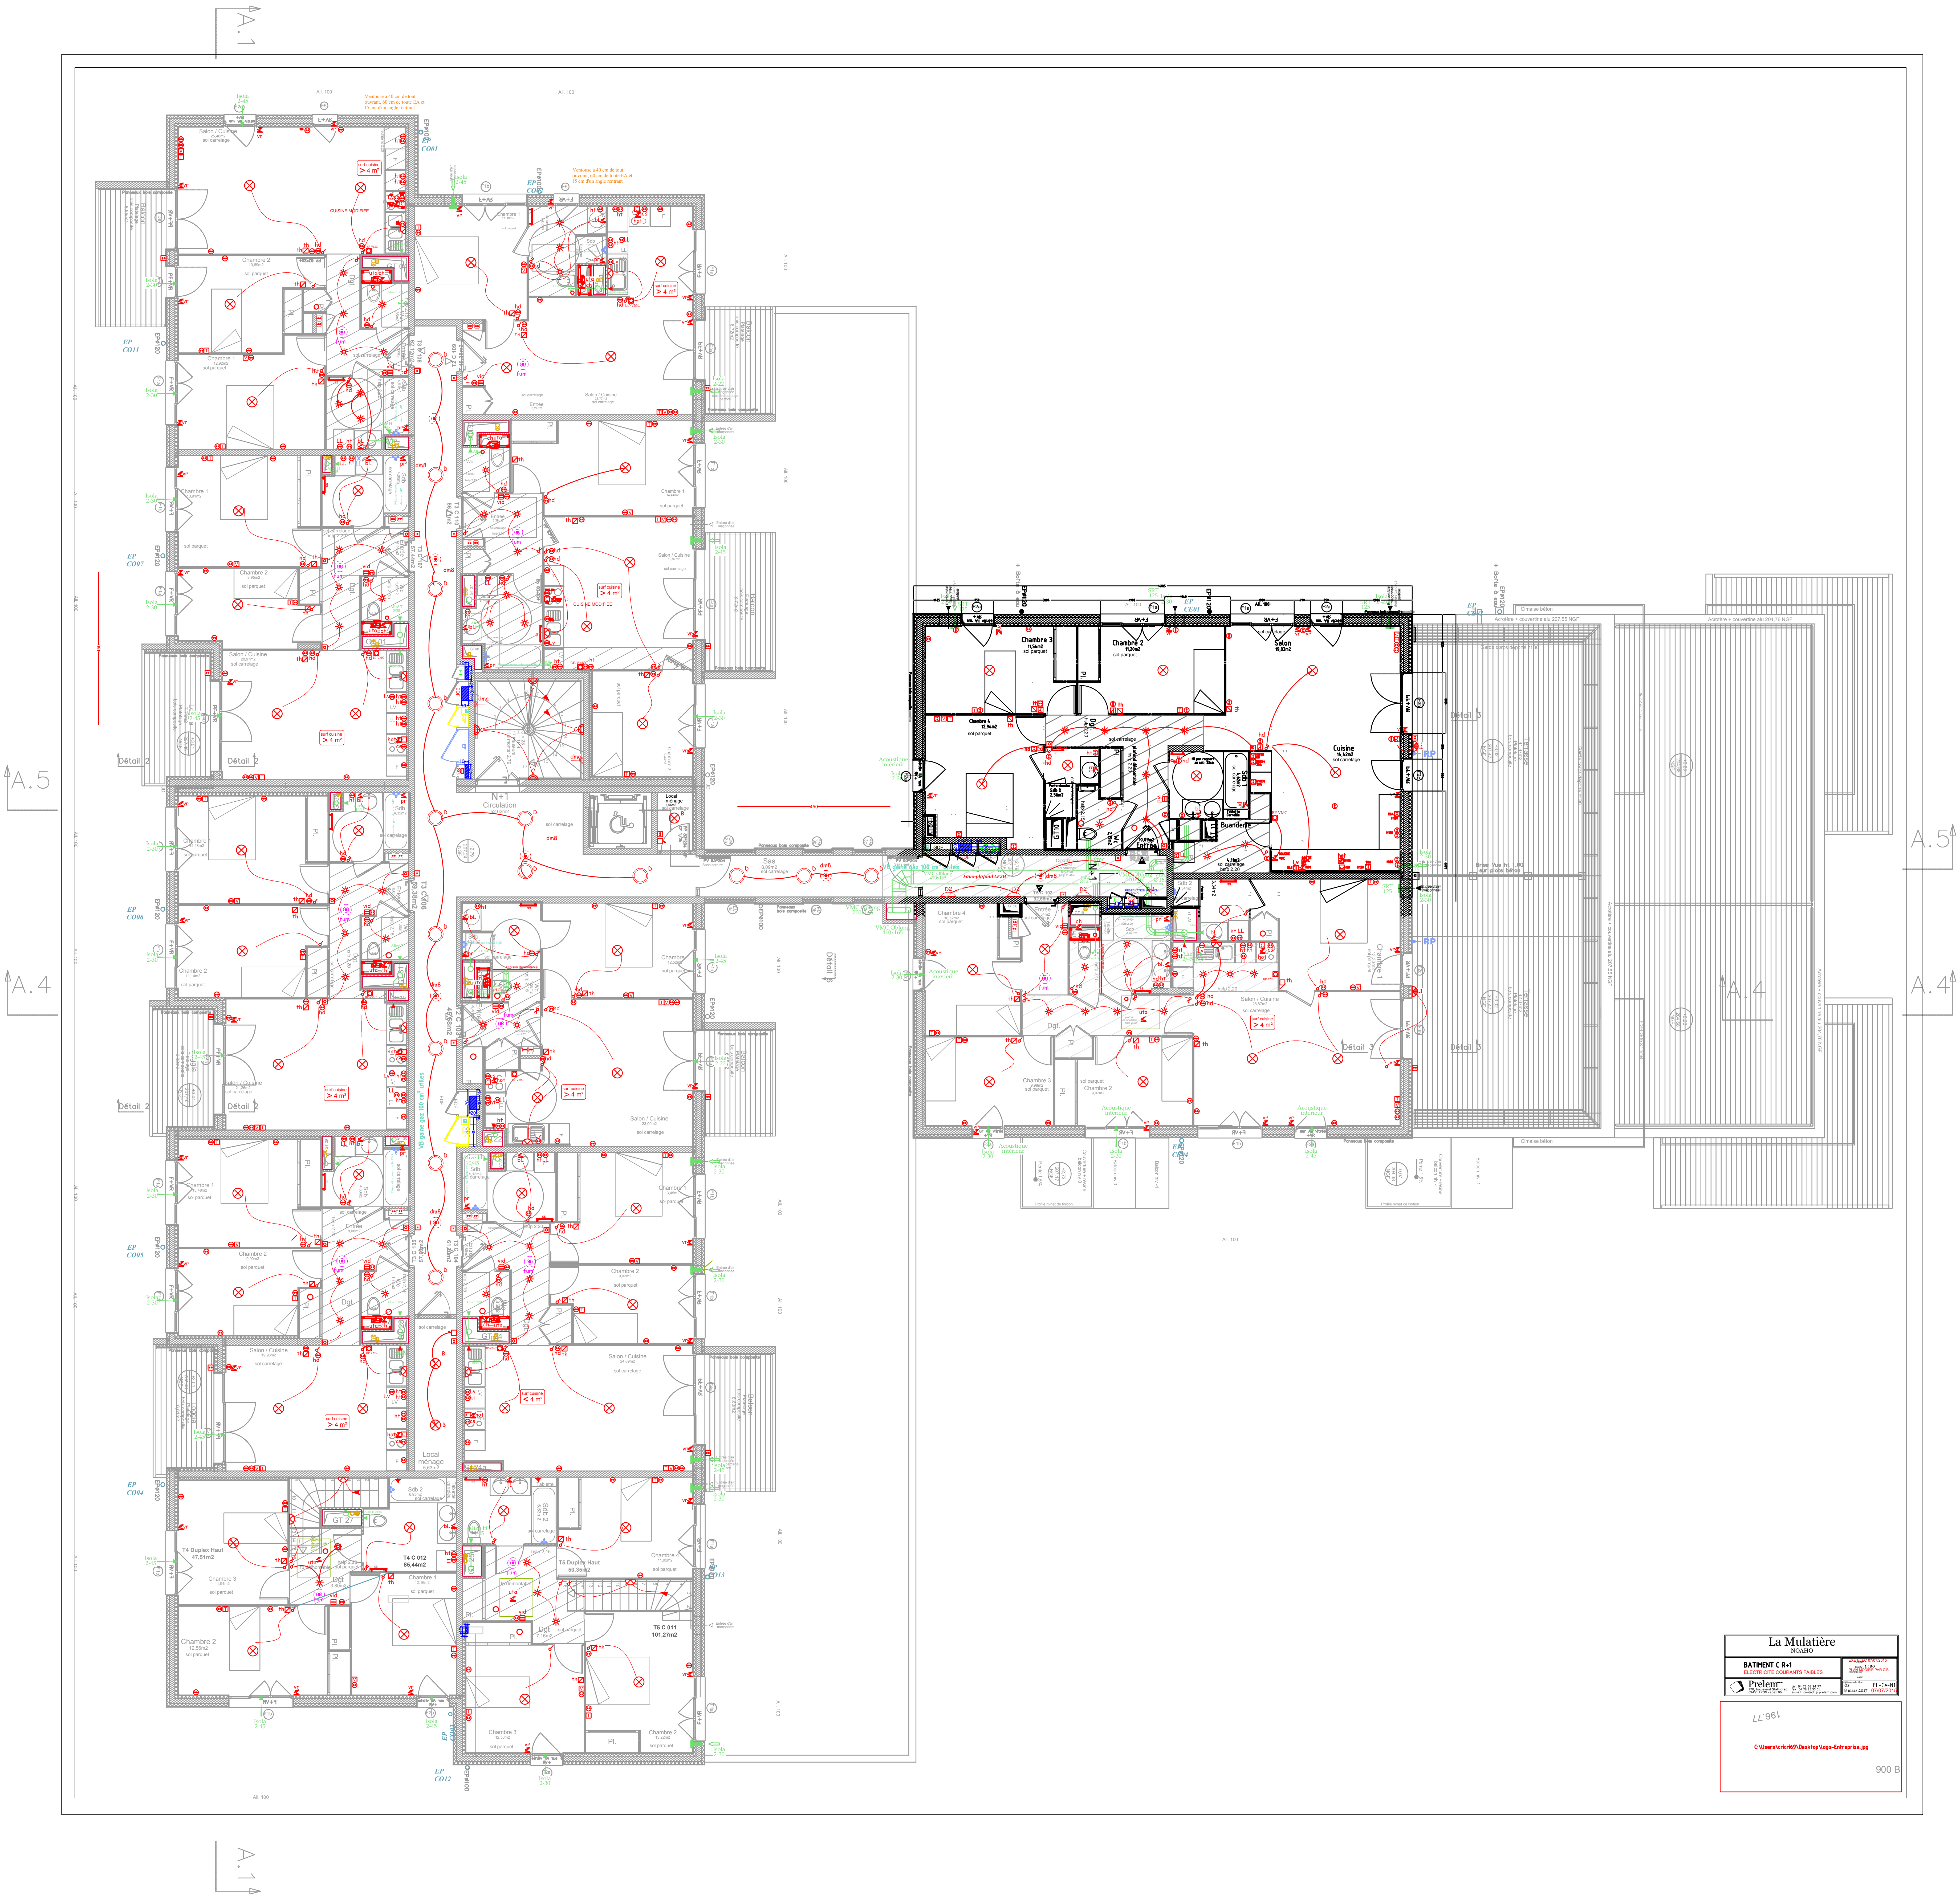

La Mulatière

NOAHO

BATIMENT C R+1

ELECTRICITE COURANTS FAIBLES

EXE ELEC 07/07/2015
Phase
Échelle 1 : 50
PLAN MODIFIE PAR C.B
Imprimé par
Date

Référence du Plan
OS
EL-Ce-N1
8 mars 2017
07/07/2015

Prelem
170, boulevard Stalingrad
69451 LYON cedex 06
tél: 04 78 68 94 77
fax: 04 78 85 55 01
e-mail: contact @ prelem.com

196.77

C:\Users\cricri69\Desktop\logo-Entreprise.jpg

900 B