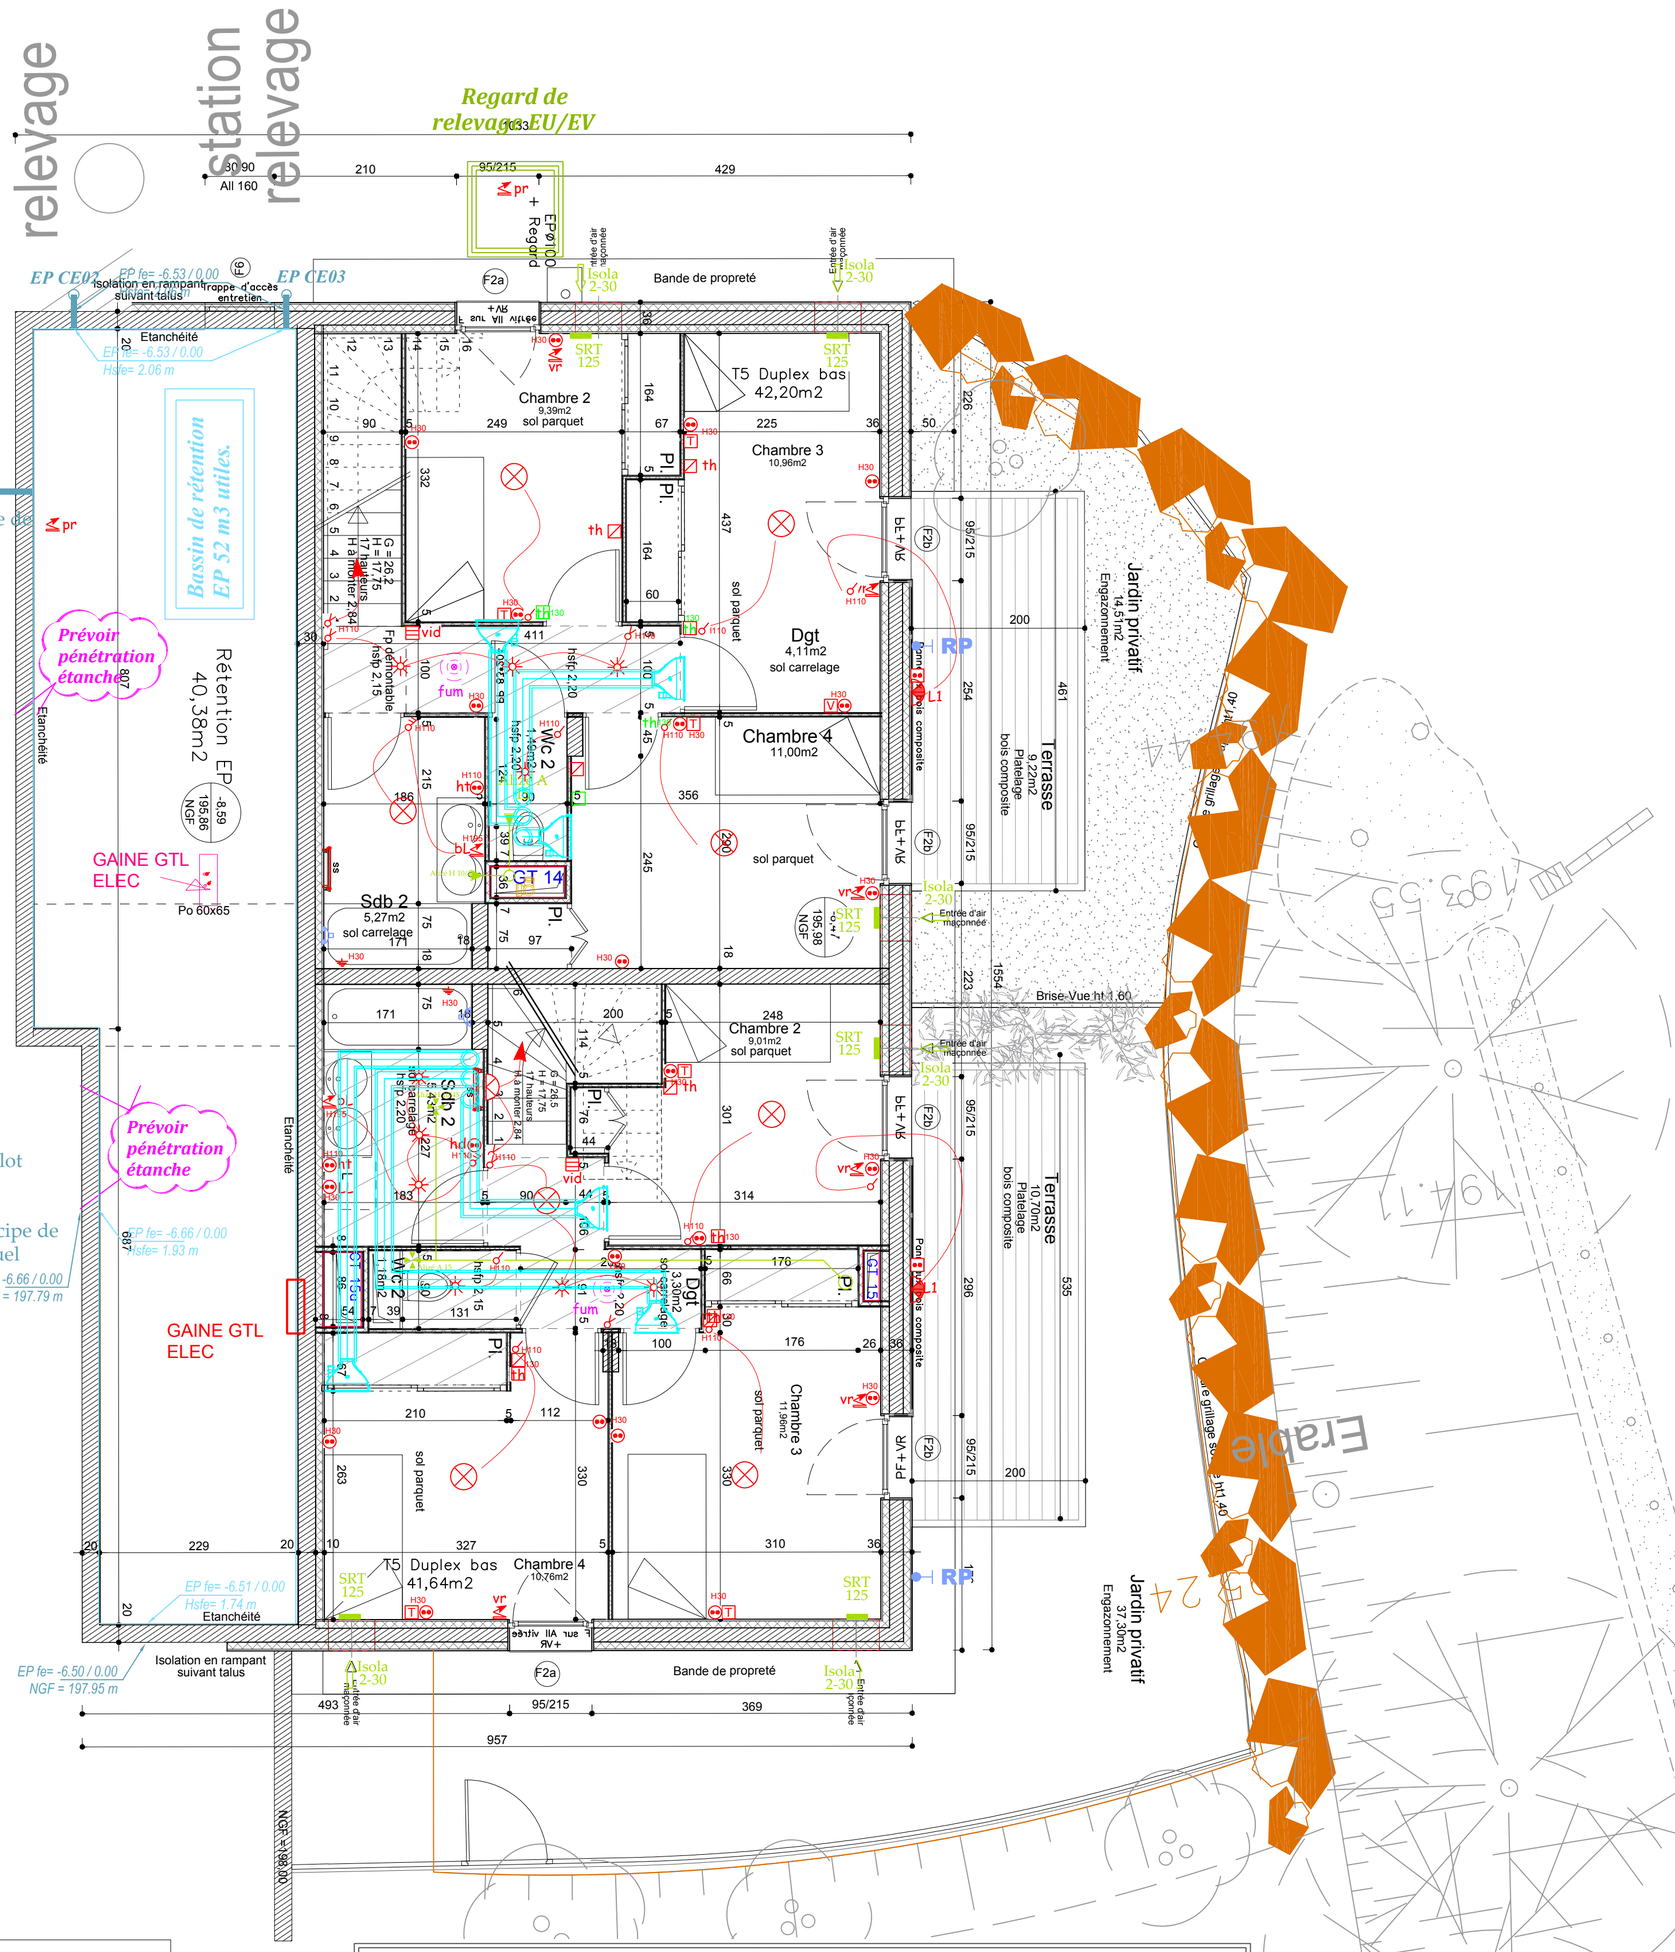


GT
MODIFS
MOD-EL

ELEC-CFO
ELEC-cfa
ELEC-ssi

BT
TELECOM
convecteurs
radiateurs
radiateurs-TXT
CHAUFF
GAZ
cartouche

CALOR IFUGE
CHU
ECS
EF
EP
EPext

vmc-souffl
VMC
CLIM

Prelem fluides

d'après 01_280_150416_DCE_BATC_NIV-3.dwg
dossier prlm\dossiers\noaho\la mulatière\plans reçus\2015-04-20 dm\c
adapté le 2015-04-21
par jean-baptiste

La Mulatière
NOAHO

BATIMENT C SOUS SOL-3
ELECTRICITE COURANTS FAIBLES

EXE ELEC 14/06/2015
Phase
Échelle 1 : 50
PLAN MODIFIE PAR C.B
Imprimé par
Date 14/06/2015

Référence du Plan
OS EL-Ce-70
8 mars 2017

Prelem
170, boulevard Stalingrad
69451 LYON cedex 06
tél: 04 78 68 94 77
fax: 04 78 85 55 01
e-mail: contact @ prelem.com

C:\Users\cricri69\Desktop\logo-Entreprise.jpg