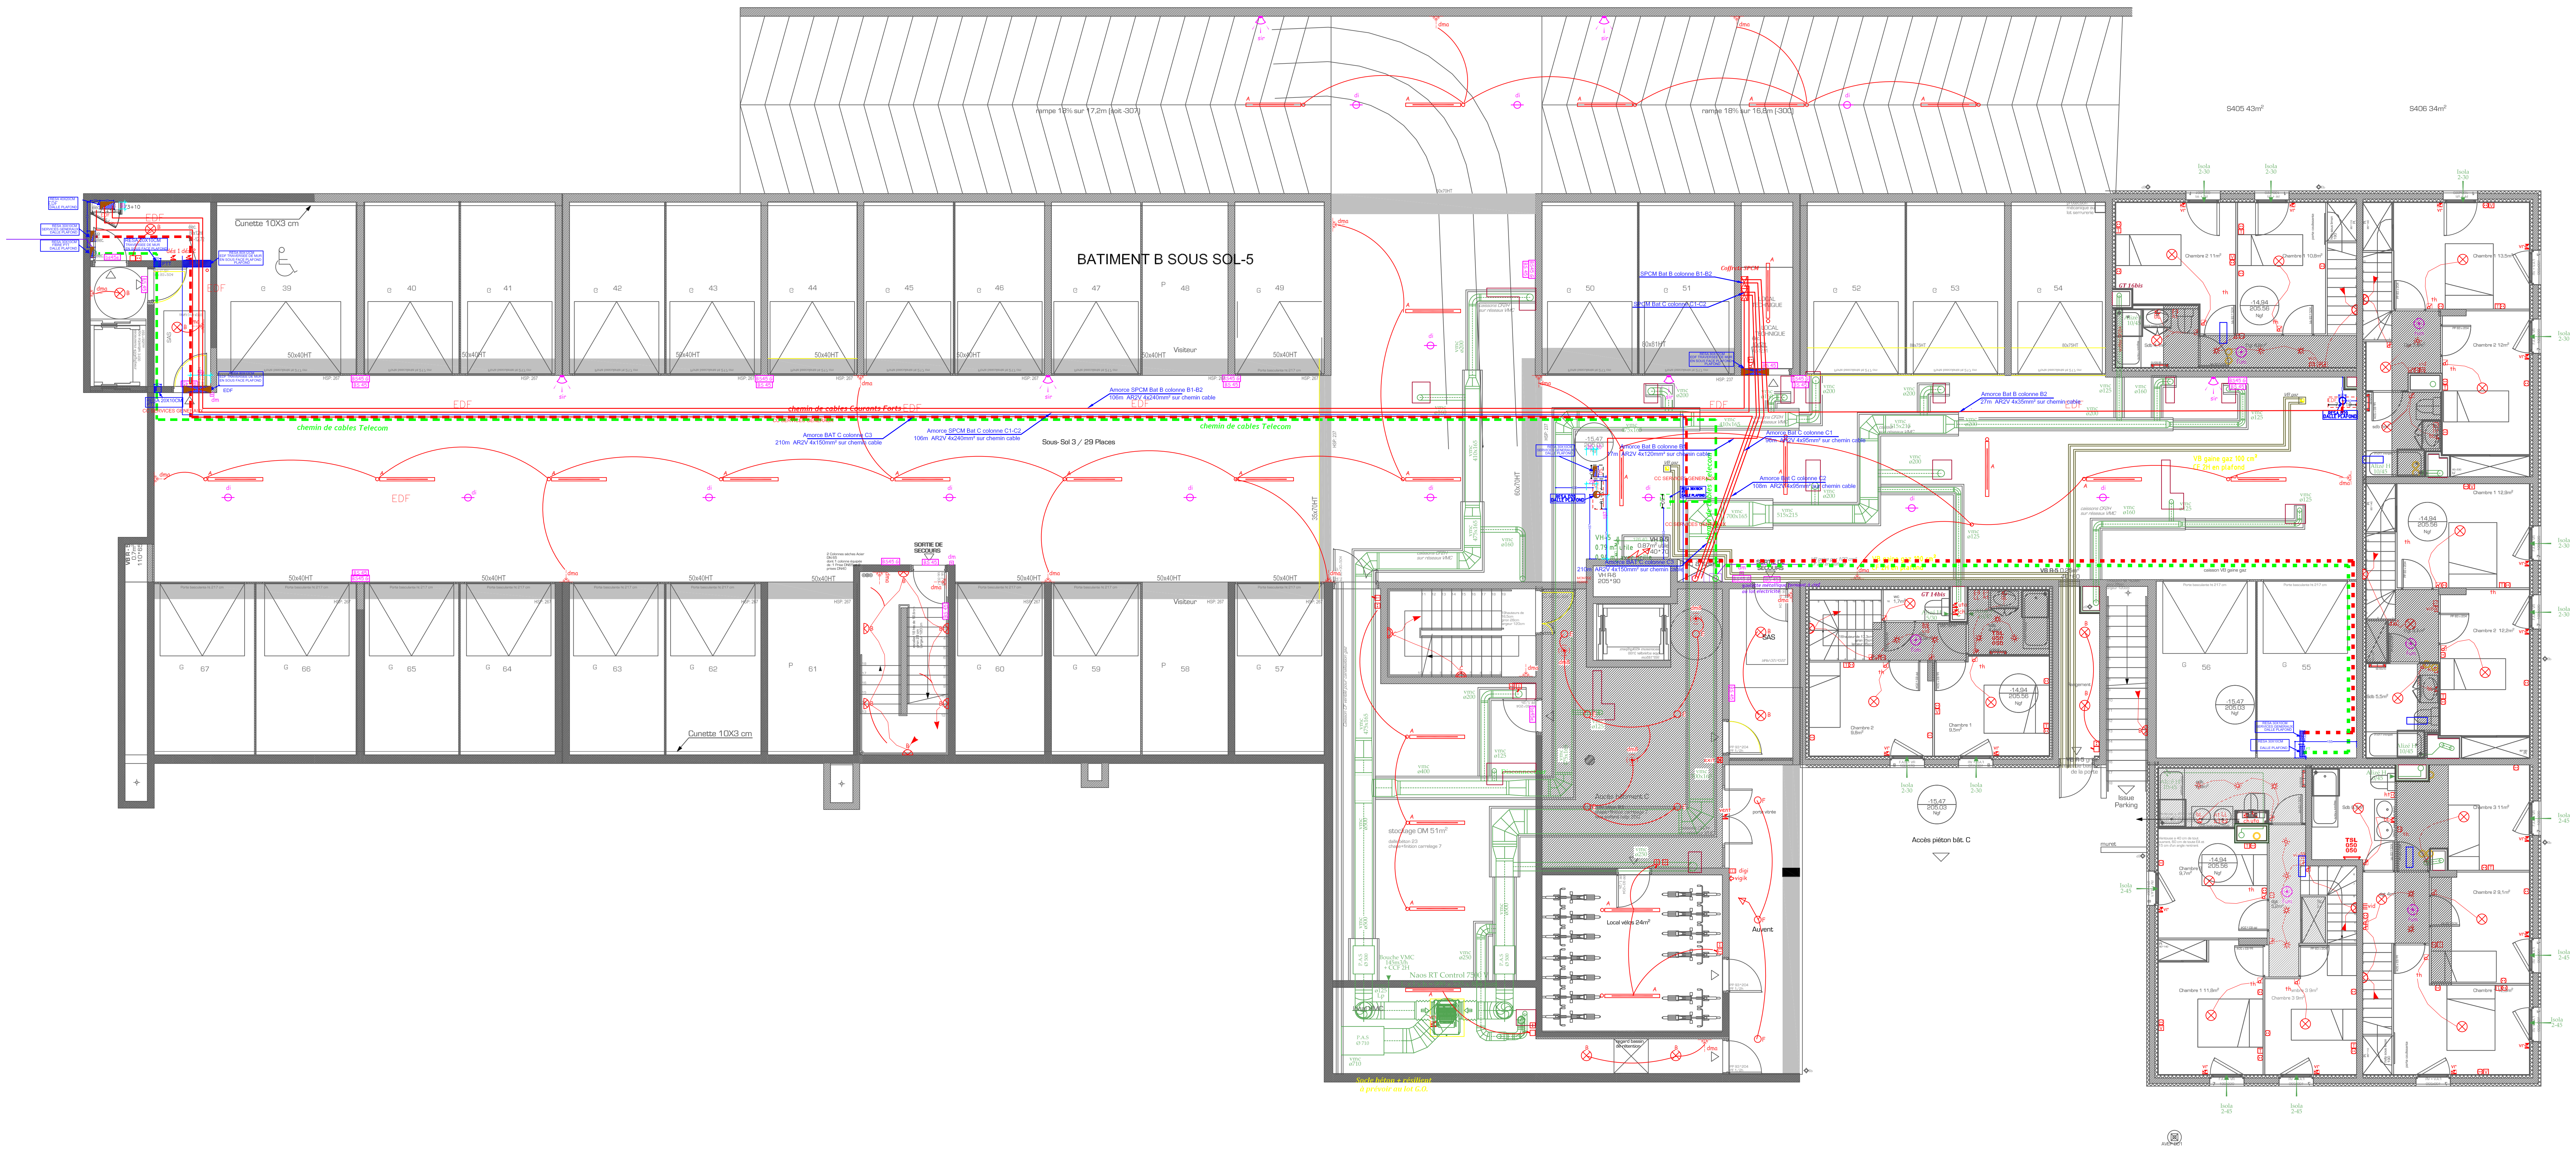
BATIMENT B SOUS SOL-5
Cunette 10X3 cm
chemin de cables Courants Forts
EDF
CO SERVICES GENERAUX
chemin de cables Telecom
Amorce SPCM Bat B colonne B1-B2
106m AR2V 4x240mm² sur chemin cable
Amorce BAT C colonne C3
210m AR2V 4x150mm² sur chemin cable
Amorce SPCM Bat C colonne C1-C2
106m AR2V 4x240mm² sur chemin cable
Sous- Sol 3 / 29 Places
50x40HT
35x70HT
Visiteur
Porte basculante ht 217 cm
HSP: 267
HSP: 237
BS45 G
BS 45
dma
sir
di
dm
SORTIE DE SECOURS
2 Colonnes séches Acier DN 65 dont 1 colonne équipée de :1 Prise DN65 et 2 prises DN40
39
40
41
42
43
44
45
46
47
48
49
50
51
52
53
54
55
56
57
58
59
60
61
62
63
64
65
66
67
Local vélos 24m²
Accès piéton bât. C

Sortie VMC dans regard
maçonné avec chapeau
pare-pluie DN 500.
Hors lots techniques

La Mulatière
NOAHO

BATIMENT B SOUS SOL-5
ELECTRICITE COURANTS FAIBLES

Prelem
170, boulevard Stalingrad
69451 LYON cedex 06
tél: 04 78 68 94 77
fax: 04 78 85 55 01
e-mail: contact @ prelem.com

Phase EXE ELEC 14/09/2015
Échelle 1 : 50
Imprimé par PLAN MODIFIE PAR C.B
Date 14/09/2015
Référence du Plan PB-B-B50
OS
28 sept. 2015
INDICE C

C:\Users\cricri69\Desktop\logo-Entreprise.jpg