"2ème Tranche BAT D, E, F"

DISTANCE CV2 & CV4			
DISTANCE	M	0 à 50 m	>50 à 100 m
LECTEURS	S mm²	0,75	
BP DE SORTIE	D mm	6/10	
DPW; DPTEL; DBxx	S mm²	0,75	
ALIM	S mm²	0,75	▨

NOM DES BORNES POUR UNE PORTE

Porte

L+ L- BP+ BP- COM NF NO

NOTA : METTRE LE SWITCH SUR LA POSITION "B" DES MONITEURS

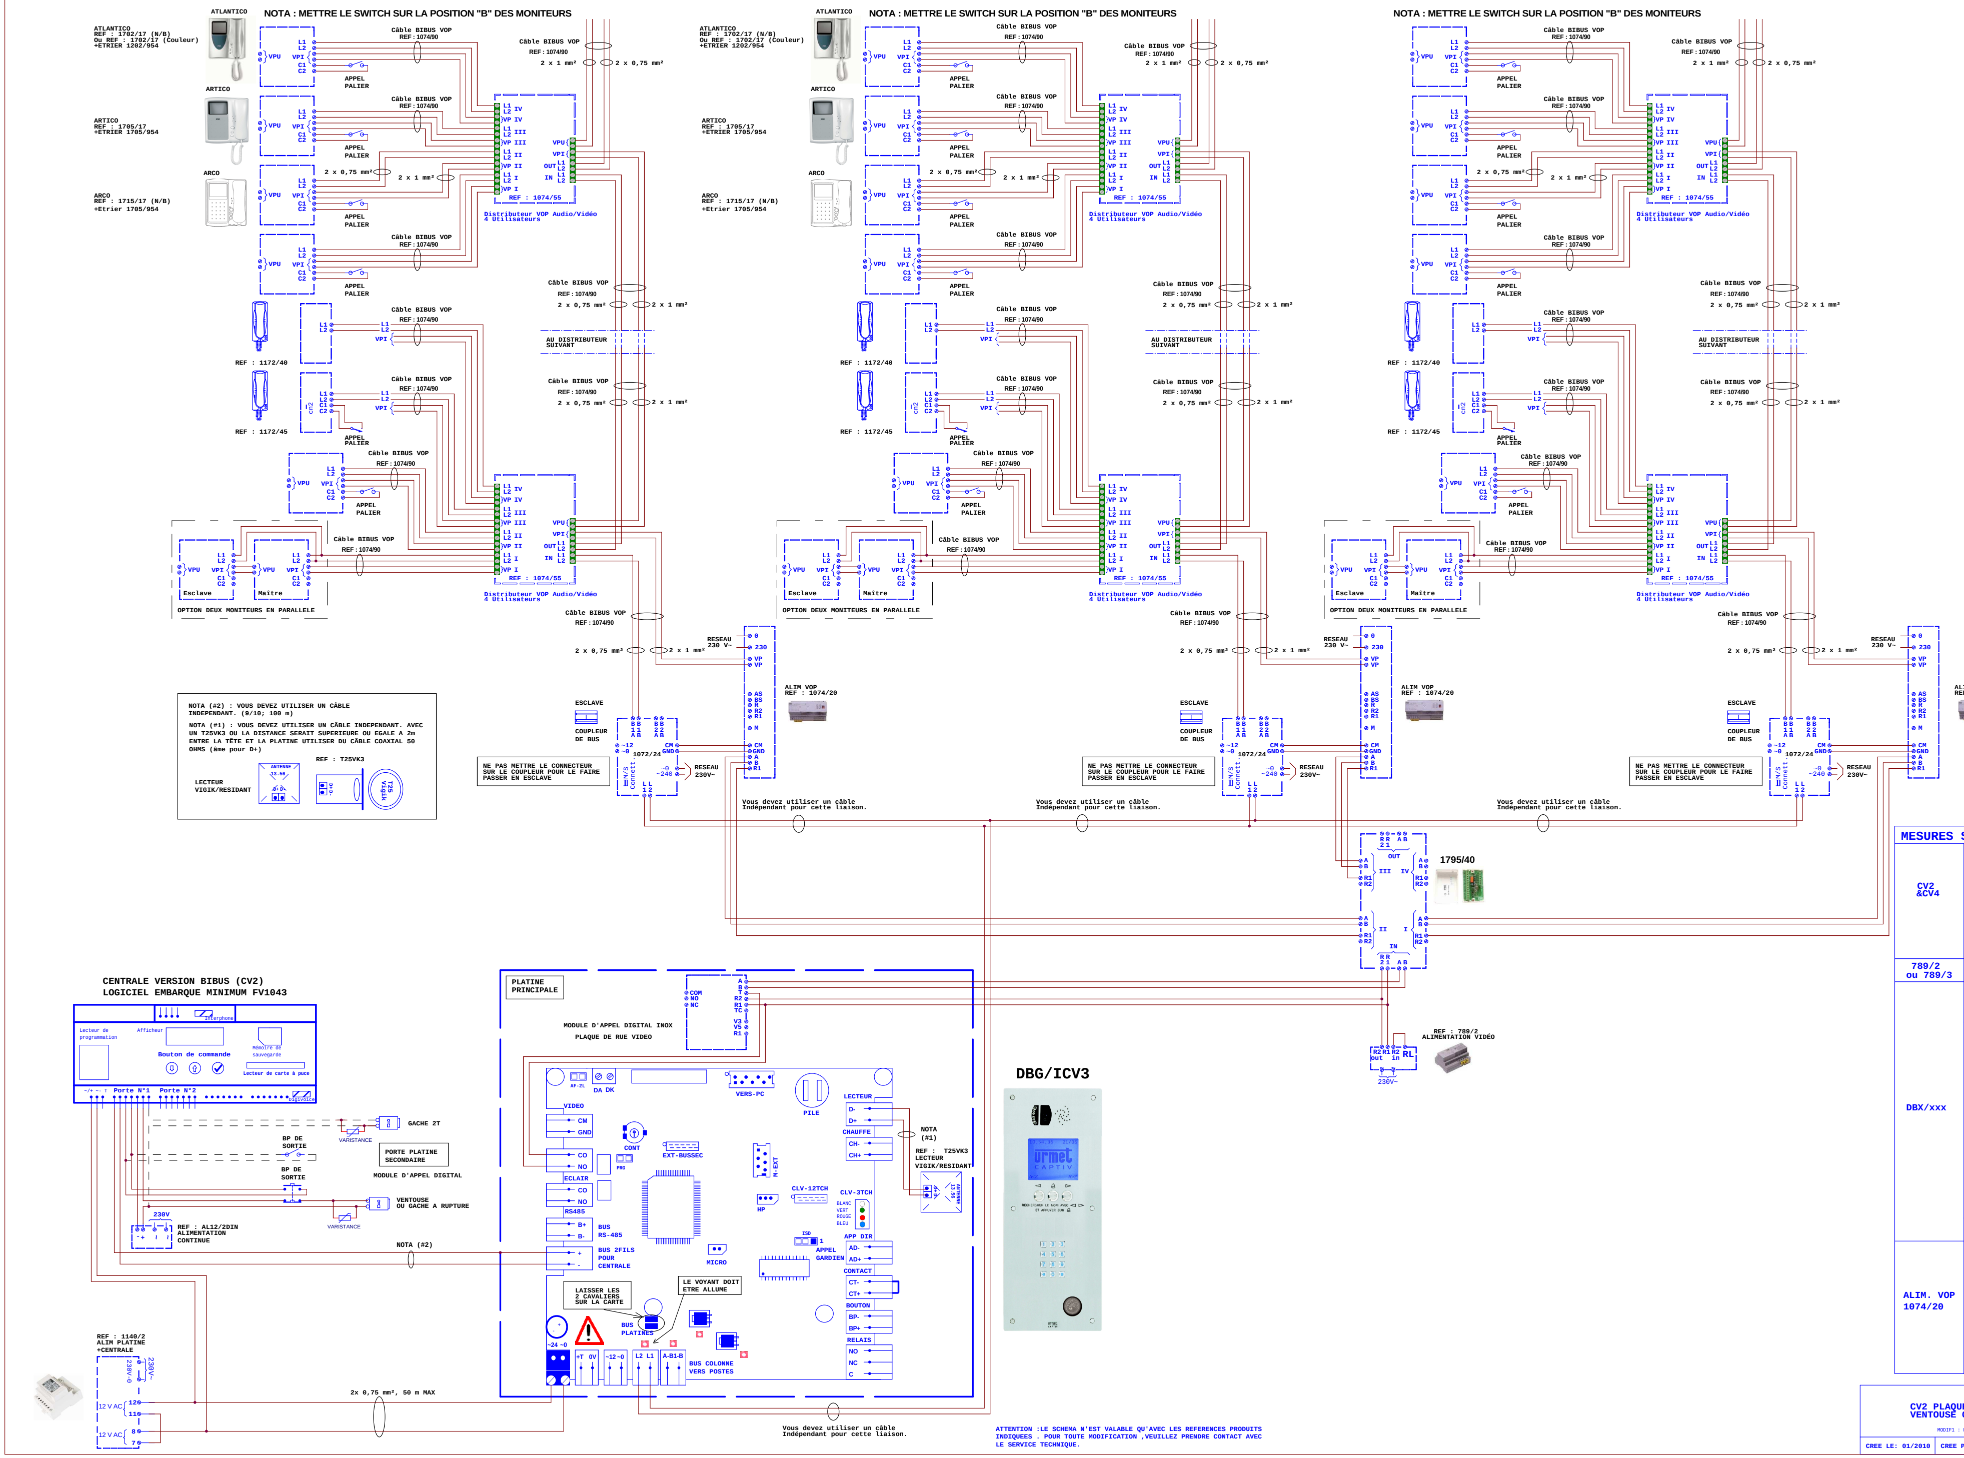

NOTA (#2) : VOUS DEVEZ UTILISER UN CÂBLE INDEPENDANT. (9/10; 100 m)

NOTA (#1) : VOUS DEVEZ UTILISER UN CÂBLE INDEPENDANT. AVEC UN T25VK3 OU LA DISTANCE SERAIT SUPERIEURE OU EGALE A 2m ENTRE LA TÊTE ET LA PLATINE UTILISER DU CÂBLE COAXIAL 50 OHMS (âme pour D+)

LECTEUR VIGIK/RESIDANT

ANTENNE 13.56 D+ D-

REF : T25VK3

D+ D-

T25 Vigik

DU COUPLEUR + 1074/20 AUX POSTES					
DISTANCE MAX	M m	50	100	200	▨
VPI,VPU,L1,L2		CABLE 1074/90			▨
DU 1074/20 A LA PLATINE DE RUE					
DISTANCE MAX	M m	50	100	200	400
R1,R2	D mm	▨		▨	▨
	S mm²	0,75		2	6
A,B	D mm	PAIRE TORSADEE 8/10			
SIGNAL PILOTE					
DISTANCE MAX	M m	10	▨		
CM,GND	S mm²	0,75	▨		
DU COUPLEUR A LA PLATINE DE RUE PRINCIPALE					
DISTANCE MAX	M m	50	100	200	400
L1,L2,0~,12~	D mm	▨		▨	
	S mm²	0,75		2	6
DE LA PLATINE DE RUE A LA GACHE					
DISTANCE MAX	M m	50	▨		
	S mm²	2	▨		

FORMULES DIAMETRES/SECTIONS

$S = 3,14 \times (D/2)^2$ (Section en mm²)

$D = 2 \times \sqrt{S/3,14}$ (Diamètre en mm)

MESURES SUR LE SYSTEME BIBUS OPEN (V1)

CV2 &CV4	Alimentation centrale avec 1140/2 Mesure sur la centrale ~/+, ~/- : 23-28 Vac BUS CENTRALE<->PLATINE Ou BUS CENTRALE<->RECEPEUR Ou BUS CENTRALE<->LECTEUR PROX. L1+, L1- : 11,5 Vdc (CV2,CV4) L2+, L2- : 11,5 Vdc (CV2,CV4) L3+, L3- : 11,5 Vdc (CV4) L4+, L4- : 11,5 Vdc (CV4) Bouton poussoir de sortie (contact NO) (sans appuyer sur le BP) BP1+, BP1- : 5,7 Vdc (CV2,CV4) BP2+, BP2- : 5,7 Vdc (CV2,CV4) BP3+, BP3- : 5,7 Vdc (CV4) BP4+, BP4- : 5,7 Vdc (CV4)
789/2 ou 789/3	'R2in' raccordé à 'RL' R1,R2out : 18-20 Vdc
DBX/xxx	**Platine défilement Secondaire** B1A-B1B(sérigraphie circuit A-B1-B): 22 Vdc en permanence. Poste décroché après appel mesure sur L1,L2 d'un poste Audio ~ 18 Vdc
	Platine défilement Principale Dans le système Bibus, plusieurs plaques de rue Peuvent être câblées en parallèle avec L1,L2. Par Contre, une seule doit alimenter ce bus, c'est le Rôle de la platine maître en mettant les pontets sur Leur picots. (Les coupleurs 1072/24 peuvent être aussi Configurés en Maître ou en Esclave) ☐ Les 2 pontets de la carte sont enlevés Sans les fil sur le bornier L1,L2 L1,L2 (sérigraphie circuit L1,L2): 0Vdc ■ Les 2 pontets de la carte sont en place Sans les fil sur le bornier L1,L2 L1,L2 (sérigraphie circuit L1,L2): 22Vdc **Platine avec caméra** R1,R2 : 18-20 Vdc (en permanence) R1,T : Déclenchement de la caméra Effectué par le 'Relais Vidéo' CO, NO Quand le contact se ferme l'éclairage de la Caméra s'allume en blanc, lors de l'appel. Le signal vidéo est disponible sur A, B Une deuxième sortie vidéo est disponible pour Envoyer le signal vidéo sur câble coaxial (KX6 <200m) V3 : âme coaxial V5 : tresse coaxial
	Bus de communication Platine <-> Centrale B2F + - : 11,5 Vdc
ALIM. VOP 1074/20	Alimentation Vidéo BIBUS V.O.P (Vidéo on power) R1,R2 : 18-20 Vdc (en permanence) A,B : Entrée signal vidéo AS,BS : Deuxième entrée signal vidéo nécessite Un pilotage par la borne 'R' VP,VP : Alimentation du moniteur colonne + Signal Vidéo Ses bornes alimentent les moniteurs de la colonne. Sans appel en cours ou absence de signal vidéo (A,B;AS,BS) VP,VP: 0 Vdc Appel en cours VP,VP : 28 Vdc (VP, VP chargé avec sa colonne et signal vidéo présent) Appel en cours VP,VP : ~30 Vdc (VP, VP à vide sans sa colonne et signal vidéo présent)

ATTENTION :LE SCHEMA N'EST VALABLE QU'AVEC LES REFERENCES PRODUITS INDIQUEES . POUR TOUTE MODIFICATION ,VEUILLEZ PRENDRE CONTACT AVEC LE SERVICE TECHNIQUE.

CV2 PLAQUE A DEFILEMENT BIBUS VIDEO VENTOUSE OU GACHE 2T

MODIF1 : FILS CAMERA R1,T -> PLATINE CO,NO VIDEO

CREE LE: 01/2010	CREE PAR: TV	MODIFIE LE:05/2010	N° MODIF. 1	SCH: DV4F4934

urmet CAPTIV