


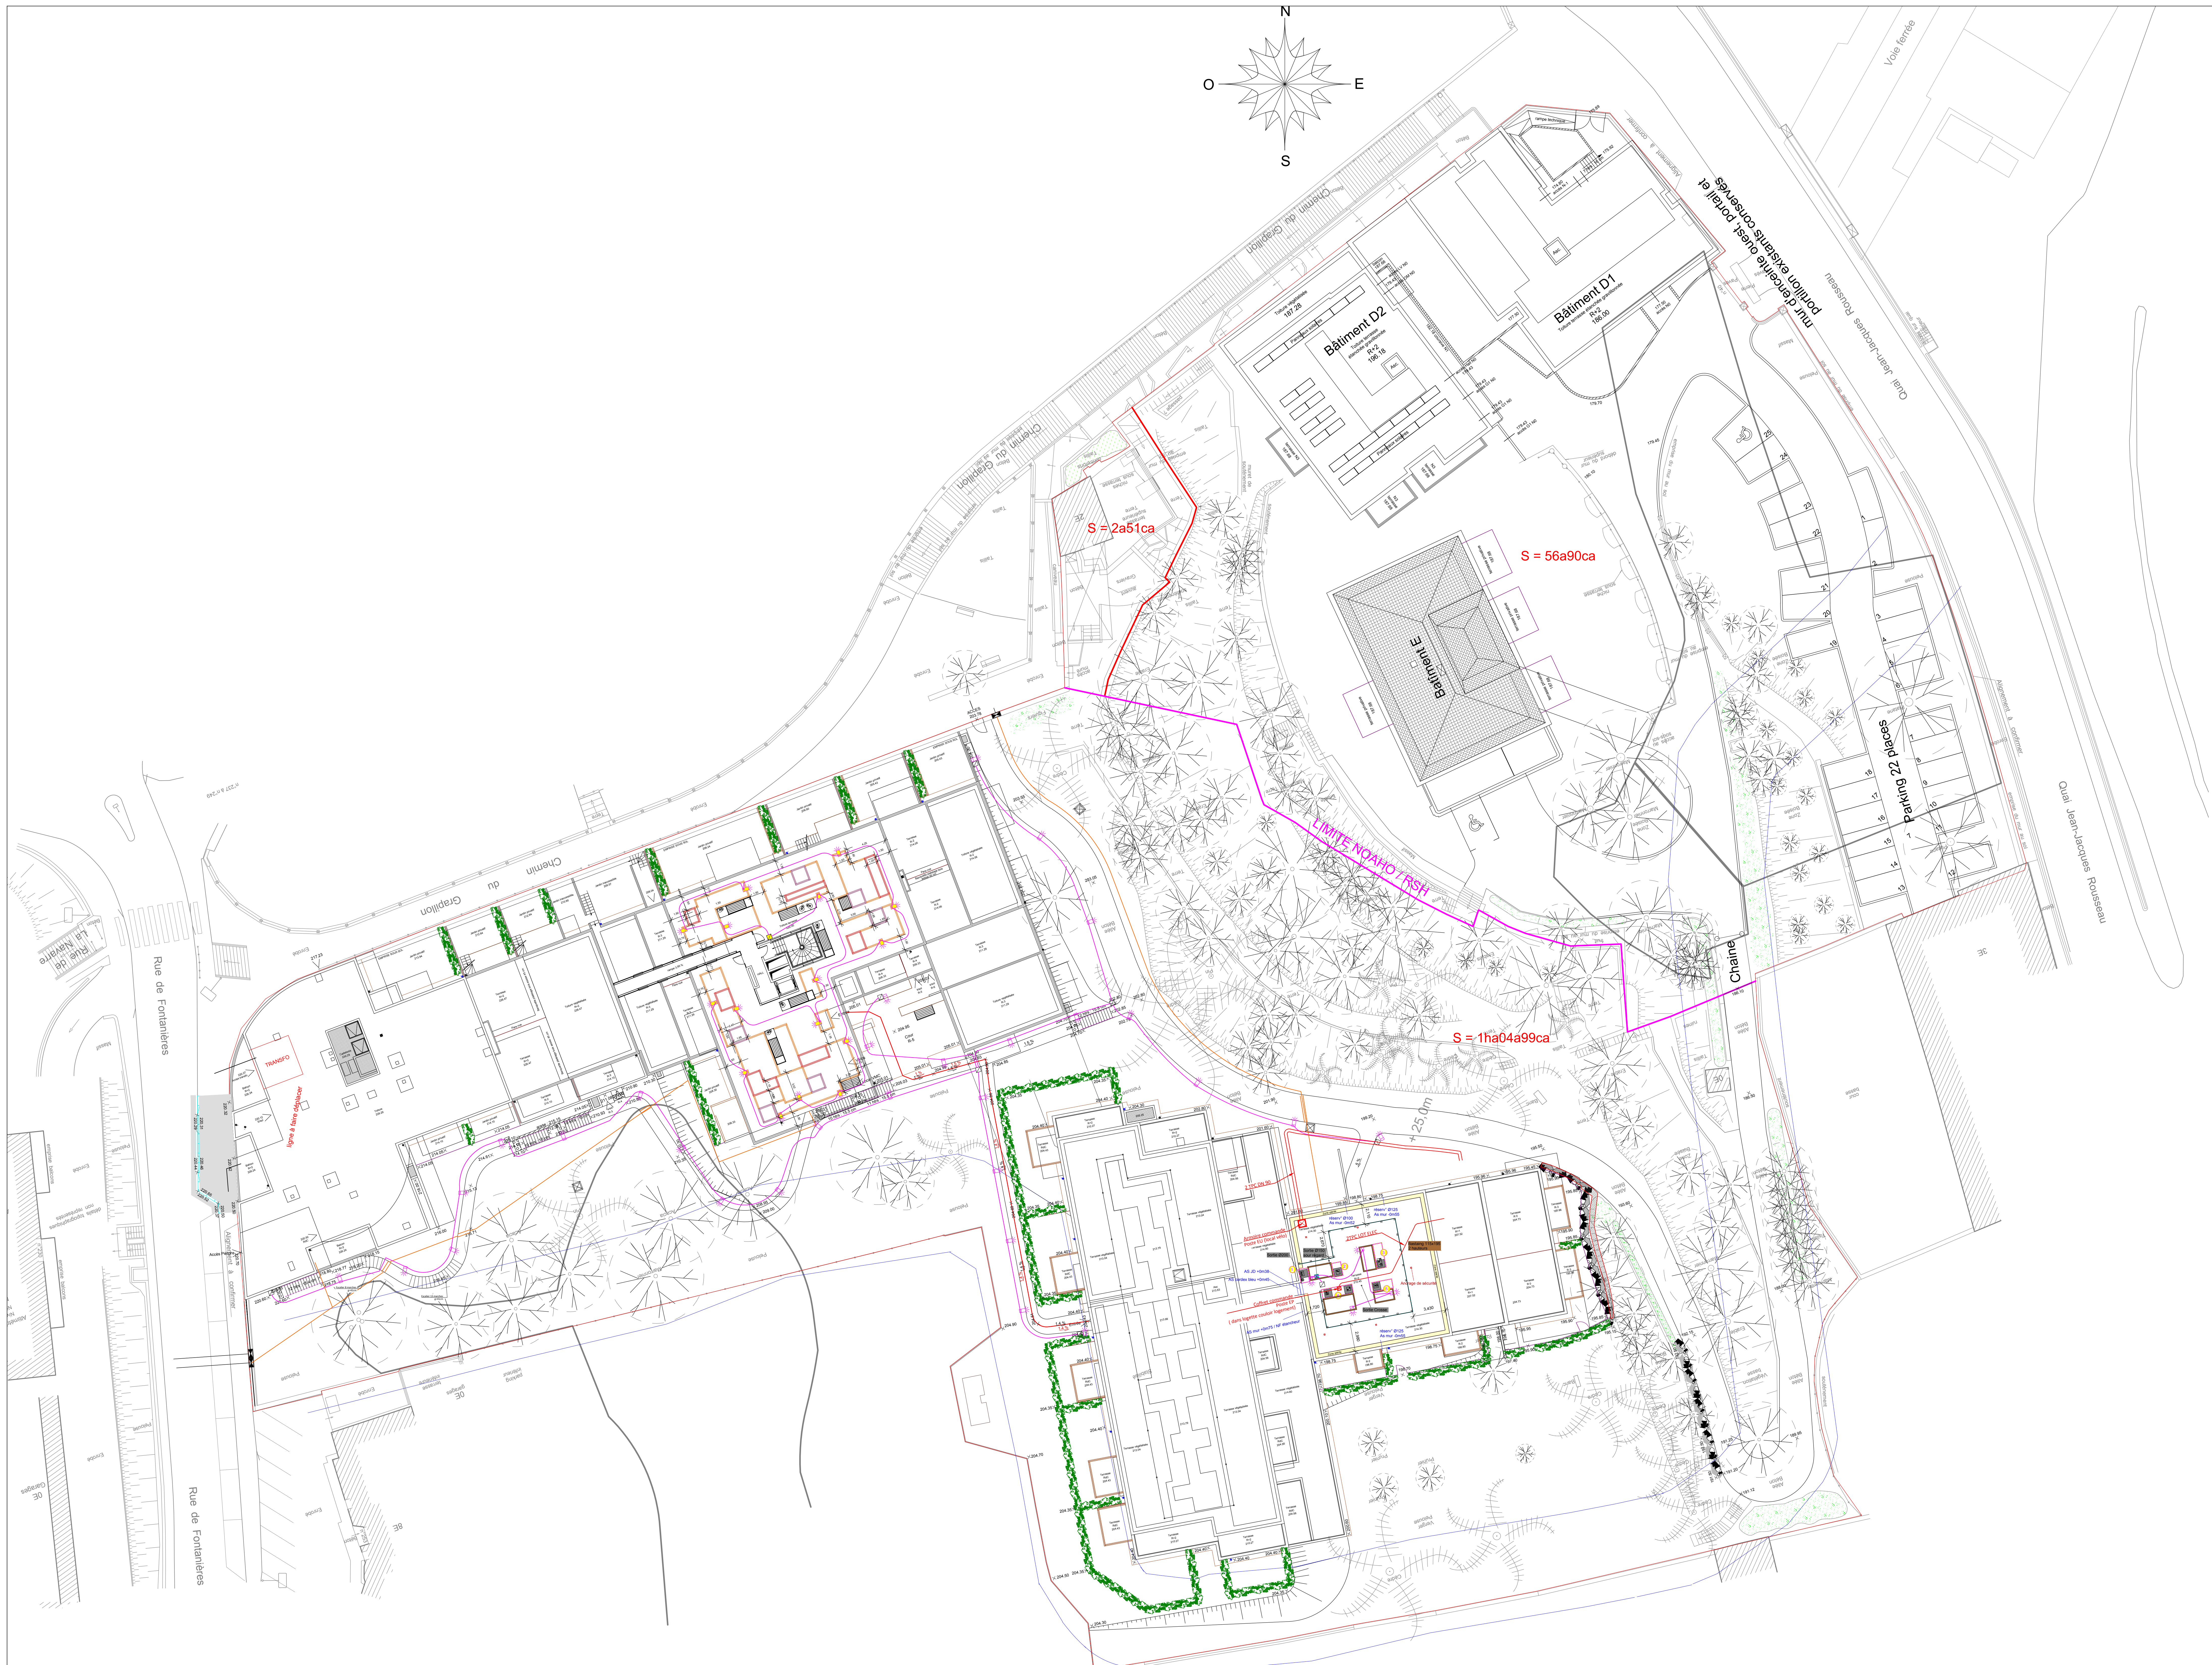

- LEGENDE PROJET
- VMC - Edicule maçonné - grille 4 côtés - 70 x 70 x 70 cm
 - EP - Cheminée de visite - Ø 800
 - EP - Regard de vannage pour pompes immergées - Ø 800
 - VMC - Tranchée seule
 - EP - Regard de branchement - 50 x 50 cm
 - GAZ - Coffret S2300 (hors lot VRD)
 - GAZ - Tranchée seule
 - GAZ - Caniveau technique - 30 x 30 int
 - EP - Grille plate carrée - 80 x 80 cm
 - EP - Grille plate carrée - 40 x 40 cm
 - EP - Caniveau à grille - I : 15 cm
 - EP - Caniveau à grille - I : 25 cm
 - ERDF - Raccordement transfo (travaux concessionnaire)
 - EP - Canalisat PVC - CR8 ou PE de refoulement
 - ERDF - Fourreau 90
 - EU - Station de relevage
 - EU - Cheminée de visite - Ø 1000
 - EU - Cheminée de visite - Ø 800
 - EU - Station de relevage
 - EU - Canalisat PVC - CR8 ou PE de refoulement
 - CABLE - Chambre L2T (travaux concessionnaire)
 - CABLE - Gaine H4 (travaux concessionnaire)
 - SG - Chambre de tirage - 50 x 50 cm
 - SG - 2 fourreaux 63
 - ECL - Chambre de tirage - 50 x 50 cm
 - ECL - Borne lumineuse - htr : 1.5 m
 - ECL - Câblage sous fourreau 63
 - ARRO - Canalisat peHd DN 40 sous fourreau Ø 63
 - ARRO - Canalisat peHd DN 32
 - ARRO - Canalisat peHd DN 32 sous fourreau Ø 63
 - ARRO - Canalisat peHd DN 16 (départ G&G)
 - ARRO - Regard de branchement - 50 x 50 cm
 - AEP - Bouche à clé (travaux concessionnaire)
 - AEP - Poteau incendie (travaux concessionnaire)
 - AEP - Canalisat peHd (travaux concessionnaire)
 - PTT - Chambre L2T (travaux concessionnaire)
 - PTT - Gaine H4 (travaux concessionnaire)
 - ARRO - Bouche d'arrosage incongelable - DN 32
 - ARRO - Vidange

NOAHO
Cité Park - Bâtiment D
23, Avenue de Fourmagnol
69 300 - CALUIRE ET CUIRE

CONSTRUCTION D'UN
ENSEMBLE IMMOBILIER
40, Quai Jean-Jacques Rousseau
Rue des Fontanières
69 350 - LA MULATIERE

PLAN DES RESEAUX SECS

PHASE DOE	N° PLAN 03	IND 01		
RD	DATE	MODIFICATIONS	DESSEIN PAR	CONTROLE PAR
00	16/02/2017	1ère diffusion	O COISSIEU	A GIL

DEAL

CHAZAL

ATELIER D'IS
11, Rue de la République
69 001 - LYON
Tel : 04 78 33 20 20
ateliers@deal.fr

ATELIER DE LA PASSERELLE
30, Rue de la République
69 001 - LYON
Tel : 04 78 33 20 20
a.p@passerelle-lyon.fr

SPRINGER Aménagement
440, Rue de la République
69 001 - LYON
Tel : 04 78 33 20 20
springer@springer.fr