




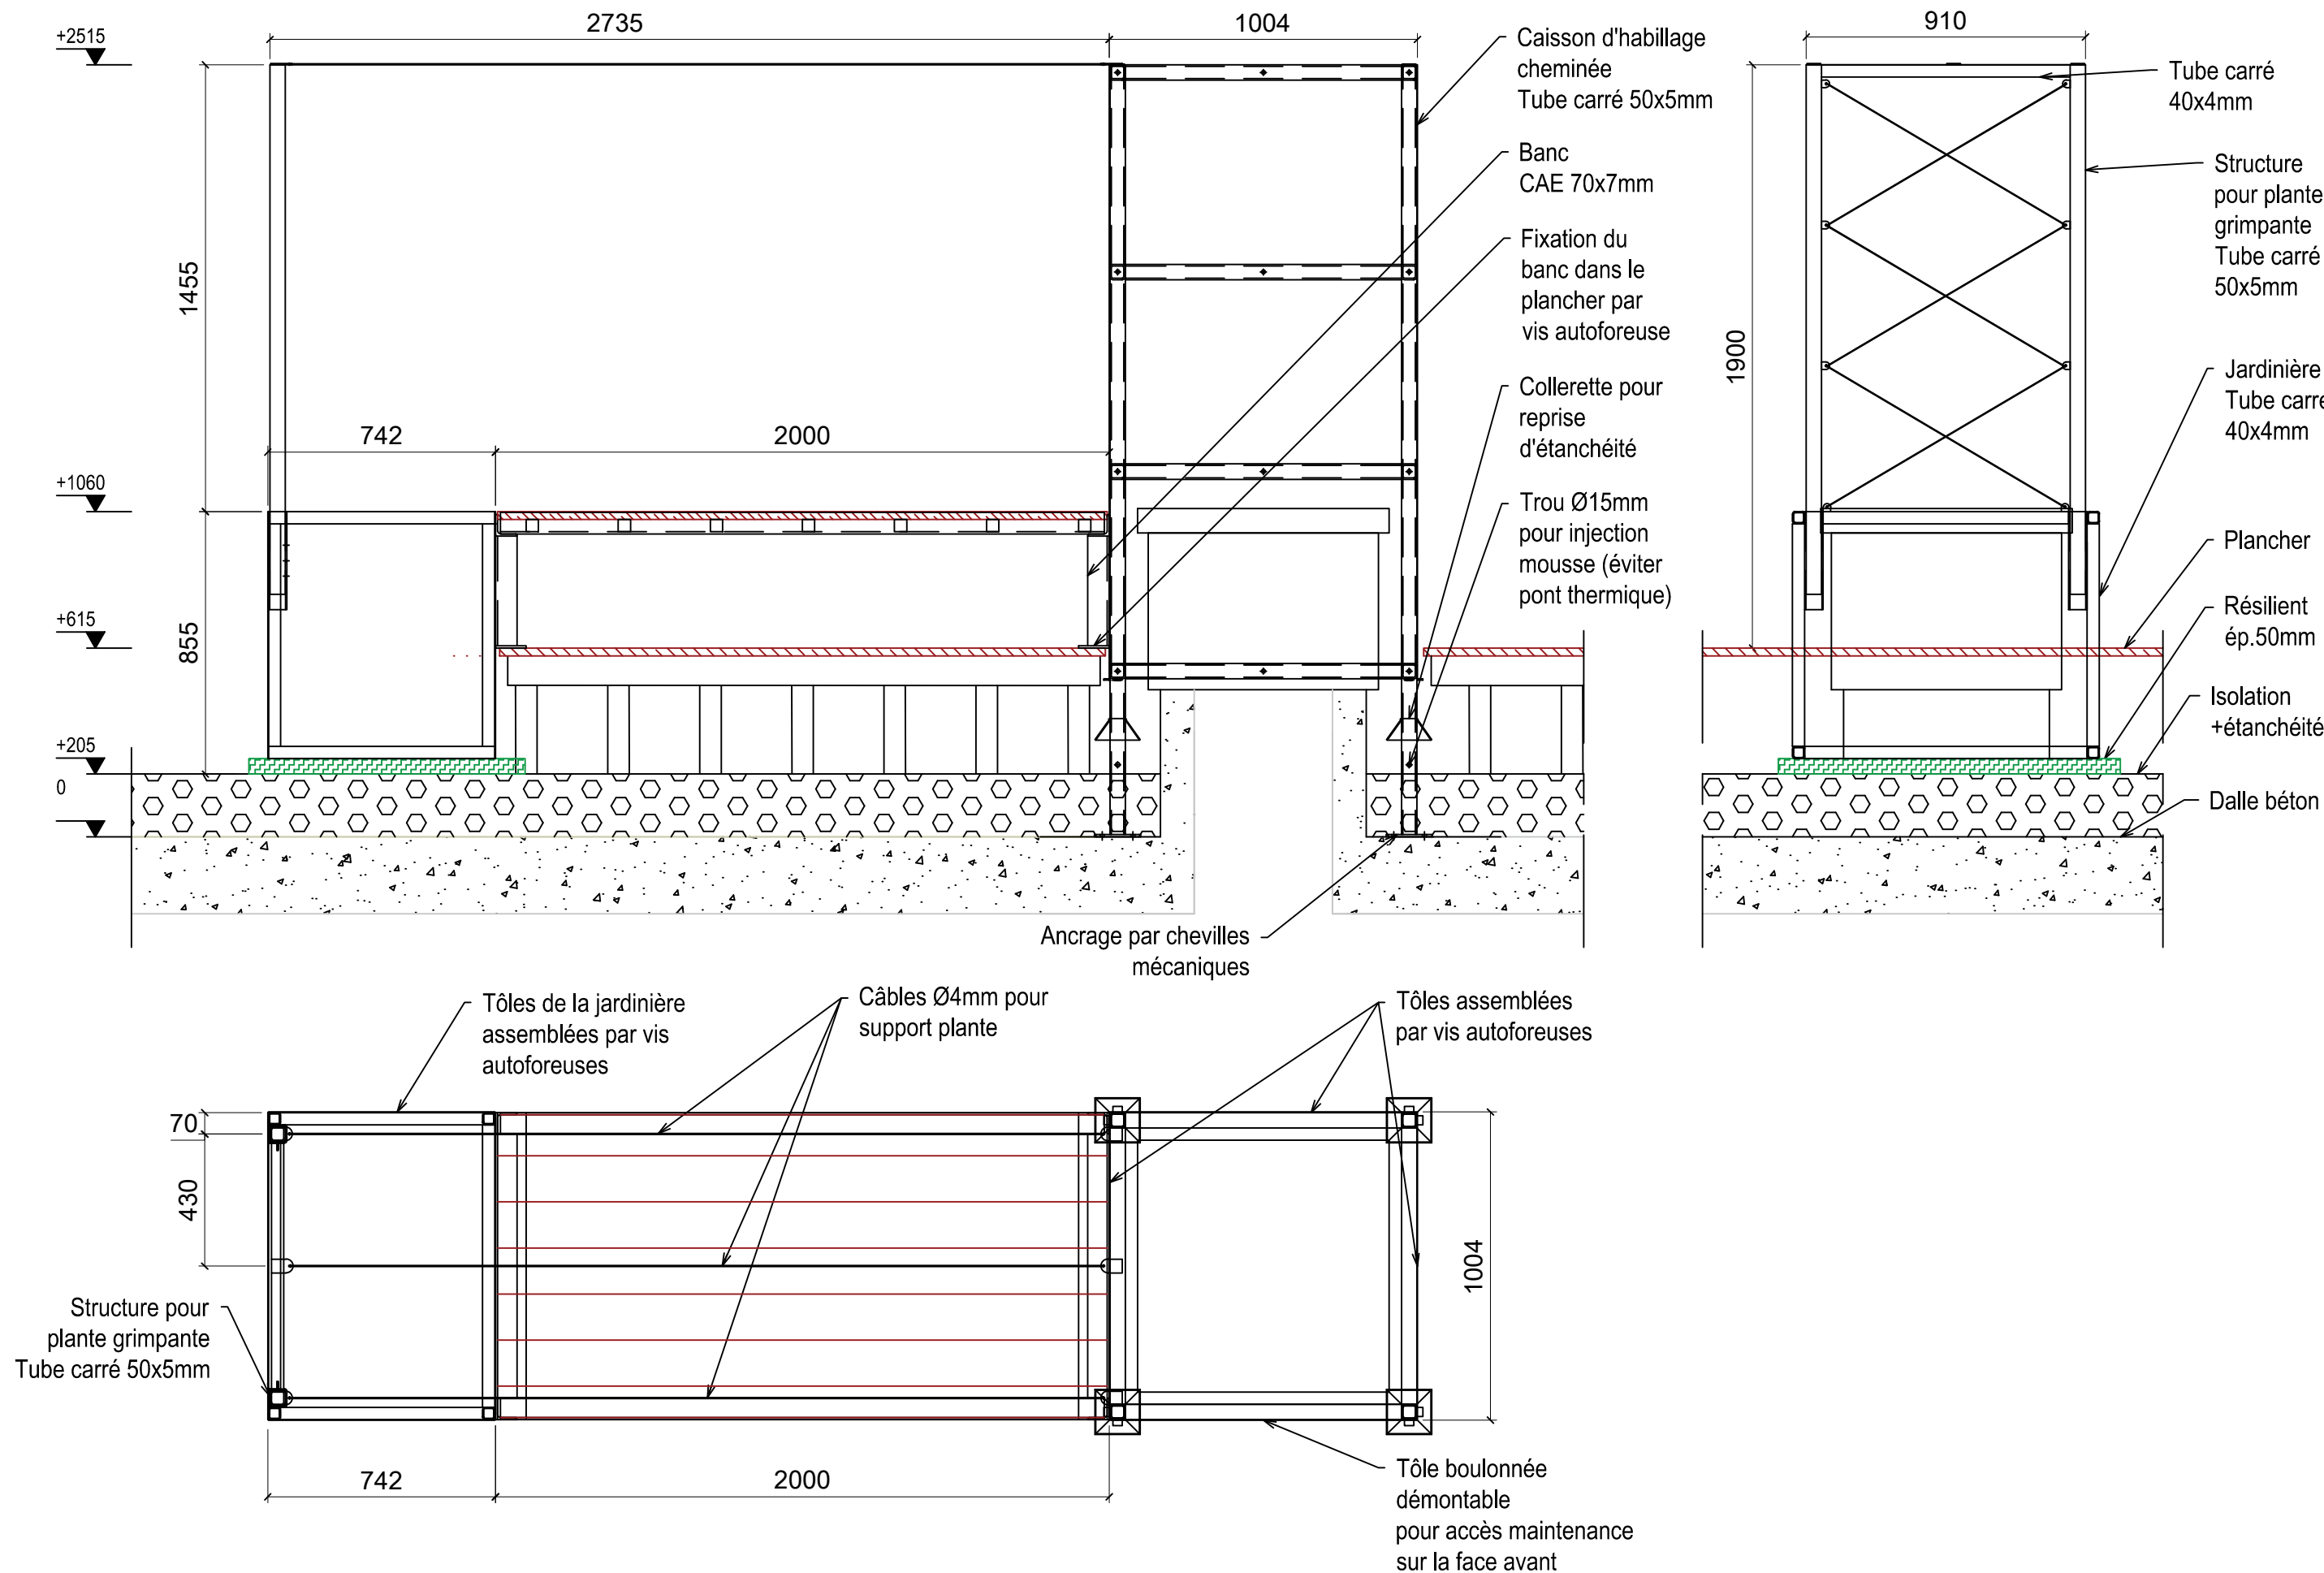

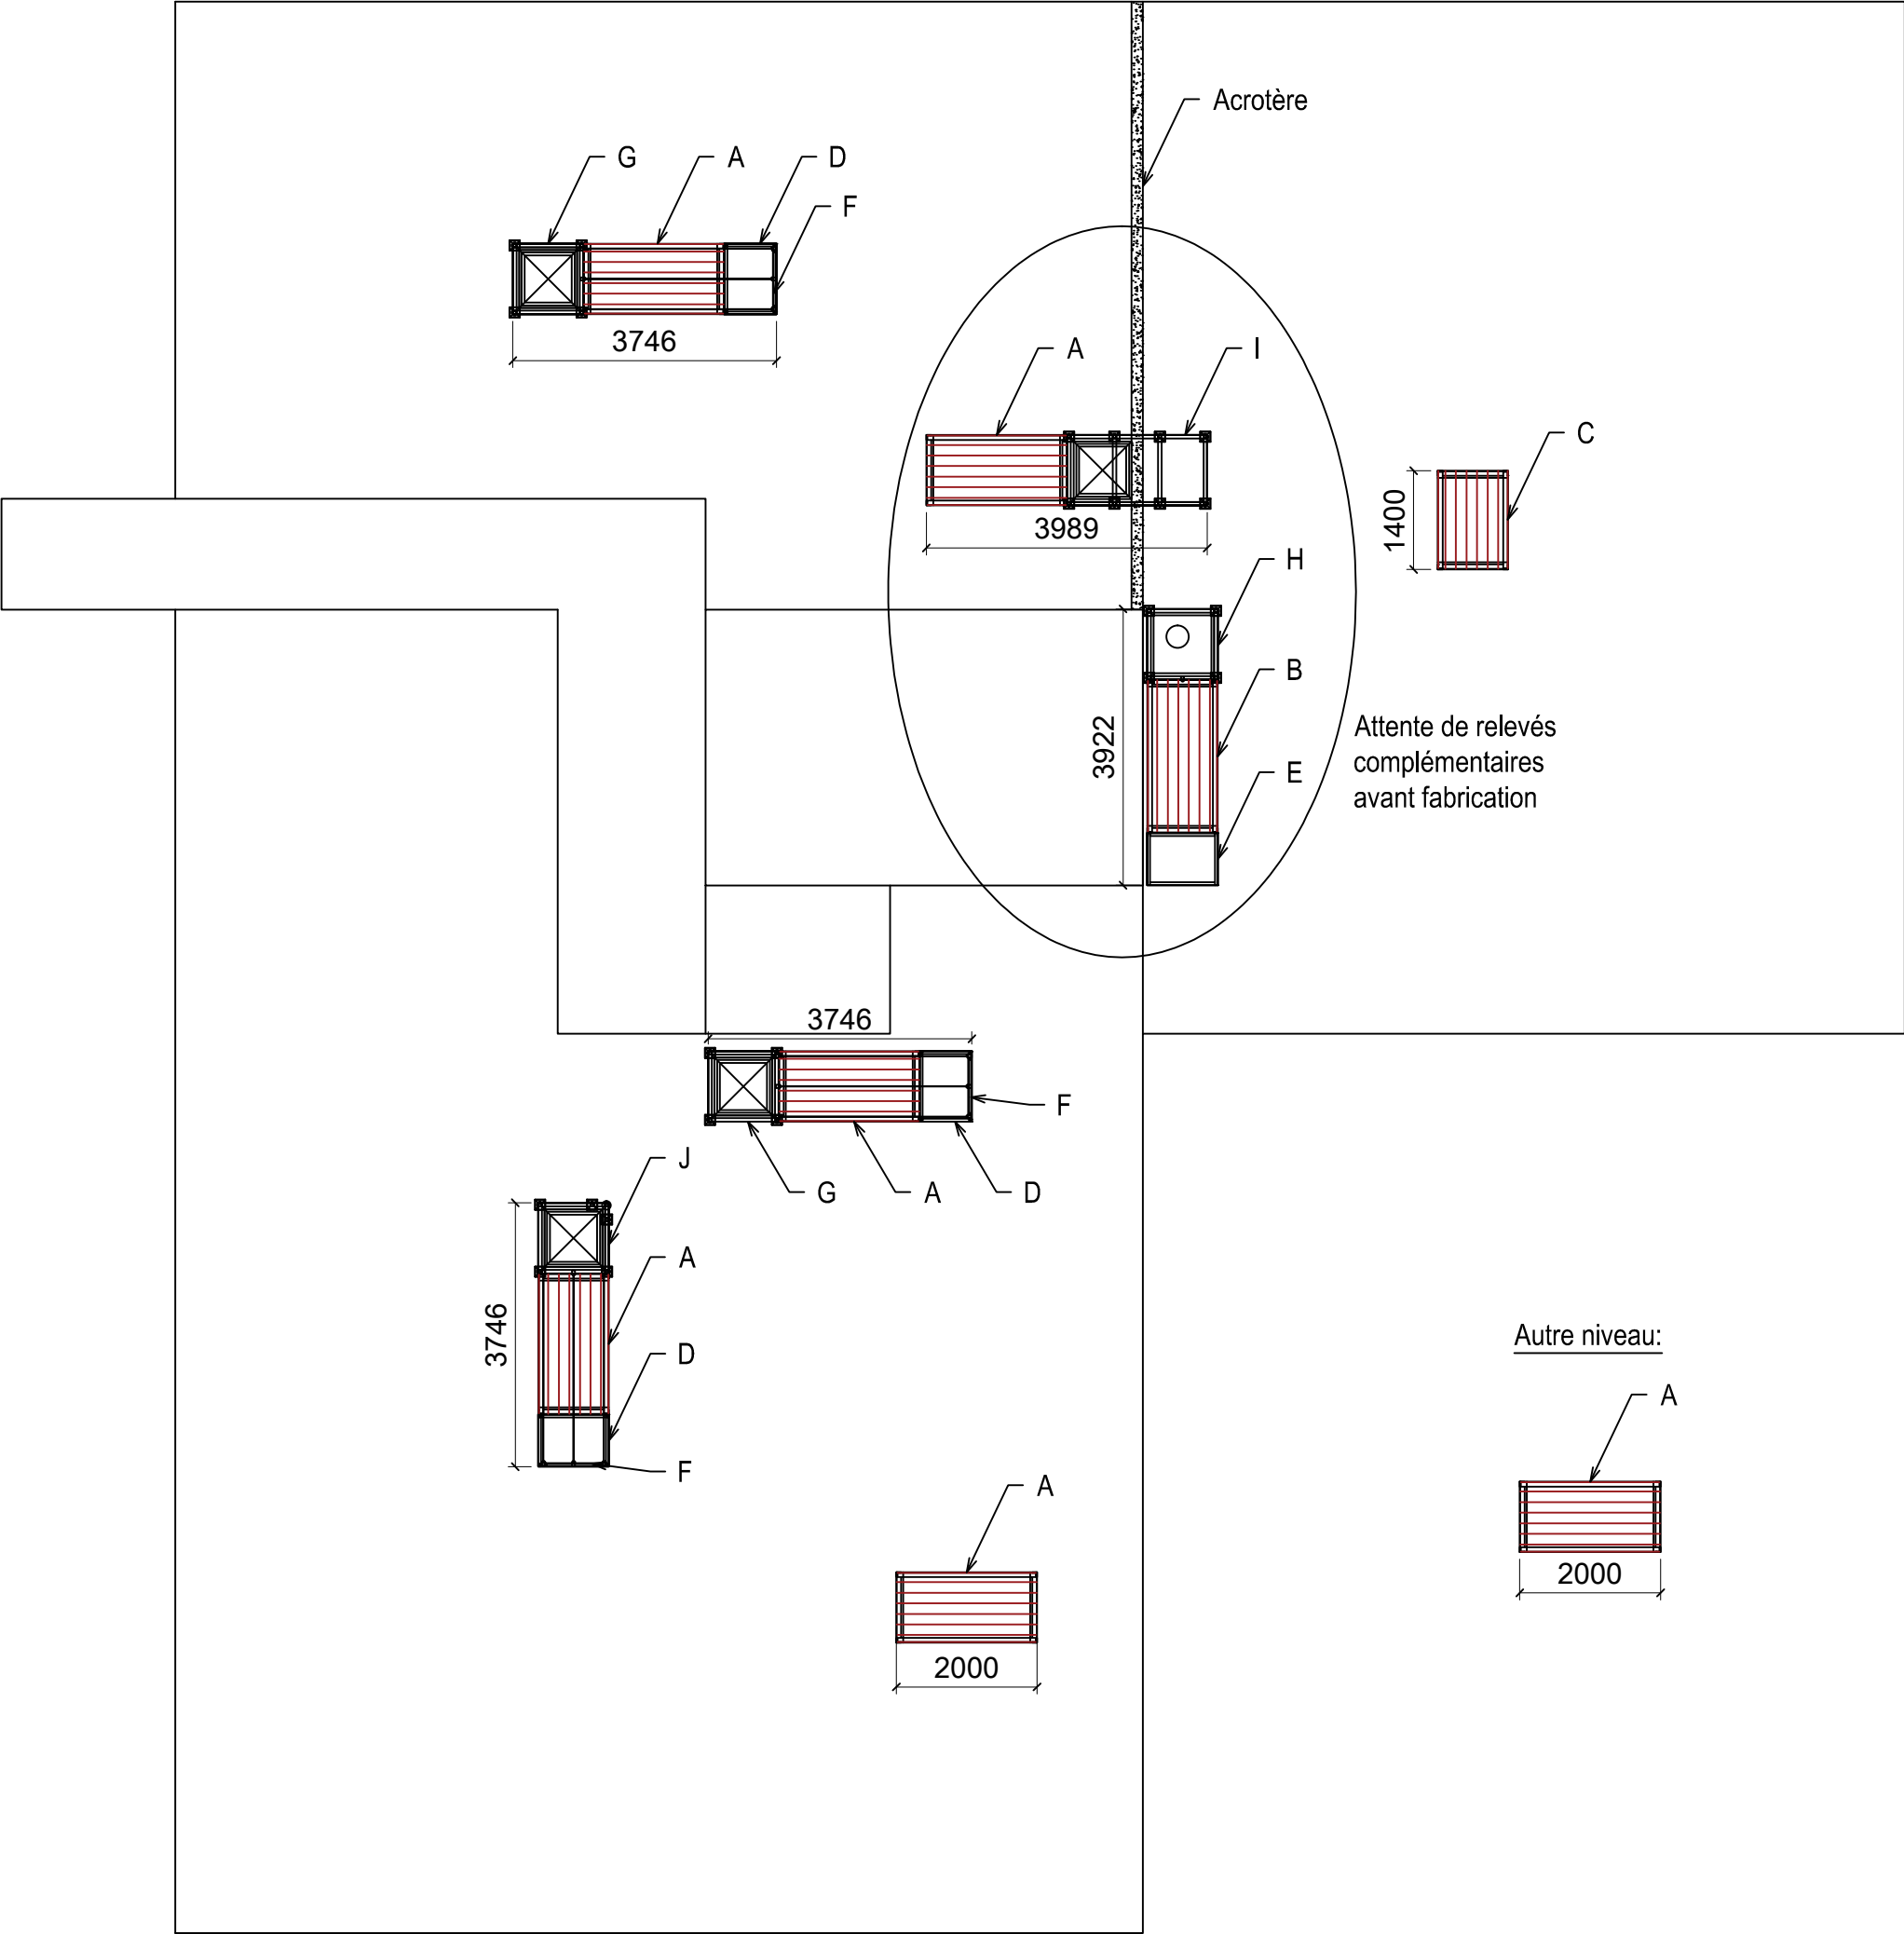

Liste des structures		
Rep.	Libellé	Qté
A	Banc 2m	6
B	Banc env. 2.2m (à valider)	1
C	Banc 1.4m	1
D	Jardinière	3
E	Jardinière 2	1
F	Support plante	3
G	Cheminée gauche	2
H	Cheminée droite (à valider)	1
I	Cheminée double (à valider)	1
J	Cheminée avec poteaux décalés	1
Matériau : Acier S235 / Laquage RAL 9016		

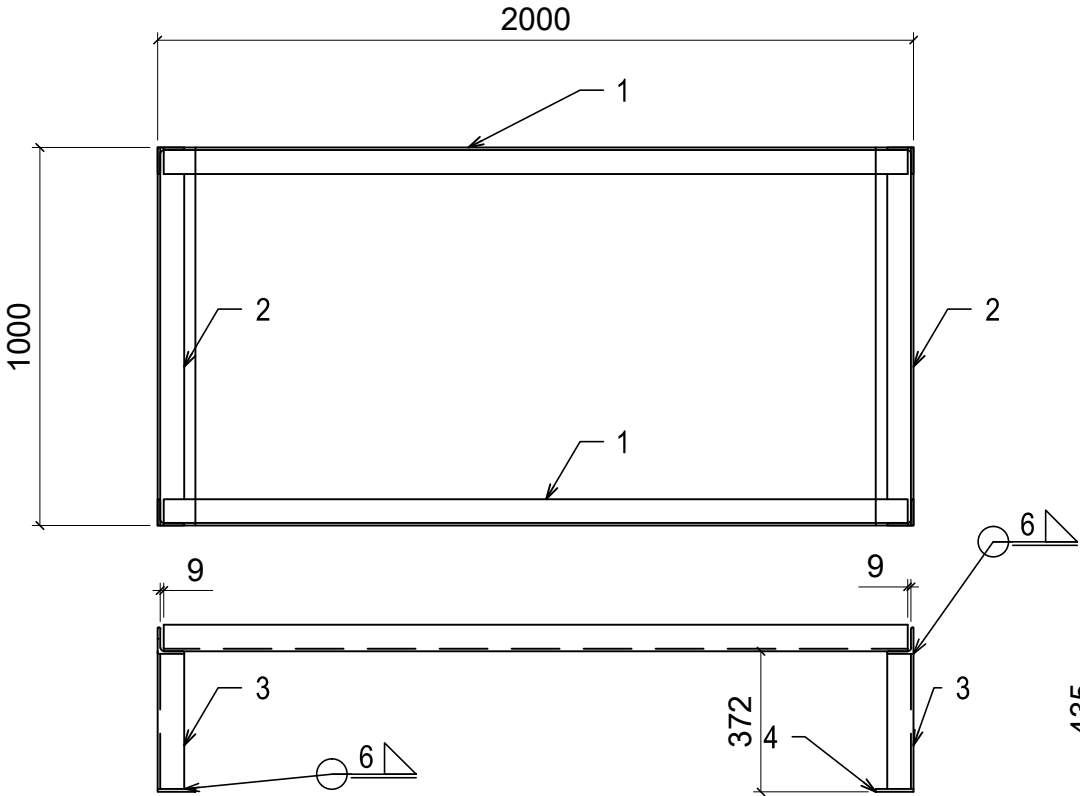

Soudure continue


- Contrôle visuel 100%
- Contrôle dimensionnel 100%

a = 6mm

Liste des pièces		
Rep.	Libellé	Qté
1	Assise longueur	2
2	Assise largeur	2
3	Poteau	4
4	Plat de fixation au sol	2
Matériau : Acier S235 / Laquage RAL 9016		


Ech: 1/20

Repère 1

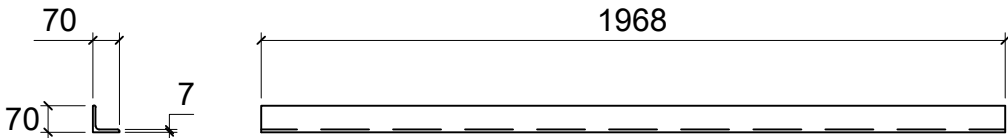


Ech: 1/20

Repère 2

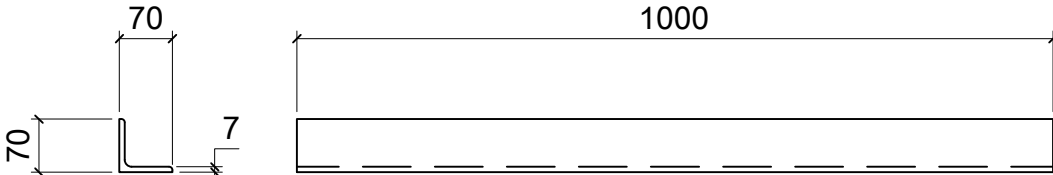


Ech: 1/10

Repère 3

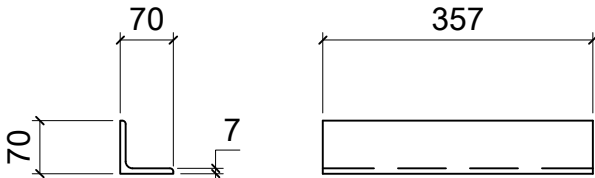

Ech: 1/10

Repère 4

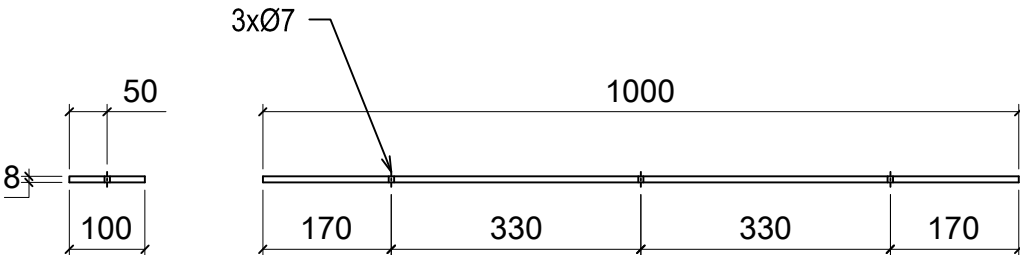


Ech: 1/10

A	19/05/16	Première édition	YC	OM
Ind.	Date	Désignation des modifications	Dessiné par	Contrôle
			FOR 	Ech. : 1
			Unité : mm	Folio : 03/12
			Plan : 16-AF0006-PL3	

Banc longueur 2m - Bâtiment B - Rep. A

PLAN DE FABRICATION

Ce document est la propriété de la société DOPAM'IN. Il ne pourra, sans notre autorisation expresse, être reproduit ou communiqué à des tiers.

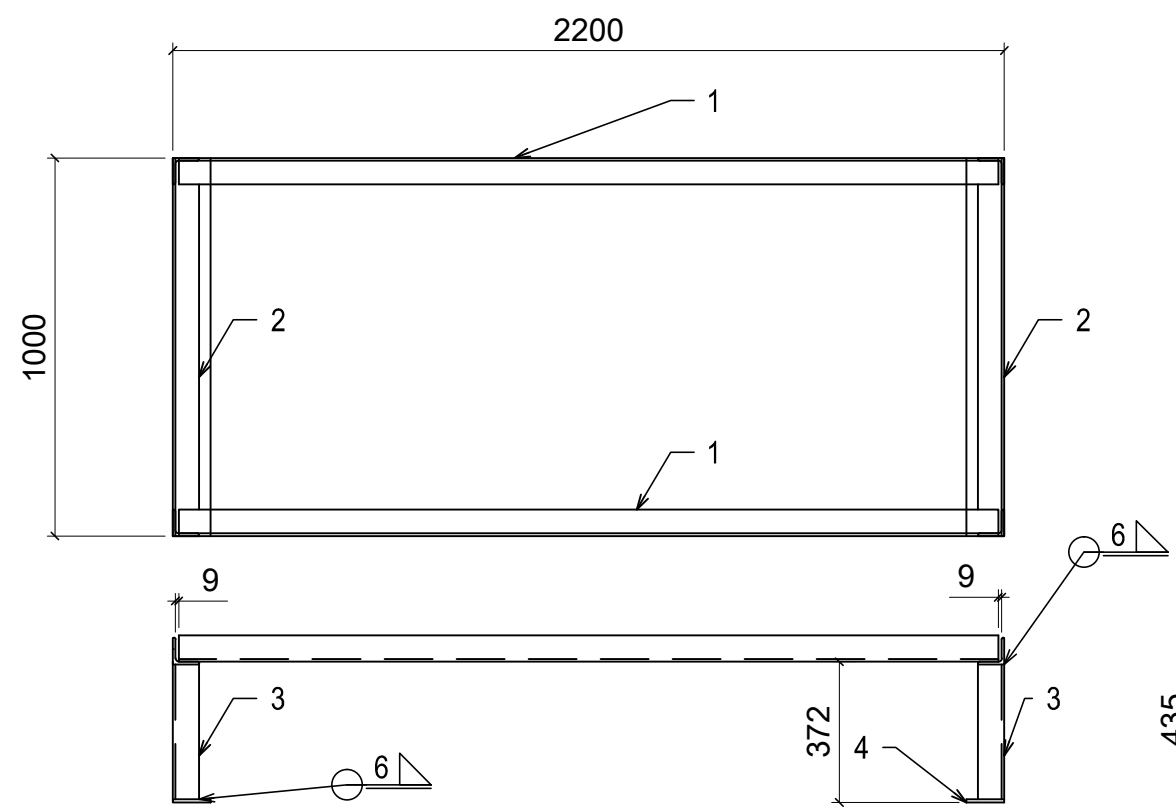

Soudure continue

- Contrôle visuel 100%
- Contrôle dimensionnel 100%

a = 6mm



Liste des pièces		
Rep.	Libellé	Qté
1	Assise longueur	2
2	Assise largeur	2
3	Poteau	4
4	Plat de fixation au sol	2
Matériau : Acier S235 / Laquage RAL 9016		

Ech: 1/20

Repère 1

Repère 2



Ech: 1/10

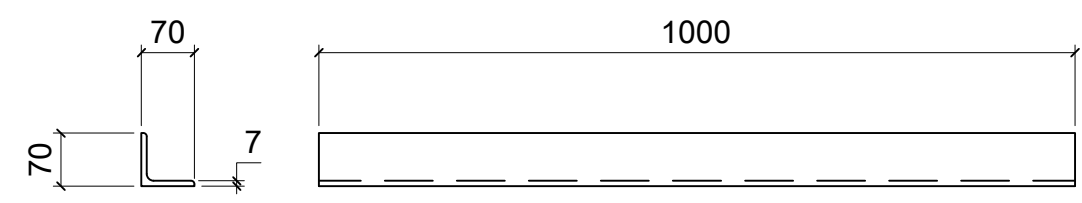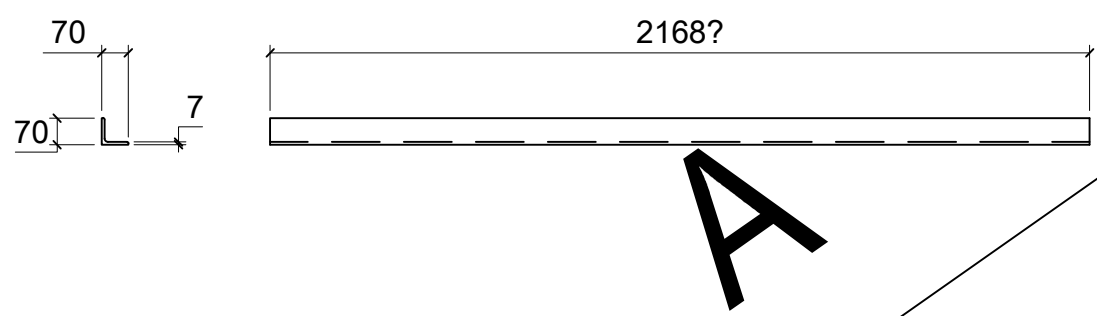


Repère 3

Repère 4

Ech: 1/10

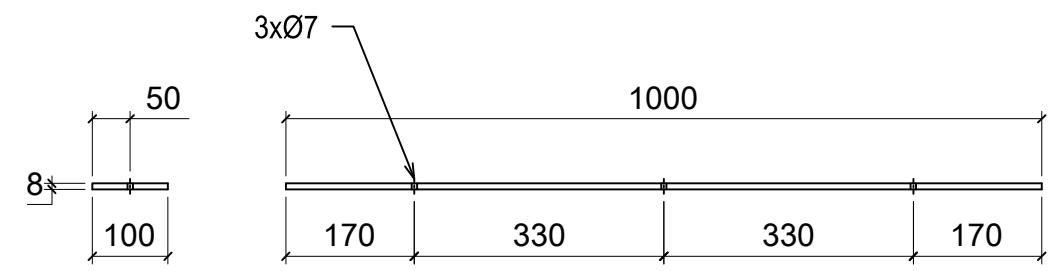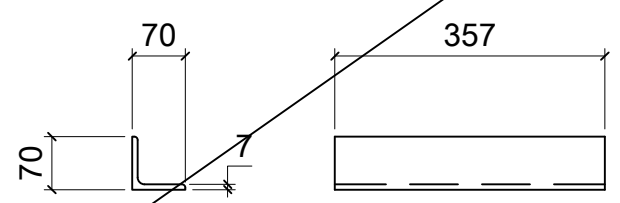

A	19/05/16	Première édition	YC	OM
Ind.	Date	Désignation des modifications	Dessiné par	Contrôle
 Banc longueur 2.2m - Bâtiment B - Rep. B PLAN DE FABRICATION			FOR 	Ech. : 1
			Unité : mm	Folio : 04/12
			Plan : 16-AF0006-PL3	
Ce document est la propriété de la société DOPAM'IN. Il ne pourra, sans notre autorisation expresse, être reproduit ou communiqué à des tiers.				

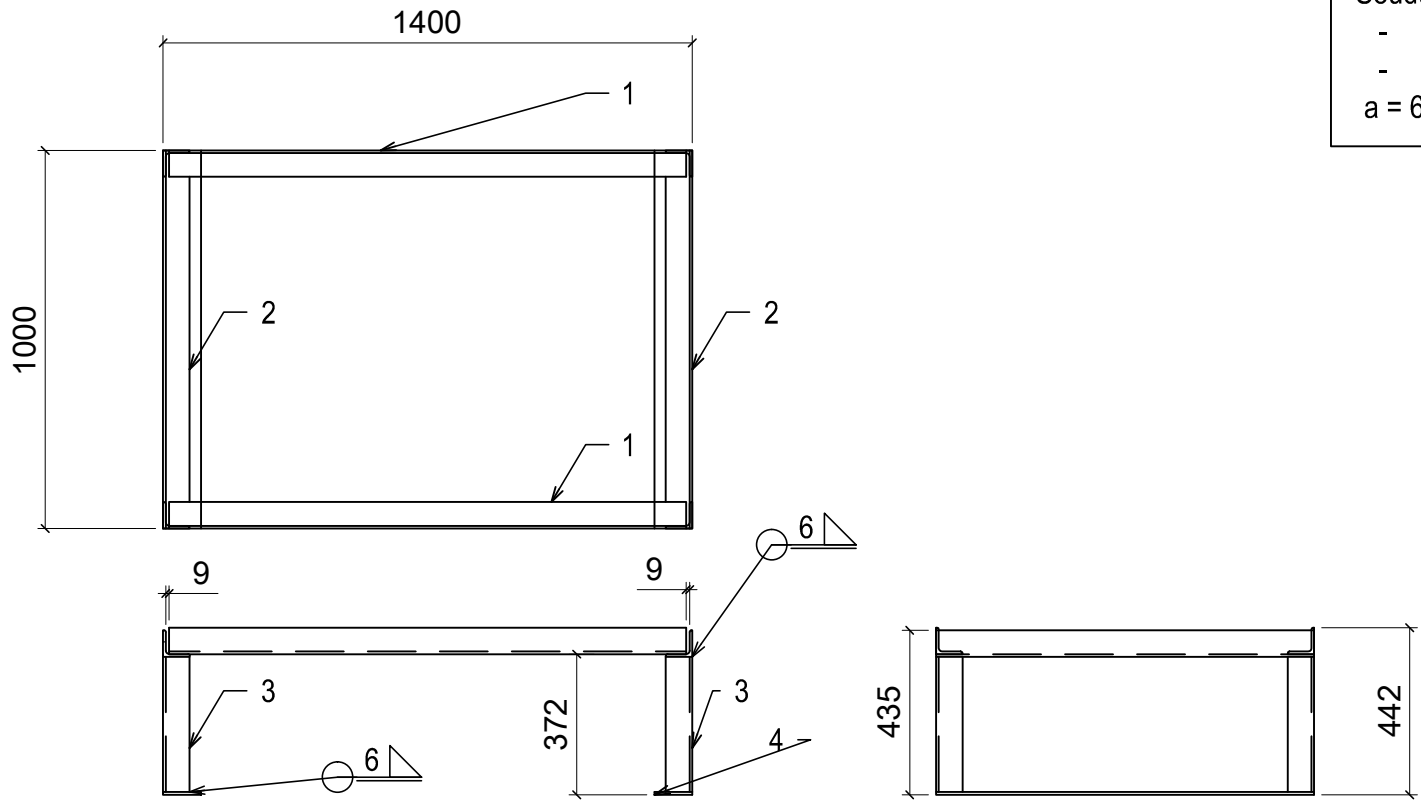

Soudure continue

- Contrôle visuel 100%
- Contrôle dimensionnel 100%

a = 6mm

Liste des pièces		
Rep.	Libellé	Qté
1	Assise longueur	2
2	Assise largeur	2
3	Poteau	4
4	Plat de fixation au sol	2
Matériau : Acier S235 / Laquage RAL 9016		



Ech: 1/20

Repère 1

Ech: 1/20

Repère 2

Ech: 1/10

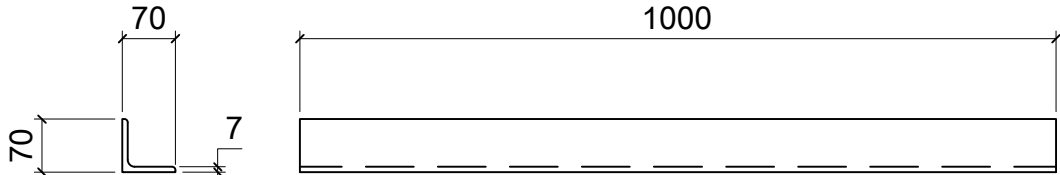
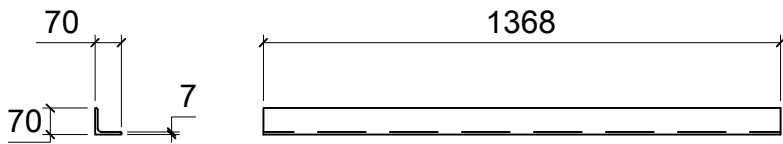


Repère 3

Ech: 1/10

Repère 4

Ech: 1/10

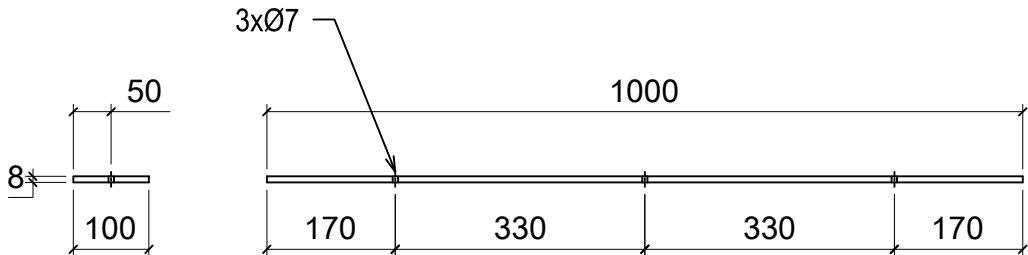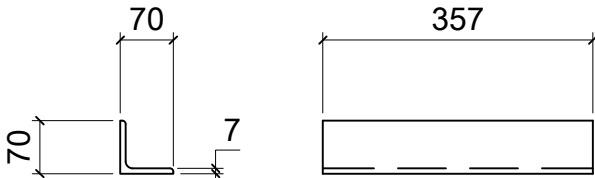

A	19/05/16	Première édition	YC	OM
Ind.	Date	Désignation des modifications	Dessiné par	Contrôle
 DOPAM'IN INGÉNIERIE			FOR 	Ech. : 1
			Unité : mm	Folio : 05/12
			Plan : 16-AF0006-PL3	

Banc longueur 1.4m - Bâtiment B - Rep. C




PLAN DE FABRICATION

Ce document est la propriété de la société DOPAM'IN. Il ne pourra, sans notre autorisation expresse, être reproduit ou communiqué à des tiers.

Soudure continue

- Contrôle visuel 100%
- Contrôle dimensionnel 100%


a = 4mm

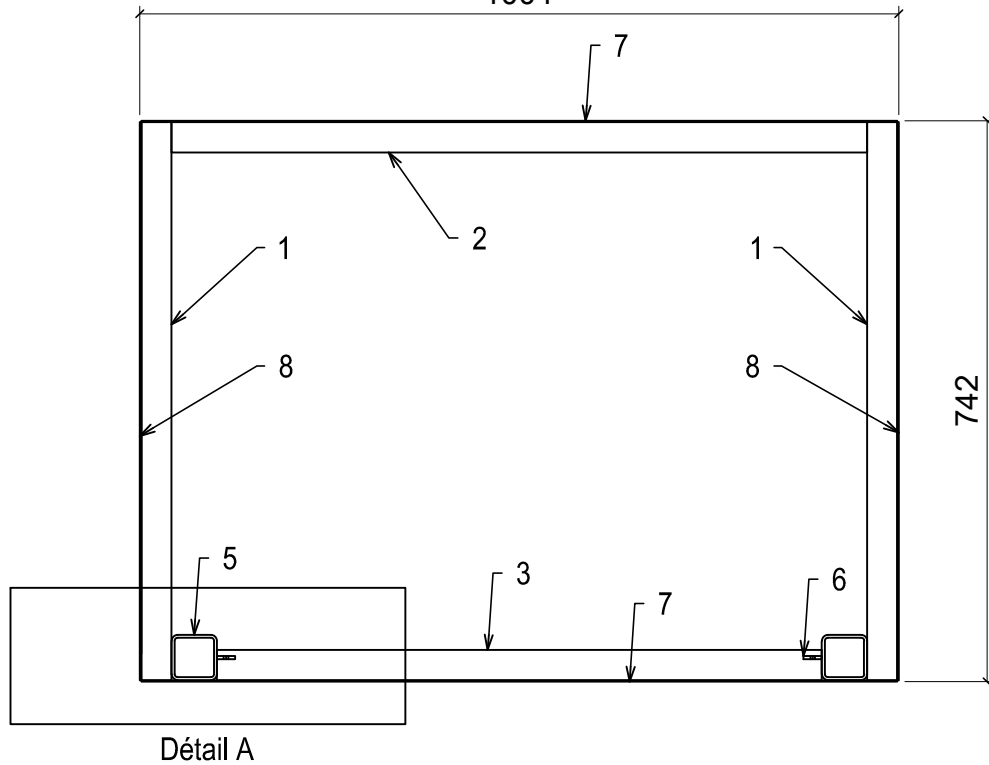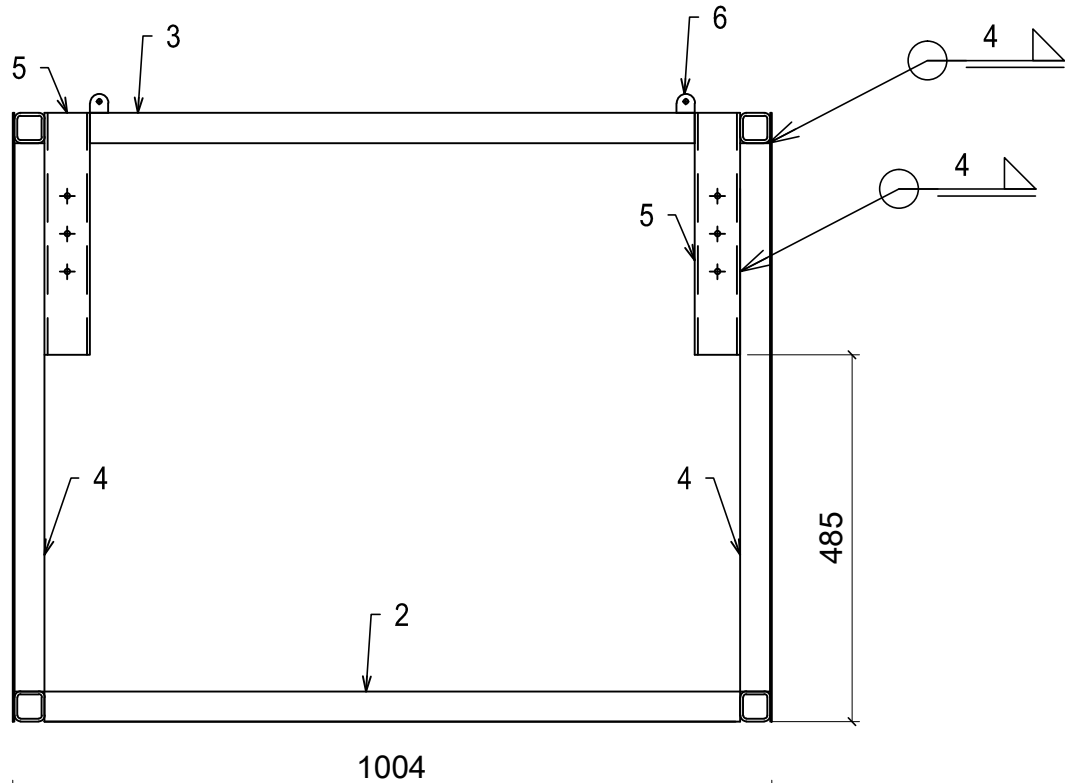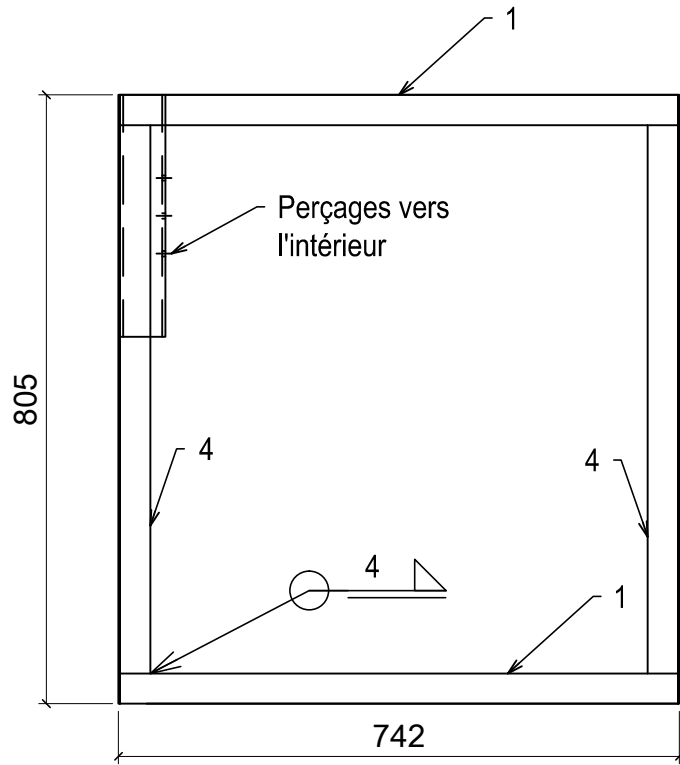




Détail A

Repère 1	Ech: 1/10
TCAR 40x4	738
Repère 2	Ech: 1/10
TCAR 40x4	920
Repère 3	Ech: 1/10
TCAR 40x4	800
Repère 4	Ech: 1/10
TCAR 40x4	725
Repère 5	Ech: 1/10
TCAR 60x4	320
	3xØ7
Repère 6	Ech: 1/2
	24
	15
	25
	12
	4
	Ø6
Repère 7	Ech: 1/40
	1000
	805
Repère 8	Ech: 1/40
	738
	805

Liste des pièces		
Rep.	Libellé	Qté
1	Tube horizontal 1	4
2	Tube horizontal 2	3
3	Tube horizontal 3	1
4	Tube vertical 1	4
5	Tube vertical 2	2
6	Chape	2
7	Tôle 1	2
8	Tôle 2	2
Matériau : Acier S235 / Laquage RAL 9016		

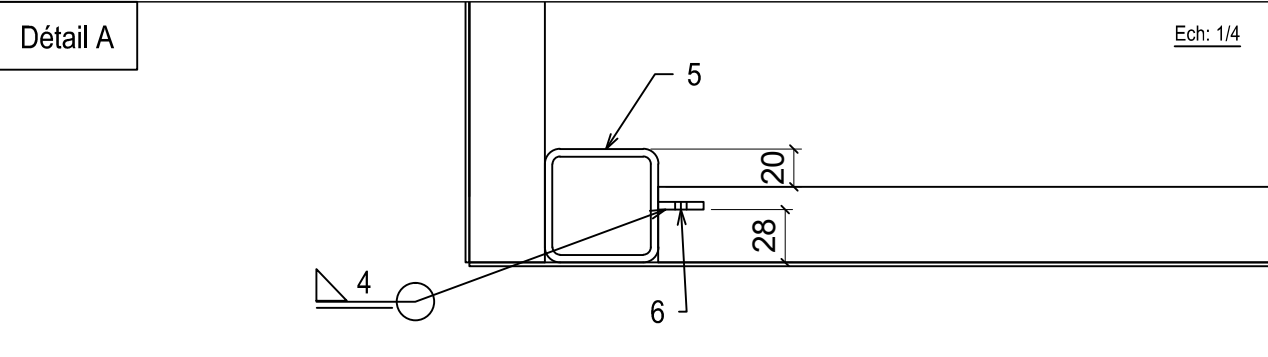

A	19/05/16	Première édition	YC	OM
Ind.	Date	Désignation des modifications	Dessiné par	Contrôle
 DOPAM'IN INGÉNIERIE			FOR	Ech.: 1
			Unité: mm	Folio: 06/12
			Plan: 16-AF0006-PL3	
Ce document est la propriété de la société DOPAM'IN. Il ne pourra, sans notre autorisation expresse, être reproduit ou communiqué à des tiers.				

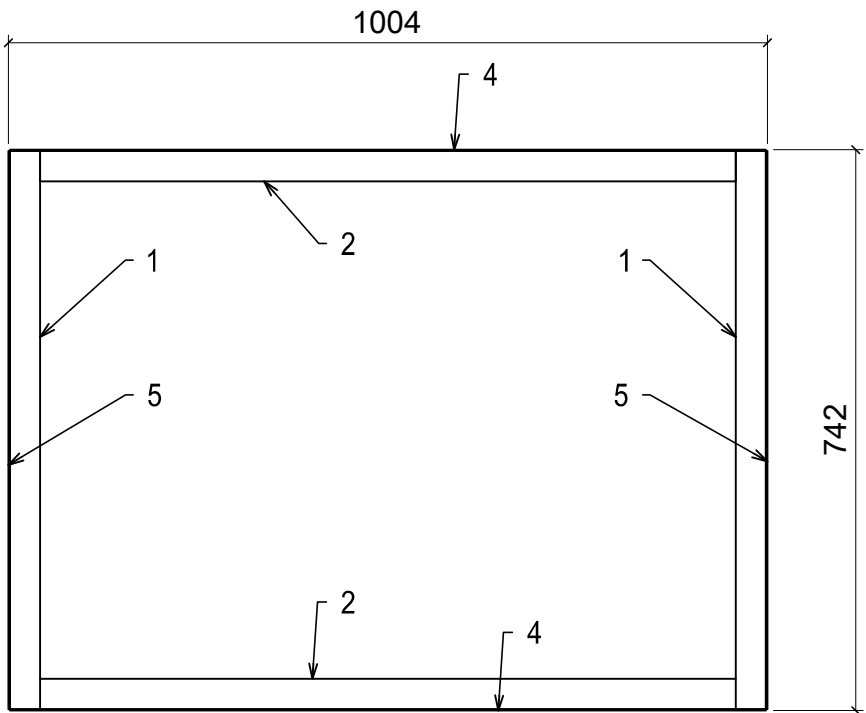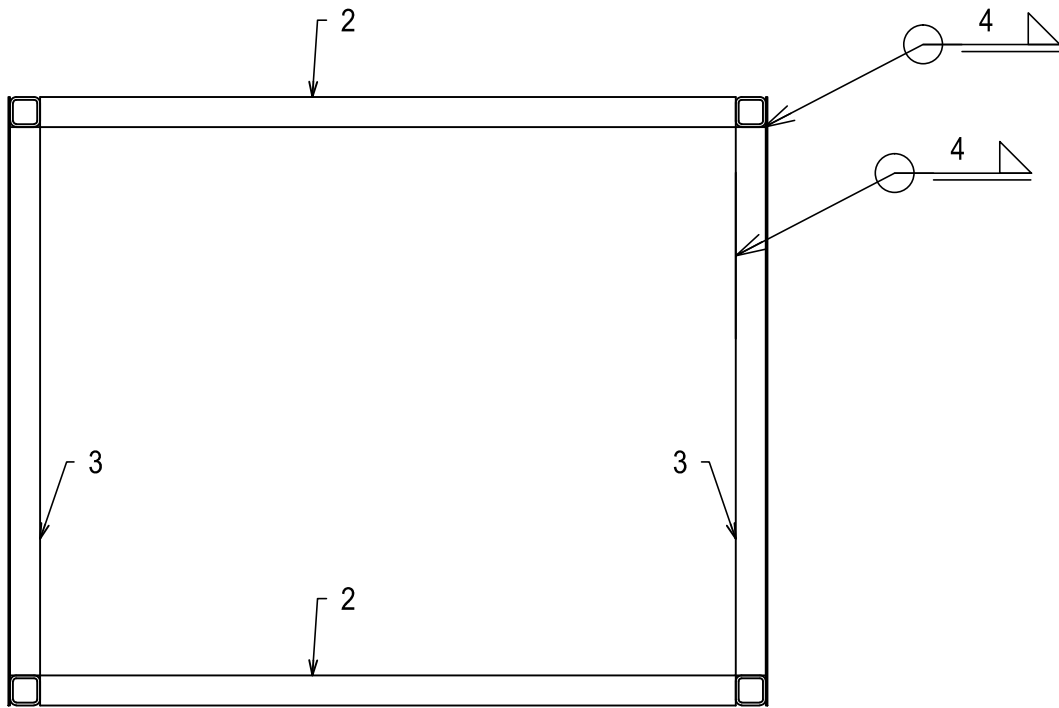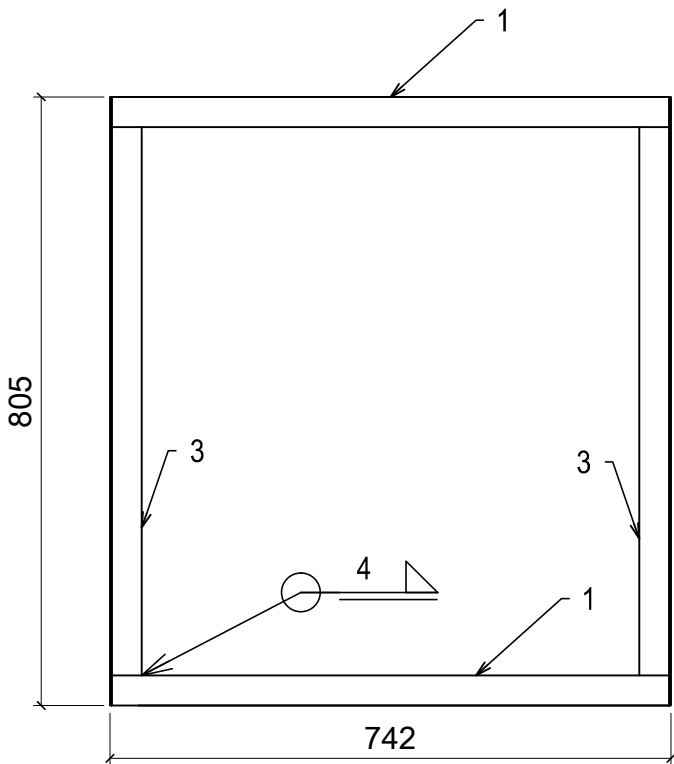

Liste des pièces

Rep.	Libellé	Qté
1	Tube horizontal 1	4
2	Tube horizontal 2	4
3	Tube vertical	4
4	Tôle 1	2
5	Tôle 2	2

Matériau : Acier S235 / Laquage RAL 9016

Repère 1

Ech: 1/10

TCAR 40x4

738

Repère 2

Ech: 1/10

TCAR 40x4

920

Repère 3

Ech: 1/10

TCAR 40x4

725

Repère 4

Ech: 1/40

1000

805

Repère 5

Ech: 1/40

738

805

Soudure continue

- Contrôle visuel 100%
 - Contrôle dimensionnel 100%
- a = 4mm



Jardinière 2 bâtiment B - Rep. E
PLAN DE FABRICATION

Ce document est la propriété de la société DOPAM'IN. Il ne pourra, sans notre autorisation expresse, être reproduit ou communiqué à des tiers.

FOR

Unité : mm

Plan : 16-AF0006-PL3

Ech. : 1

Folio : 07/12

YC

Dessiné par

OM

Contrôle

A


19/05/16

Première édition


Ind.

Date







Désignation des modifications

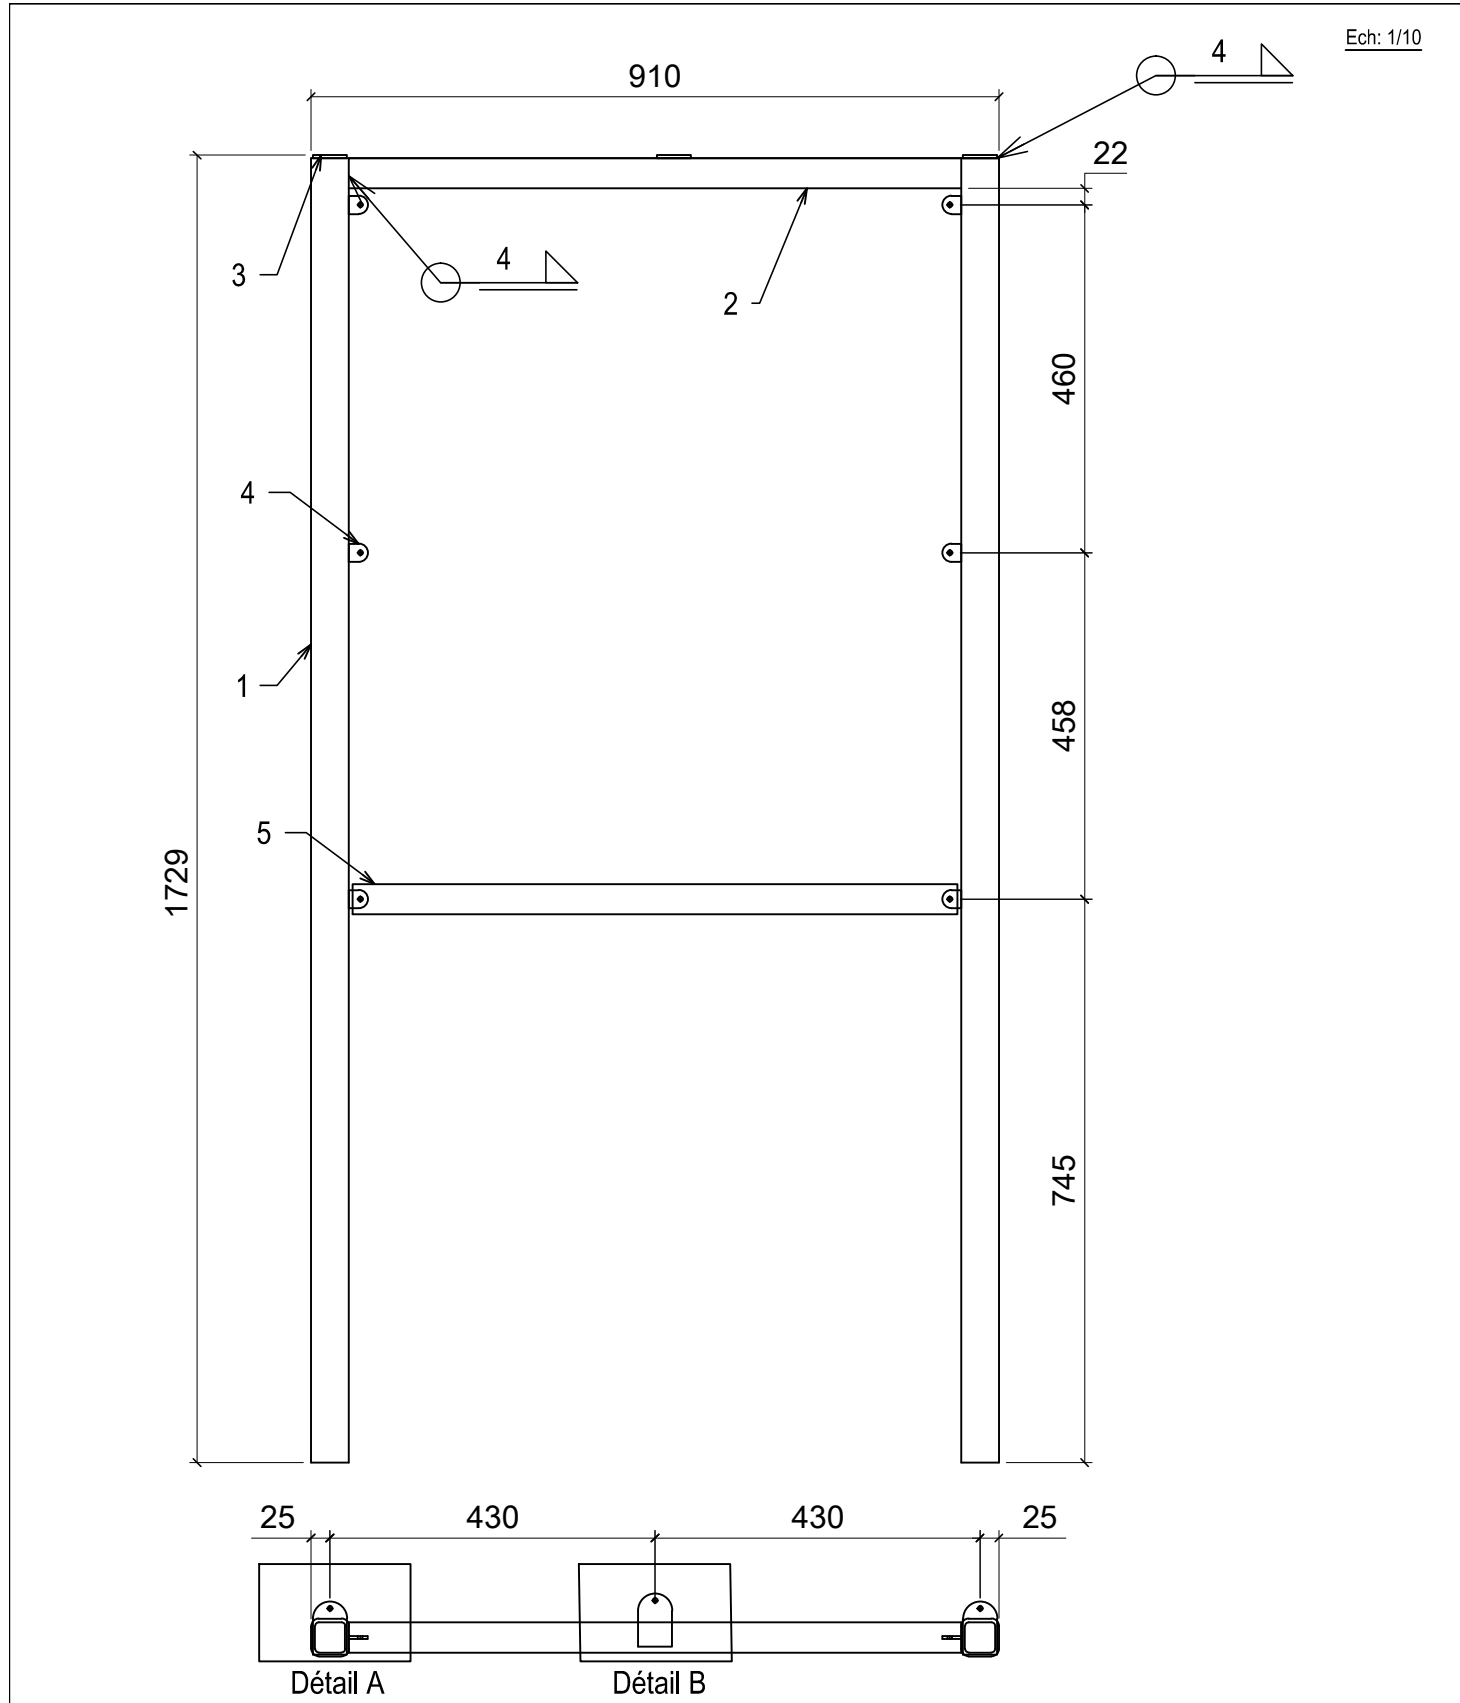



Détail A

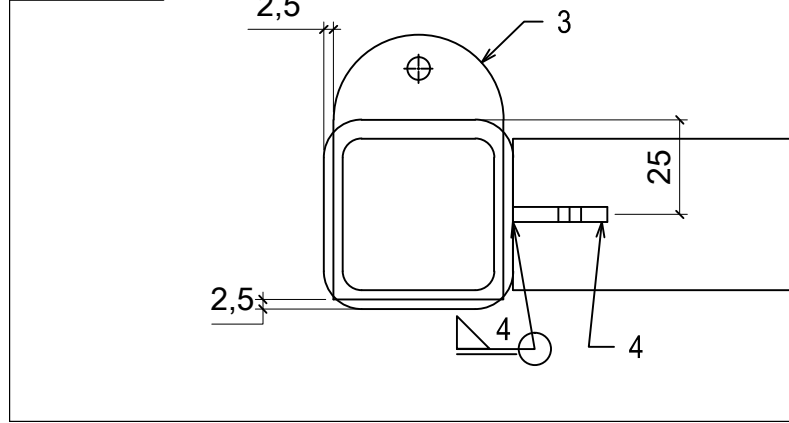

Détail B

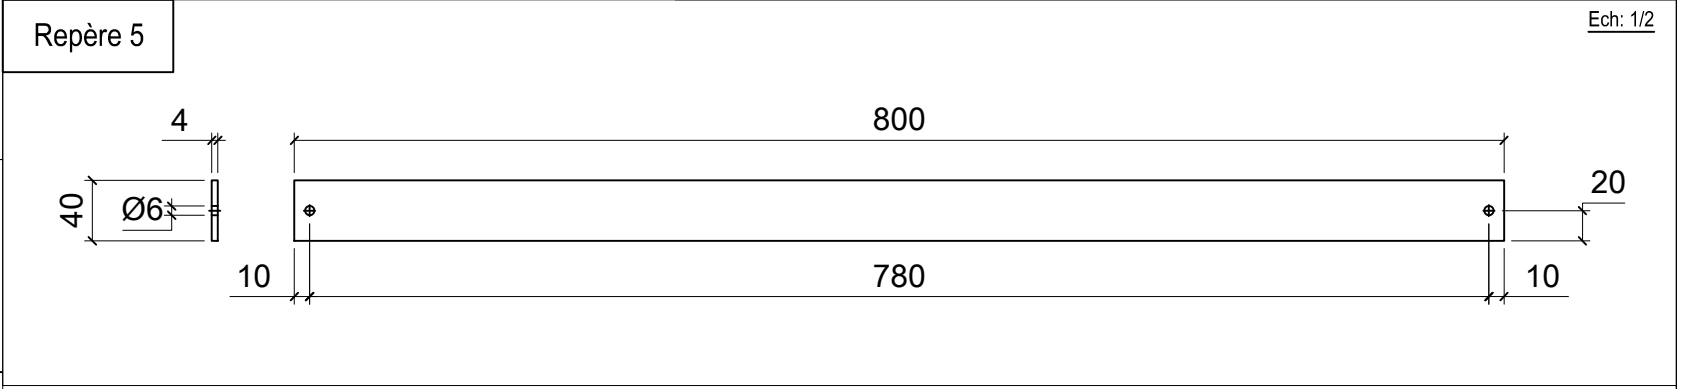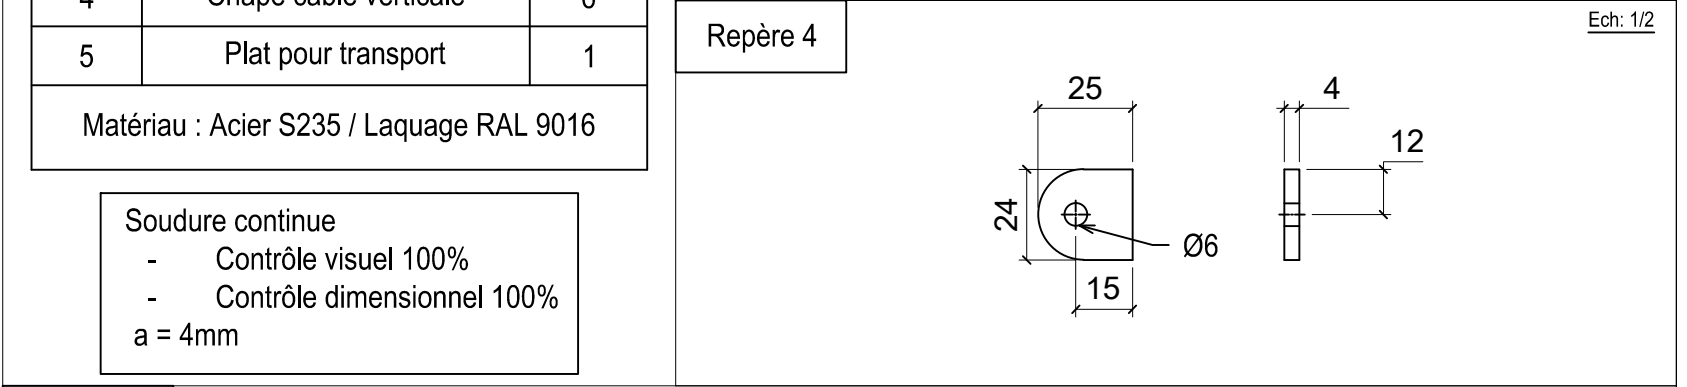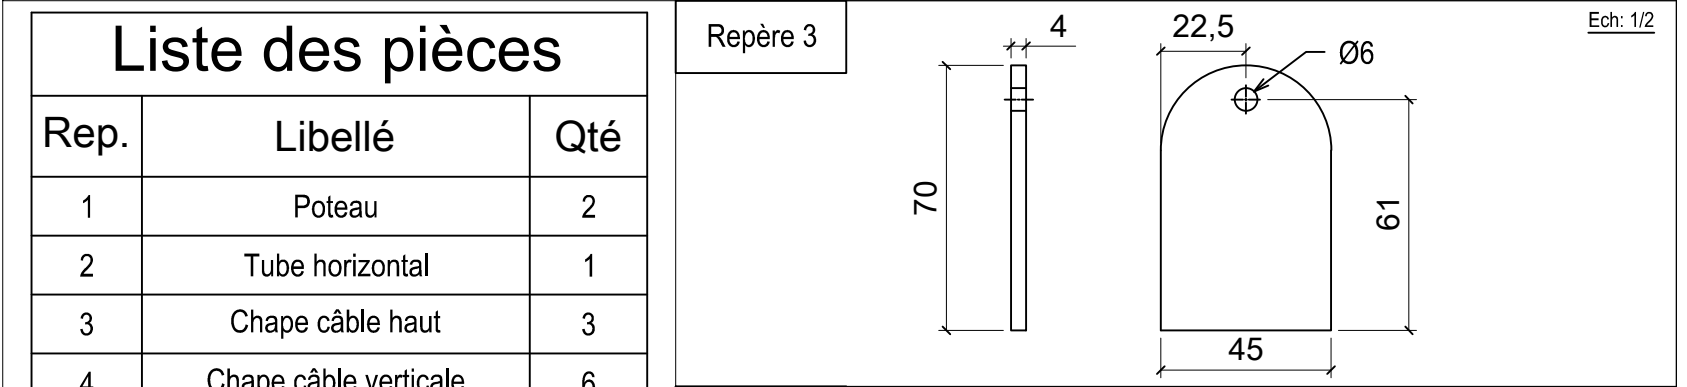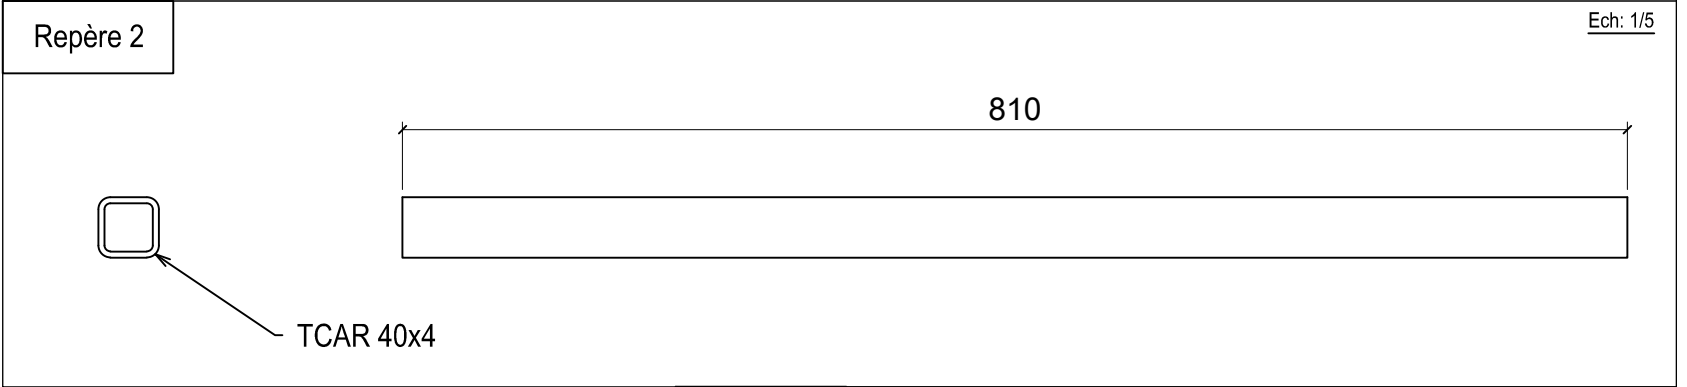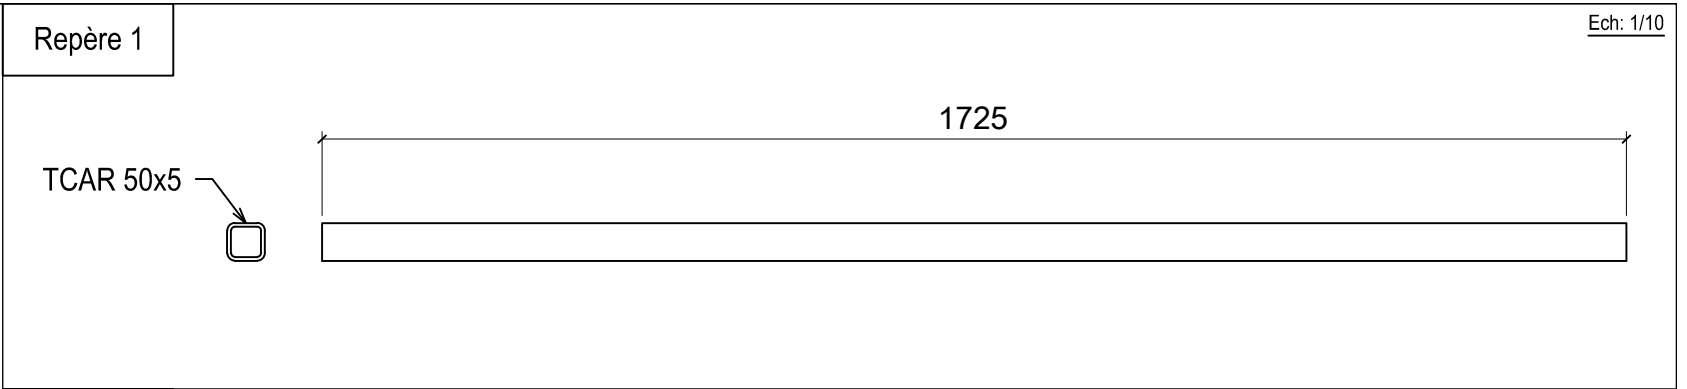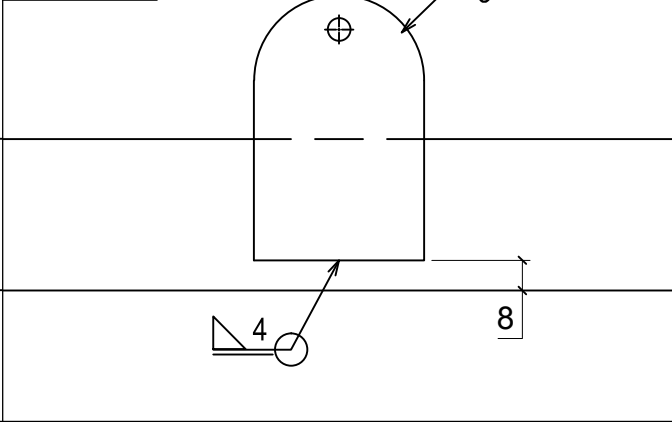


A	19/05/16	Première édition	YC	OM
Ind.	Date	Désignation des modifications	Dessiné par	Contrôle
			Support plante bâtiment B - Rep. F PLAN DE FABRICATION	
Ce document est la propriété de la société DOPAM'IN. Il ne pourra, sans notre autorisation expresse, être reproduit ou communiqué à des tiers.			FOR 	Ech.: 1
			Unité: mm	Folio: 08/12
			Plan: 16-AF0006-PL3	

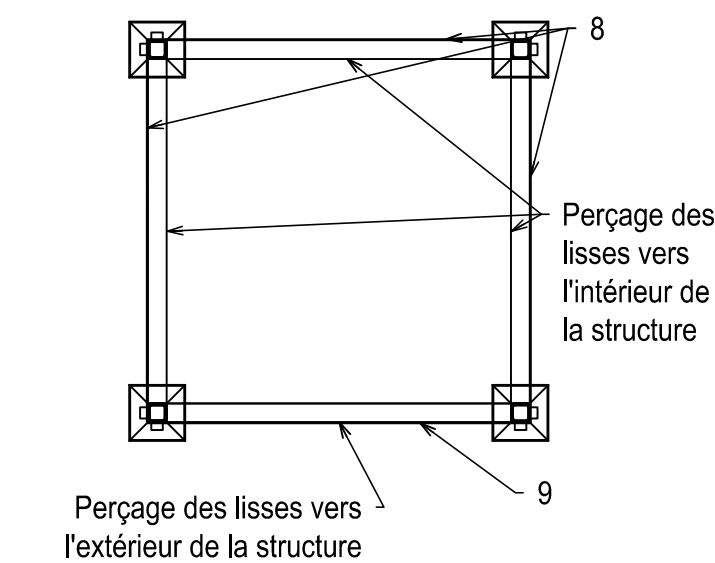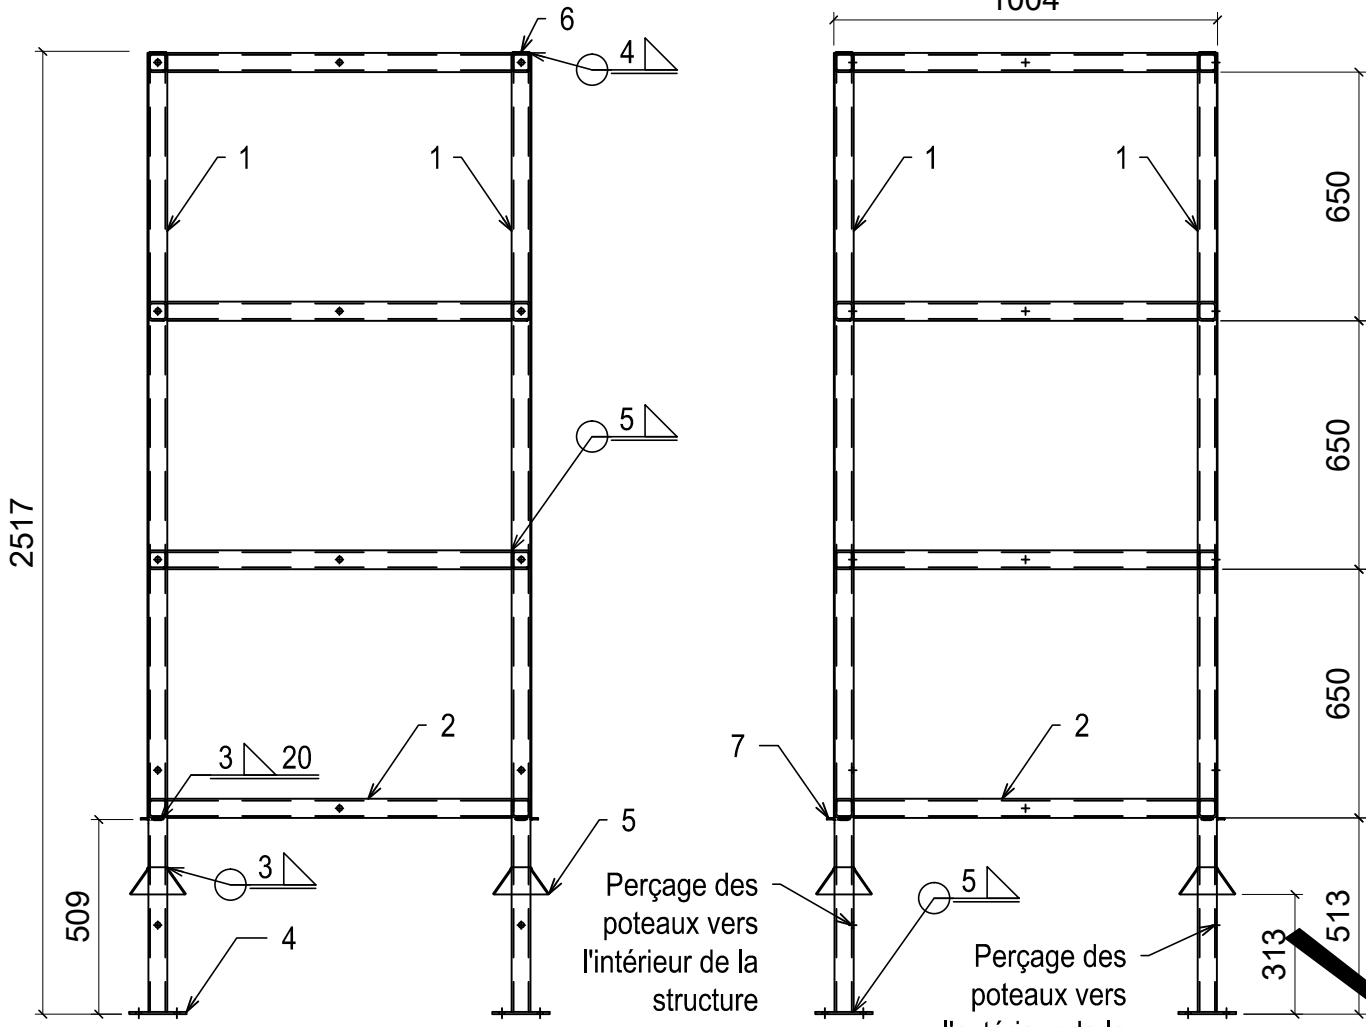

Soudure continue
- Contrôle visuel 100%
- Contrôle dimensionnel 100%
a = 5mm













Liste des pièces		
Rep.	Libellé	Qté
1	Poteau	4
2	Lisse	16
3	Chape	0
4	Platine	4
5	Collerette	4
6	Bouchon	4
7	Plat	8
8	Tôle assemblée par autoforeuses	3
9	Tôle boulonnée	1
Matériau : Acier S235 / Laquage RAL 9016		

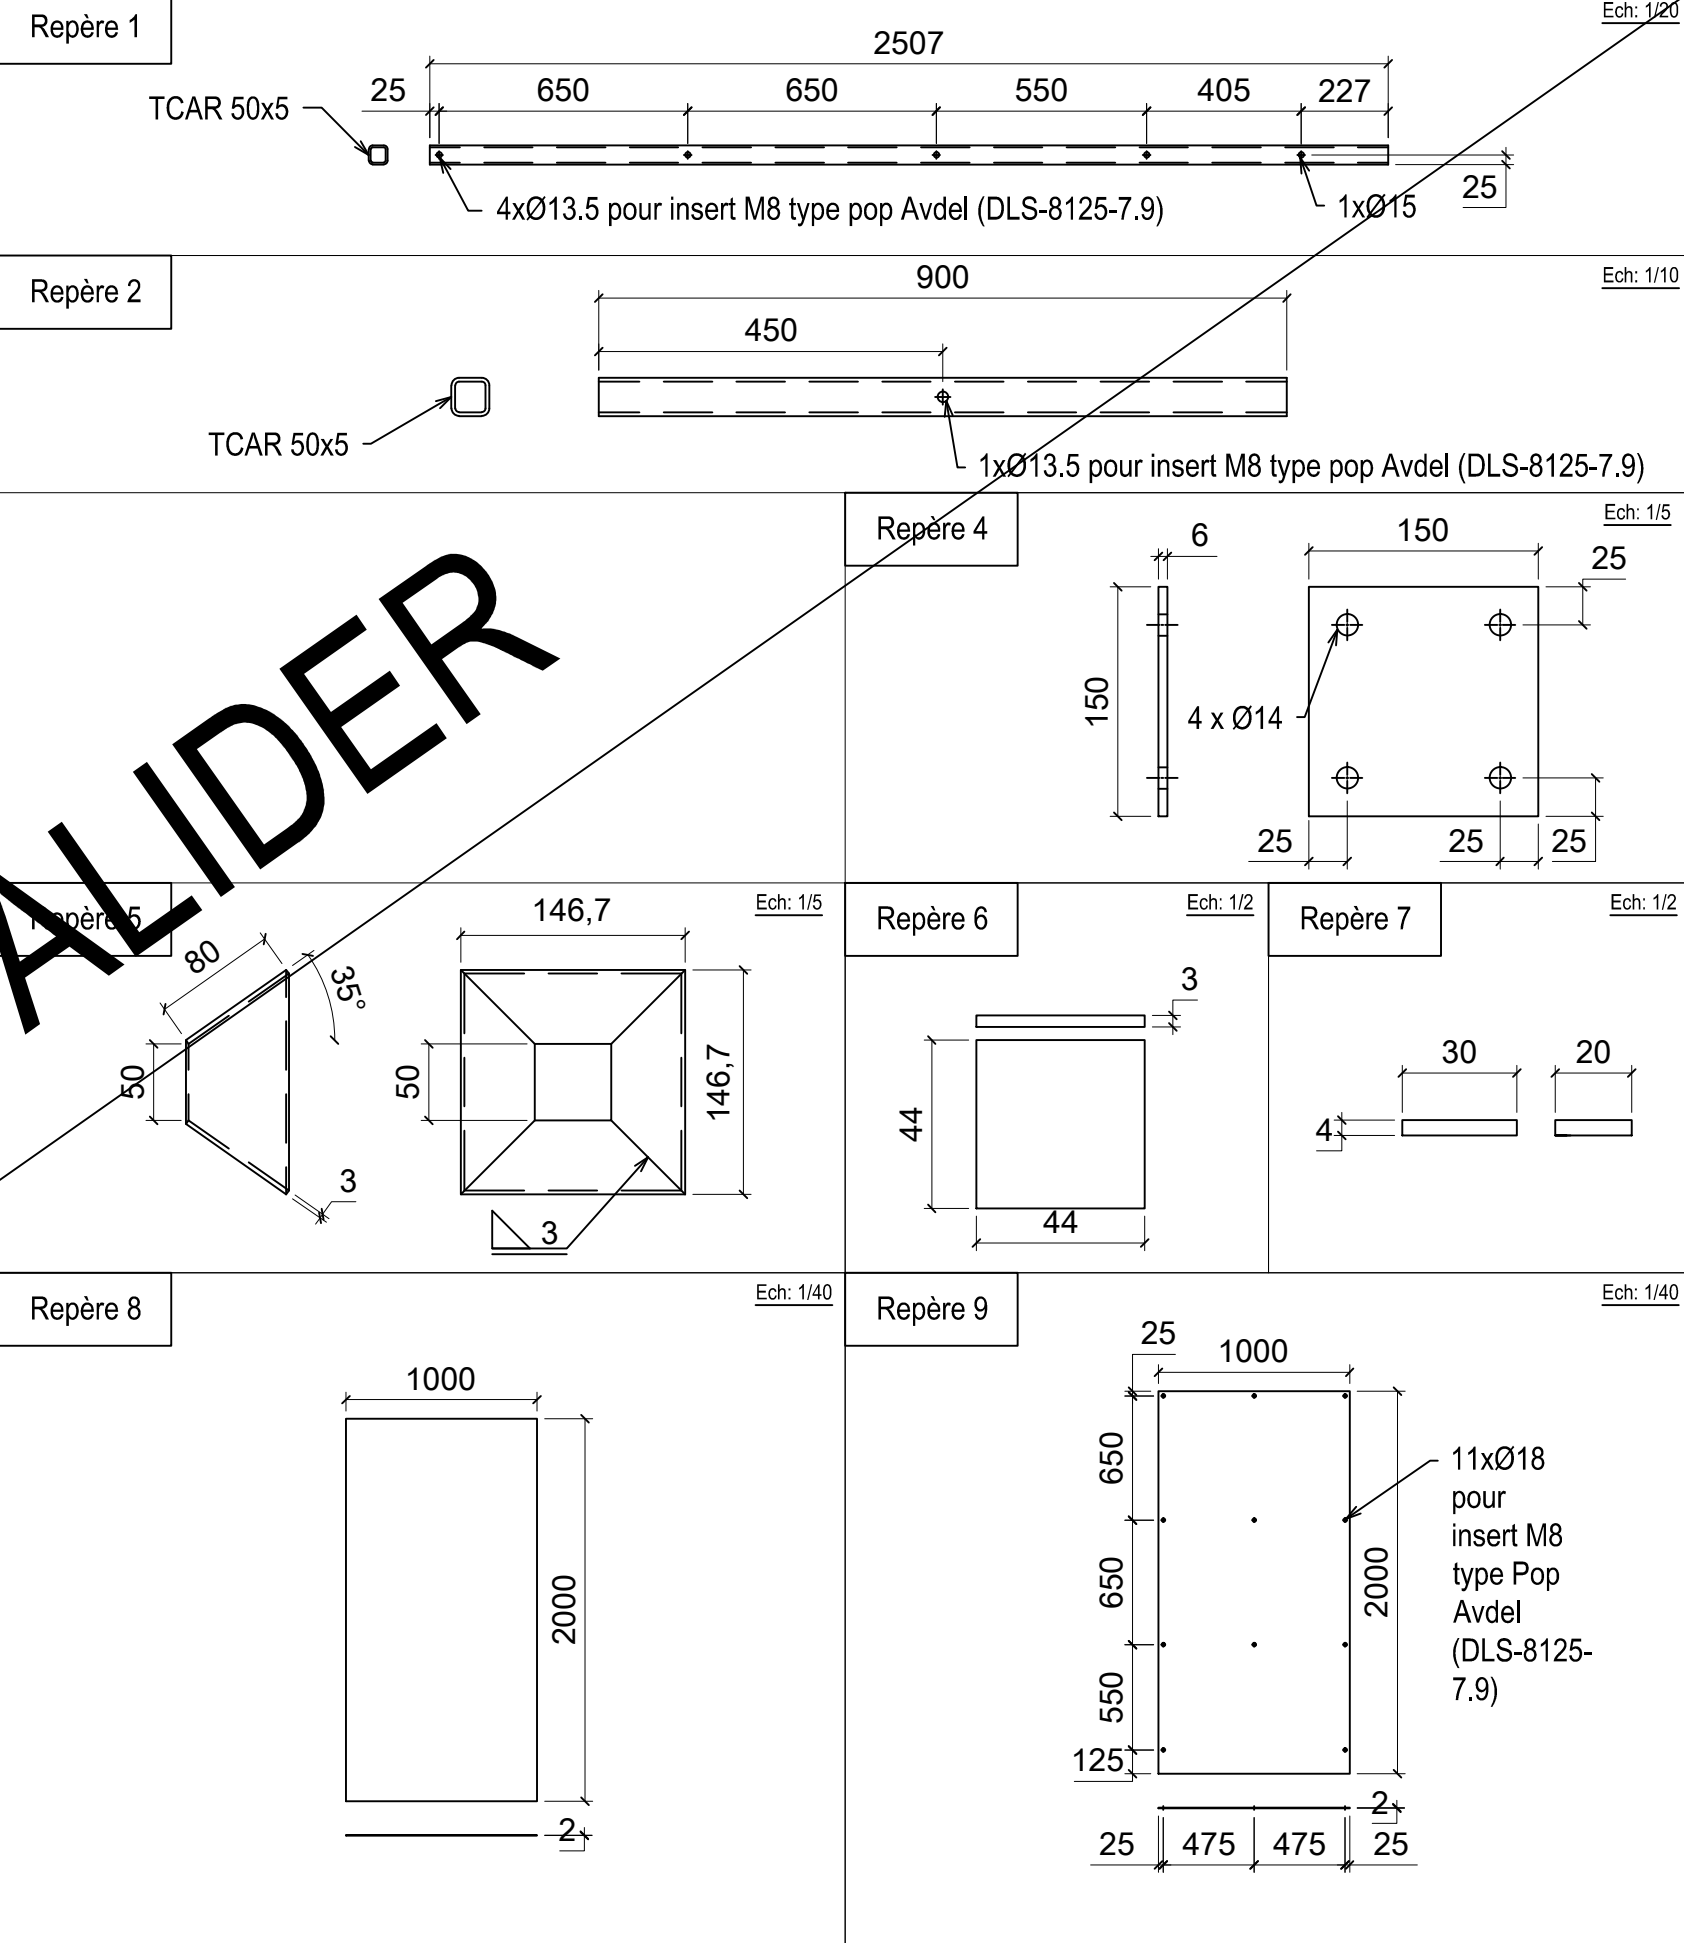

A	19/05/16	Première édition		YC	OM
Ind.	Date		Désignation des modifications	Dessiné par	Contrôle
			Cheminée droite - Bâtiment B - Rep. H	FOR	Ech.: 1
			PLAN DE FABRICATION	Unité: mm	Folio: 10/12
				Plan: 16-AF0006-PL3	



Ech: 1/20

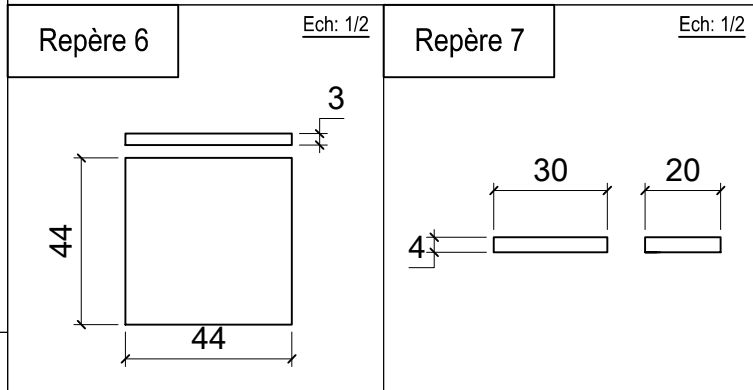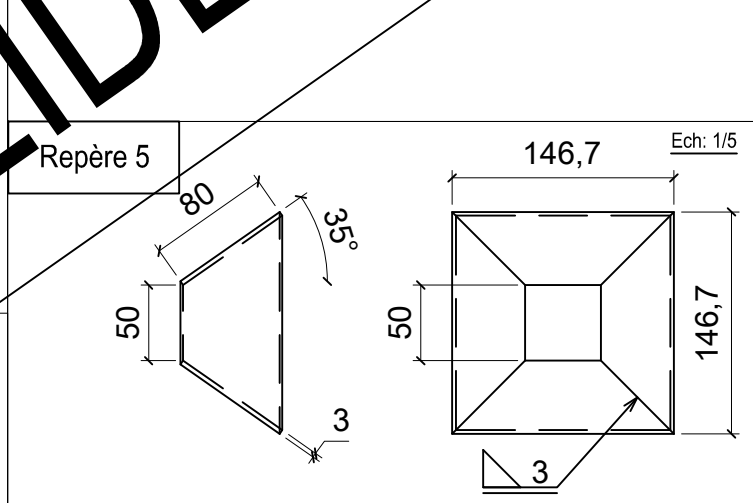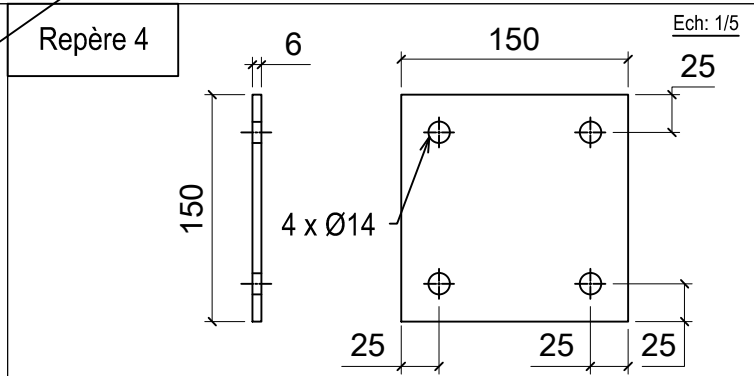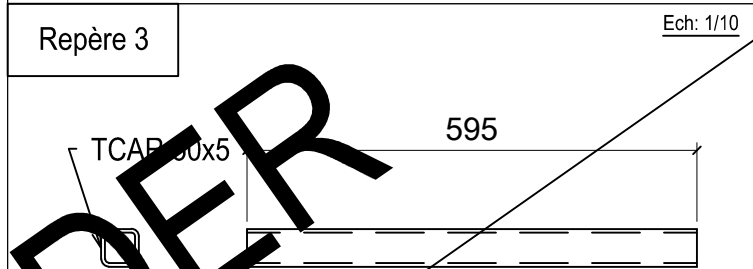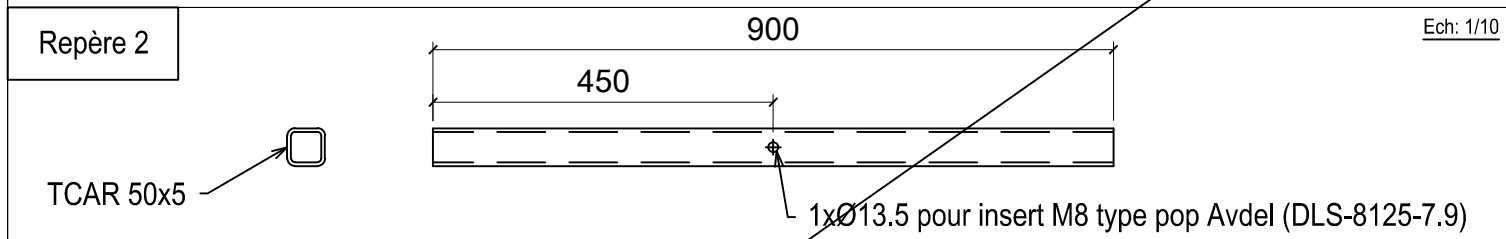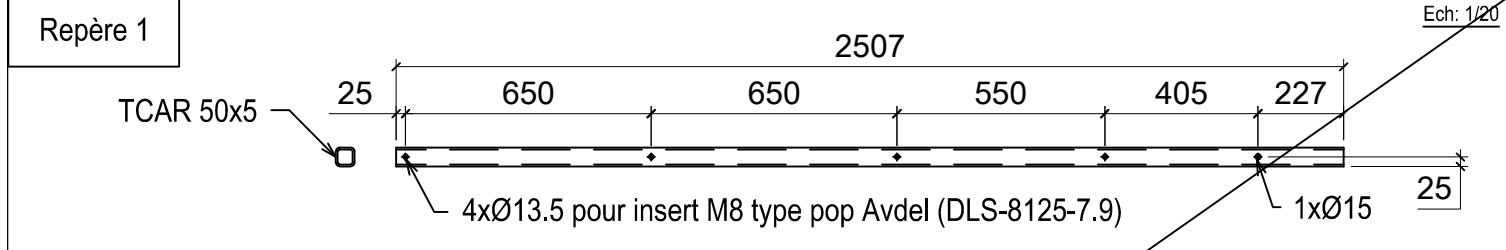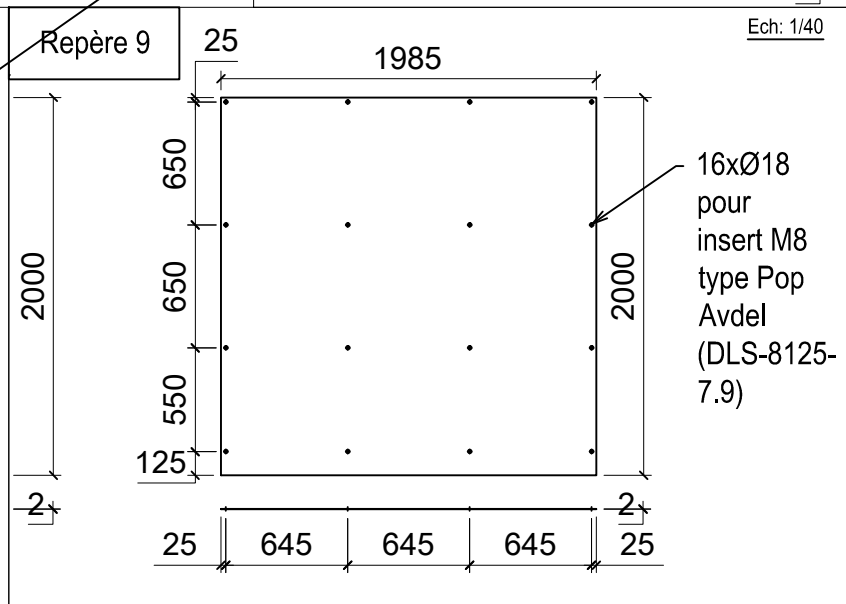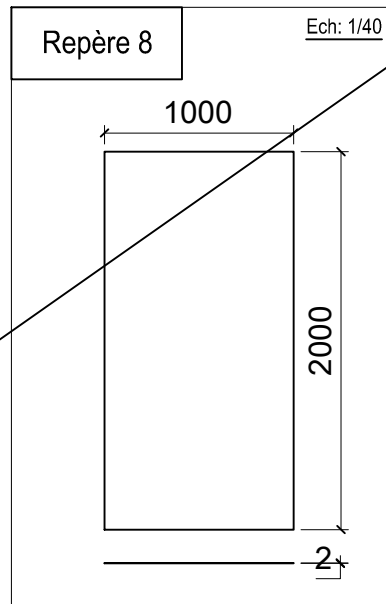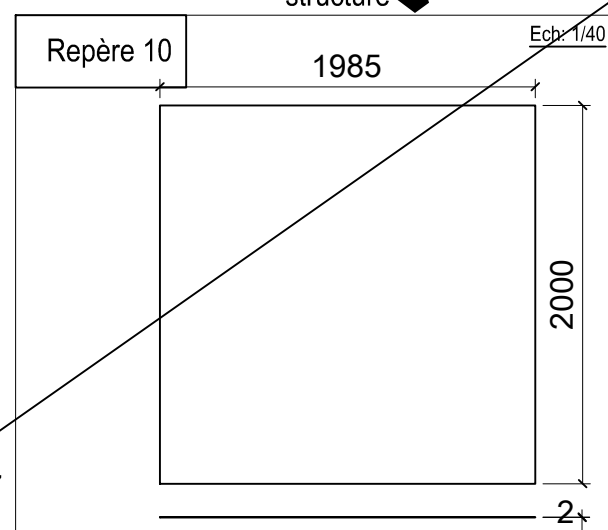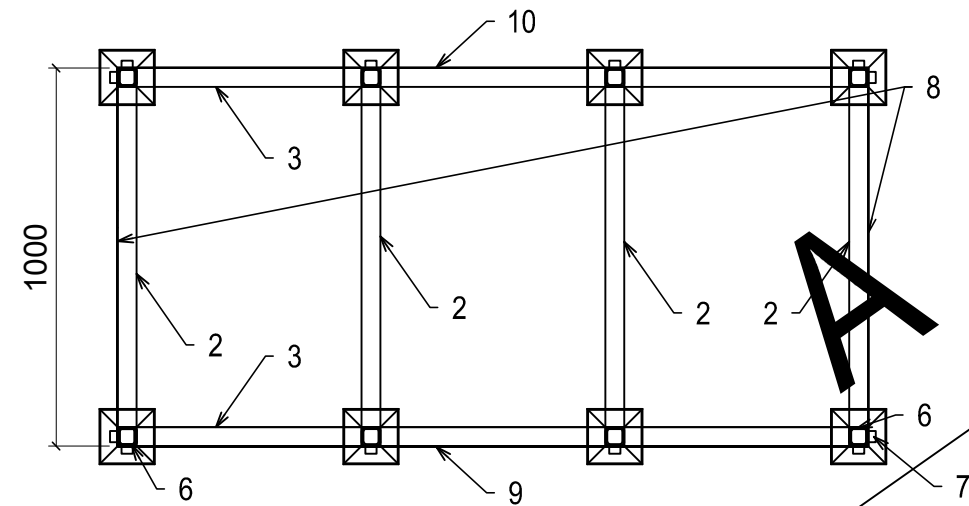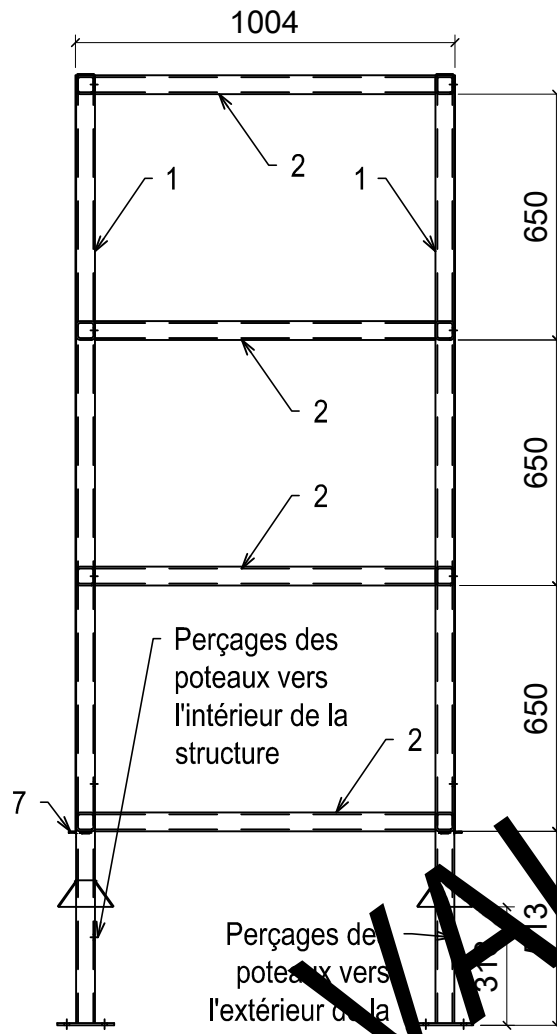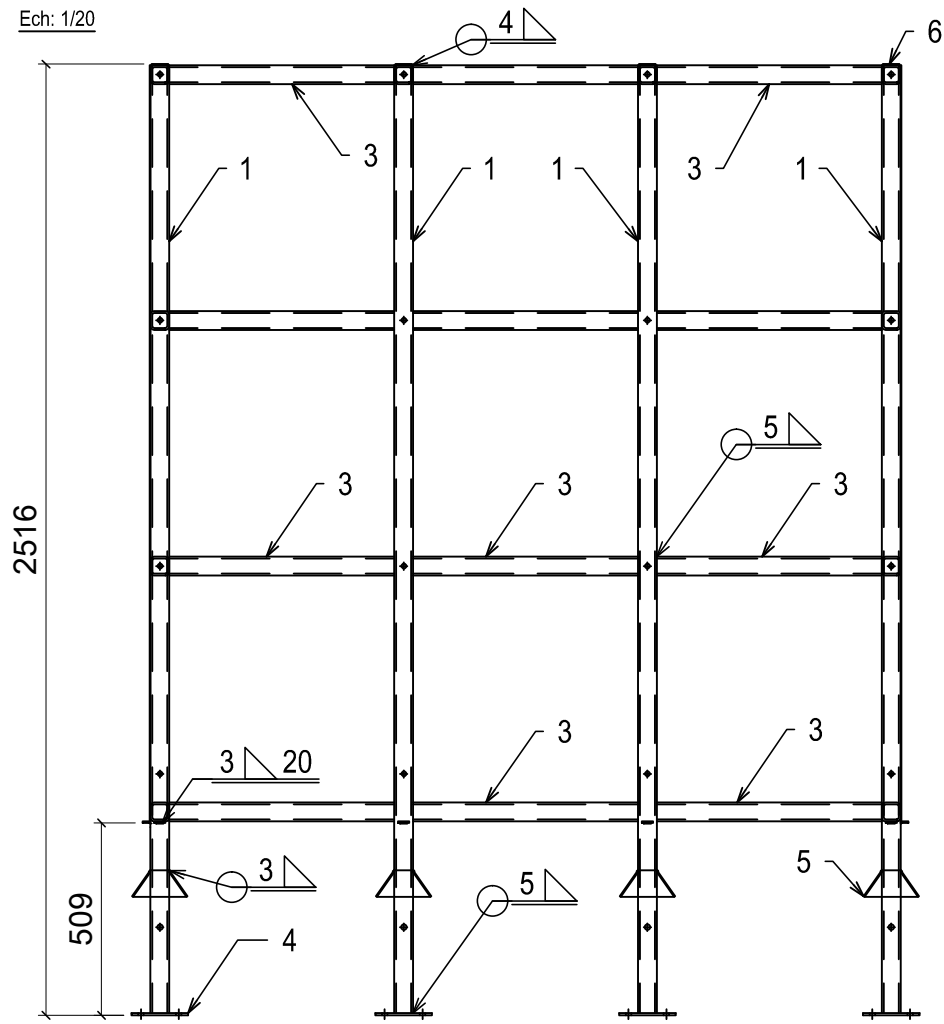

Liste des pièces		
Rep.	Libellé	Qté
1	Poteau	8
2	Lisse	10
3	Lisse 2	24
4	Platine	8
5	Collerette	8
6	Bouchon	8
7	Plat	12
8	Tôle assemblée par autoforeuses	2
9	Tôle boulonnée	1
10	Tôle assemblée par autoforeuses 2	1
Matériau : Acier S235 / Laquage RAL 9016		

Soudure continue

- Contrôle visuel 100%
- Contrôle dimensionnel 100%












a = 5mm

A	19/05/16	Première édition	YC	OM
Ind.	Date	Désignation des modifications	Dessiné par	Contrôle
Cheminée double - Bâtiment B - Rep. I			FOR	Ech.: 1
PLAN DE FABRICATION			Unité: mm	Folio: 11/12
Ce document est la propriété de la société DOPAM'IN. Il ne pourra, sans notre autorisation expresse, être reproduit ou communiqué à des tiers.			Plan: 16-AF0006-PL3	






Cheminée double - Bâtiment B - Rep. I

PLAN DE FABRICATION

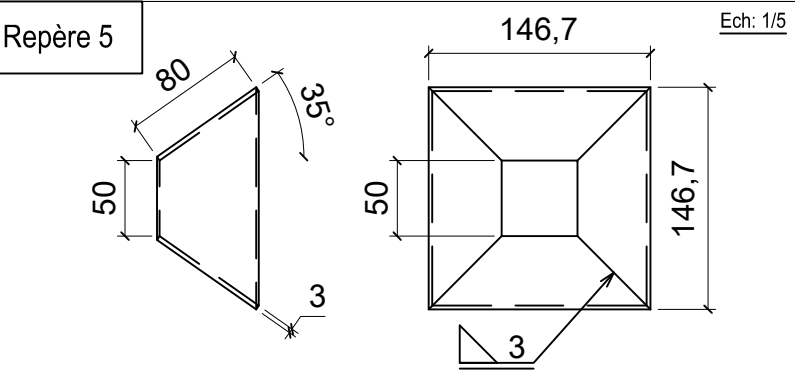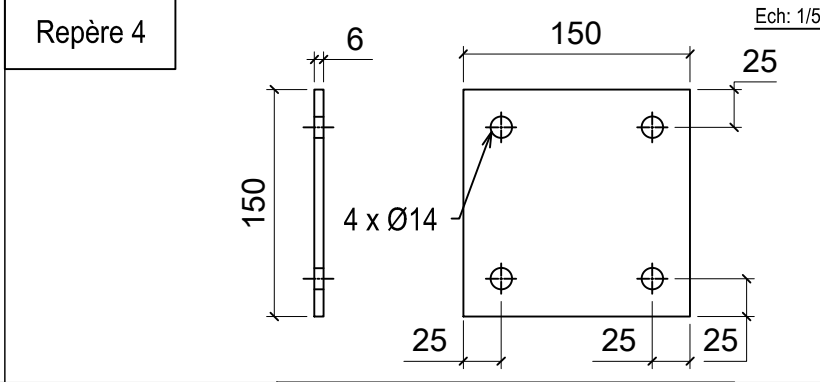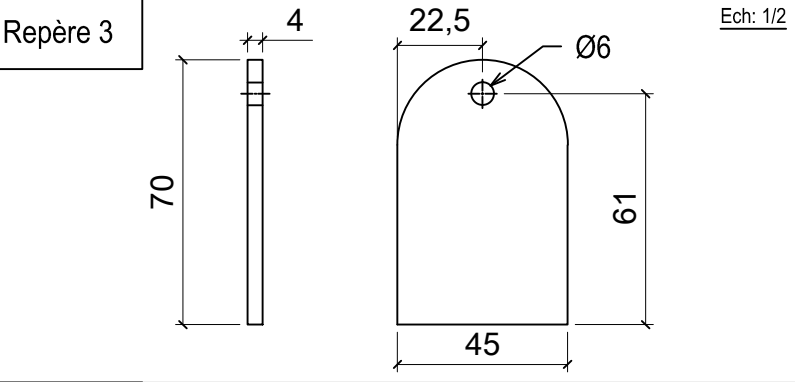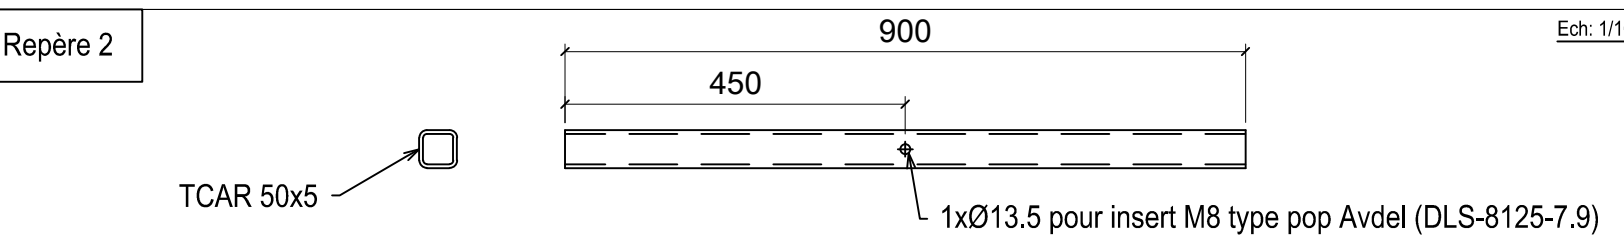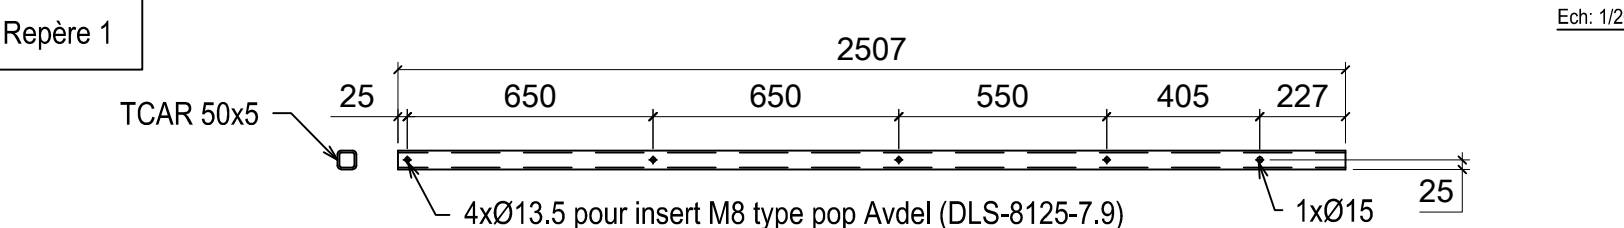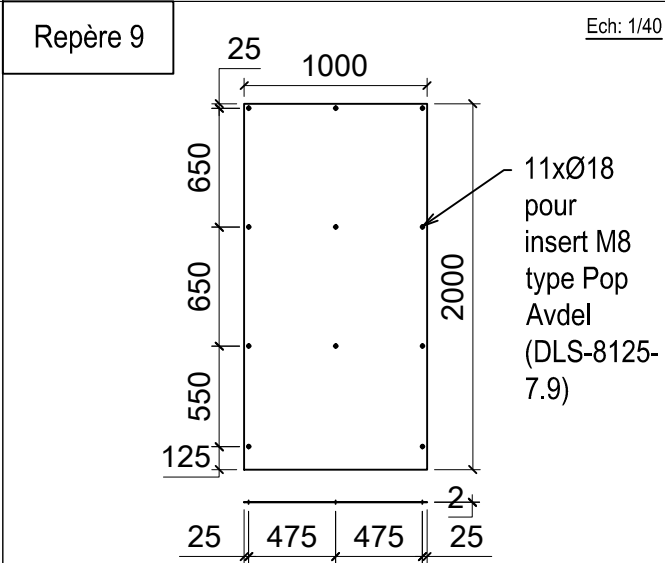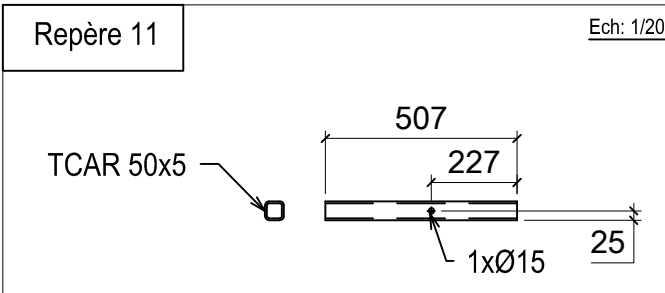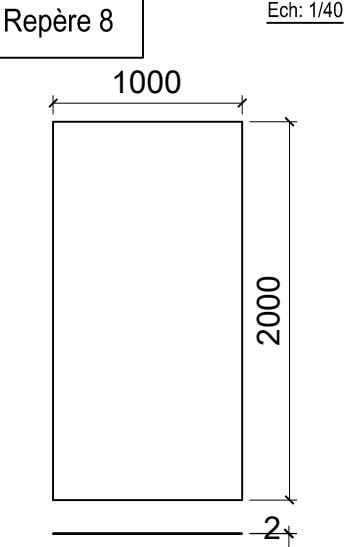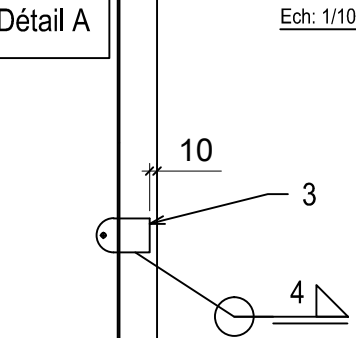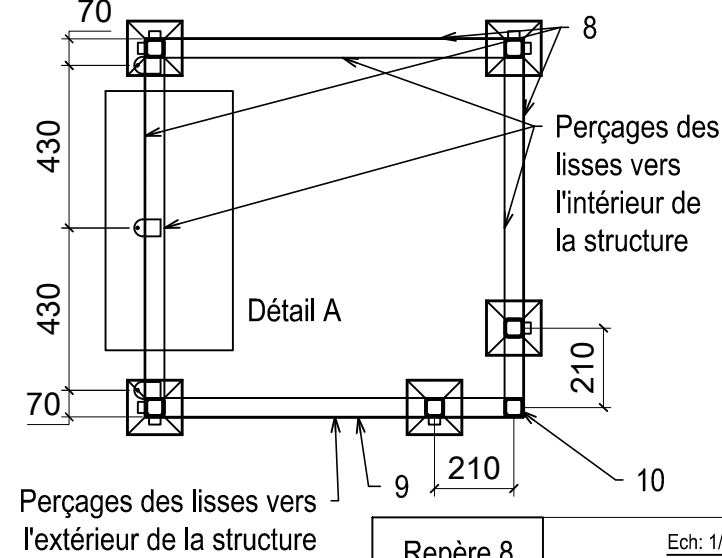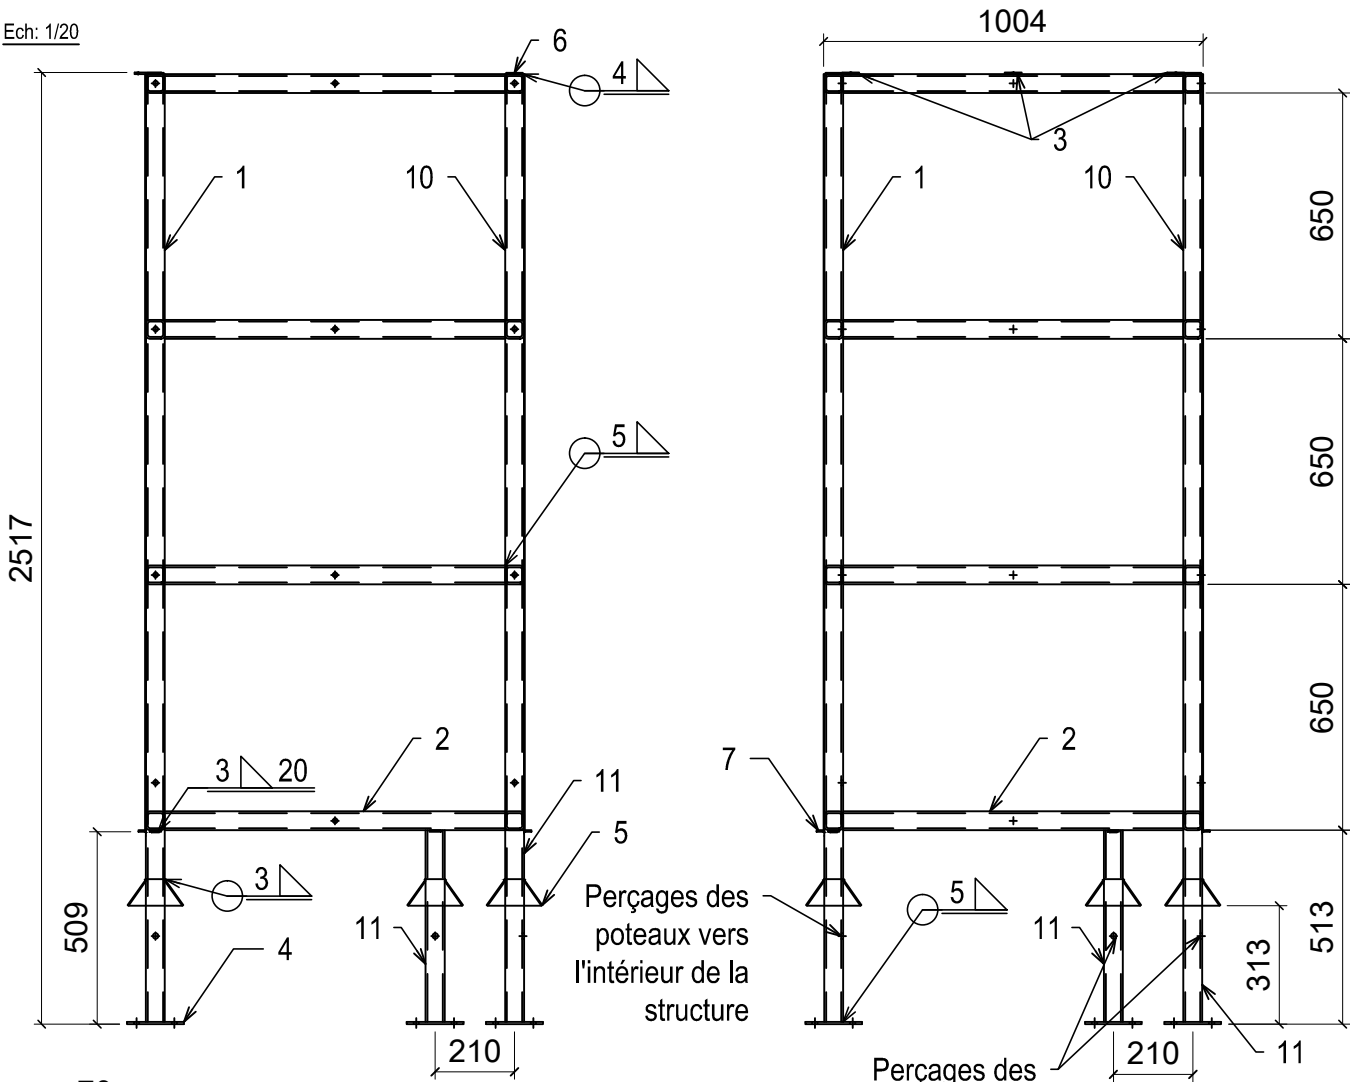

Soudure continue
- Contrôle visuel 100%
- Contrôle dimensionnel 100%
a = 5mm

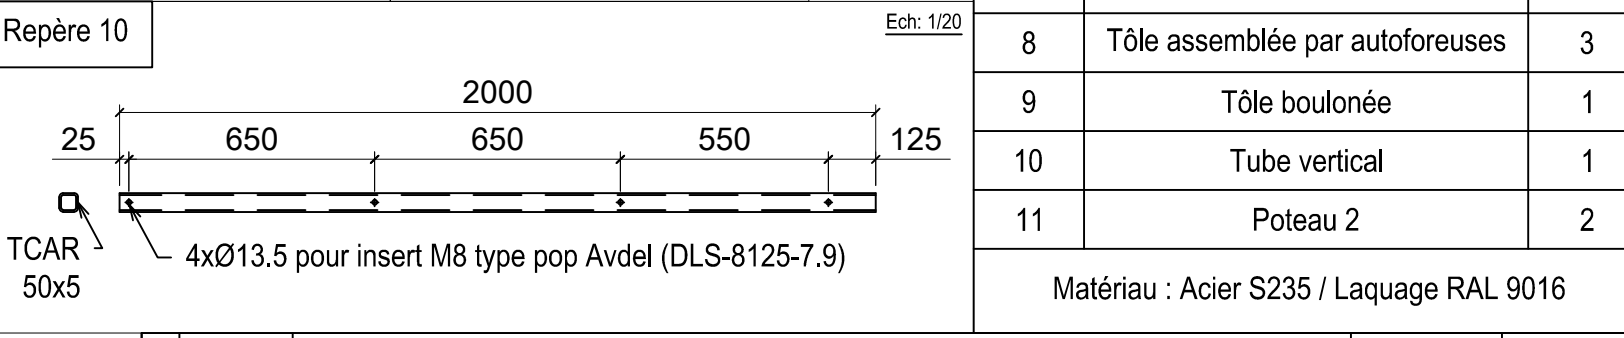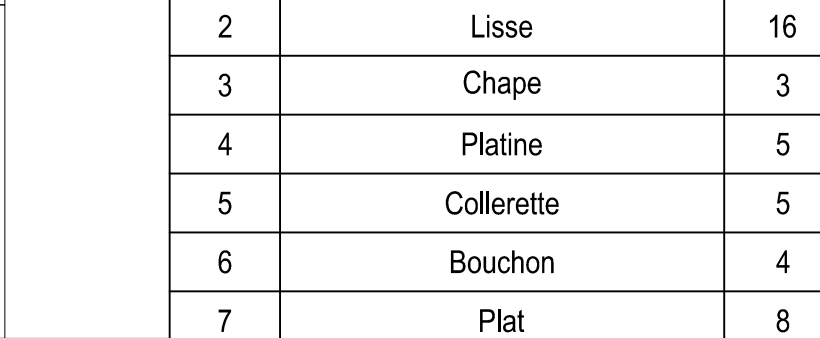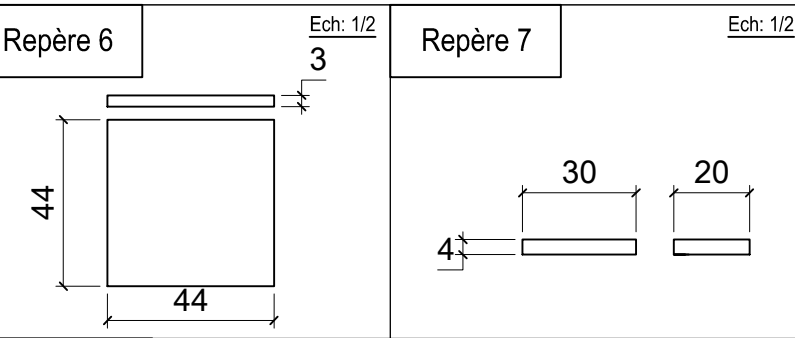

Liste des pièces		
Rep.	Libellé	Qté
1	Poteau	3
2	Lisse	16
3	Chape	3
4	Platine	5
5	Collerette	5
6	Bouchon	4
7	Plat	8
8	Tôle assemblée par autoforeuses	3
9	Tôle boulonnée	1
10	Tube vertical	1
11	Poteau 2	2
Matériau : Acier S235 / Laquage RAL 9016		

A	19/05/16	Première édition	YC	OM
Ind.	Date	Désignation des modifications	Dessiné par	Contrôle
 Cheminée avec poteaux décalés - Bâtiment B - Rep. J PLAN DE FABRICATION Ce document est la propriété de la société DOPAM'IN. Il ne pourra, sans notre autorisation expresse, être reproduit ou communiqué à des tiers.			FOR 	Ech. : 1
			Unité : mm	Folio : 12/12
			Plan : 16-AF0006-PL3	