


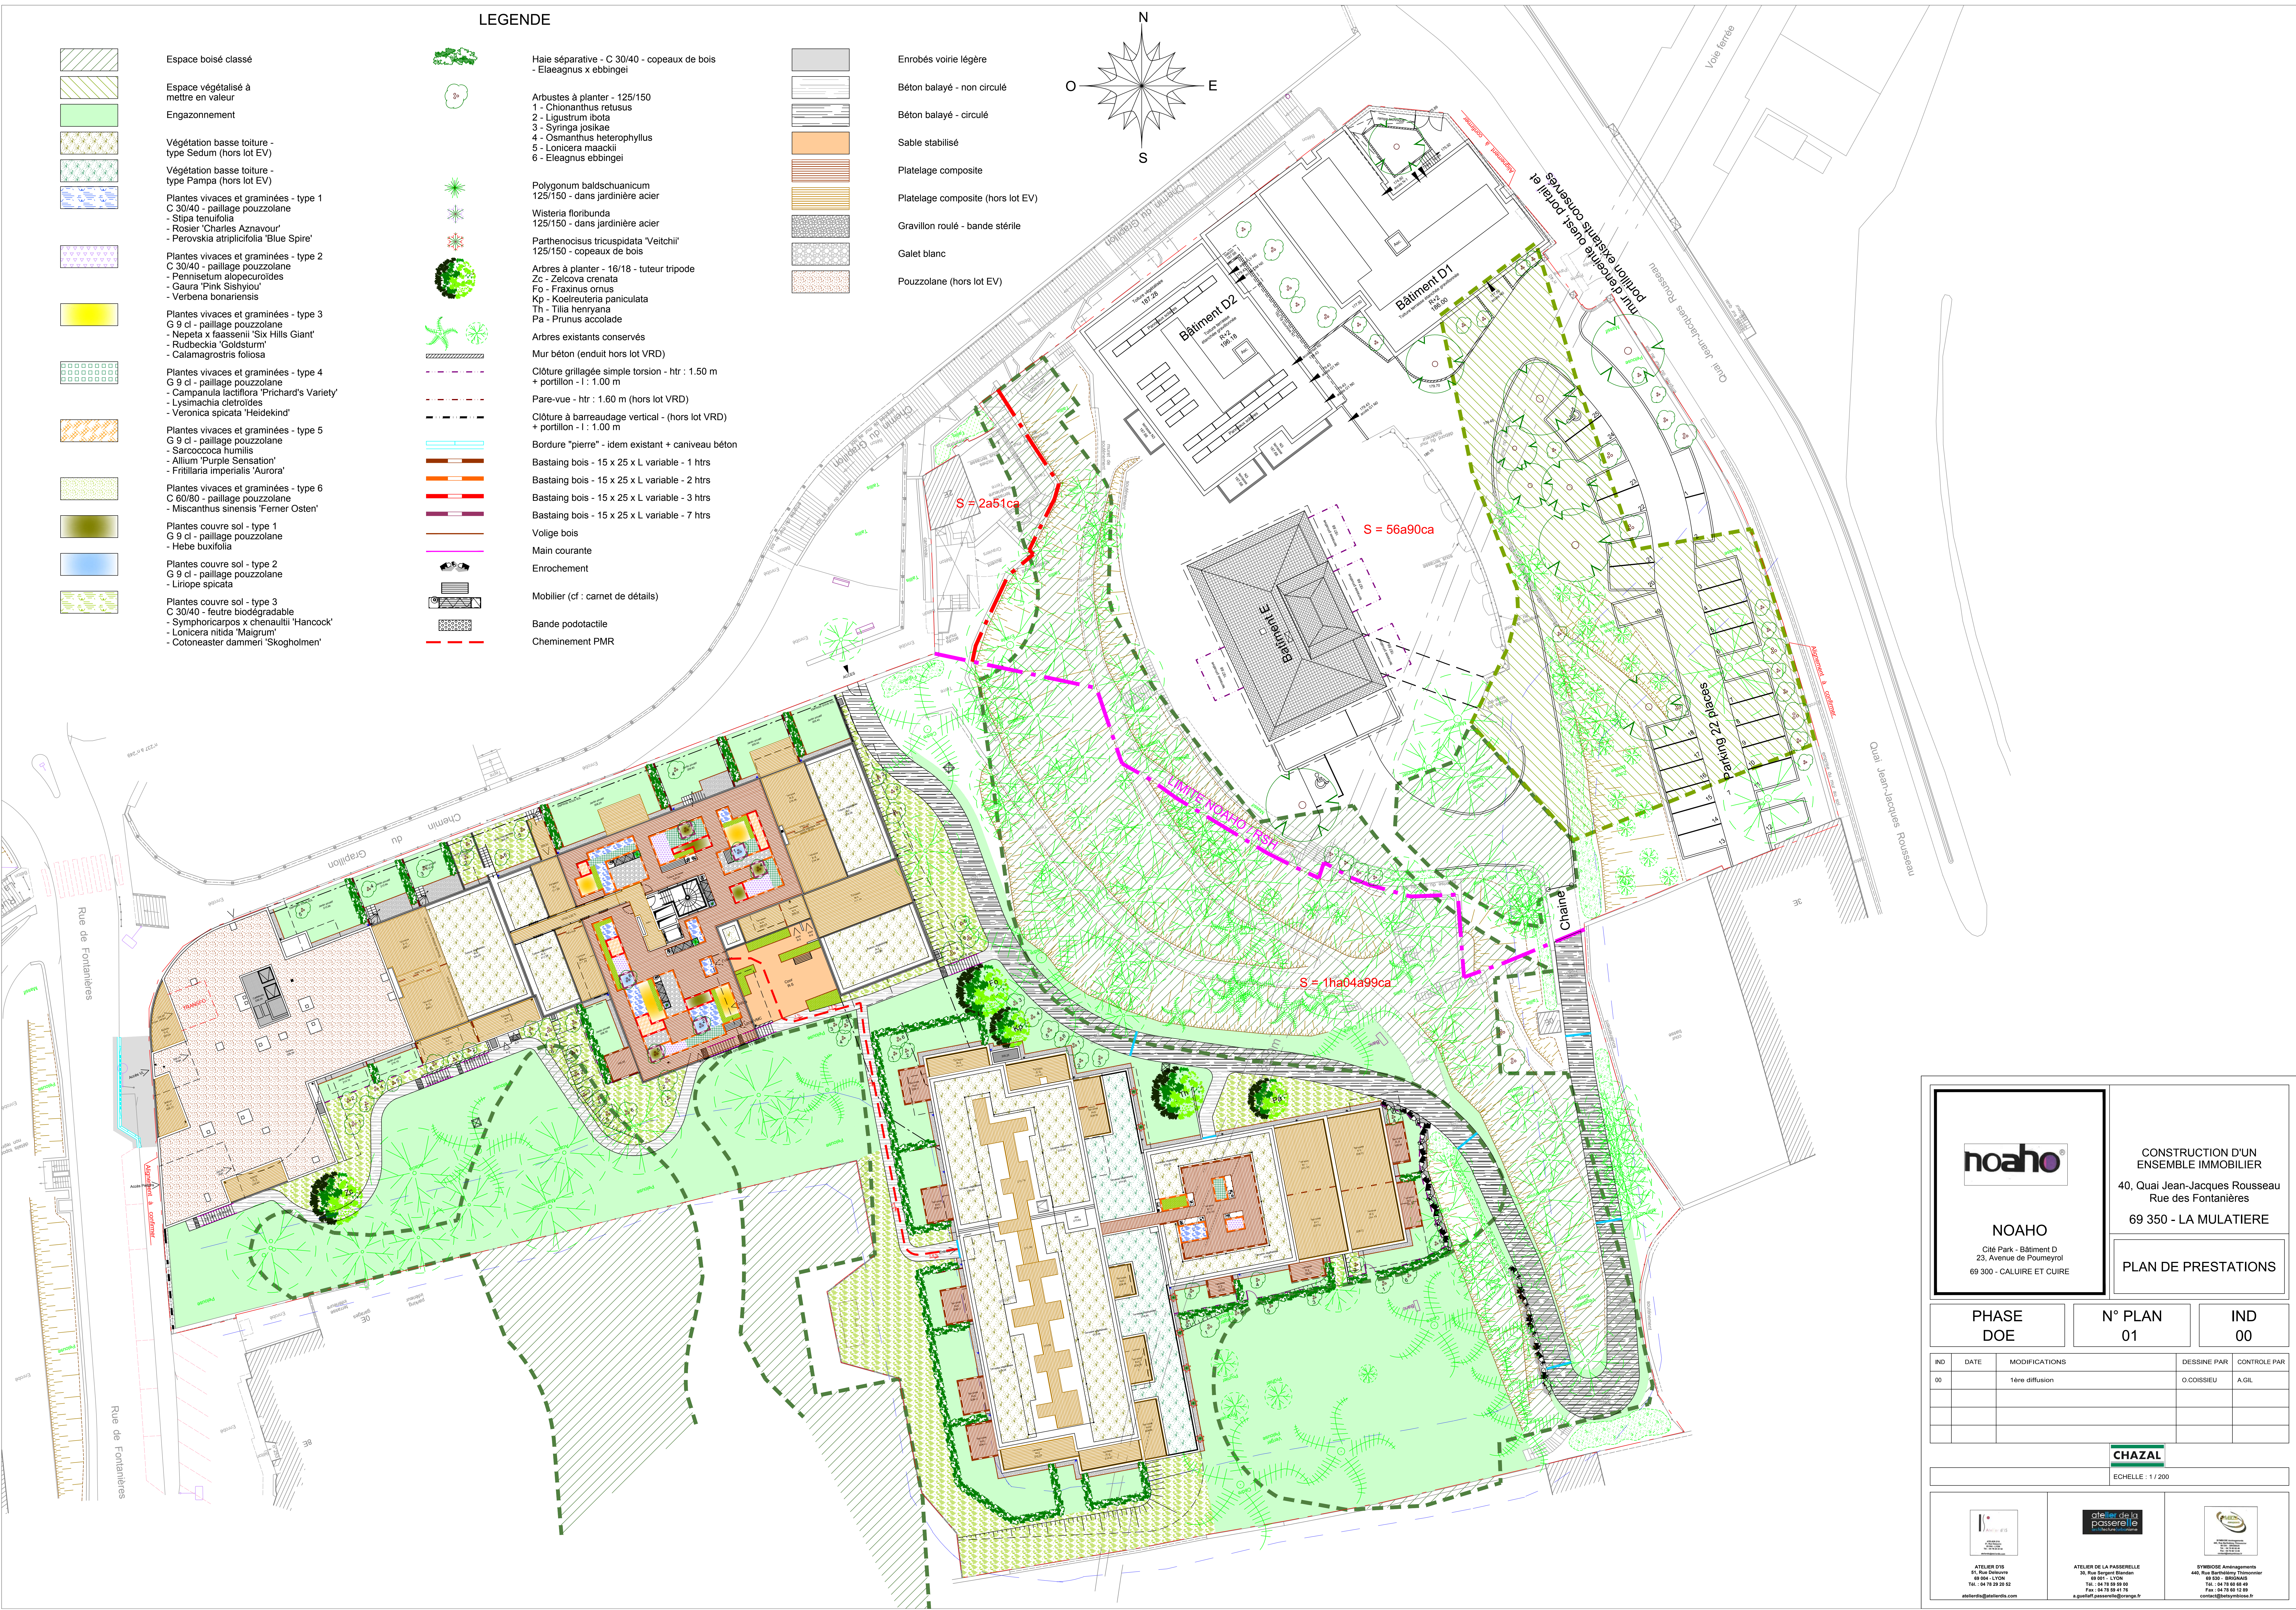



CONSTRUCTION D'UN
ENSEMBLE IMMOBILIER

40, Quai Jean-Jacques Rousseau
Rue des Fontanières
69 350 - LA MULATIERE

NOAHO

Cité Park - Bâtiment D
23, Avenue de Poumeyrol
69 300 - CALLUIRE ET CUIRE

PLAN DE PRESTATIONS

PHASE DOE	N° PLAN 01	IND 00
--------------	---------------	-----------

IND	DATE	MODIFICATIONS	DESSINE PAR	CONTROLE PAR
00		1ère diffusion	O COISSEU	A GIL

CHAZAL

ECHELLE : 1 / 200



ATELIER D18
51, Rue Denecour
69 004 - LYON
Tel : 04 78 28 50 52
www.atelierd18.com



ATELIER DE LA PASSERELLE
35, Rue Sergent Blonden
69 001 - LYON
Tel : 04 78 08 01 10
Fax : 04 78 08 41 78
a.gautier@passerellegroup.fr



SYMBOISE Animateurs
445, Rue Barthélemy Thiers
69 001 - LYON
Tel : 04 78 08 01 10
Fax : 04 78 08 12 89
contact@symboise.fr