
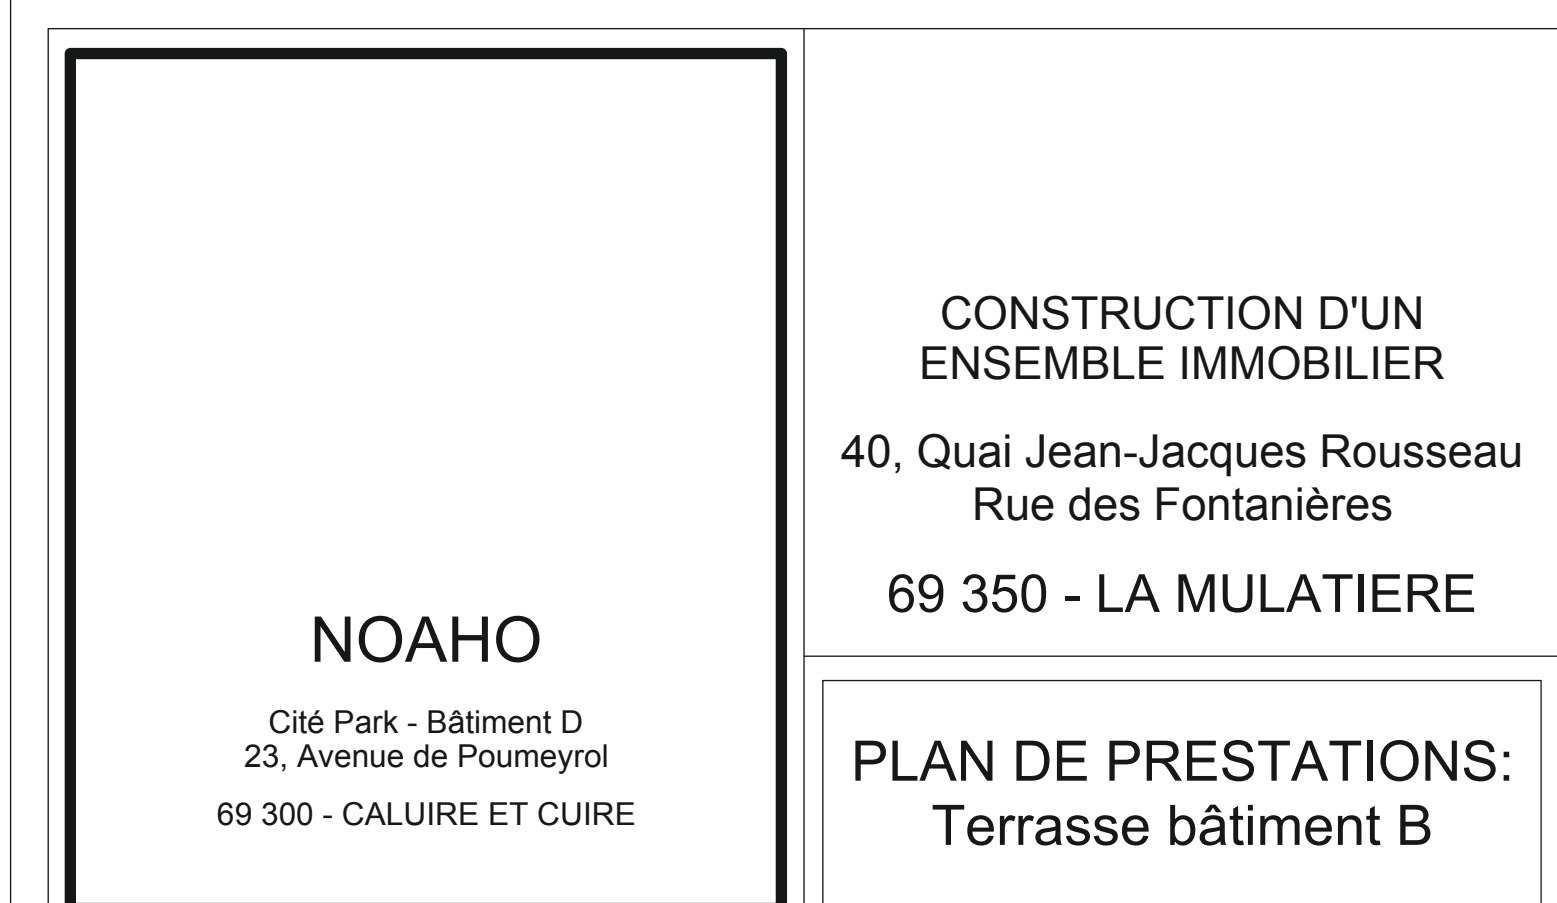


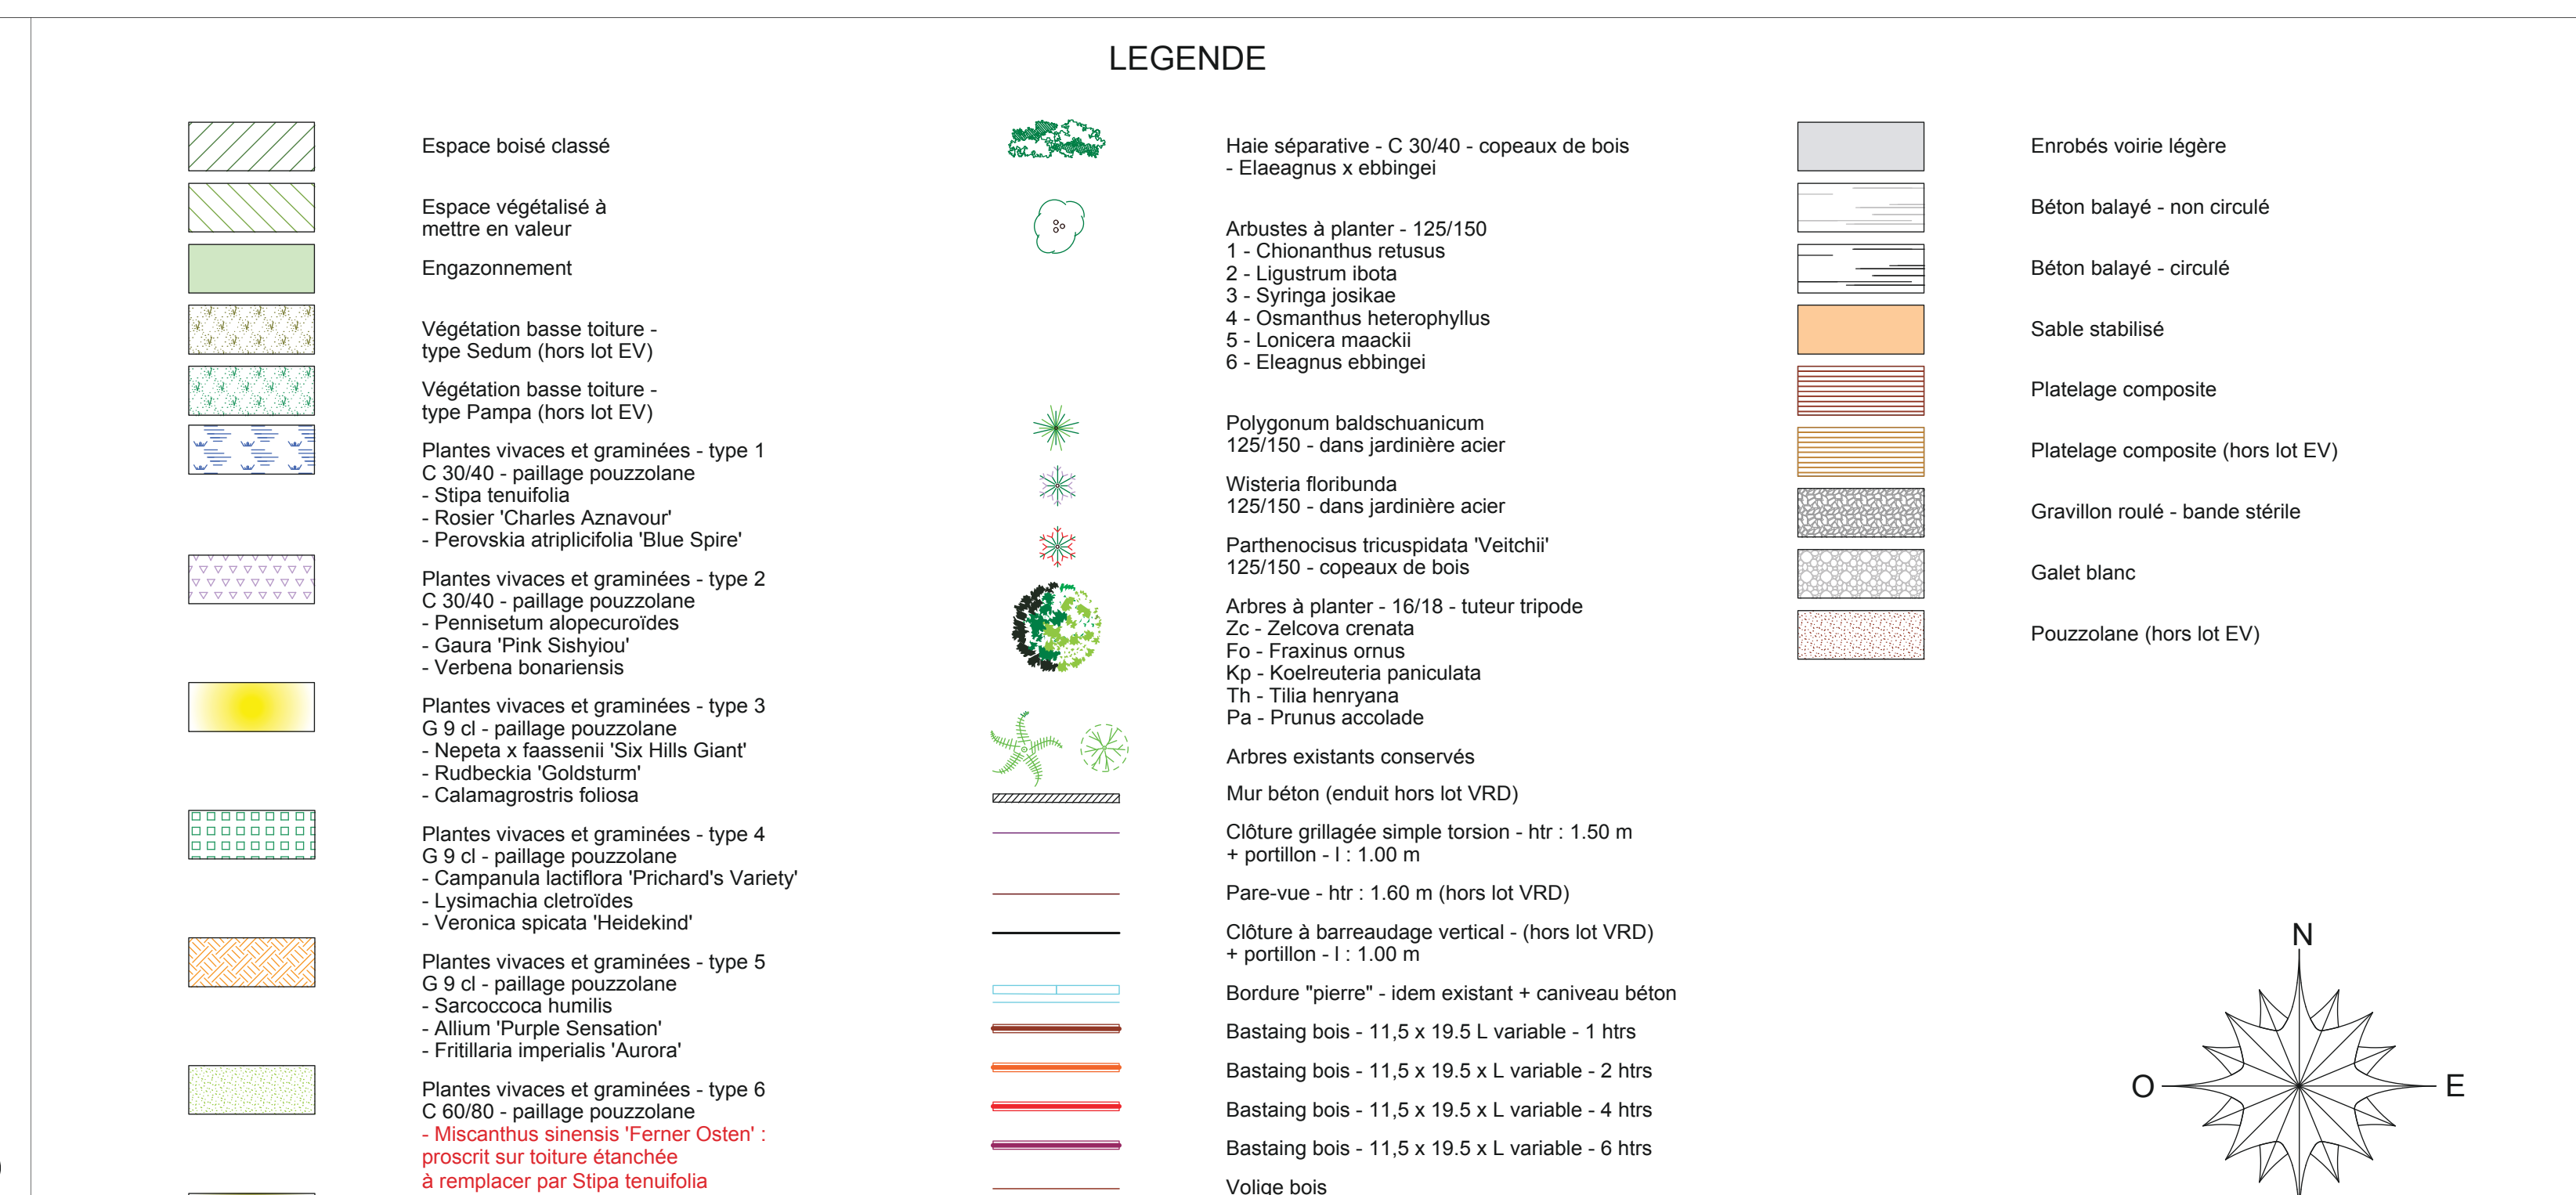

PHASE EXE		N° PLAN 08	IND 02	
IND	DATE	MODIFICATIONS	DESSINE PAR	CONTROLE PAR
00	02/05/2016	1ère diffusion	C. BAUBY	A. GIL
01	09/05/2016	Ajout légendes, réseaux et détails des cornières	C. BAUBY	A. GIL
02	31/05/2016	Mise à la cote des serrures suivant détails DOPAMIN	C. BAUBY	A. GIL

 CHAZAL SAS 28 rue Lavoisier 69800 SAINT PRIEST Tél : 04.37.25.36.00 / Fax : 04.37.25.36.19			ECHELLE PLAN : 1 / 100	ECHELLE COUPE : 1/20
DATE : 31/05/2016				

ATELIER D'YS 81, Rue Delavare 69 004 - LYON Tel. : 04 78 29 20 22 atelierd@atelierdys.com	ATELIER DE LA PASSERELLE 30, Rue-Sergent Blanches 69 001 - LYON Tel. : 04 78 28 89 50 Fax : 04 78 69 47 71 a.guelfetti.passerelle@orange.fr	SYMBOISE Aménagements 460, Rue Barthélémy Thiersmier 69 030 - BRIGNAUX Tel. : 04 73 85 65 48 Fax : 04 78 62 12 99 contact@symboise.fr
--	--	---