
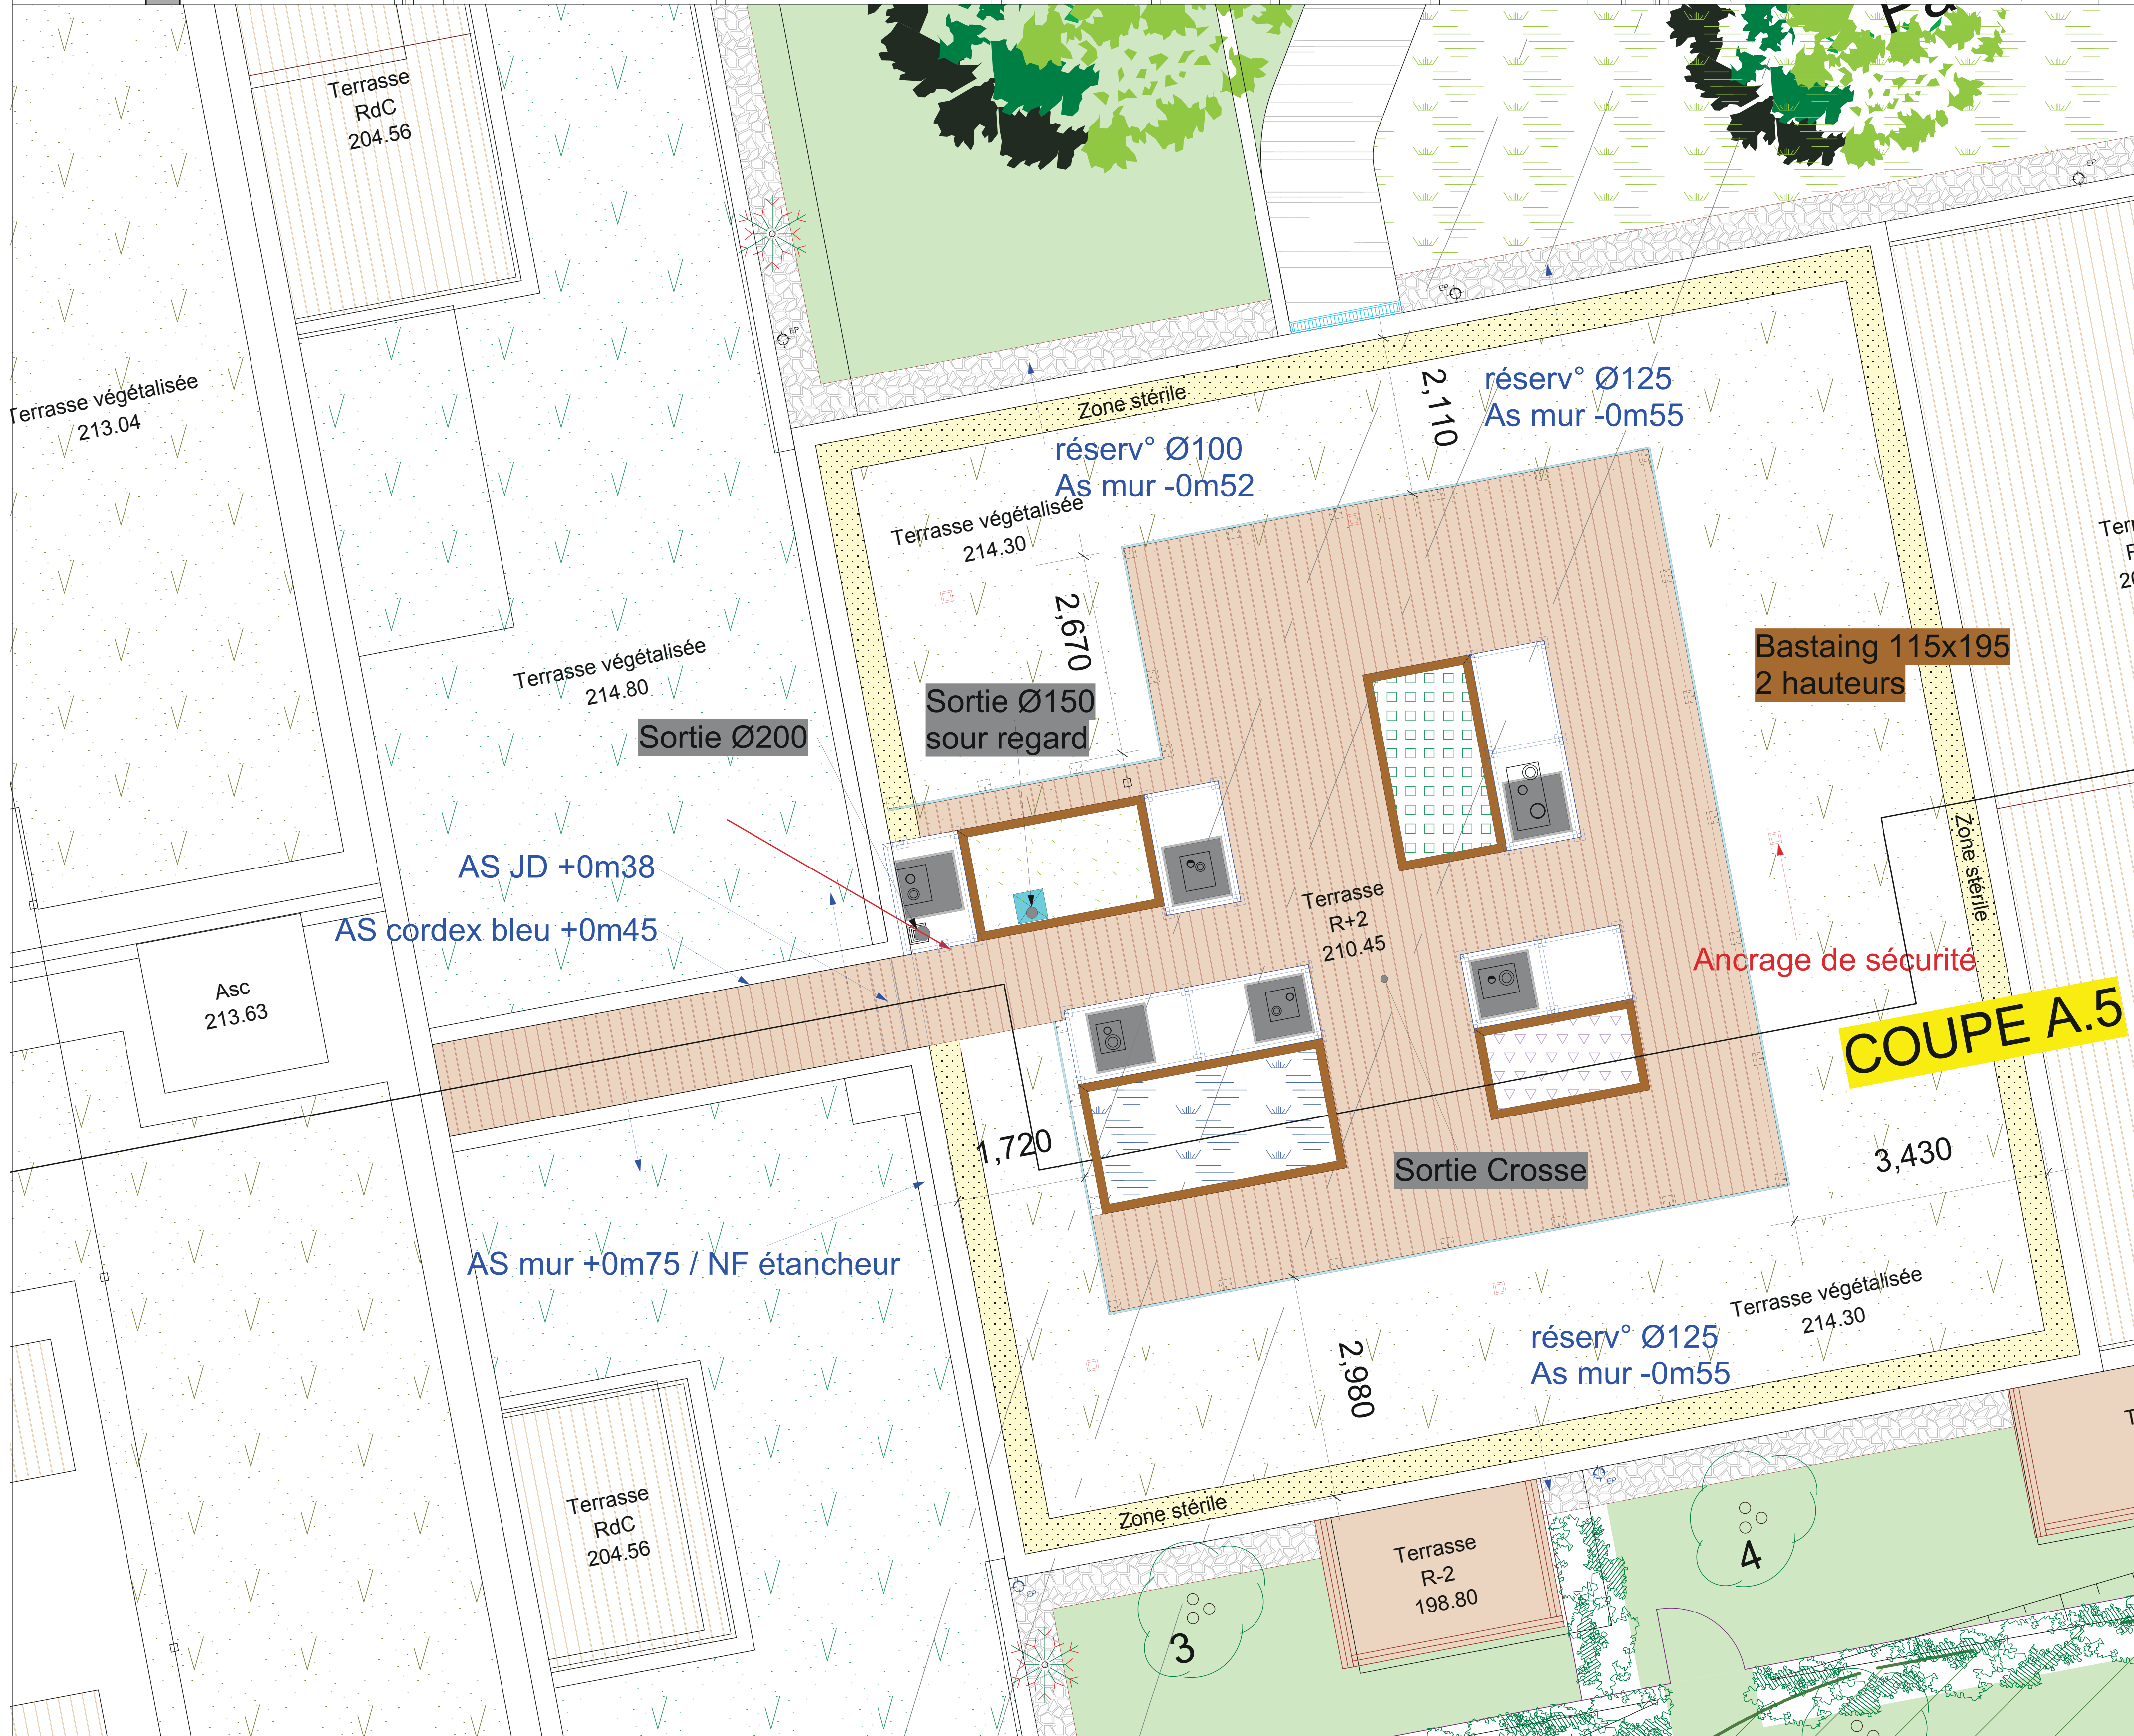


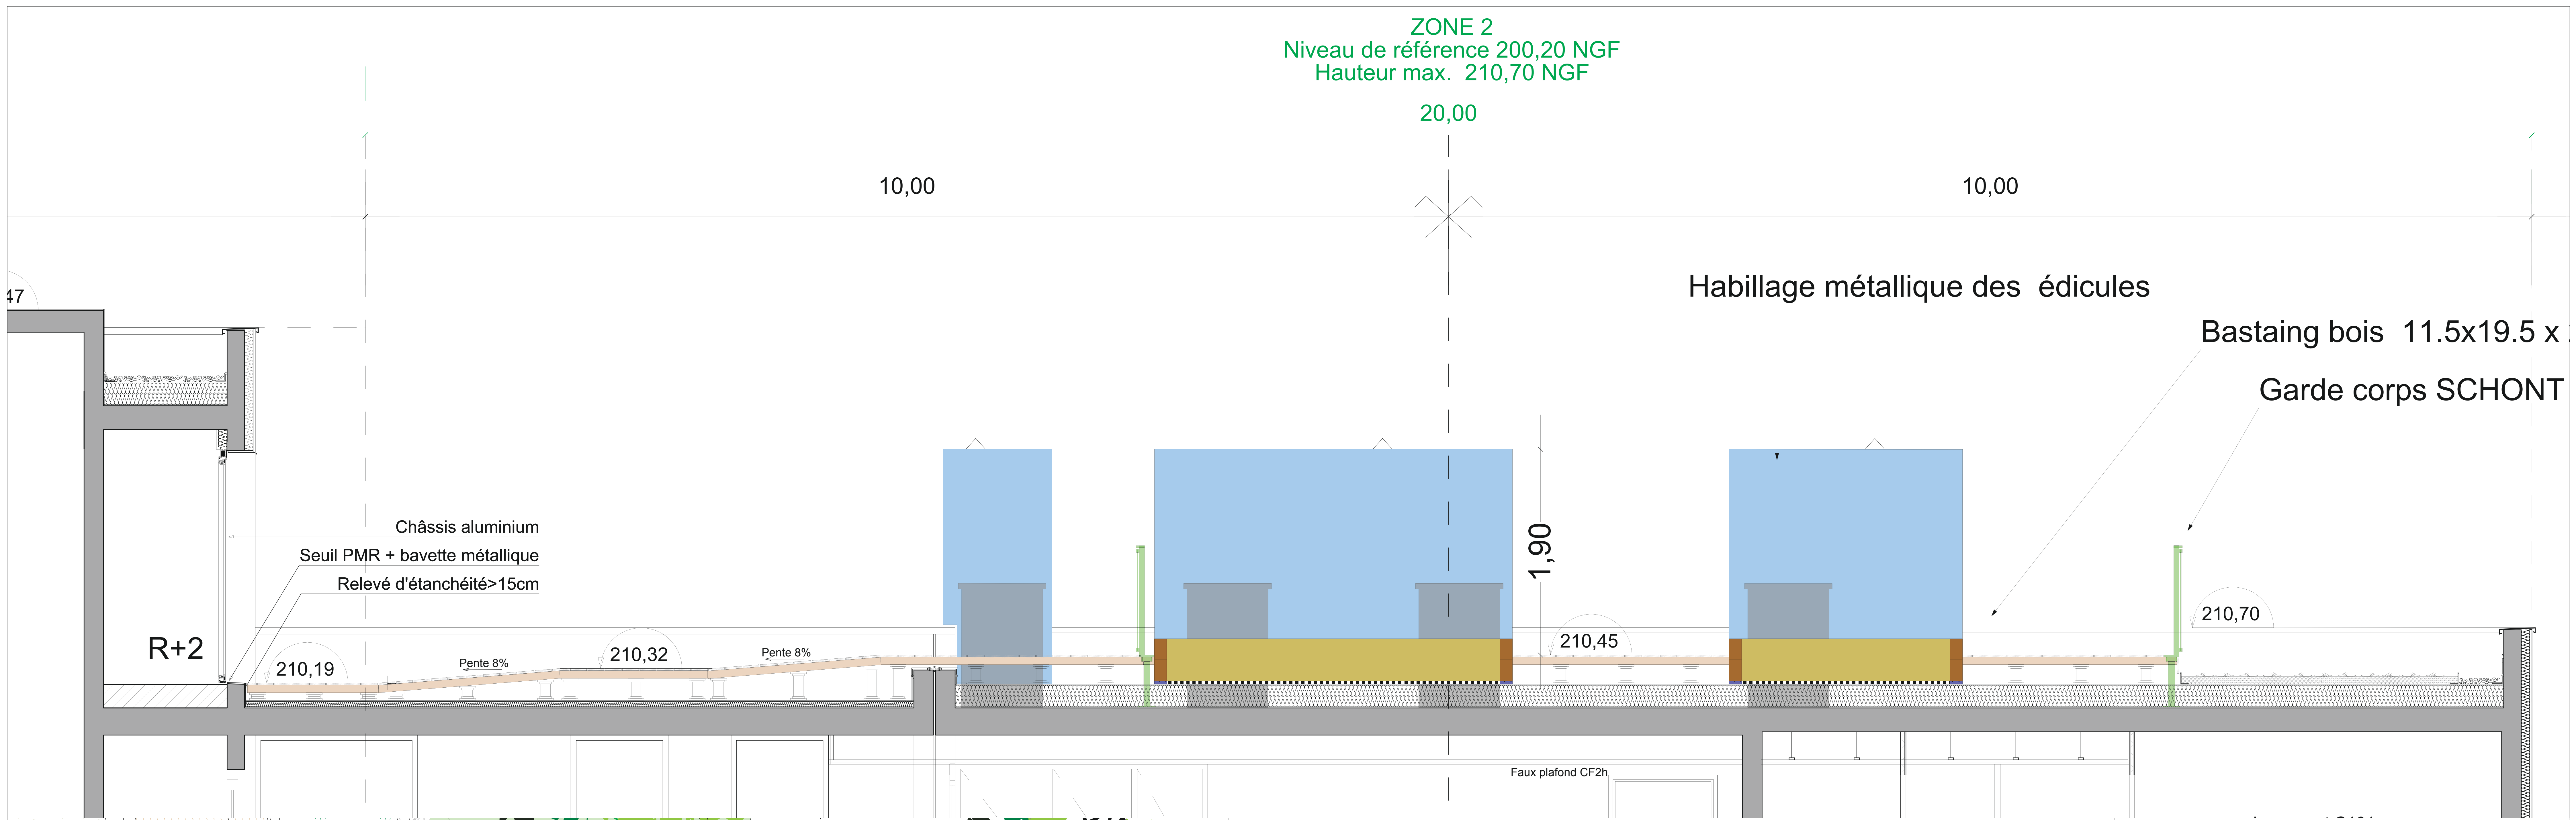

CONSTRUCTION D'UN ENSEMBLE IMMOBILIER

40, Quai Jean-Jacques Rousseau
Rue des Fontanières
69 350 - LA MULATIERE

NOAHO

Cité Park - Bâtiment D
23, Avenue de Poincy
69 300 - CALURE ET CUIRE

PLAN DE PRESTATIONS:
Terrasse bâtiment C

IND	DATE	MODIFICATIONS	DESSINE PAR	CONTROLE PAR
00	07/12/2015	1ère diffusion - levé de l'existant	C. BAUBY	A. GIL
01	08/02/2016	Implantation serrurerie SCHONT / basting / habillage édicules	C. BAUBY	A. GIL
02	10/02/2016	Recalage d'implantation suite à relevé sur site	C. BAUBY	A. GIL
03	31/05/2016	Modifications de serrurerie suivant capotages SCHONT Mise à la cote des serrures suivant détails DOPAMIN	C. BAUBY	A. GIL

CHAZAL SAS
21 rue Lavoisier
69600 SAINT PRIEST
Tél : 04 78 25 36 00 / Fax : 04 78 25 36 19

DATE : 31/05/2016

ECHELLE PLAN : 1/50

ECHELLE COUPE : 1/20

ATELIER D'IS
51, Rue Delorme
69 001 - LYON
Tél : 04 78 29 20 82
atelierdis@atelierdis.com

ATELIER DE LA PASSERELLE
30, Rue Serpent Blandin
69 001 - LYON
Tél : 04 78 29 20 80
Fax : 04 78 29 20 81
a.gueriff@passerelleorange.fr

SYMBOSE Aménagements
440, Rue Barthélemy Trimoisier
69 030 - BRIGNAUX
Tél : 04 78 68 68 69
Fax : 04 78 68 68 69
contact@symbose.fr

LEGENDE

Espace boisé classé

Espace végétalisé à mettre en valeur

Engazonnement

Végétation basse toiture - type Sedum (hors lot EV)

Végétation basse toiture - type Pampa (hors lot EV)

Plantes vivaces et graminées - type 1

C 30/40 - paillage pouzzolane

Stipa tenuifolia

Rosier 'Charles Aznavour'

Pierovskia atriplicifolia 'Blue Spire'

Plantes vivaces et graminées - type 2

C 30/40 - paillage pouzzolane

Pennisetum alopecuroides

Gaura 'Pink Sherry'

Verbena bonariensis

Plantes vivaces et graminées - type 3

G 9 ci - paillage pouzzolane

Nepeta x faassenii 'Six Hills Giant'

Rudbeckia 'Goldsturm'

Calluna vulgaris

Plantes vivaces et graminées - type 4

G 9 ci - paillage pouzzolane

Campulidactylus 'Pichard's Variety'

Lysimachia clethroides

Veronica spicata 'Heidekind'

Plantes vivaces et graminées - type 5

G 9 ci - paillage pouzzolane

Sarcococca humilis

Allium 'Purple Sensation'

Fritillaria imperialis 'Aurora'

Plantes vivaces et graminées - type 6

C 60/80 - paillage pouzzolane

Miscanthus sinensis 'Fernald's'

proscrit sur toiture étanchée à remplacer par Stipa tenuifolia

Plantes couvre sol - type 1

G 9 ci - paillage pouzzolane

Hebe buxifolia

Plantes couvre sol - type 2

G 9 ci - paillage pouzzolane

Liriope spicata

Plantes couvre sol - type 3

C 30/40 - paillage pouzzolane

Symphoricarpos x chenaultii 'Hancock'

Lonicera nitida 'Maigrum'

Cotoneaster dammeri 'Sikhgholmen'

Haie séparative - C 30/40 - copeaux de bois - Elaeagnus x ebbingei

Arbustes à planter - 125/150

1 - Chionanthus retusus

2 - Ligustrum ibota

3 - Syringa josikae

4 - Osmanthus heterophyllus

5 - Lonicera nitida

6 - Elaeagnus ebbingei

Polygonum baldschuanicum

125/150 - dans jardinière acier

Wisteria floribunda

125/150 - dans jardinière acier

Parthenocissus tricuspidata 'Veitchii'

125/150 - copeaux de bois

Arbres à planter - 16/18 - tuteur tripode

2c - Zelkova crenata

P0 - Fraxinus ornus

Kp - Koeleria paniculata

Th - Fila henryana

Pa - Prunus avocet

Arbres existants conservés

Mur béton (enduit hors lot VRD)

Clture grillagée simple torsion - htr : 1.50 m + portillon - i : 1.00 m

Pare-vue - htr : 1.60 m (hors lot VRD)

Clture à barreaudage vertical - (hors lot VRD) + portillon - i : 1.00 m

Bordure "pierre" - idem existant + caniveau béton

Bastaing bois - 11,5 x 19,5 x L variable - 2 htrs

Enrobés voirie légère

Béton balayé - non circulé

Béton balayé - circulé

Sable stabilisé

Pietelage composite

Pietelage composite (hors lot EV)

Gravillon roulé - bande stérile

Galet blanc

Pouzzolane (hors lot EV)

Volige bois

Main courante

Enrochement

Mobilier (cf : carnet de détails)

Bande podotactile

Cheminement PMR